



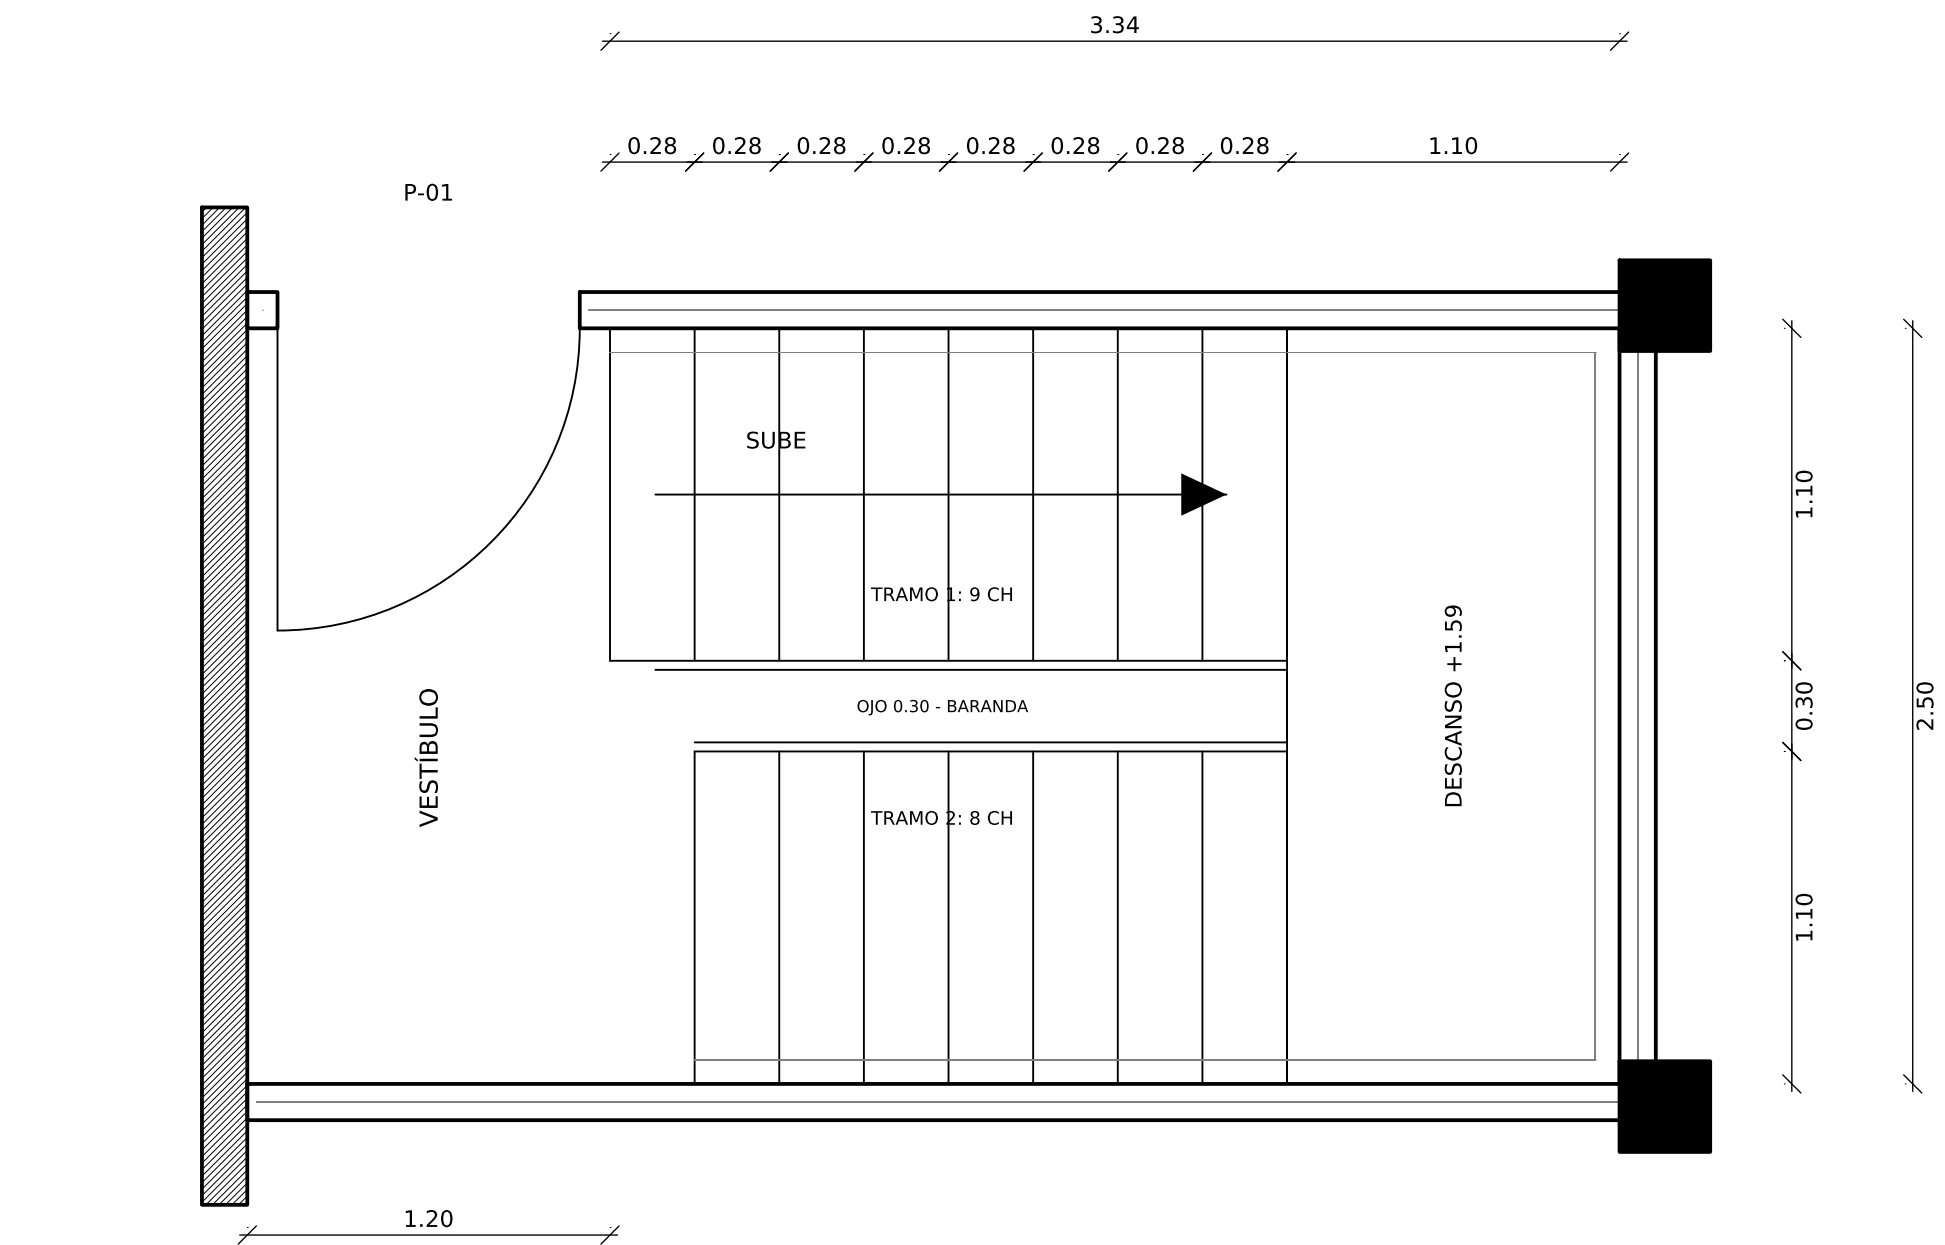


PLANTA DE ESCALERA

NIVEL 1 (VESTÍBULO); NIVELES 2 Y 3 IGUALES
Esc. 1:25

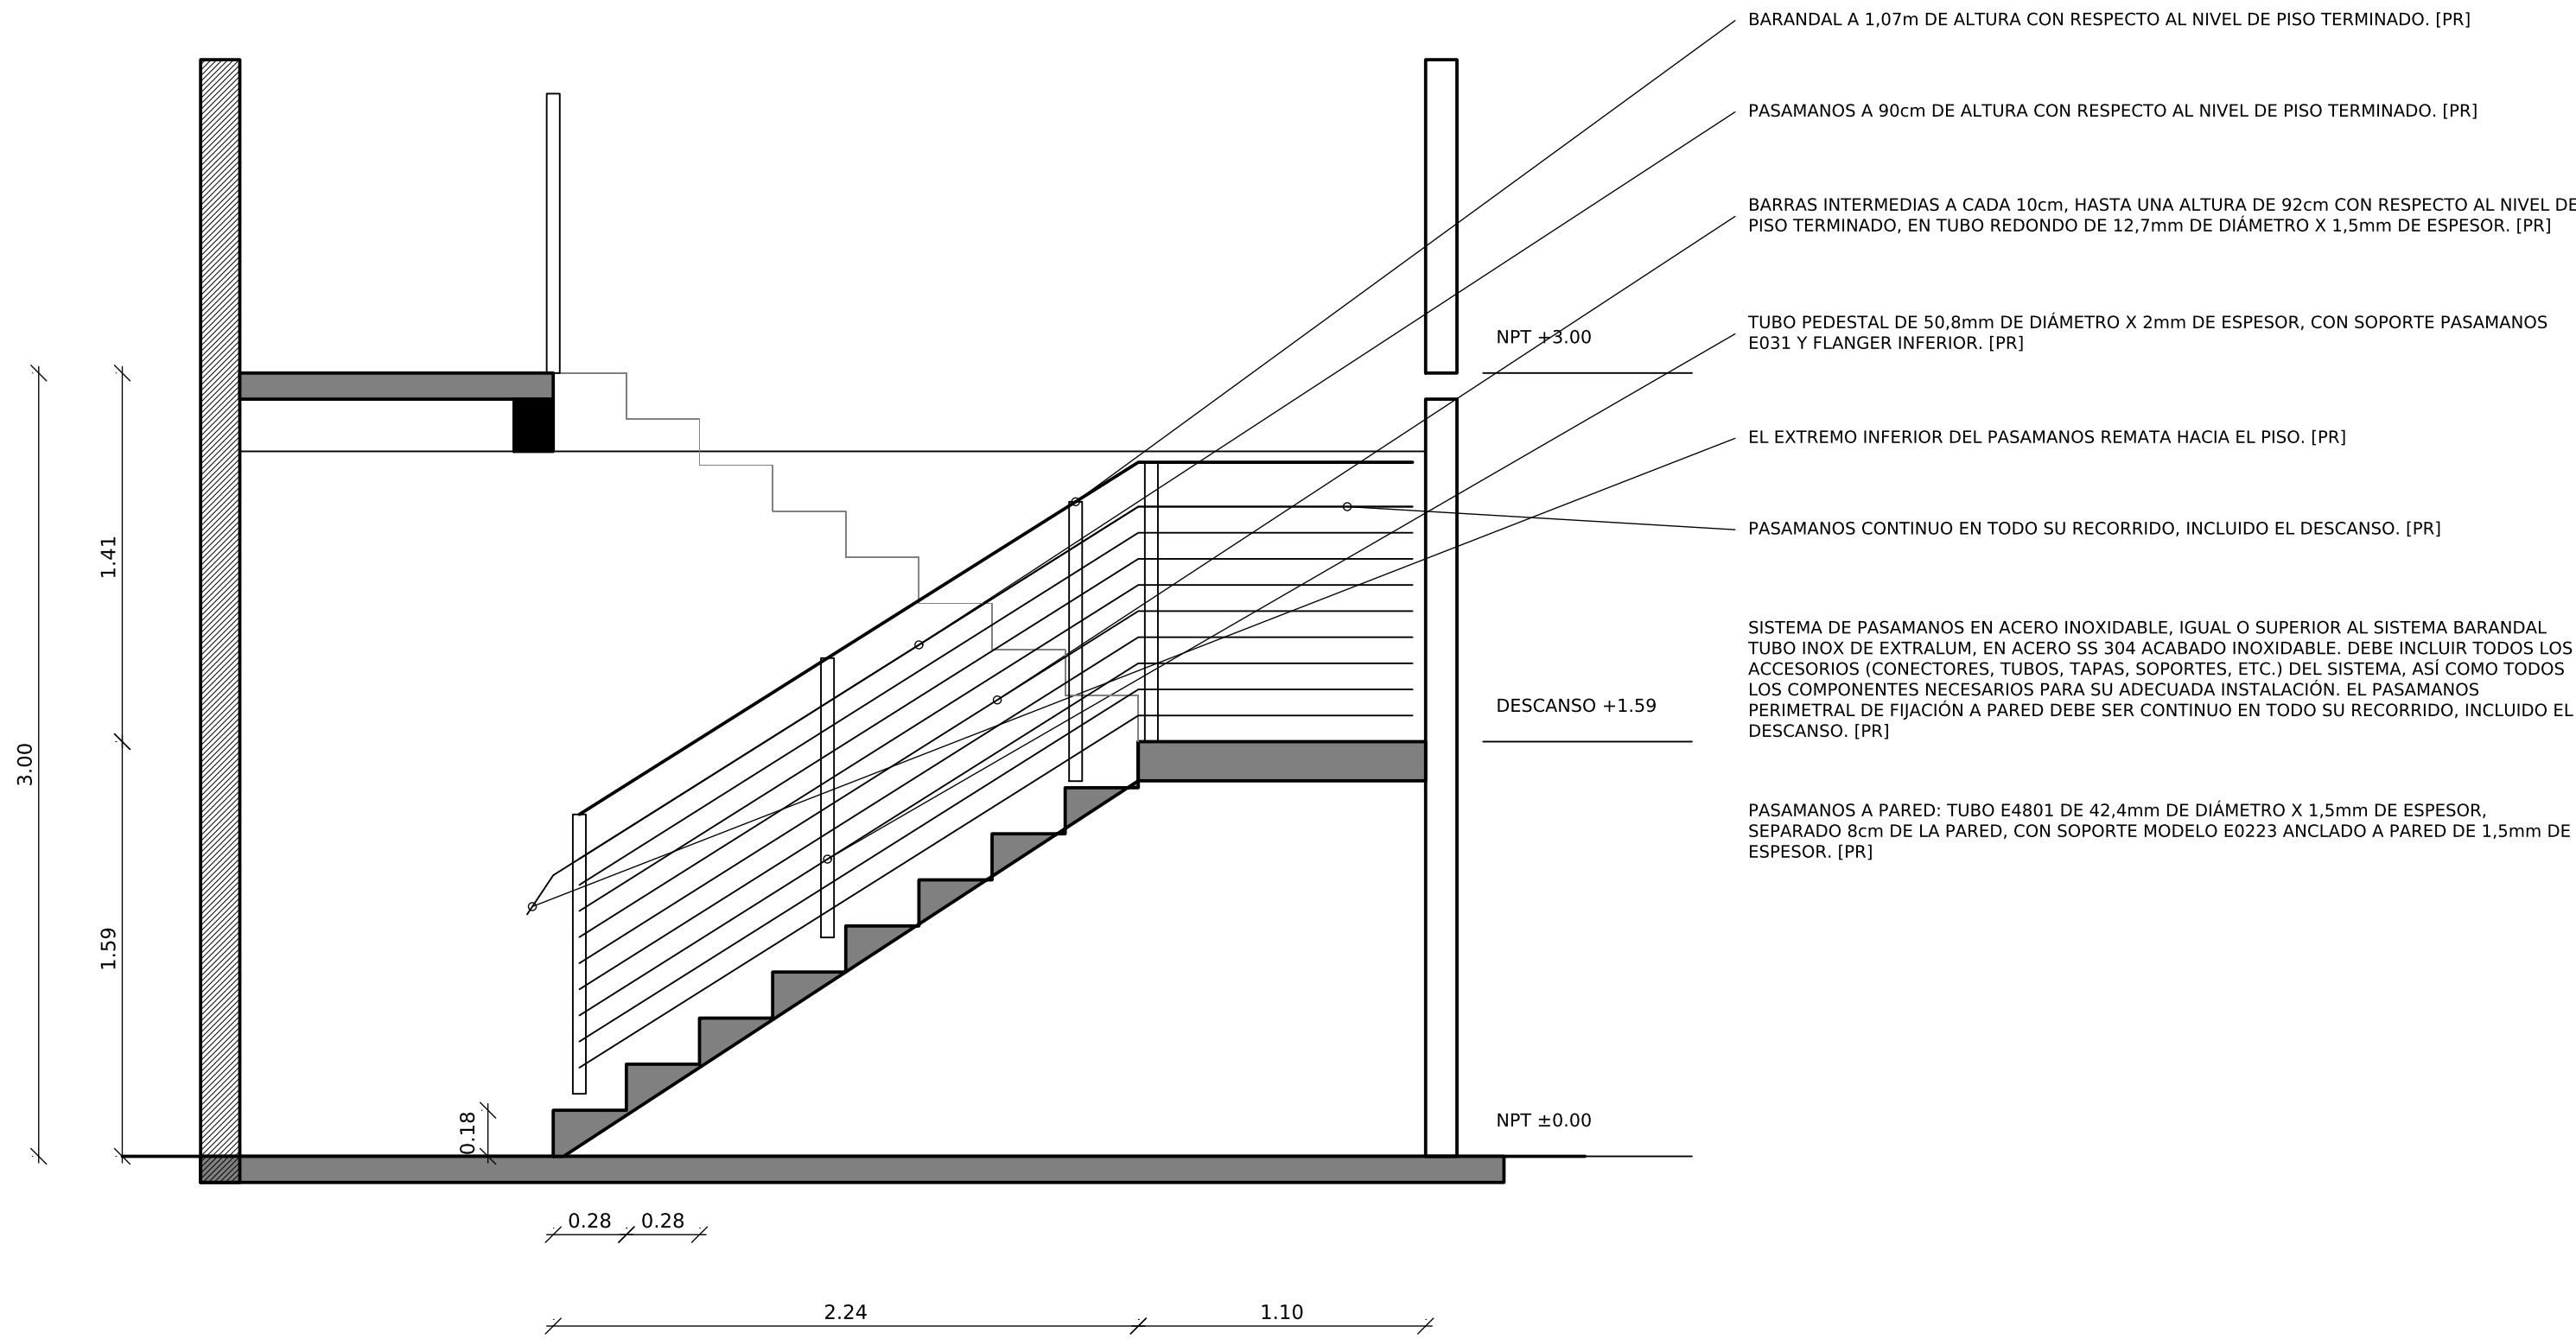

CORTE DE ESCALERA (EN EL OJO, VISTA HACIA EL EJE 4)


TRAMO NIVEL 1 A NIVEL 2; TRAMO NIVEL 2 A NIVEL 3 IGUAL
Esc. 1:25

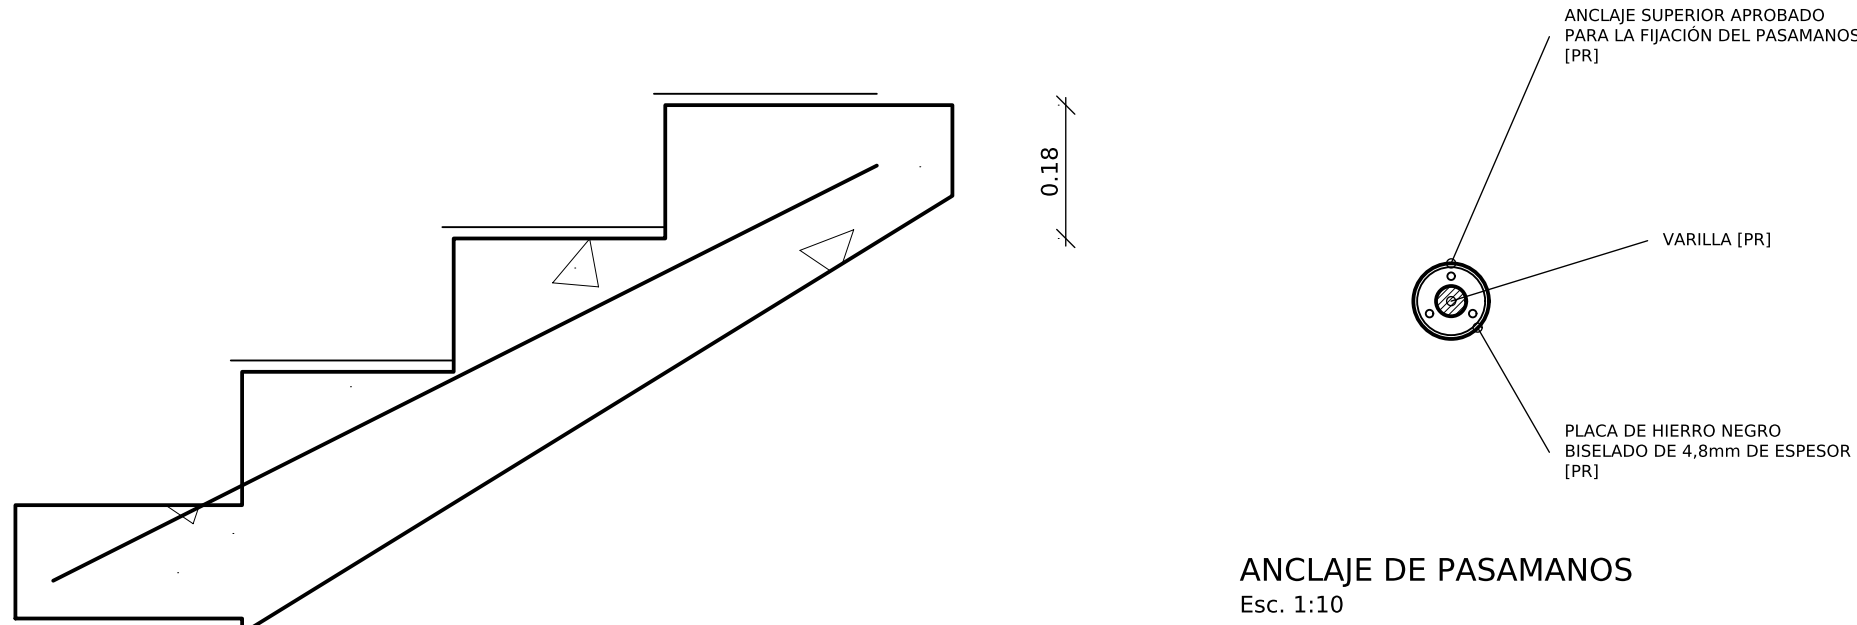

DETALLE DE ESCALÓN

LOSA DE ESCALERA DE CONCRETO ARMADO; ESPESOR Y REFUERZO SEGÚN PLANOS ESTRUCTURALES (PD). CONTRAHUELLA 0,176 m Y HUELLA 0,28 m. ACABADO DE GRADAS POR DEFINIR (PD).

ESCALÓN A CONSTRUIR SEGÚN MANUAL DE DISPOSICIONES TÉCNICAS AL REGLAMENTO DE SEGURIDAD HUMANA Y PROTECCIÓN CONTRA INCENDIOS DEL CUERPO DE BOMBEROS DE COSTA RICA (VERIFICAR). [PR]

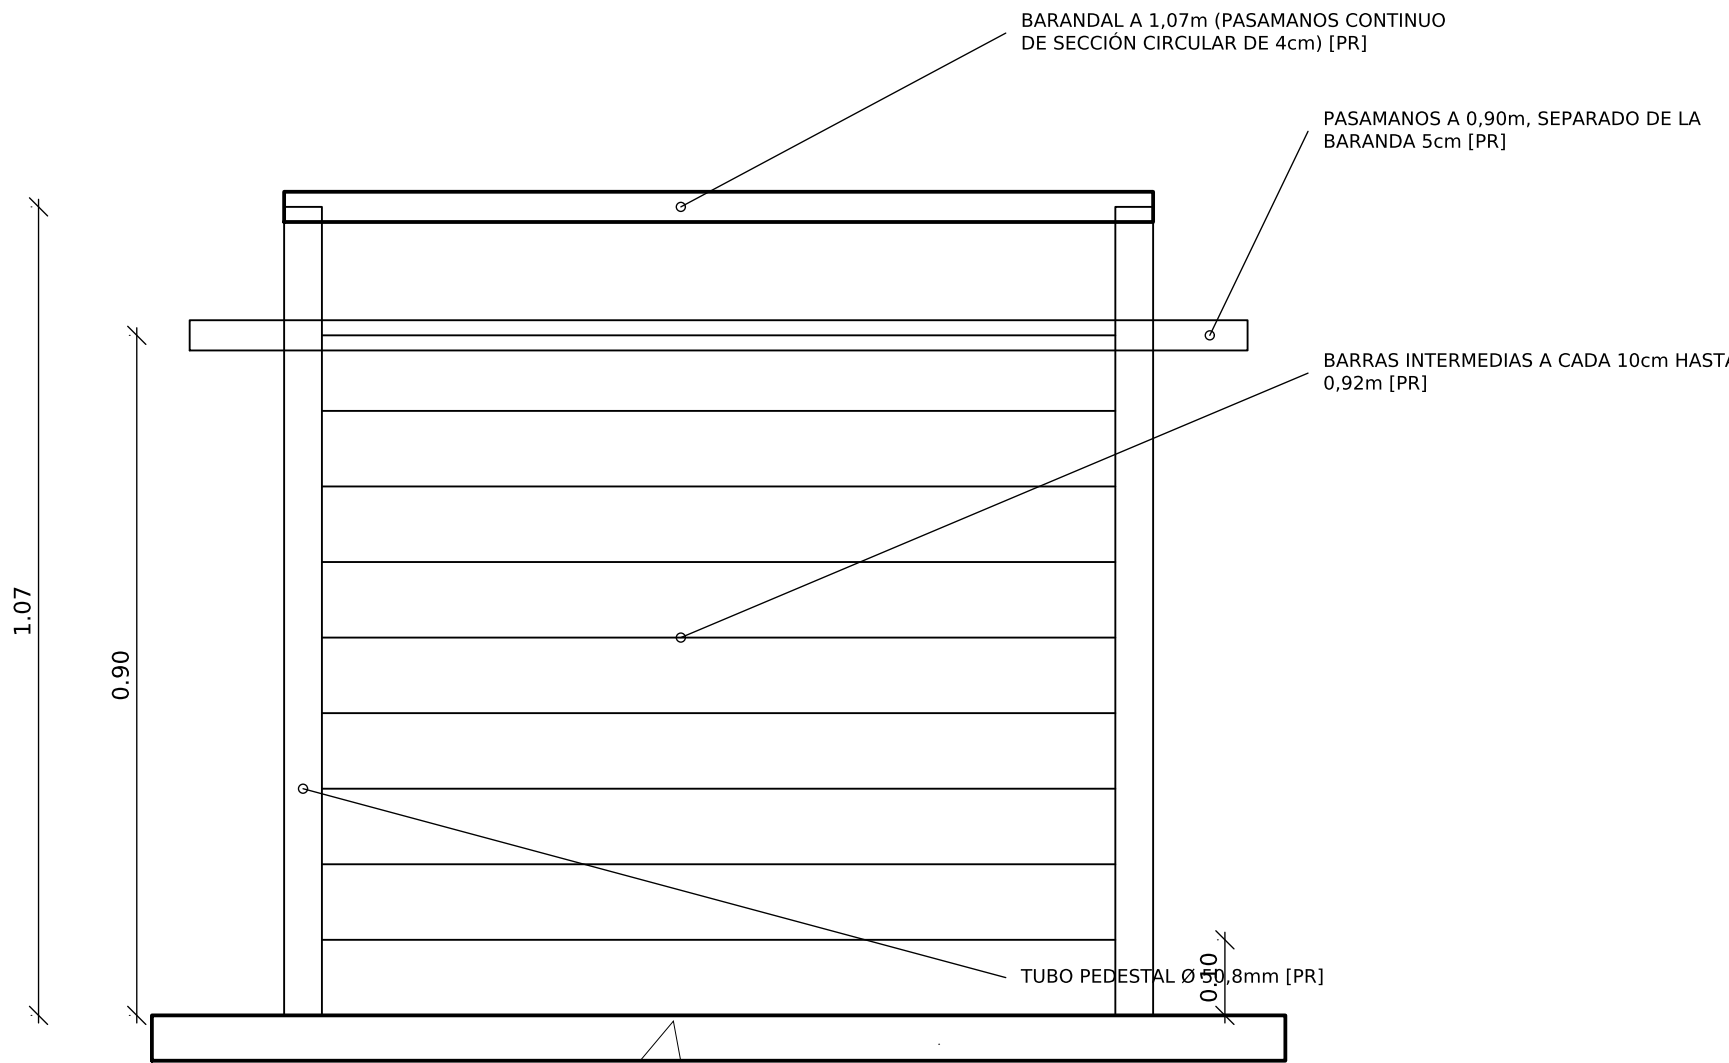

DETALLE DE BARANDA Y PASAMANOS

DISEÑO DE LAS BARANDAS Y PASAMANOS DE FORMA TAL QUE NO HAYA PROYECCIONES QUE PUEDAN ENGANCHARSE A LAS ROPAS SUELTAS. [PR]

NOTAS:

- TODAS LAS MEDIDAS ESTÁN DADAS EN METROS, SALVO INDICACIÓN CONTRARIA. [PR]
- ESCALERA EN U ENTRE EL NIVEL 1 Y EL NIVEL 3; 17 CONTRAHUELLAS DE 0,176 m Y HUELLA DE 0,28 m POR NIVEL (TRAMO 1: 9 CH; TRAMO 2: 8 CH); ANCHO DE TRAMO 1,10 m; OJO 0,30 m; DESCANSO 1,10 x 2,50 m A +1,59 (N1-N2) Y +4,59 (N2-N3).
- EN EL NIVEL 1 LA ESCALERA QUEDA EN EL VESTÍBULO CERRADO (PAREDES STEEL TECH 0,12 m, PUERTA PRINCIPAL P-01). BARANDA EN EL OJO DE LA ESCALERA Y EN EL BORDE DEL PASILLO HACIA EL VACÍO EN LOS NIVELES 2 Y 3; PASAMANOS A PARED EN EL LADO EXTERIOR DE LOS TRAMOS.
- LAS REFERENCIAS NORMATIVAS DE LA REFERENCIA (REGLAMENTO NACIONAL DE PROTECCIÓN CONTRA INCENDIOS) DEBEN VERIFICARSE CONTRA LA VERSIÓN VIGENTE. [PR]
- ESTRUCTURA DE LA ESCALERA SEGÚN PLANOS ESTRUCTURALES.

[PR] = NOTA TOMADA DEL PROYECTO DE REFERENCIA, PENDIENTE DE REVISIÓN.

ESPACIO PARA SELLOS Y TIMBRES

CivilCon Diseño y Construcción SRLTDA Céd. Jurídica: 3-102-762712		
PROFESIONAL RESPONSABLE: DIRECTOR TÉCNICO: Steven Viales (Civil) IC-40759 David Barrantes (Electricidad) IE-27499		
PROYECTO: VIVIENDA UNIFAMILIAR DISTRITO 03 SANTIAGO, CANTÓN 05 SAN RAFAEL, PROVINCIA 04 HEREDIA, COSTA RICA.		
INFORMACIÓN REGISTRO PÚBLICO: FOLIO REAL: 4-041200-000 PLANO CATASTRADO: 4-57389-2023 ÁREA SEGÚN CATASTRO: 256 m²		
CONTENIDO: ESCALERA PLANTA. CORTE. DETALLES DE ESCALÓN, BARANDA Y PASAMANOS. NOTAS.		
ESCALAS: INDICADAS		
CONTROL DE REVISIONES		
REV.	FECHA	DESCRIPCIÓN
0	06-10-2026	VERSIÓN DE TRABAJO PARA REVISIÓN
ESTADO:		
VERSIÓN DE TRABAJO NO APTA PARA CONSTRUCCIÓN NI TRÁMITE		
LUGAR		LÁMINA
COSTA RICA		A11
OCT 2026		TOTAL --