


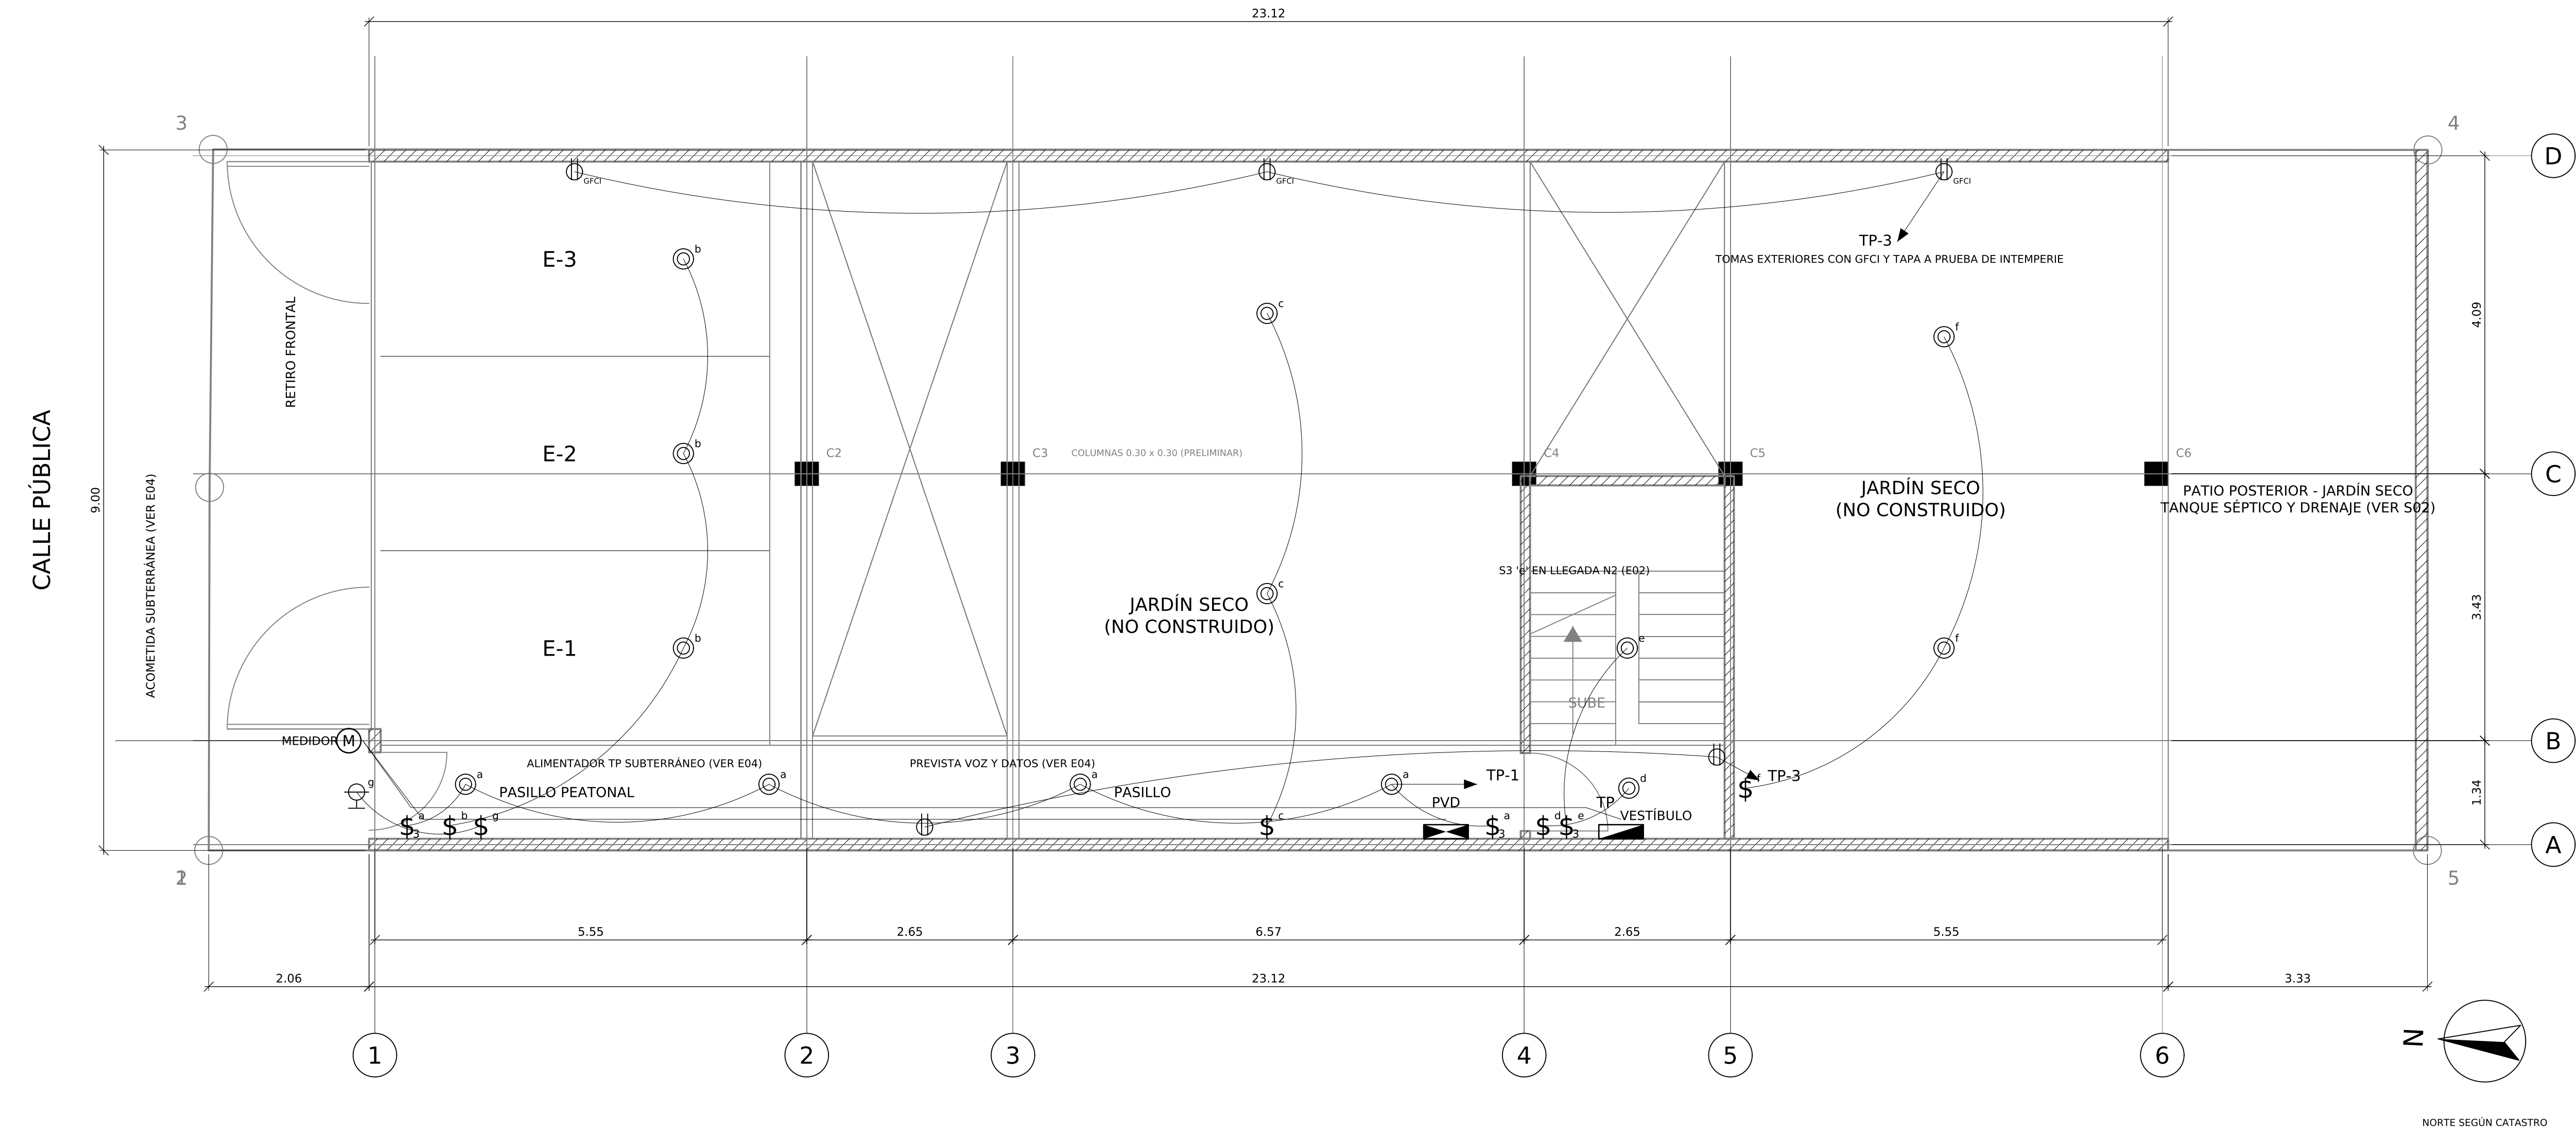

PLANTA ELÉCTRICA NIVEL 1
ILUMINACIÓN, TOMACORRIENTES Y VOZ/DATOS
Esc. 1:50



SIMBOLOGÍA ELÉCTRICA

	MEDIDOR ELÉCTRICO A 1,90 m S.N.P.T.
	TABLERO DE DISTRIBUCIÓN ELÉCTRICA
	TABLERO DE DISTRIBUCIÓN DE VOZ Y DATOS
	LUMINARIA EN SUPERFICIE DE CIELO
	LUMINARIA EMPOTRADA EN CIELO DE GYPSUM
	LUMINARIA EN PARED (APLIQUE)
	APAGADOR SENCILLO 15 A, 120 V, A 1,30 m S.N.P.T.
	APAGADOR DE TRES VÍAS 20 A, 120 V, A 1,30 m S.N.P.T.
	TOMACORRIENTE DOBLE POLARIZADO 120 V, 20 A, A 0,30 m S.N.P.T.
	TOMACORRIENTE DOBLE POLARIZADO 120 V, 20 A, A 1,50 m S.N.P.T.
	TOMACORRIENTE DOBLE 120 V, 20 A, CON PROTECCIÓN GFCI
	SALIDA ESPECIAL 240 V (VER CUADRO DE TABLEROS, E04)
	SALIDA DE TELEVISIÓN
	SALIDA DE VOZ Y DATOS

CIRCUITOS DEL NIVEL 1 (TABLERO TP)

CIRC.	DESCRIPCIÓN	DISYUNTOR	CONDUCTORES THHN
TP-1	ILUMINACIÓN NIVEL 1 (a-g)	1P-20 A	2 #12 + #12 T
TP-3	TOMACORRIENTES NIVEL 1 (GFCI EN EXTERIOR)	1P-20 A	2 #12 + #12 T

LETRAS a-g: AGRUPACIÓN DE LUMINARIAS POR APAGADOR. ALIMENTADORES DE TN2 Y TN3, DEMÁS CIRCUITOS DEL TP: VER E04.

NOTAS:

- TODAS LAS MEDIDAS ESTÁN DADAS EN METROS.
- LAS MEDIDAS DEBEN SER VERIFICADAS EN SITIO.
- TODA LA INSTALACIÓN SE REALIZARÁ EN TUBERÍA SEGÚN SE INDICA EN EL TABLERO. EN EL NIVEL 1 (ESTRUCTURA EXPUESTA, SIN CIELO) LA TUBERÍA EXPUESTA A MENOS DE 2,5 m DE ALTURA SERÁ METÁLICA (EMT).
- TODAS LAS SALIDAS, TANTO ELÉCTRICAS COMO DE TV Y DATOS, SERÁN POR MEDIO DE CAJAS DE CONEXIÓN RECTANGULARES U OCTOGONALES CON SUS RESPECTIVAS TAPAS.
- SE IDENTIFICARÁN EN EL TABLERO LOS DIFERENTES CIRCUITOS Y SE DEJARÁN AL MENOS DOS TUBOS PREVISTOS COMO ADICIONALES.
- TOMACORRIENTES EN ESTACIONAMIENTOS Y EXTERIORES CON PROTECCIÓN GFCI Y TAPA A PRUEBA DE INTEMPERIE.
- DIAGRAMA UNIFILAR, CUADROS DE TABLEROS, NOTAS GENERALES Y DETALLES EN LA LÁMINA E04.

ESPACIO PARA SELLOS Y TIMBRES

CivilCon Diseño y Construcción SRLTDA
Céd. Jurídica: 3-102-762712

PROFESIONAL RESPONSABLE:
DIRECTOR TÉCNICO:
Steven Viales (Civil) IC-40759
David Barrantes (Electricidad) IE-27499

PROYECTO:
VIVIENDA UNIFAMILIAR
DISTRITO 03 SANTIAGO, CANTÓN 05 SAN RAFAEL,
PROVINCIA 04 HEREDIA, COSTA RICA.

INFORMACIÓN REGISTRO PÚBLICO:
FOLIO REAL: 4-041200-000
PLANO CATASTRADO: 4-57389-2023
ÁREA SEGÚN CATASTRO: 256 m²


CONTENIDO:
ELECTRICIDAD
PLANTA ELÉCTRICA NIVEL 1.
ILUMINACIÓN Y TOMACORRIENTES.
VOZ Y DATOS.
SIMBOLOGÍA.
NOTAS.

ESCALAS: 1:50

CONTROL DE REVISIONES		
REV.	FECHA	DESCRIPCIÓN
0	06-10-2026	VERSIÓN DE TRABAJO PARA REVISIÓN
1	06-10-2026	SIN MENCIÓN A SECADORA
2	07-10-2026	LISTA DEFINITIVA (22); PARA TRÁMITE

ESTADO:
PARA TRÁMITE
CFIA Y MUNICIPALIDAD

LUGAR	LÁMINA
COSTA RICA	E01
OCT 2026	TOTAL 22

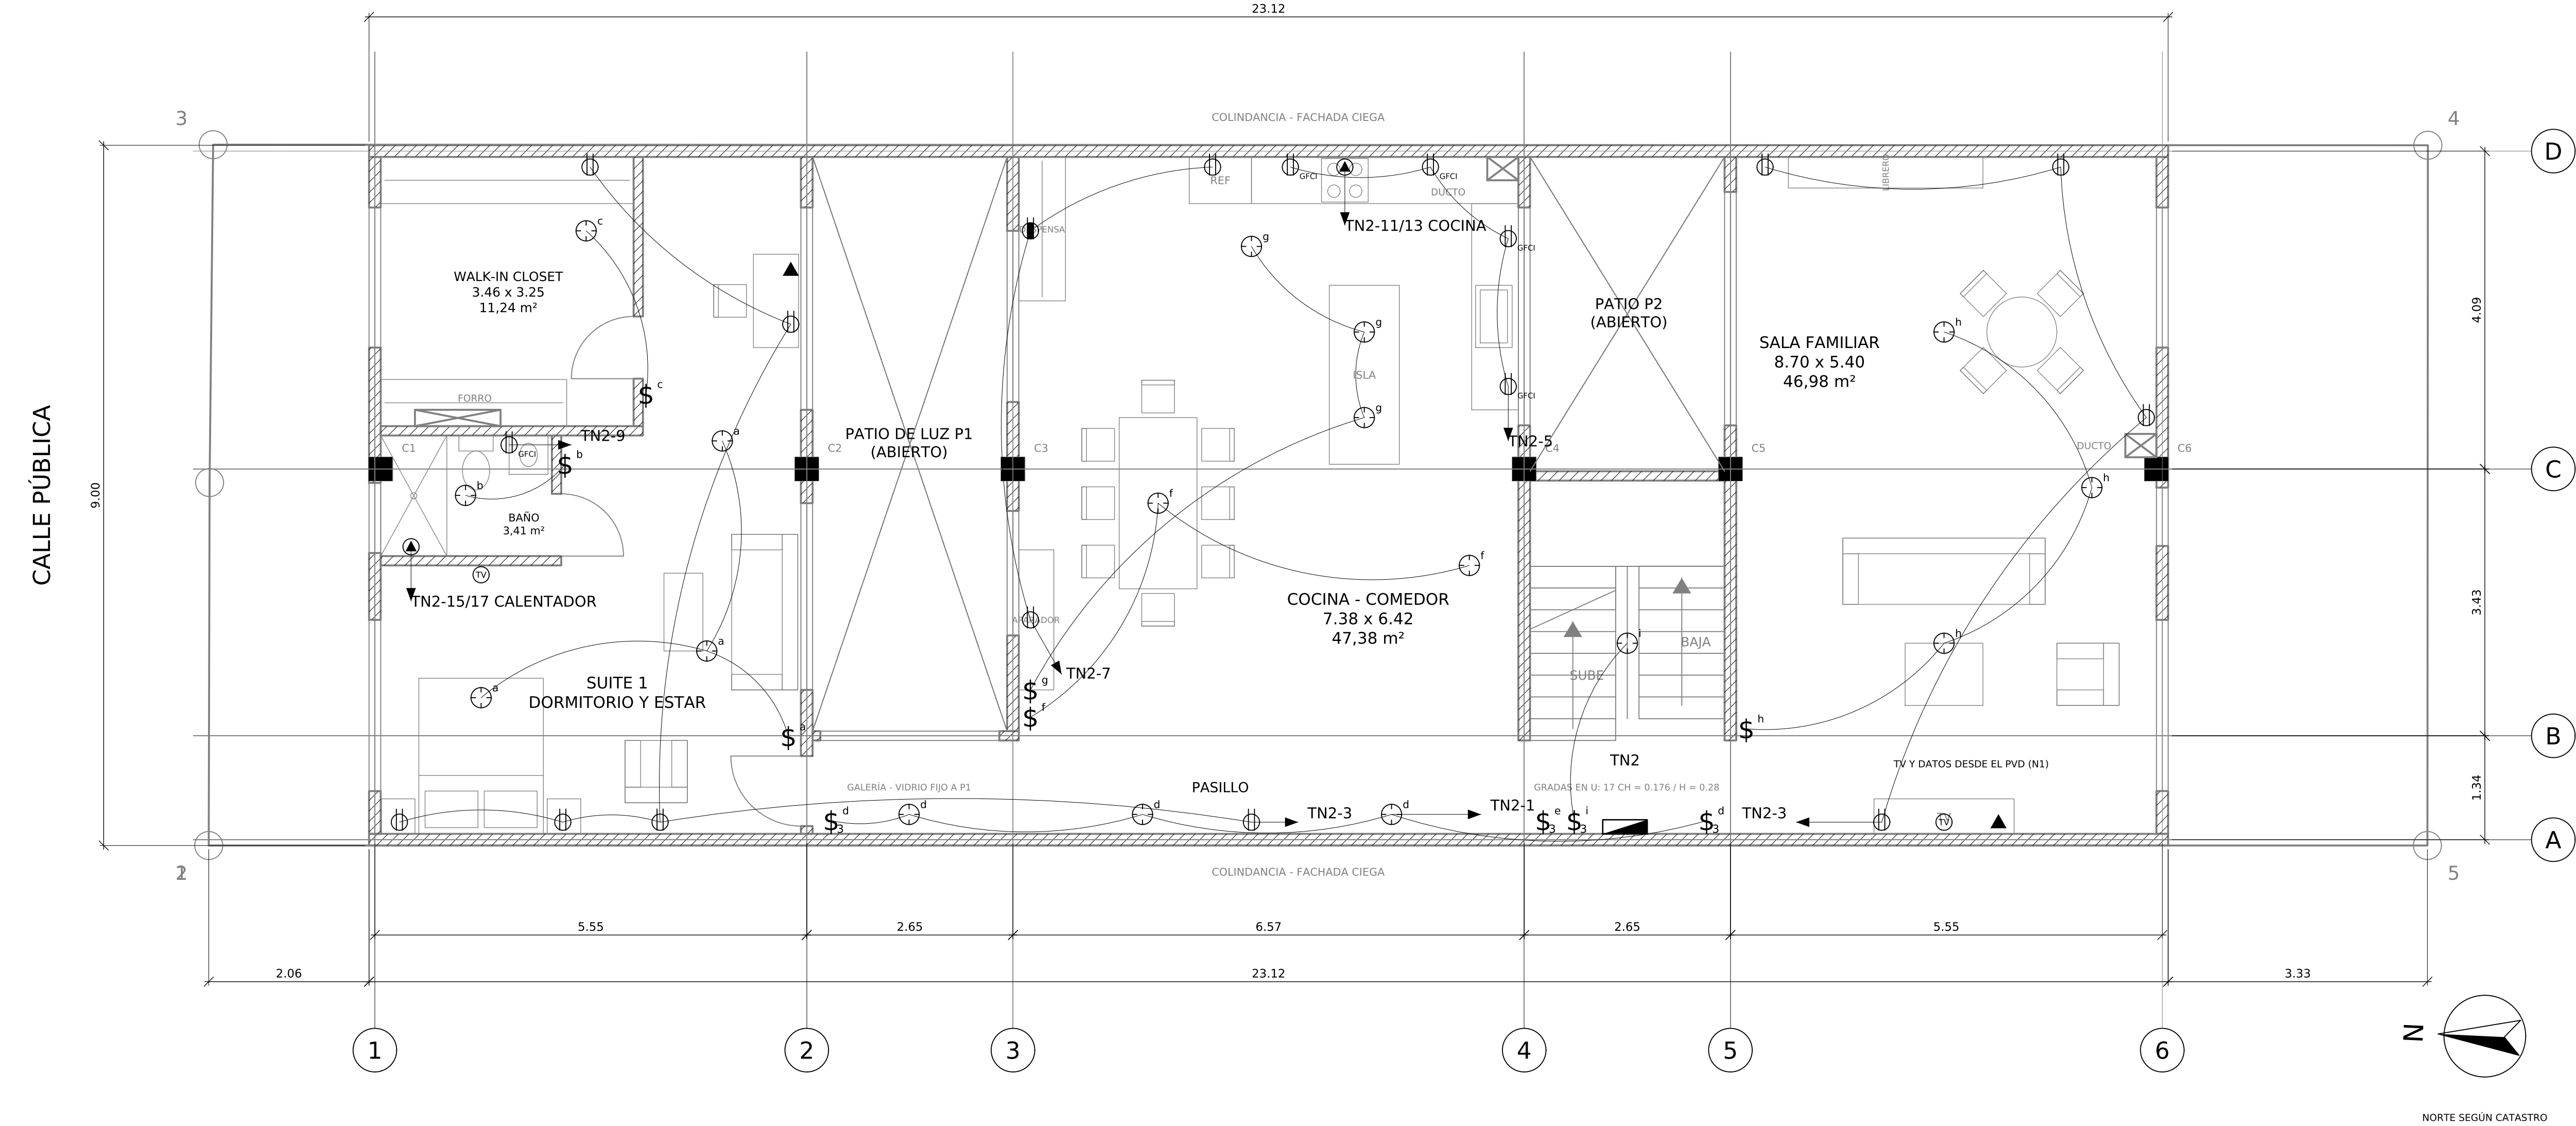

PLANTA ELÉCTRICA NIVEL 2
ILUMINACIÓN, TOMACORRIENTES Y VOZ/DATOS
Esc. 1:50

SIMBOLOGÍA ELÉCTRICA

	MEDIDOR ELÉCTRICO A 1,90 m S.N.P.T.
	TABLERO DE DISTRIBUCIÓN ELÉCTRICA
	TABLERO DE DISTRIBUCIÓN DE VOZ Y DATOS
	LUMINARIA EN SUPERFICIE DE CIELO
	LUMINARIA EMPOTRADA EN CIELO DE GYPSUM
	LUMINARIA EN PARED (APLIQUE)
	APAGADOR SENCILLO 15 A, 120 V, A 1,30 m S.N.P.T.
	APAGADOR DE TRES VÍAS 20 A, 120 V, A 1,30 m S.N.P.T.
	TOMACORRIENTE DOBLE POLARIZADO 120 V, 20 A, A 0,30 m S.N.P.T.
	TOMACORRIENTE DOBLE POLARIZADO 120 V, 20 A, A 1,50 m S.N.P.T.
	TOMACORRIENTE DOBLE 120 V, 20 A, CON PROTECCIÓN GFCI
	SALIDA ESPECIAL 240 V (VER CUADRO DE TABLEROS, E04)
	SALIDA DE TELEVISIÓN
	SALIDA DE VOZ Y DATOS

CIRCUITOS DEL NIVEL 2 (SUBTABLERO TN2)

CIRC.	DESCRIPCIÓN	DISYUNTOR	CONDUCTORES THHN
TN2-1	ILUMINACIÓN NIVEL 2 (a-i)	1P-20 A	2 #12 + #12 T
TN2-3	TOMACORRIENTES GENERALES NIVEL 2	1P-20 A	2 #12 + #12 T
TN2-5	TOMAS DE COCINA 1 (GFCI)	1P-20 A	2 #12 + #12 T
TN2-7	TOMAS DE COCINA 2 (REFRIGERADORA Y OTROS)	1P-20 A	2 #12 + #12 T
TN2-9	TOMAS DE BAÑO (GFCI)	1P-20 A	2 #12 + #12 T
TN2-11/13	COCINA ELÉCTRICA 240 V	2P-40 A	2 #8 + #10 T
TN2-15/17	CALENTADOR DE PASO BAÑO SUITE 1, 240 V	2P-40 A	2 #10 + #10 T

LETRAS a-i: AGRUPACIÓN DE LUMINARIAS POR APAGADOR, CARGAS, CAÍDAS DE TENSIÓN Y ALIMENTADOR DEL TN2: VER E04.

NOTAS:

- TODAS LAS MEDIDAS ESTÁN DADAS EN METROS.
- LAS MEDIDAS DEBEN SER VERIFICADAS EN SITIO.
- TODA LA INSTALACIÓN SE REALIZARÁ EN TUBERÍA SEGÚN SE INDICA EN EL TABLERO; EN NINGÚN CASO SE USARÁ TUBERÍA EXPUESTA (TUBERÍA SOBRE CIELO DE GYPSUM Y EN PAREDES).
- TODAS LAS SALIDAS, TANTO ELÉCTRICAS COMO DE TV Y DATOS, SERÁN POR MEDIO DE CAJAS DE CONEXIÓN RECTANGULARES U OCTOGONALES CON SUS RESPECTIVAS TAPAS.
- SE IDENTIFICARÁN EN EL TABLERO LOS DIFERENTES CIRCUITOS Y SE DEJARÁN AL MENOS DOS TUBOS PREVISTOS COMO ADICIONALES.
- TOMACORRIENTES DE COCINA SOBRE MUEBLE Y DE BAÑO CON PROTECCIÓN GFCI.
- SALIDAS ESPECIALES 240 V: COCINA ELÉCTRICA Y CALENTADOR DE PASO DEL BAÑO; ALTURA Y CONEXIÓN SEGÚN EL FABRICANTE DEL EQUIPO.
- GRADAS: EL S3 'g' CONTROLA, CON EL DEL VESTÍBULO, LA LUZ DE GRADAS DEL NIVEL 1 (E01); EL S3 'i' CONTROLA, CON EL DEL NIVEL 3, LA LUZ DE GRADAS DEL NIVEL 2 (E03).
- SALIDAS DE TV Y DATOS CON TUBERÍA INDEPENDIENTE DESDE EL PVD DEL NIVEL 1.
- DIAGRAMA UNIFILAR, ALIMENTADOR DEL TN2, CUADROS DE TABLEROS, NOTAS GENERALES Y DETALLES EN LA LÁMINA E04.

ESPACIO PARA SELLOS Y TIMBRES

CivilCon Diseño y Construcción SRLTDA
Céd. Jurídica: 3-102-762712

PROFESIONAL RESPONSABLE:
DIRECTOR TÉCNICO:
Steven Viales (Civil) IC-40759
David Barrantes (Electricidad) IE-27499

PROYECTO:
VIVIENDA UNIFAMILIAR
DISTRITO 03 SANTIAGO, CANTÓN 05 SAN RAFAEL,
PROVINCIA 04 HEREDIA, COSTA RICA.

INFORMACIÓN REGISTRO PÚBLICO:
FOLIO REAL: 4-041200-000
PLANO CATASTRADO: 4-57389-2023
ÁREA SEGÚN CATASTRO: 256 m²

CONTENIDO:
ELECTRICIDAD
PLANTA ELÉCTRICA NIVEL 2.
ILUMINACIÓN Y TOMACORRIENTES.
VOZ Y DATOS.
SIMBOLOGÍA.
NOTAS.

ESCALAS: 1:50


CONTROL DE REVISIONES

REV.	FECHA	DESCRIPCIÓN
0	06-10-2026	VERSIÓN DE TRABAJO PARA REVISIÓN
1	07-10-2026	LISTA DEFINITIVA (22); PARA TRÁMITE

ESTADO:

PARA TRÁMITE
CFIA Y MUNICIPALIDAD

LUGAR	LÁMINA
COSTA RICA	E02
OCT 2026	TOTAL 22

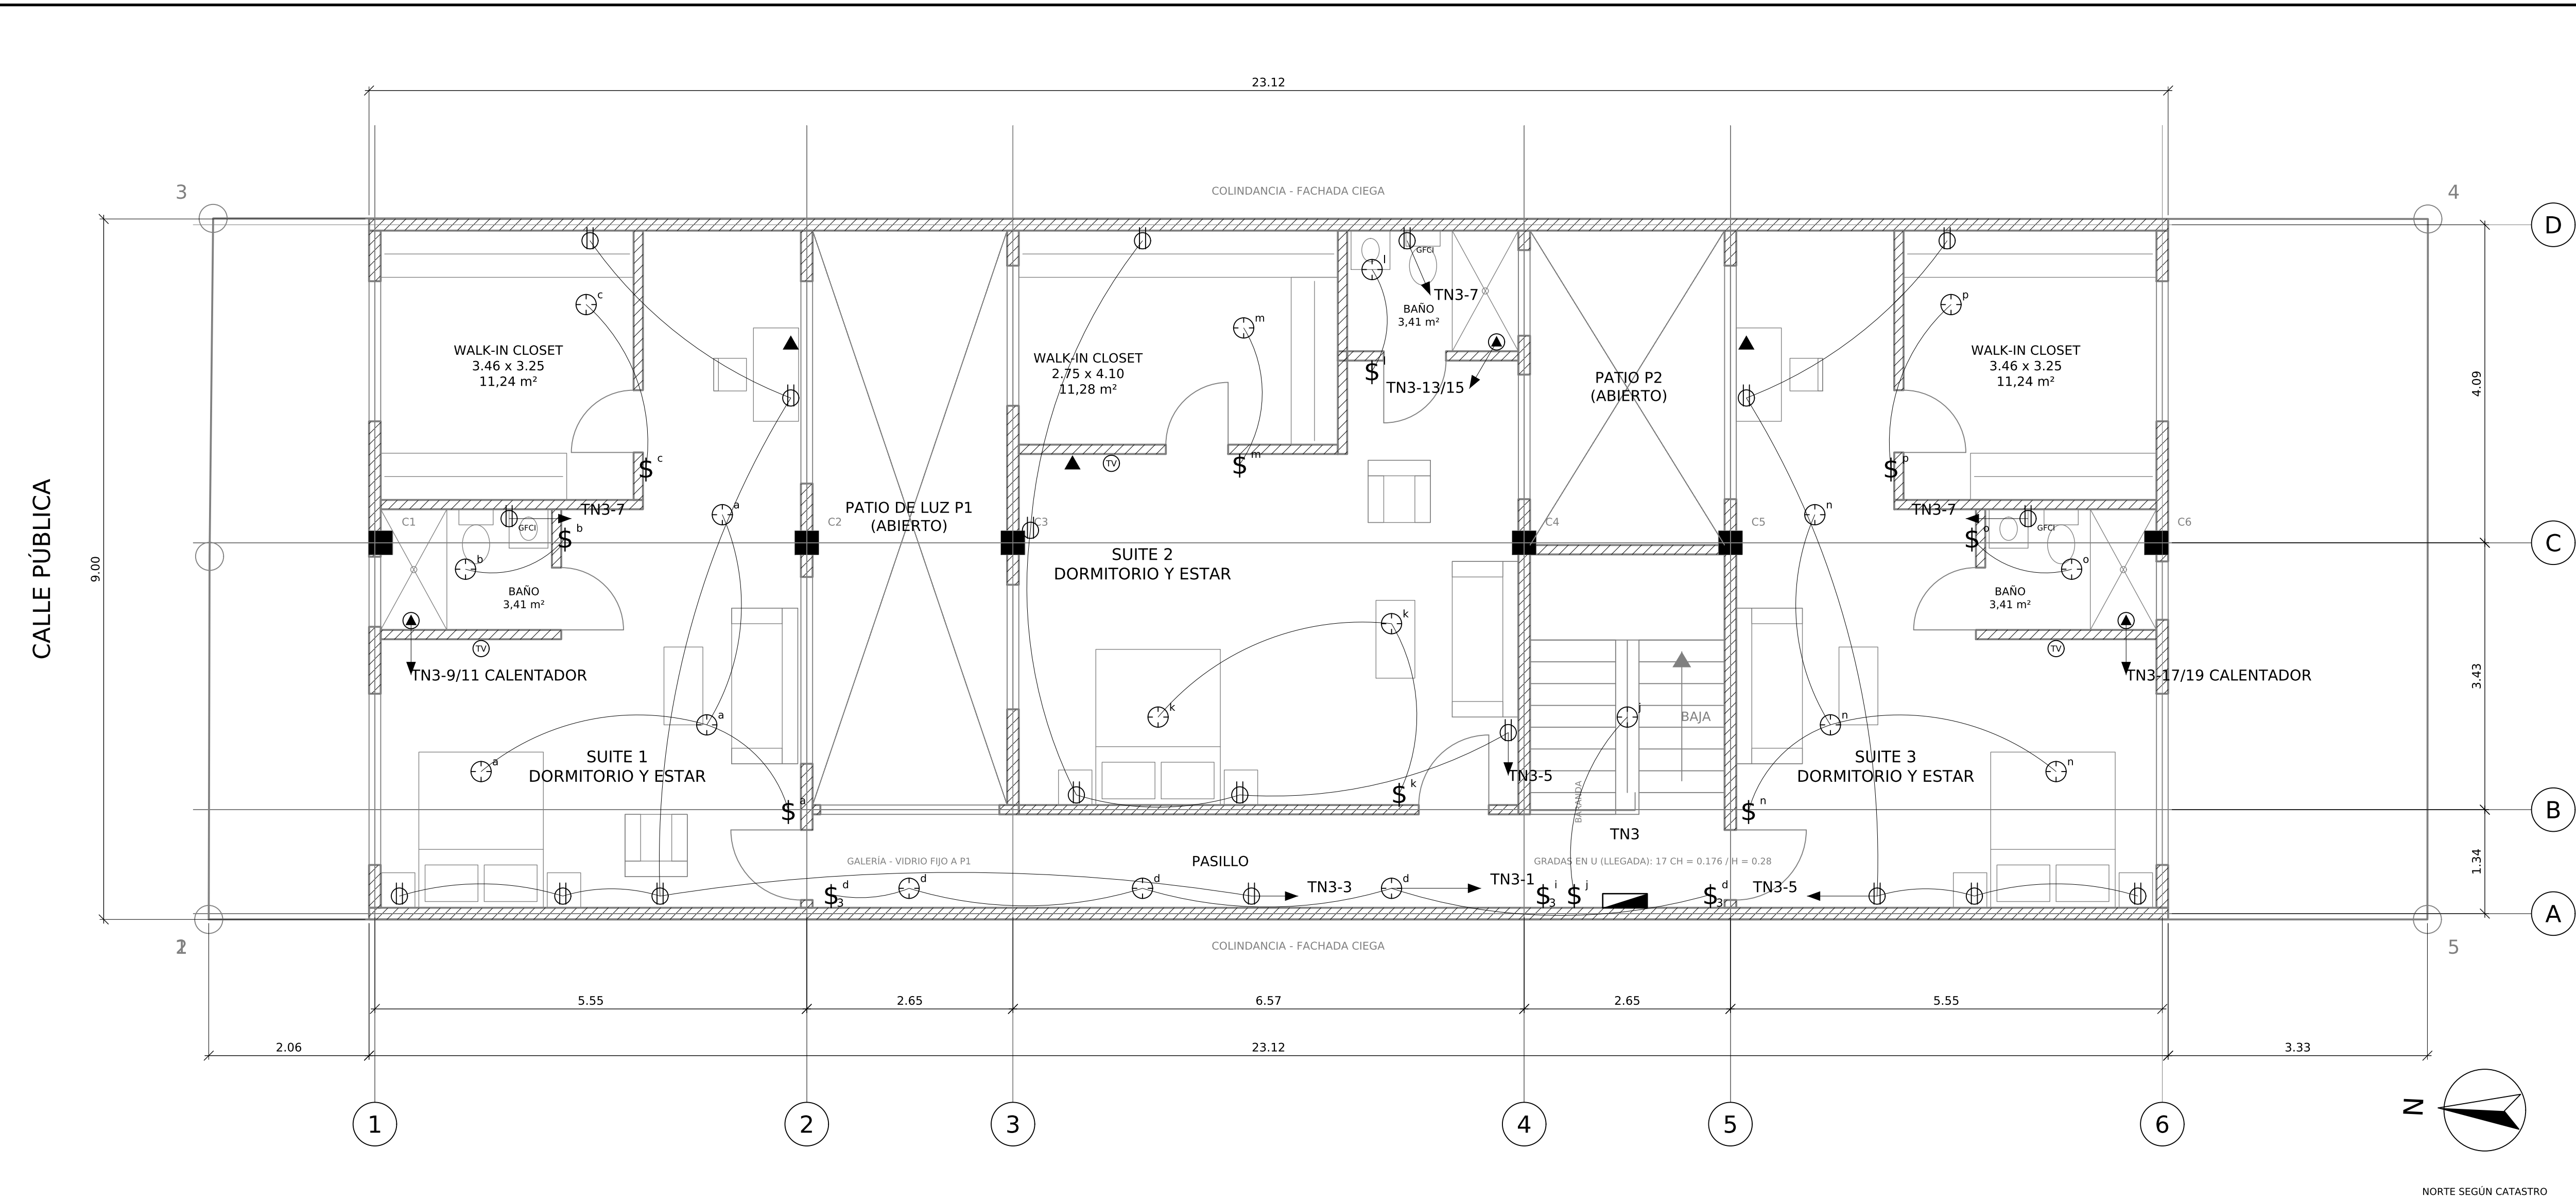

PLANTA ELÉCTRICA NIVEL 3
ILUMINACIÓN, TOMACORRIENTES Y VOZ/DATOS
Esc. 1:50



SIMBOLOGÍA ELÉCTRICA

	MEDIDOR ELÉCTRICO A 1,90 m S.N.P.T.
	TABLERO DE DISTRIBUCIÓN ELÉCTRICA
	TABLERO DE DISTRIBUCIÓN DE VOZ Y DATOS
	LUMINARIA EN SUPERFICIE DE CIELO
	LUMINARIA EMPOTRADA EN CIELO DE GYPSUM
	LUMINARIA EN PARED (APLIQUE)
	APAGADOR SENCILLO 15 A, 120 V, A 1,30 m S.N.P.T.
	APAGADOR DE TRES VÍAS 20 A, 120 V, A 1,30 m S.N.P.T.
	TOMACORRIENTE DOBLE POLARIZADO 120 V, 20 A, A 0,30 m S.N.P.T.
	TOMACORRIENTE DOBLE POLARIZADO 120 V, 20 A, A 1,50 m S.N.P.T.
	TOMACORRIENTE DOBLE 120 V, 20 A, CON PROTECCIÓN GFCI
	SALIDA ESPECIAL 240 V (VER CUADRO DE TABLEROS, E04)
	SALIDA DE TELEVISIÓN
	SALIDA DE VOZ Y DATOS

CIRCUITOS DEL NIVEL 3 (SUBTABLERO TN3)

CIRC.	DESCRIPCIÓN	DISYUNTOR	CONDUCTORES THHN
TN3-1	ILUMINACIÓN NIVEL 3 (a-p)	1P-20 A	2 #12 + #12 T
TN3-3	TOMAS GENERALES SUITE 1 Y PASILLO	1P-20 A	2 #12 + #12 T
TN3-5	TOMAS GENERALES SUITES 2 Y 3	1P-20 A	2 #12 + #12 T
TN3-7	TOMAS DE BAÑOS (GFCI)	1P-20 A	2 #12 + #12 T
TN3-9/11	CALENTADOR DE PASO BAÑO SUITE 1, 240 V	2P-40 A	2 #10 + #10 T
TN3-13/15	CALENTADOR DE PASO BAÑO SUITE 2, 240 V	2P-40 A	2 #10 + #10 T
TN3-17/19	CALENTADOR DE PASO BAÑO SUITE 3, 240 V	2P-40 A	2 #10 + #10 T

LETRAS a-p: AGRUPACIÓN DE LUMINARIAS POR APAGADOR. CARGAS, CAÍDAS DE TENSION Y ALIMENTADOR DEL TN3: VER E04.

NOTAS:

- TODAS LAS MEDIDAS ESTÁN DADAS EN METROS.
- LAS MEDIDAS DEBEN SER VERIFICADAS EN SITIO.
- TODA LA INSTALACIÓN SE REALIZARÁ EN TUBERÍA SEGÚN SE INDICA EN EL TABLERO; EN NINGÚN CASO SE USARÁ TUBERÍA EXPUESTA (TUBERÍA SOBRE CIELO DE GYPSUM Y EN PAREDES).
- TODAS LAS SALIDAS, TANTO ELÉCTRICAS COMO DE TV Y DATOS, SERÁN POR MEDIO DE CAJAS DE CONEXIÓN RECTANGULARES U OCTOGONALES CON SUS RESPECTIVAS TAPAS.
- SE IDENTIFICARÁN EN EL TABLERO LOS DIFERENTES CIRCUITOS Y SE DEJARÁN AL MENOS DOS TUBOS PREVISTOS COMO ADICIONALES.
- TOMACORRIENTES DE BAÑO CON PROTECCIÓN GFCI.
- SALIDAS ESPECIALES 240 V: UN CALENTADOR DE PASO POR BAÑO; ALTURA Y CONEXIÓN SEGÚN EL FABRICANTE DEL EQUIPO.
- GRADAS: EL S3 'I' CONTROLA, CON EL DEL NIVEL 2, LA LUZ DE GRADAS DEL NIVEL 2 (E02); LA LUZ 'J' ILUMINA LA LLEGADA AL NIVEL 3.
- SALIDAS DE TV Y DATOS CON TUBERÍA INDEPENDIENTE DESDE EL PVD DEL NIVEL 1.
- DIAGRAMA UNIFILAR, ALIMENTADOR DEL TN3, CUADROS DE TABLEROS, NOTAS GENERALES Y DETALLES EN LA LÁMINA E04.

ESPACIO PARA SELLOS Y TIMBRES

CivilCon Diseño y Construcción SRLTDA
Céd. Jurídica: 3-102-762712

PROFESIONAL RESPONSABLE:
DIRECTOR TÉCNICO:
Steven Viales (Civil) IC-40759
David Barrantes (Electricidad) IE-27499

PROYECTO:
VIVIENDA UNIFAMILIAR
DISTRITO 03 SANTIAGO, CANTÓN 05 SAN RAFAEL,
PROVINCIA 04 HEREDIA, COSTA RICA.

INFORMACIÓN REGISTRO PÚBLICO:
FOLIO REAL: 4-041200-000
PLANO CATASTRADO: 4-57389-2023
ÁREA SEGÚN CATASTRO: 256 m²

CONTENIDO:
ELECTRICIDAD
PLANTA ELÉCTRICA NIVEL 3.
ILUMINACIÓN Y TOMACORRIENTES.
VOZ Y DATOS.
SIMBOLOGÍA.
NOTAS.

ESCALAS: 1:50

CONTROL DE REVISIONES

REV.	FECHA	DESCRIPCIÓN
0	06-10-2026	VERSIÓN DE TRABAJO PARA REVISIÓN
1	07-10-2026	LISTA DEFINITIVA (22); PARA TRÁMITE

ESTADO:

PARA TRÁMITE
CFIA Y MUNICIPALIDAD

LUGAR	LÁMINA
COSTA RICA	E03
OCT 2026	TOTAL 22

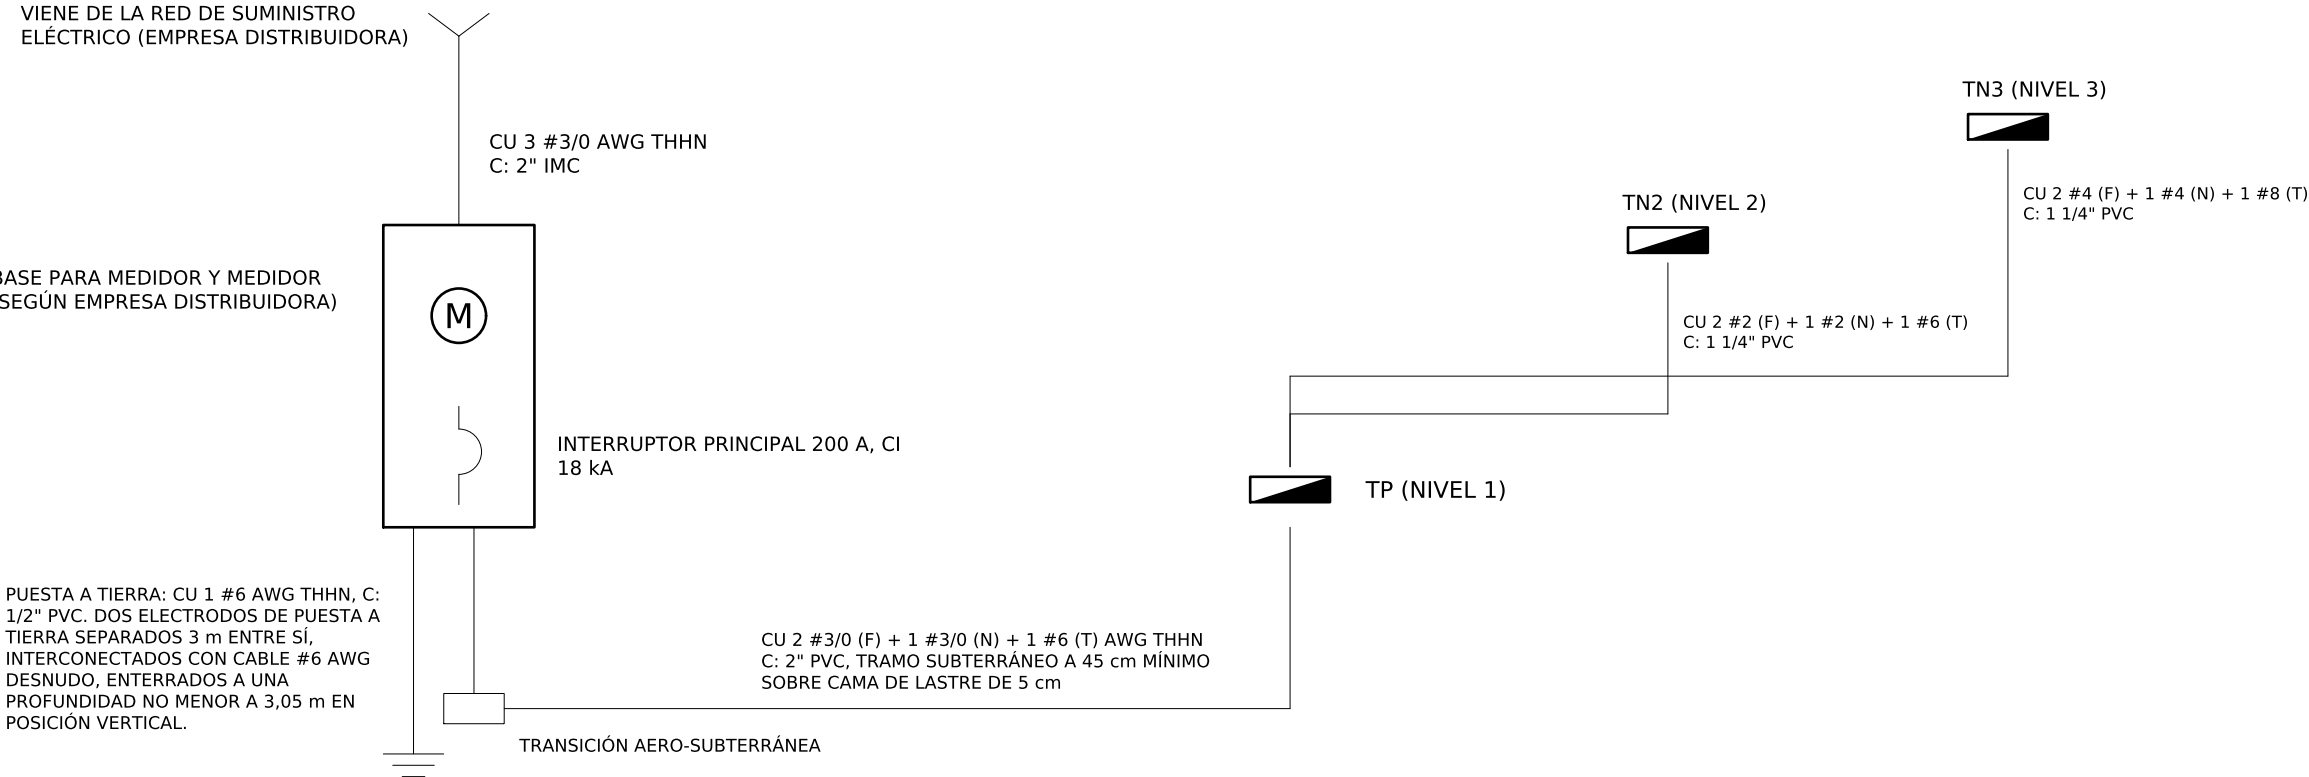


DIAGRAMA DE VOZ Y DATOS



TABLA RESUMEN DEL PROYECTO

	TABLERO TP	TABLERO TN2	TABLERO TN3
kVA TOTALES	38,3	18,5	20,0
kVA DEMANDADOS	26,8	14,8	16,0
FACTOR DE DEMANDA	0,70	0,80	0,80
FACTOR DE POTENCIA	0,95	0,95	0,95
FASES	2 #3/0 AWG	2 #2 AWG	2 #4 AWG
NEUTRO	1 #3/0 AWG	1 #2 AWG	1 #4 AWG
TIERRA	1 #6 AWG	1 #6 AWG	1 #8 AWG
LONGITUD (m)	25	15	20
TENSIÓN NOMINAL (V)	120/240	120/240	120/240
% CAÍDA DE TENSIÓN	0,58 %	0,46 %	1,04 %

DIAGRAMA UNIFILAR ELÉCTRICO

MONOFÁSICO 120/240 V

Esc. S/E

TABLERO PRINCIPAL TP (NIVEL 1, VESTÍBULO)

TABLERO MONOFÁSICO 120/240 V, BARRAS DE TIERRA, NEUTRO SÓLIDO AL 100 %, BARRAS PRINCIPALES DE COBRE, EMPOTRADO. BARRAS 225 A, 24 POLOS, INTERRUPTOR PRINCIPAL 200 A, CI 200 A. CARGA TOTAL 38,3 kVA, DEMANDADA 26,8 kVA.

N.	DESCRIPCIÓN	POL.	AMP.	FASE	NEUT.	TIERRA	DIST.	V	VA FASE A	VA FASE B	% CT	Ø mm	PROTECCIÓN
1	ILUMINACIÓN NIVEL 1	1	20	12	12	12	15	120	500	-	0,65	13	AFCI/GFCI
3	TOMACORRIENTES NIVEL 1 (GFCI)	1	20	12	12	12	15	120	-	1.000	1,30	13	AFCI/GFCI
5/7	SECADORA	2	40	10	-	8	15	240	3.000	3.000	1,19	19	CH
9/11	ALIMENTADOR SUBTABLERO TN2	2	100	2	2	6	15	240	7.400	7.400	0,46	32	CH
13/15	ALIMENTADOR SUBTABLERO TN3	2	100	4	4	8	20	240	8.000	8.000	1,04	32	CH
17/19	SPD	2	50	8	8	8	0,5	240	-	-	-	19	CH
TOTAL POR FASE (VA)									18.900	19.400			

SUBTABLERO TN2 (NIVEL 2)

TABLERO MONOFÁSICO 120/240 V, BARRAS DE TIERRA, NEUTRO SÓLIDO AL 100 %. EMPOTRADO. BARRAS 125 A, 18 POLOS, PRINCIPAL 100 A (SUBALIMENTADO). CARGA TOTAL 18,5 kVA, DEMANDADA 14,8 kVA.

N.	DESCRIPCIÓN	POL.	AMP.	FASE	NEUT.	TIERRA	DIST.	V	VA FASE A	VA FASE B	% CT	Ø mm	PROTECCIÓN
1	ILUMINACIÓN NIVEL 2	1	20	12	12	12	15	120	500	-	0,65	13	AFCI/GFCI
3	TOMAS GENERALES NIVEL 2	1	20	12	12	12	15	120	-	500	0,65	13	AFCI/GFCI
5	TOMAS DE COCINA 1 (GFCI)	1	20	12	12	12	15	120	1.500	-	1,95	13	AFCI/GFCI
7	TOMAS DE COCINA 2	1	20	12	12	12	15	120	-	1.500	1,95	13	AFCI/GFCI
9	TOMAS DE BAÑO (GFCI)	1	20	12	12	12	15	120	500	-	0,65	13	AFCI/GFCI
11/13	COCINA ELÉCTRICA	2	40	8	8	10	15	240	4.000	4.000	1,00	19	CH
15/17	CALENTADOR DE PASO BAÑO SUITE 1	2	40	10	-	8	15	240	3.000	3.000	1,19	19	CH
19/21	SPD	2	50	8	8	8	0,5	240	-	-	-	19	CH
TOTAL POR FASE (VA)									9.500	9.000			

SUBTABLERO TN3 (NIVEL 3)

TABLERO MONOFÁSICO 120/240 V, BARRAS DE TIERRA, NEUTRO SÓLIDO AL 100 %. EMPOTRADO. BARRAS 125 A, 18 POLOS, PRINCIPAL 100 A (SUBALIMENTADO). CARGA TOTAL 20,0 kVA, DEMANDADA 16,0 kVA.

N.	DESCRIPCIÓN	POL.	AMP.	FASE	NEUT.	TIERRA	DIST.	V	VA FASE A	VA FASE B	% CT	Ø mm	PROTECCIÓN
1	ILUMINACIÓN NIVEL 3	1	20	12	12	12	15	120	500	-	0,65	13	AFCI/GFCI
3	TOMAS GENERALES SUITE 1 Y PASILLO	1	20	12	12	12	15	120	-	500	0,65	13	AFCI/GFCI
5	TOMAS GENERALES SUITES 2 Y 3	1	20	12	12	12	15	120	500	-	0,65	13	AFCI/GFCI
7	TOMAS DE BAÑOS (GFCI)	1	20	12	12	12	15	120	-	500	0,65	13	AFCI/GFCI
9/11	CALENTADOR DE PASO BAÑO SUITE 1	2	40	10	-	8	15	240	3.000	3.000	1,19	19	CH
13/15	CALENTADOR DE PASO BAÑO SUITE 2	2	40	10	-	8	15	240	3.000	3.000	1,19	19	CH
17/19	CALENTADOR DE PASO BAÑO SUITE 3	2	40	10	-	8	15	240	3.000	3.000	1,19	19	CH
21/23	SPD	2	50	8	8	8	0,5	240	-	-	-	19	CH
TOTAL POR FASE (VA)									10.000	10.000			

CONDUCTORES THHN DE COBRE (AWG). CAÍDA DE TENSIÓN %CT = 2 L I R / V CON LA RESISTENCIA POR CONDUCTOR DE CADA CALIBRE.

NOTAS ELÉCTRICAS

NOTAS GENERALES

LAS INSTALACIONES ELÉCTRICAS SE REALIZARÁN DE ACUERDO CON LA NORMATIVA ELÉCTRICA VIGENTE Y LAS REGULACIONES DE LA EMPRESA DISTRIBUIDORA.
CUALQUIER CAMBIO O ADICIONAL PODRÁ REALIZARSE BAJO LA AUTORIZACIÓN DEL INGENIERO DISEÑADOR, QUIEN EVALUARÁ LOS CAMBIOS.

NO SE PERMITIRÁN CAMBIOS SIN LA PRESENTACIÓN Y APROBACIÓN DE LAS FICHAS TÉCNICAS CORRESPONDIENTES. CUALQUIER INSTALACIÓN ESTÁ SUJETA A RECHAZO POR PARTE DEL INSPECTOR SI NO SE PRESENTAN LAS FICHAS DE LOS MATERIALES Y EQUIPOS COMPRADOS.

CANALIZACIONES

LAS CANALIZACIONES DE LAS REDES ELÉCTRICAS Y TELEFÓNICAS DEBERÁN COLOCARSE Y UTILIZARSE EN FORMA INDEPENDIENTE, CON EL 40 % DEL ESPACIO (ÁREA TRANSVERSAL) LIBRE EN TODOS SUS PUNTOS.

TODAS LAS CANALIZACIONES SE HARÁN CON TUBERÍA CONDUIT PVC CERTIFICADA, DE LOS DIÁMETROS ESPECIFICADOS. LAS CONEXIONES SERÁN CONTINUAS ENTRE CAJA Y CAJA. LA TUBERÍA QUE NO VIAJE EN ESTRUCTURAS CHORREADAS SE SUJETARÁ CON GAZAS CADA 1,5 m COMO MÍNIMO.

LAS TUBERÍAS EXPUESTAS QUE VIAJEN A MENOS DE 2,5 m DE ALTURA DEBEN SER METÁLICAS (EMT, RÍGIDO, GALVANIZADO). LAS TUBERÍAS ENTERRADAS EN EXTERIORES SERÁN DE PVC SCH-40.

LAS CANALIZACIONES ELÉCTRICAS DE POTENCIA (BAJA TENSIÓN) DEBERÁN IR A UNA PROFUNDIDAD MÍNIMA DE 50 cm, CUBIERTAS CON UNA CAPA DE 10 cm (MÍNIMO) DE ARENA LIMPIA; LAS TELEFÓNICAS A 25 cm MÍNIMO, CUBIERTAS CON 5 cm DE ARENA LIMPIA.

LAS UNIONES ENTRE TUBERÍAS, CAJAS Y LÁMPARAS SE HARÁN MEDIANTE ACCESORIOS EMT DE TAMAÑO ADECUADO. LAS TUBERÍAS EN PROCESO DE INSTALACIÓN SE PROTEGERÁN CON TAPONES DE CAUCHO O MADERA.

SIMBOLOGÍA ELÉCTRICA

	MEDIDOR ELÉCTRICO A 1,90 m S.N.P.T.
	TABLERO DE DISTRIBUCIÓN ELÉCTRICA
	TABLERO DE DISTRIBUCIÓN DE VOZ Y DATOS
	LUMINARIA EN SUPERFICIE DE CIELO
	LUMINARIA EMPOTRADA EN CIELO DE GYPSUM
	LUMINARIA EN PARED (APLIQUE)
	APAGADOR SENCILLO 15 A, 120 V, A 1,30 m S.N.P.T.
	APAGADOR DE TRES VÍAS 20 A, 120 V, A 1,30 m S.N.P.T.
	TOMACORRIENTE DOBLE POLARIZADO 120 V, 20 A, A 0,30 m S.N.P.T.
	TOMACORRIENTE DOBLE POLARIZADO 120 V, 20 A, A 1,50 m S.N.P.T.
	TOMACORRIENTE DOBLE 120 V, 20 A, CON PROTECCIÓN GFCI
	SALIDA ESPECIAL 240 V (VER CUADRO DE TABLEROS, E04)
	SALIDA DE TELEVISIÓN
	SALIDA DE VOZ Y DATOS

LÁMINAS RELACIONADAS: E01 (NIVEL 1), E02 (NIVEL 2) Y E03 (NIVEL 3).

ESPACIO PARA SELLOS Y TIMBRES

CivilCon Diseño y Construcción SRLTDA
Céd. Jurídica: 3-102-762712

PROFESIONAL RESPONSABLE:
DIRECTOR TÉCNICO:
Steven Viales (Civil) IC-40759
David Barrantes (Electricidad) IE-27499

PROYECTO:
VIVIENDA UNIFAMILIAR
DISTRITO 03 SANTIAGO, CANTÓN 05 SAN RAFAEL,
PROVINCIA 04 HEREDIA, COSTA RICA.

INFORMACIÓN REGISTRO PÚBLICO:
FOLIO REAL: 4-041200-000
PLANO CATASTRADO: 4-57389-2023
ÁREA SEGÚN CATASTRO: 256 m²

CONTENIDO:
ELECTRICIDAD
DIAGRAMA UNIFILAR.
VOZ Y DATOS.
CUADROS DE TABLEROS.
NOTAS ELÉCTRICAS.
SIMBOLOGÍA.

ESCALAS: S/E









CONTROL DE REVISIONES

REV.	FECHA	DESCRIPCIÓN
0	06-10-2026	VERSIÓN DE TRABAJO PARA REVISIÓN
1	07-10-2026	LISTA DEFINITIVA (22); PARA TRÁMITE

ESTADO:

PARA TRÁMITE
CFIA Y MUNICIPALIDAD

LUGAR	LÁMINA
COSTA RICA	E04
OCT 2026	TOTAL 22

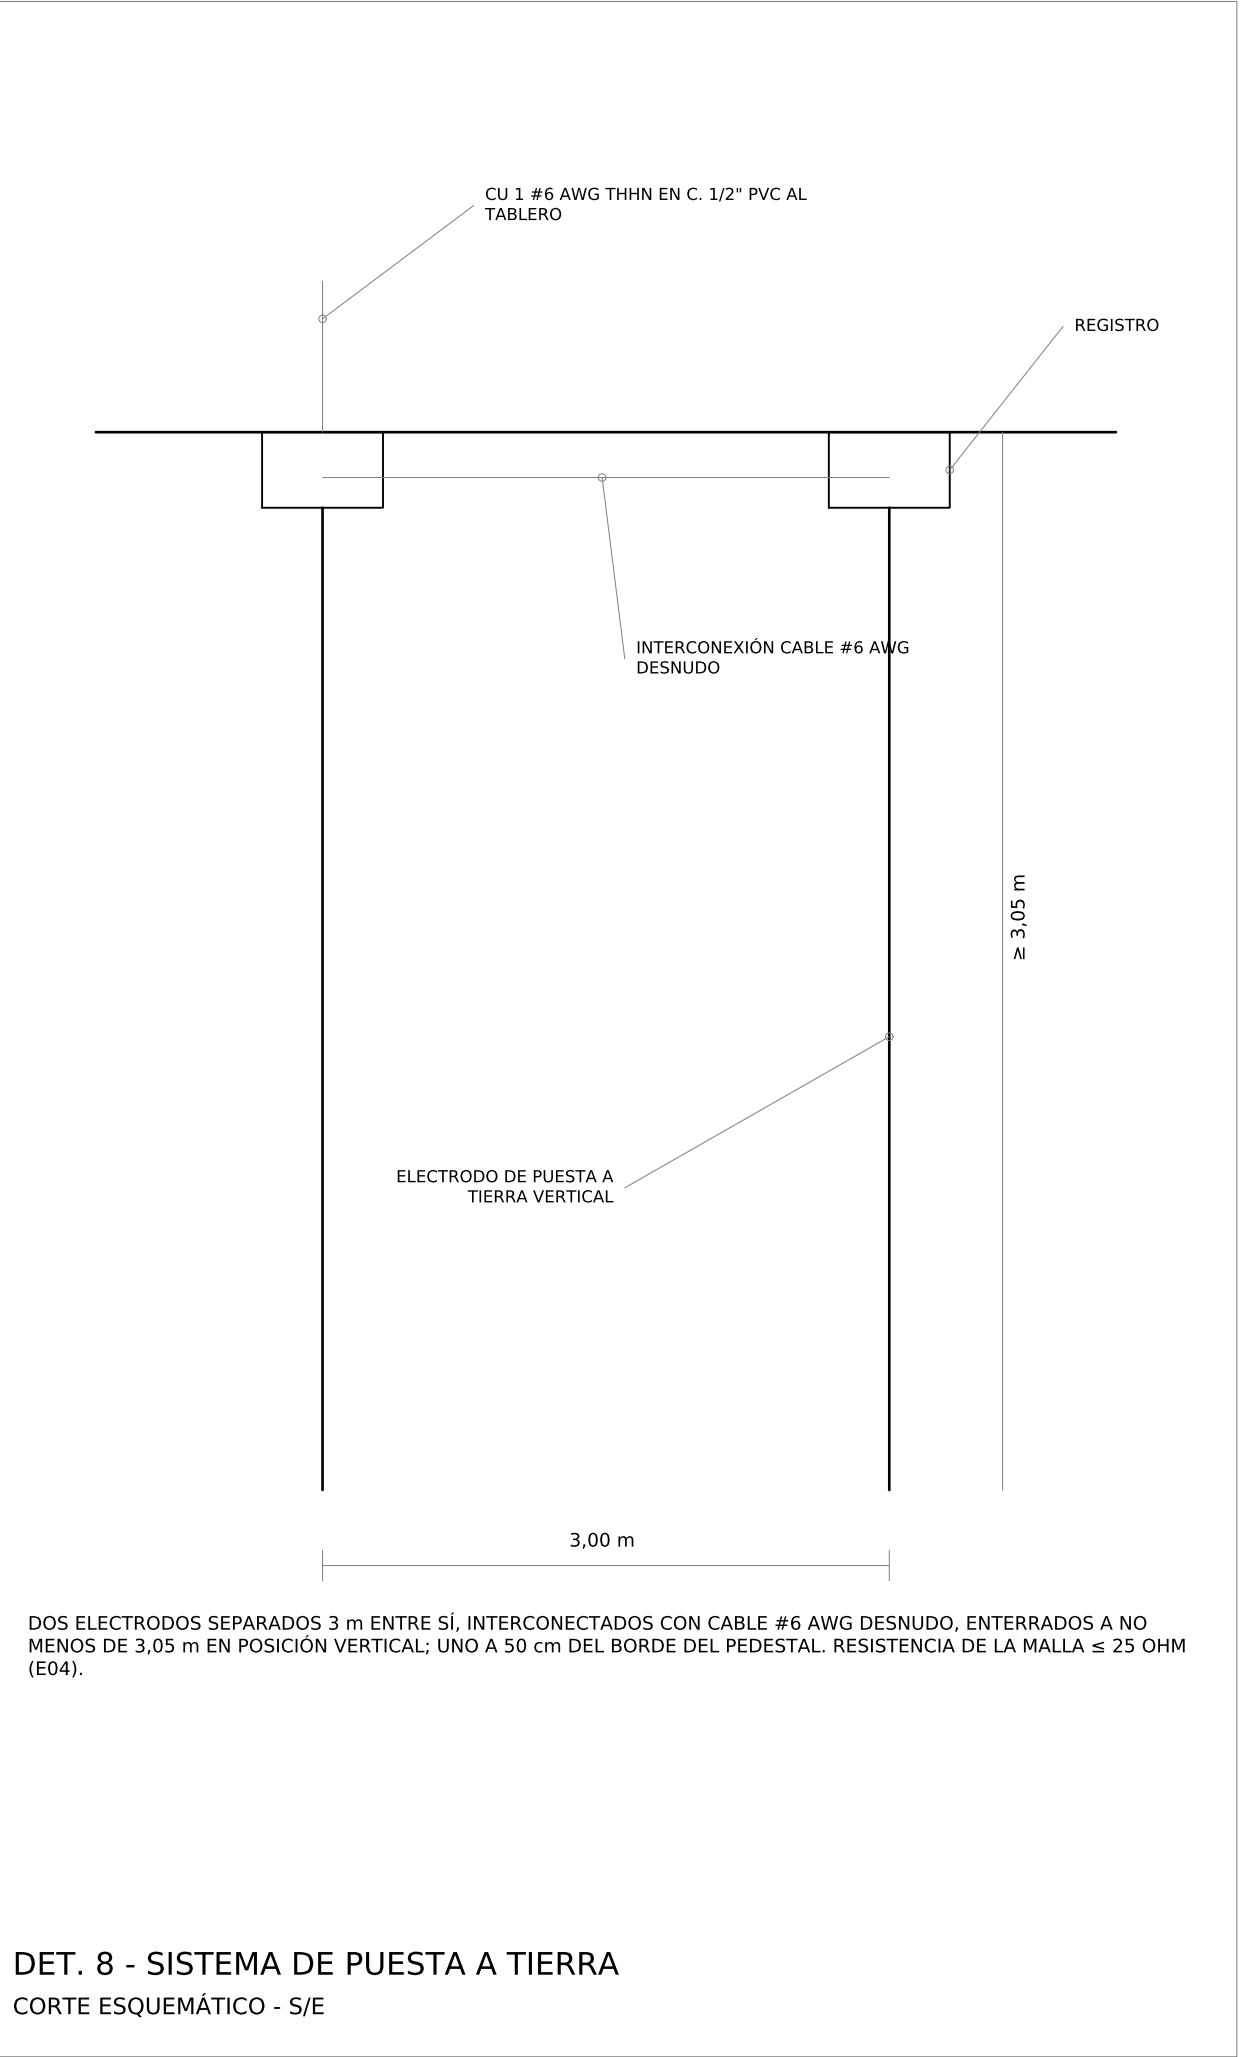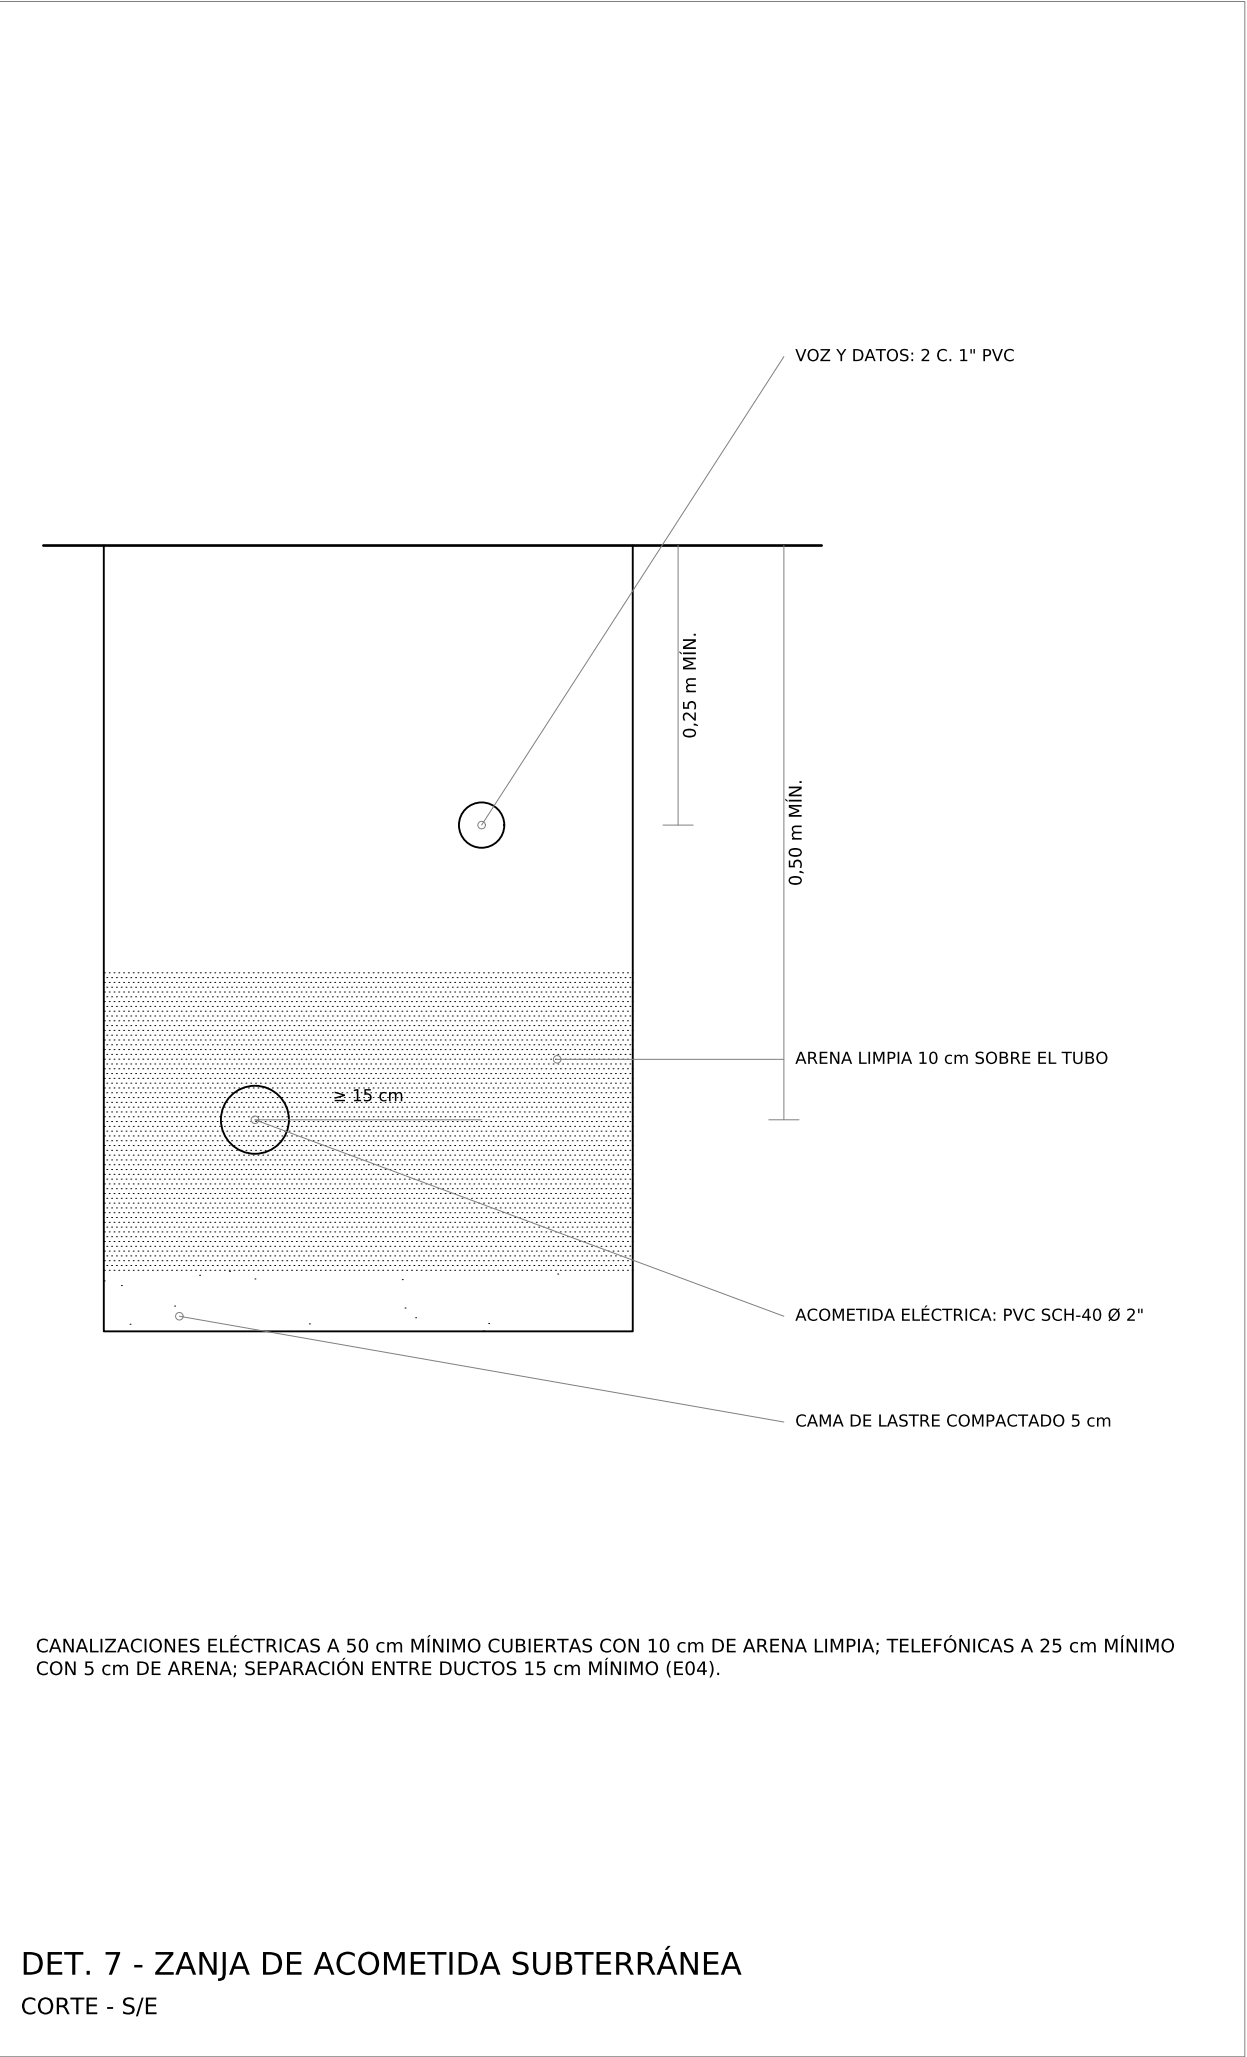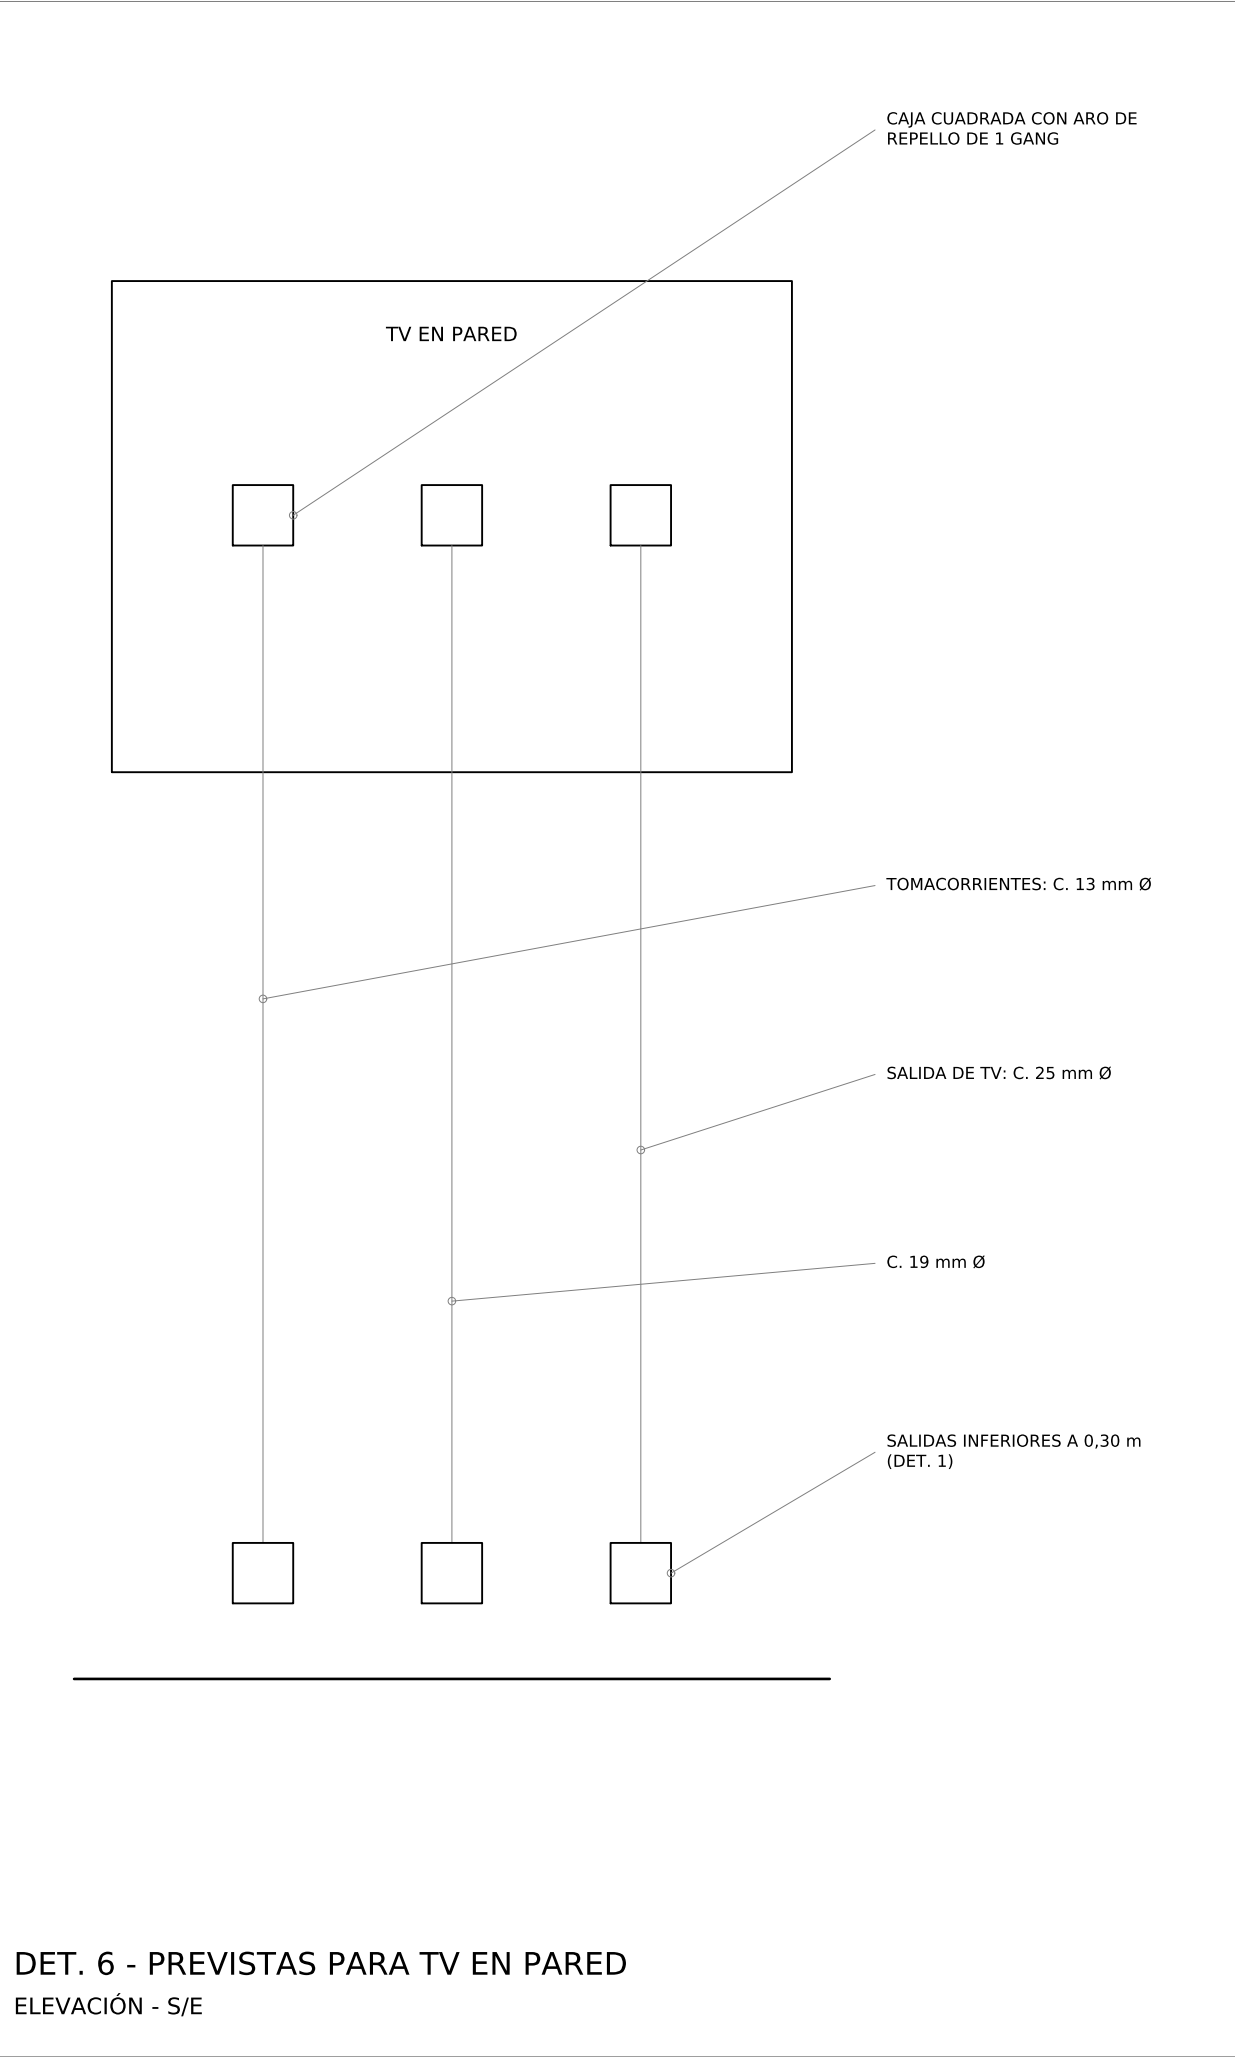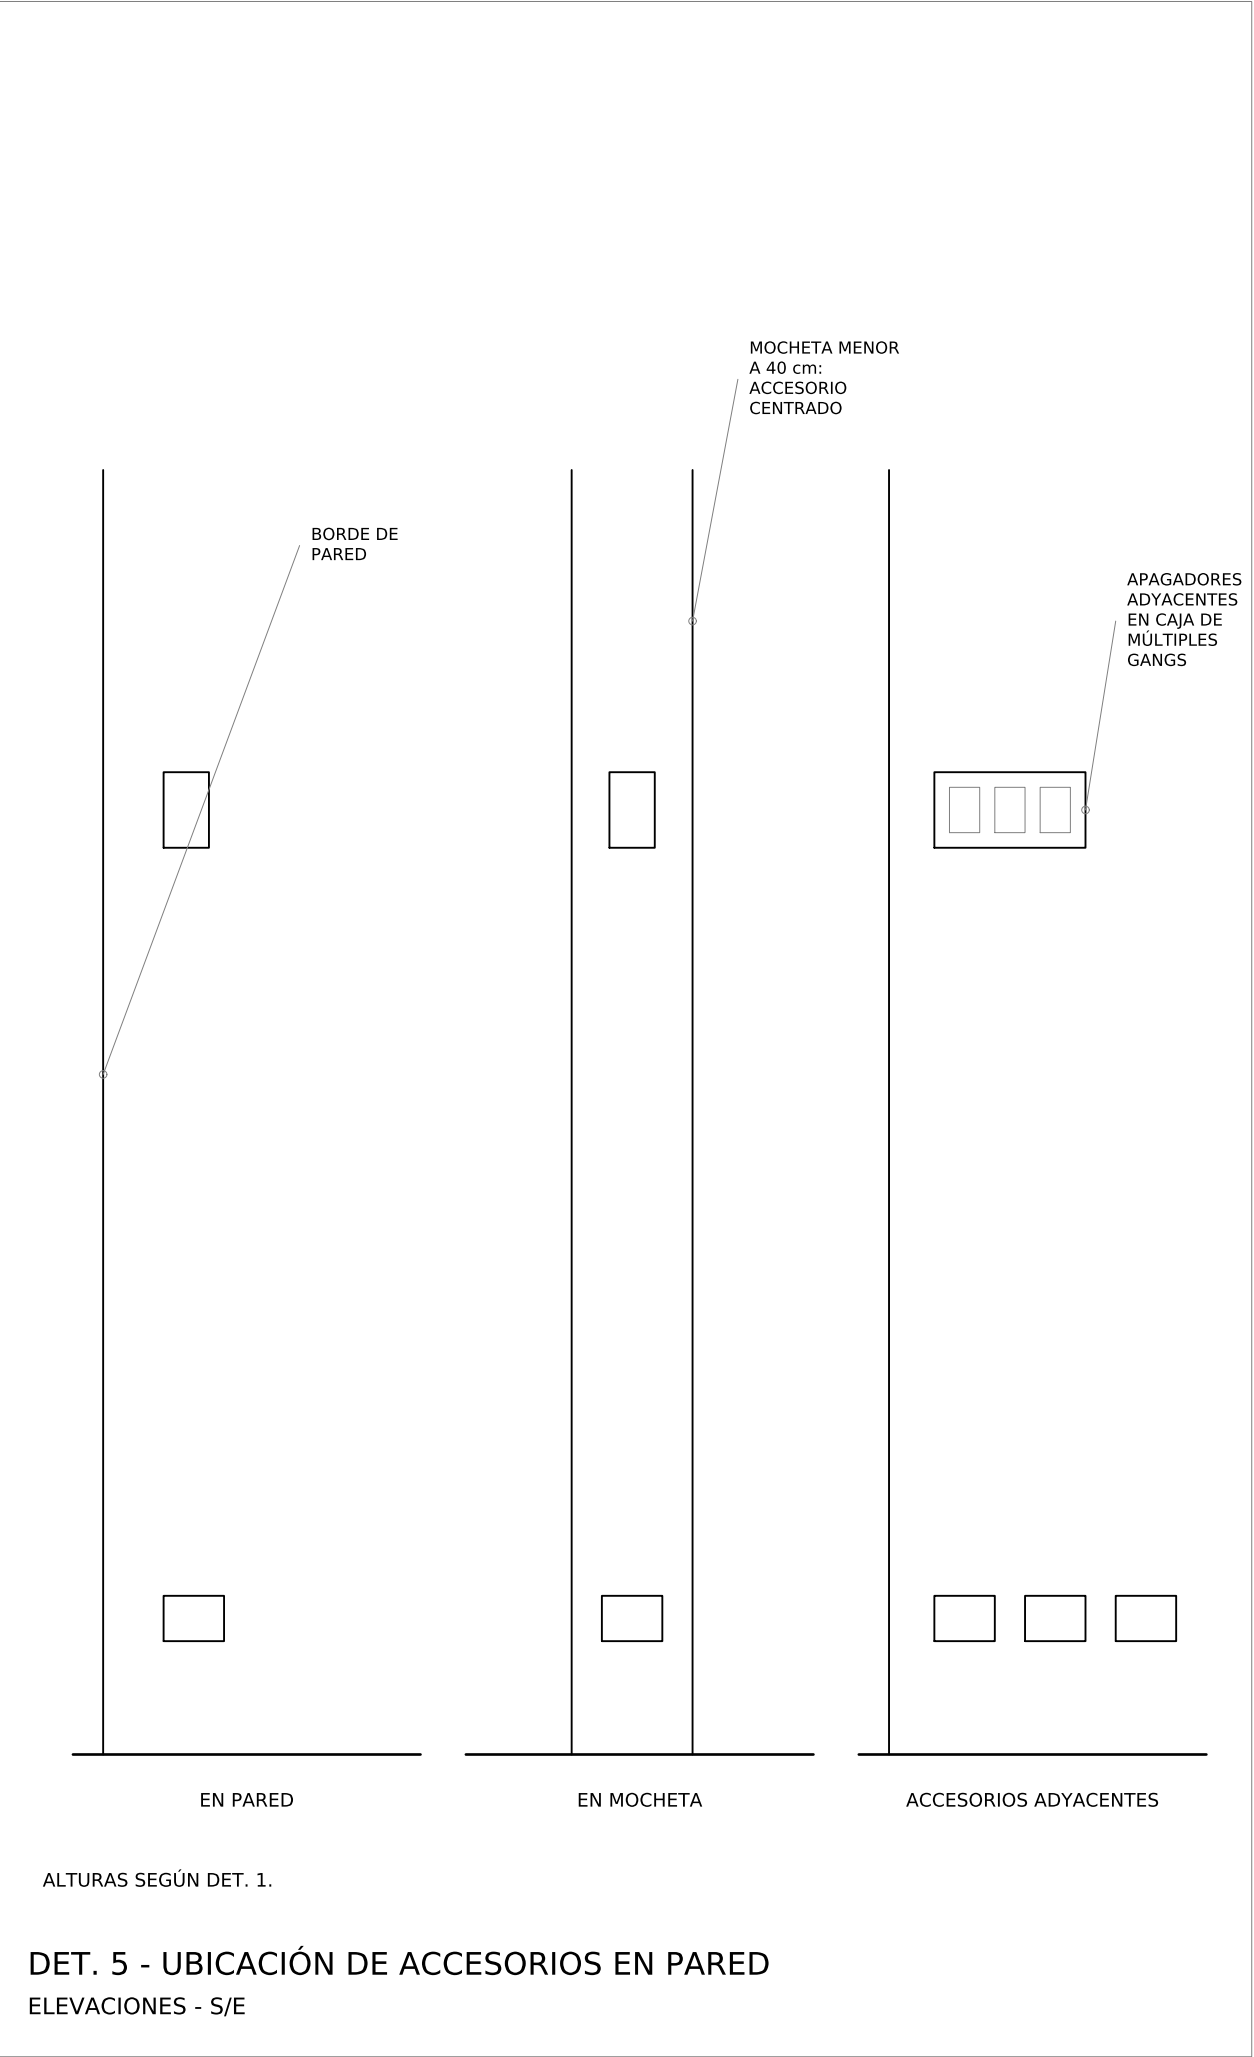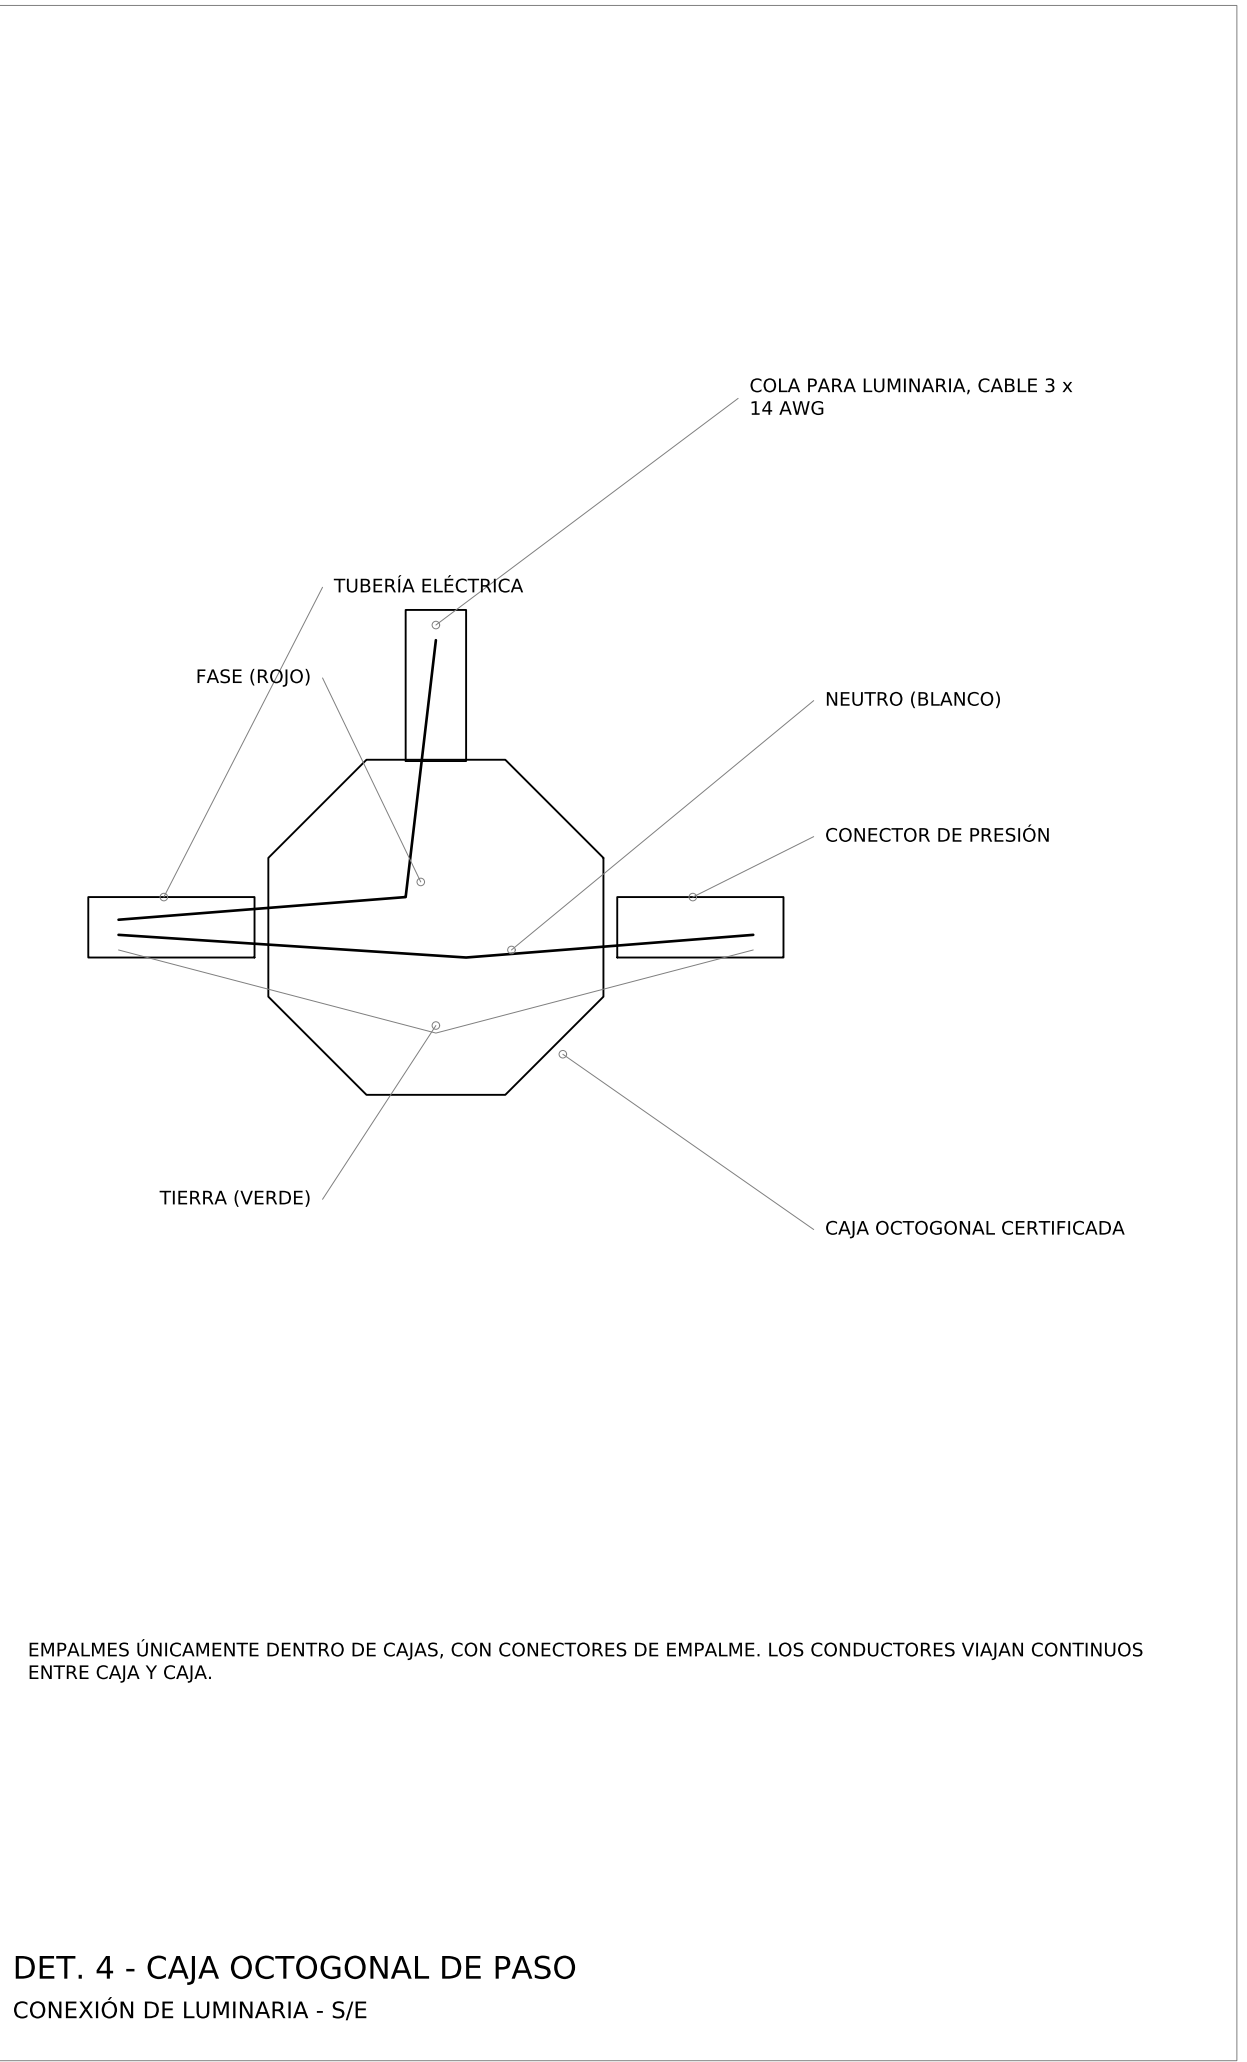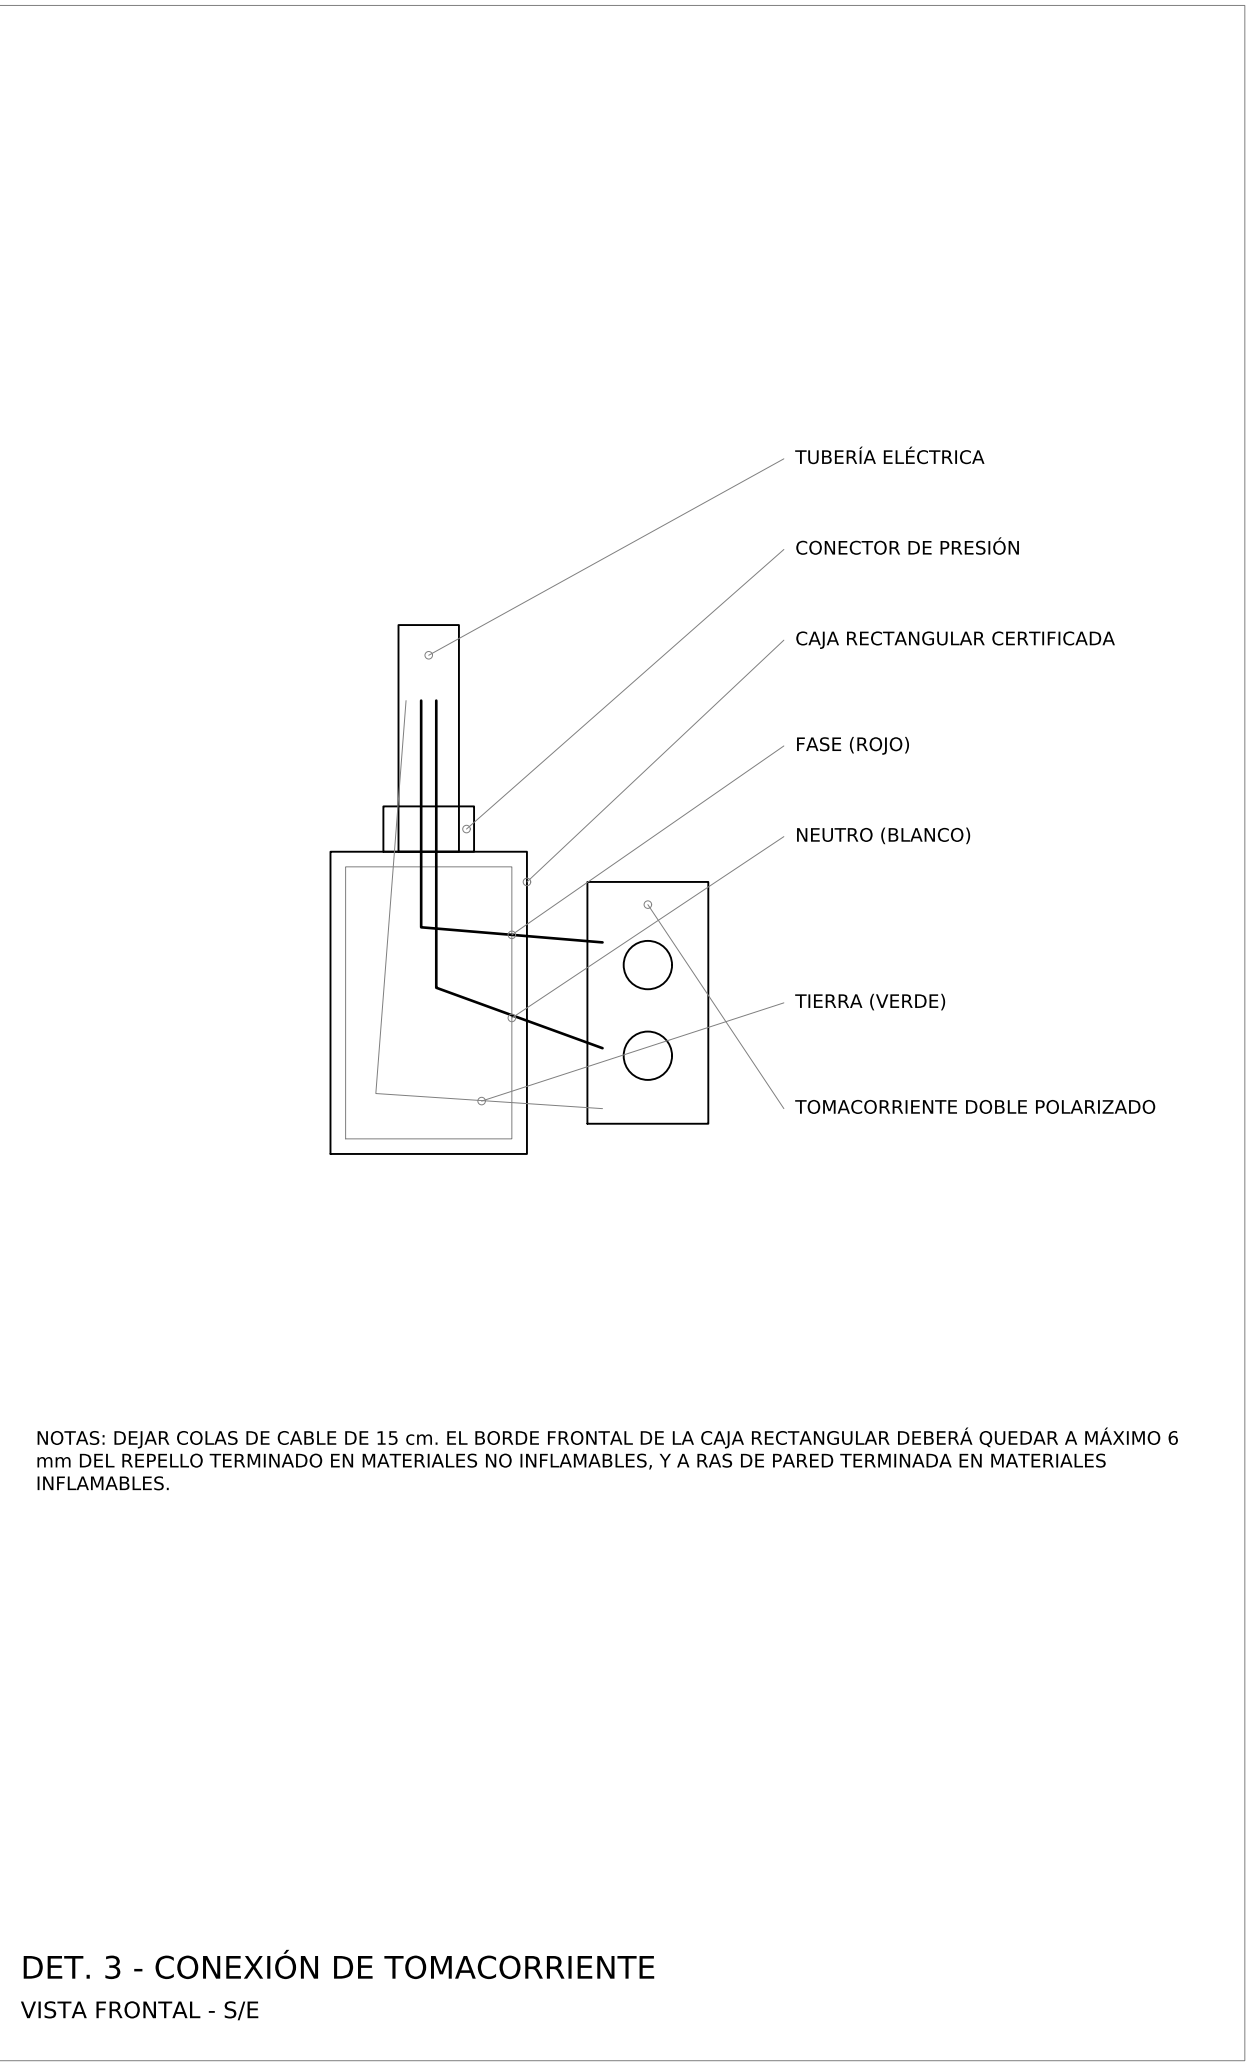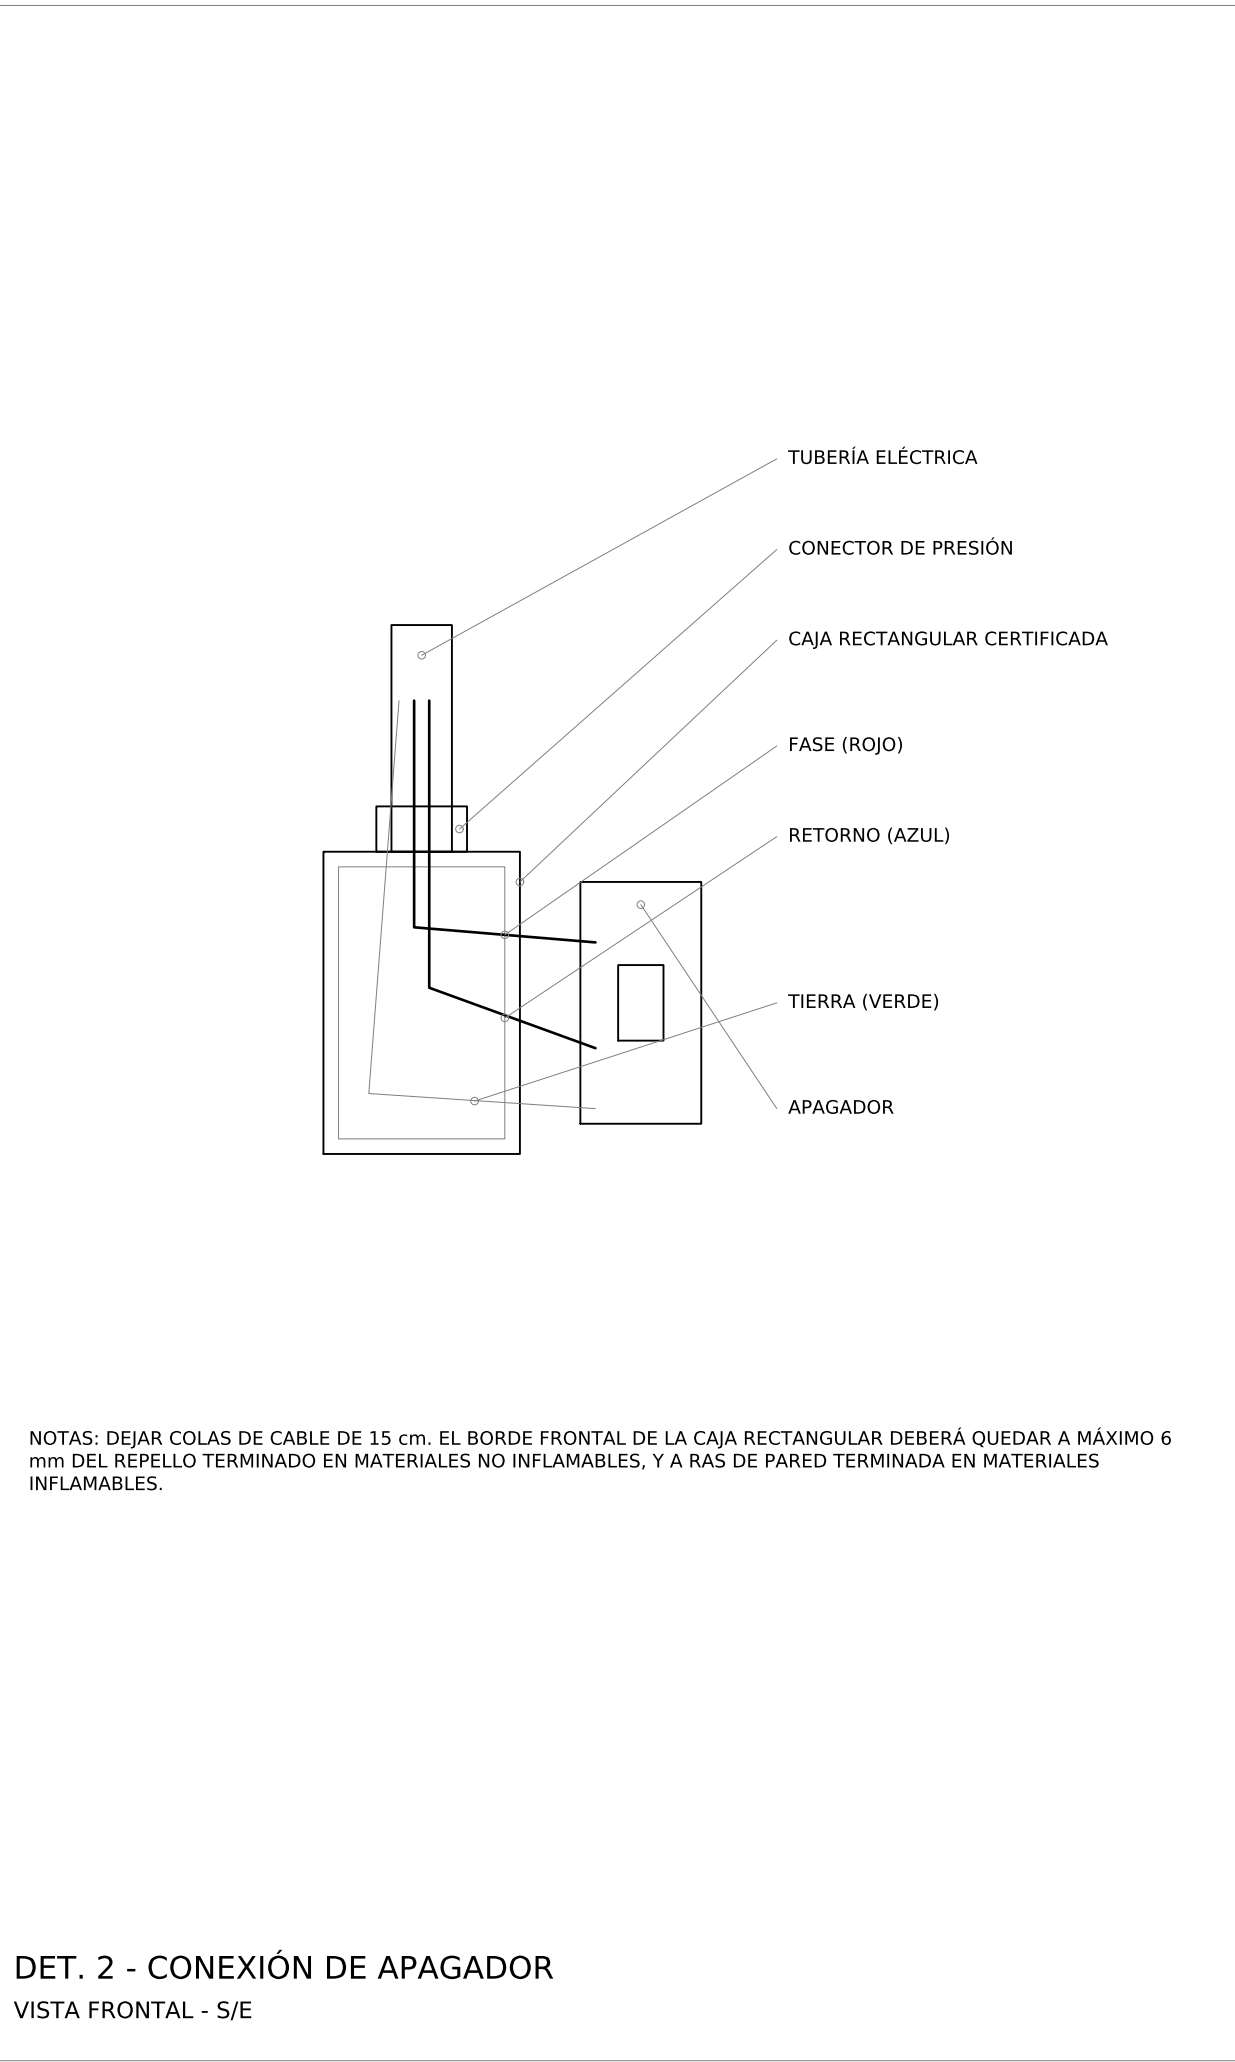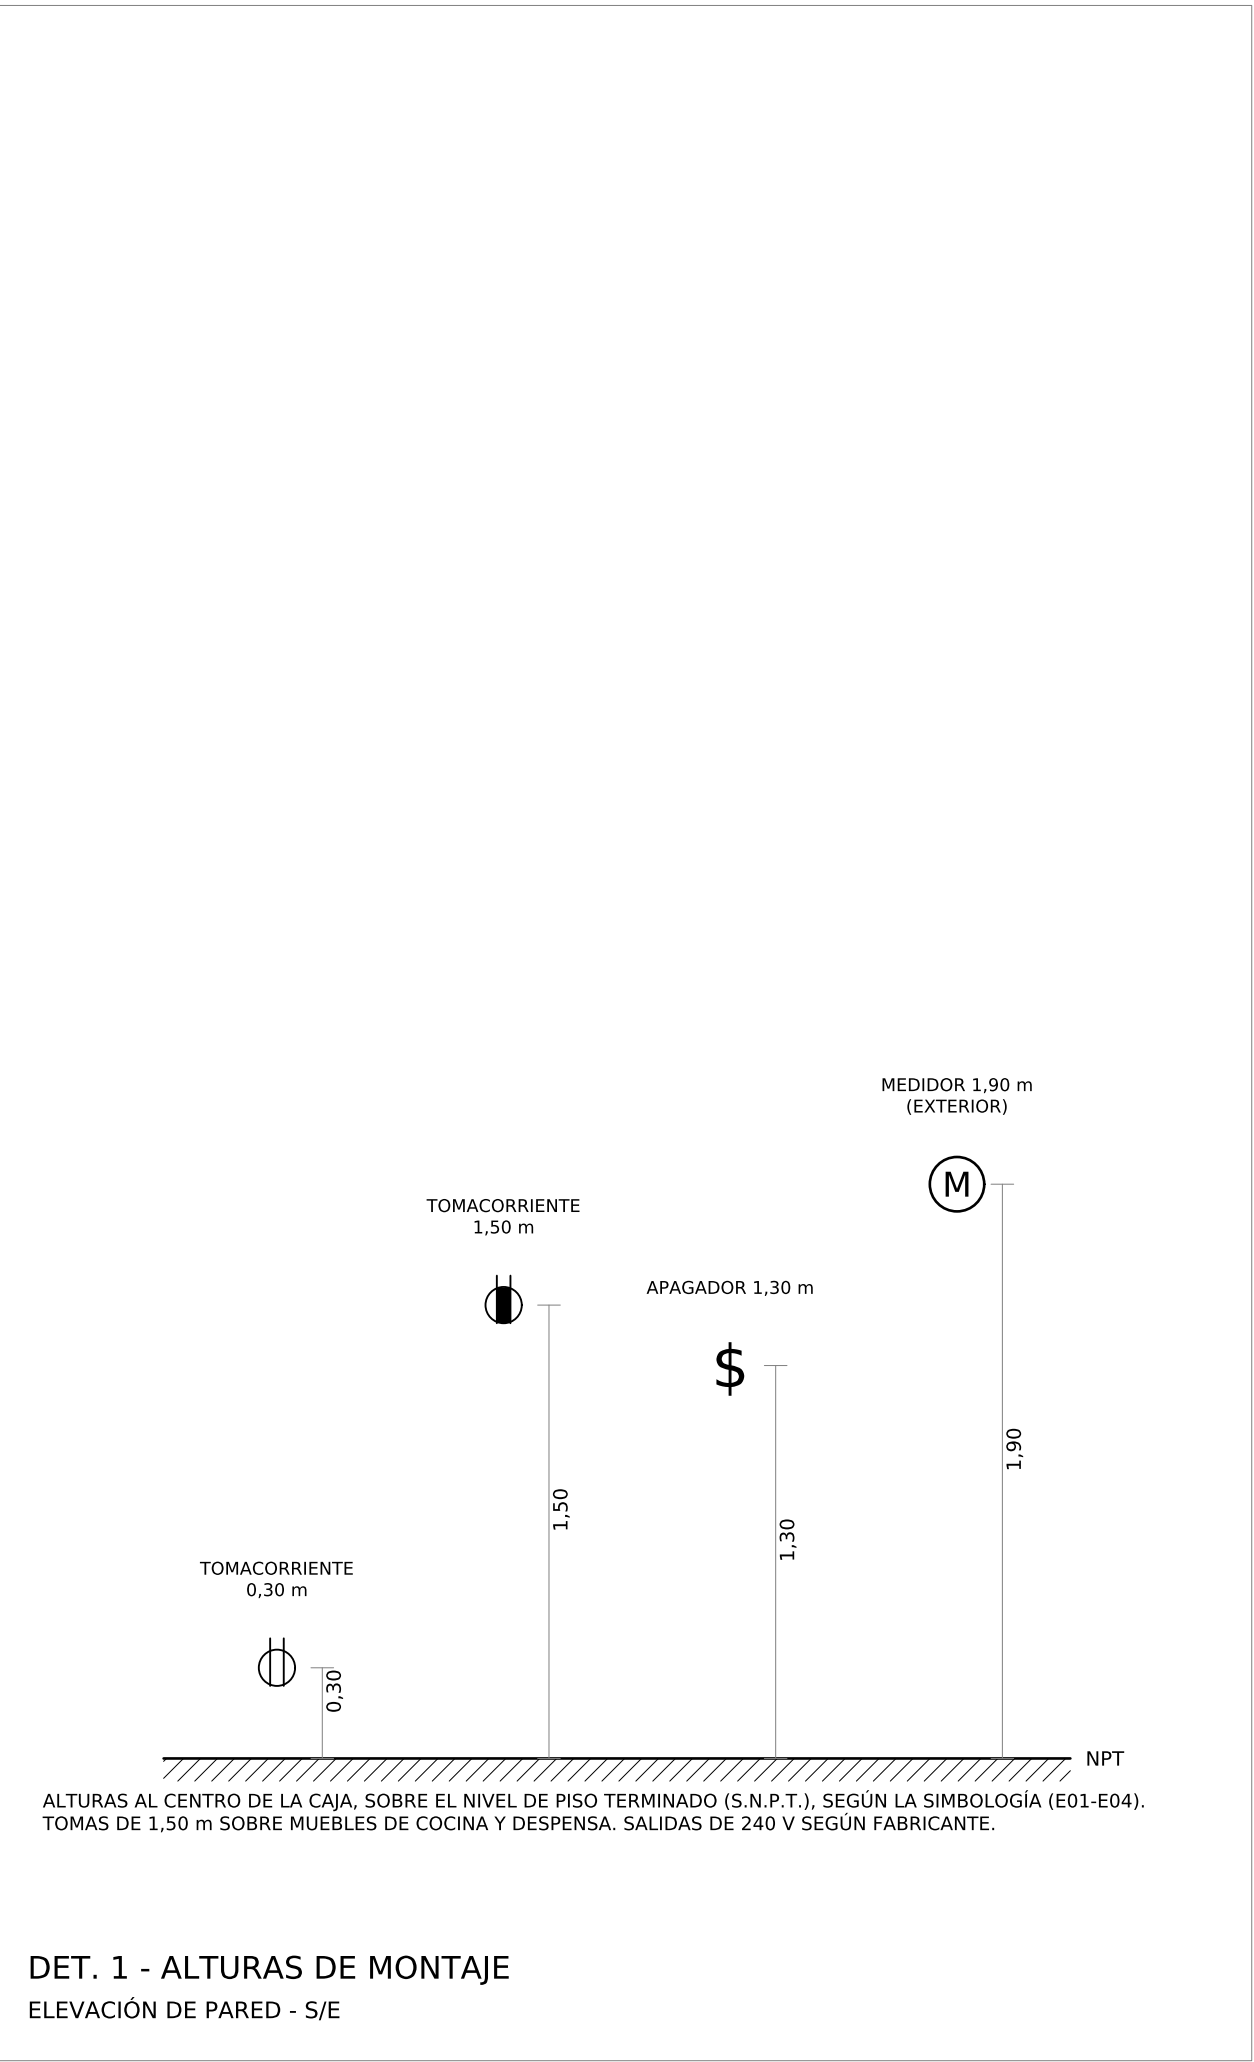

ESPACIO PARA SELLOS Y TIMBRES

CivilCon Diseño y Construcción SRLTDA Céd. Jurídica: 3-102-762712		
PROFESIONAL RESPONSABLE: DIRECTOR TÉCNICO: Steven Viales (Civil) IC-40759 David Barrantes (Electricidad) IE-27499		
PROYECTO: VIVIENDA UNIFAMILIAR DISTRITO 03 SANTIAGO, CANTÓN 05 SAN RAFAEL, PROVINCIA 04 HEREDIA, COSTA RICA.		
INFORMACIÓN REGISTRO PÚBLICO: FOLIO REAL: 4-041200-000 PLANO CATASTRADO: 4-57389-2023 ÁREA SEGÚN CATASTRO: 256 m²		
CONTENIDO: ELECTRICIDAD DETALLES ELÉCTRICOS. CONEXIONES Y ACCESORIOS. ALTURAS DE MONTAJE. ZANJA DE ACOMETIDA. PUESTA A TIERRA.		
ESCALAS: S/E		
CONTROL DE REVISIONES		
REV.	FECHA	DESCRIPCIÓN
0	06-10-2026	VERSIÓN DE TRABAJO PARA REVISIÓN
1	07-10-2026	LISTA DEFINITIVA (22); PARA TRÁMITE
ESTADO:		
PARA TRÁMITE CFIA Y MUNICIPALIDAD		
LUGAR		LÁMINA
COSTA RICA		E05
OCT 2026		TOTAL 22