




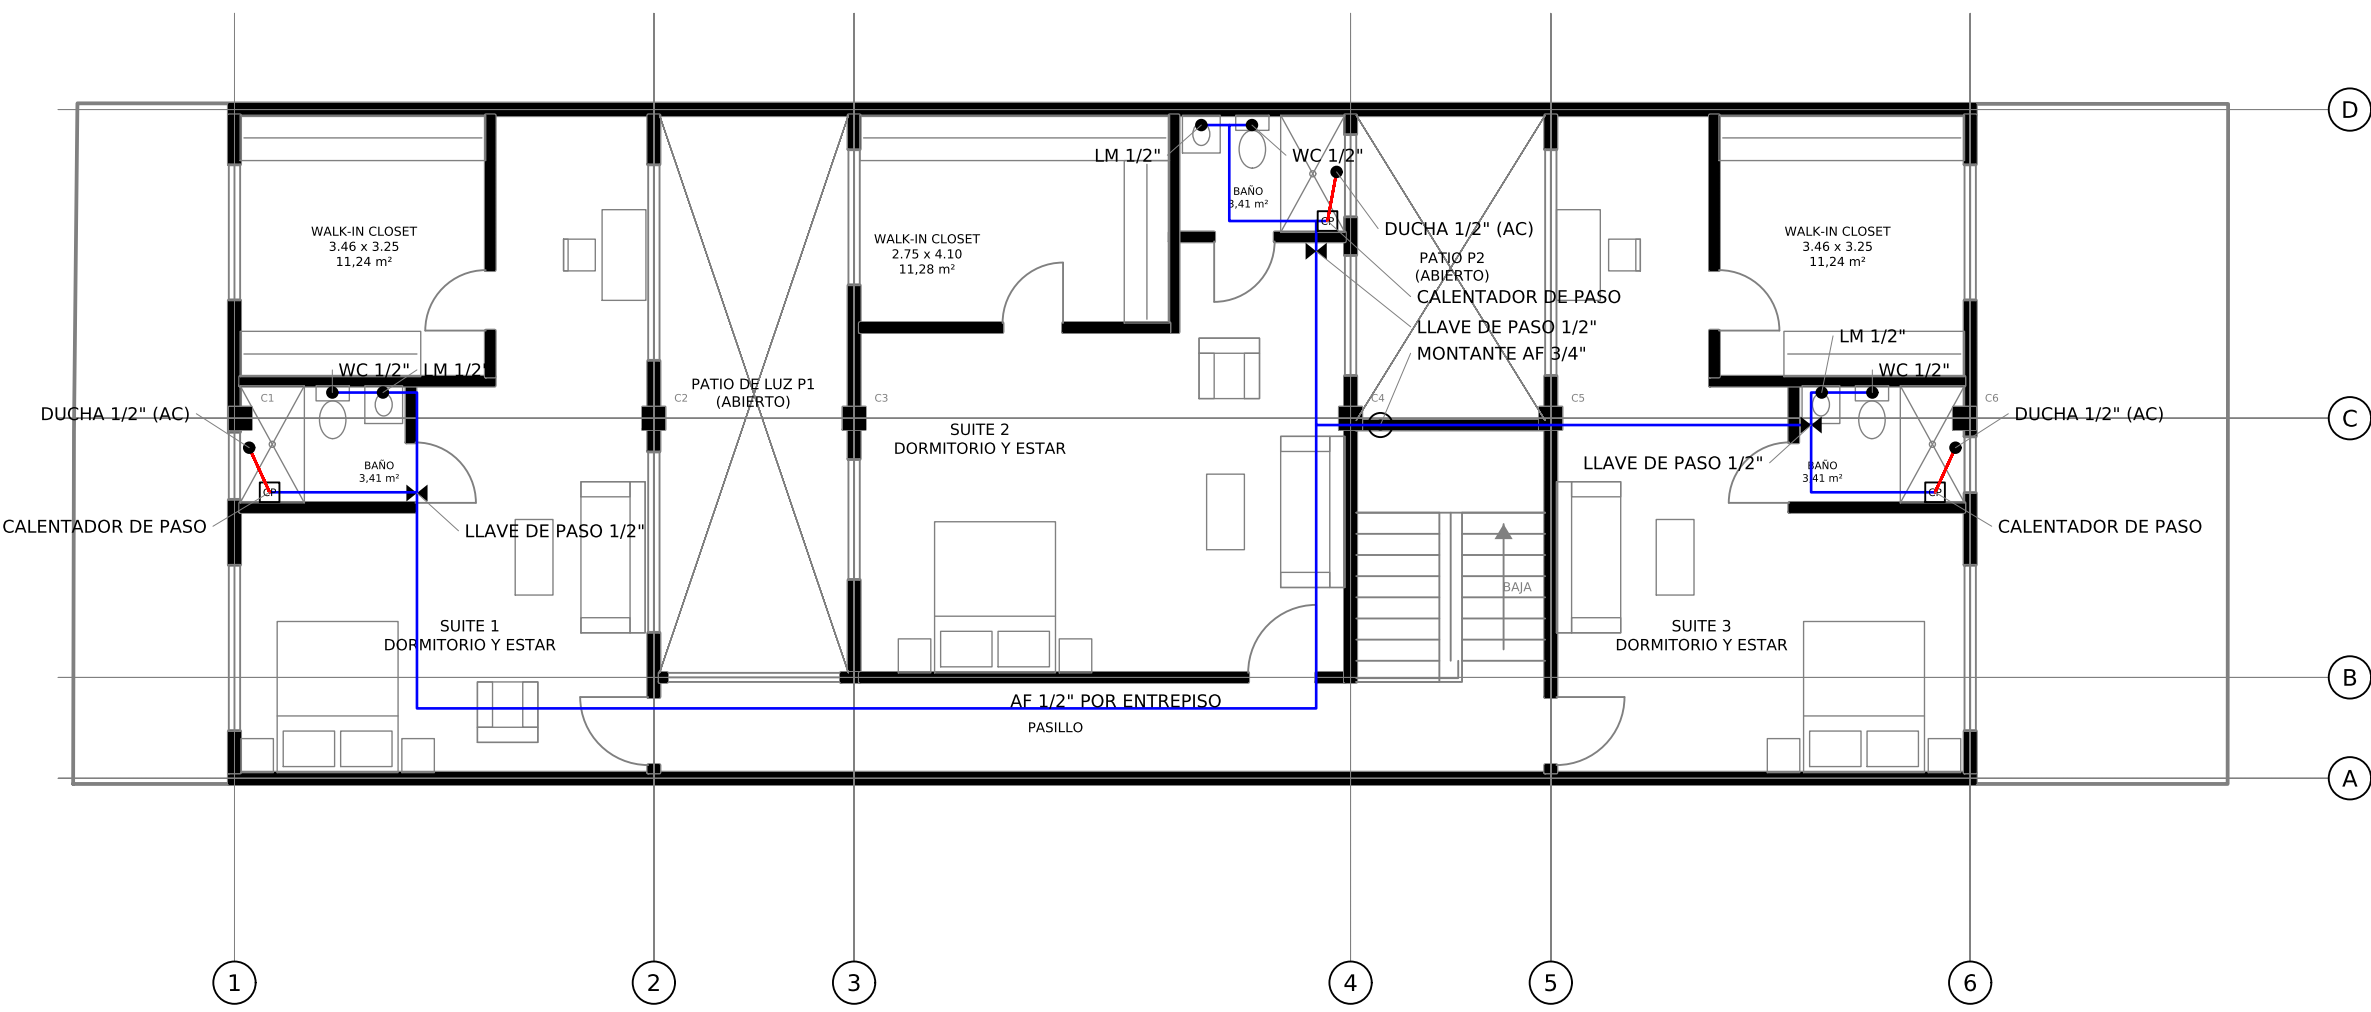

AGUA POTABLE - NIVEL 3
Esc. 1:100

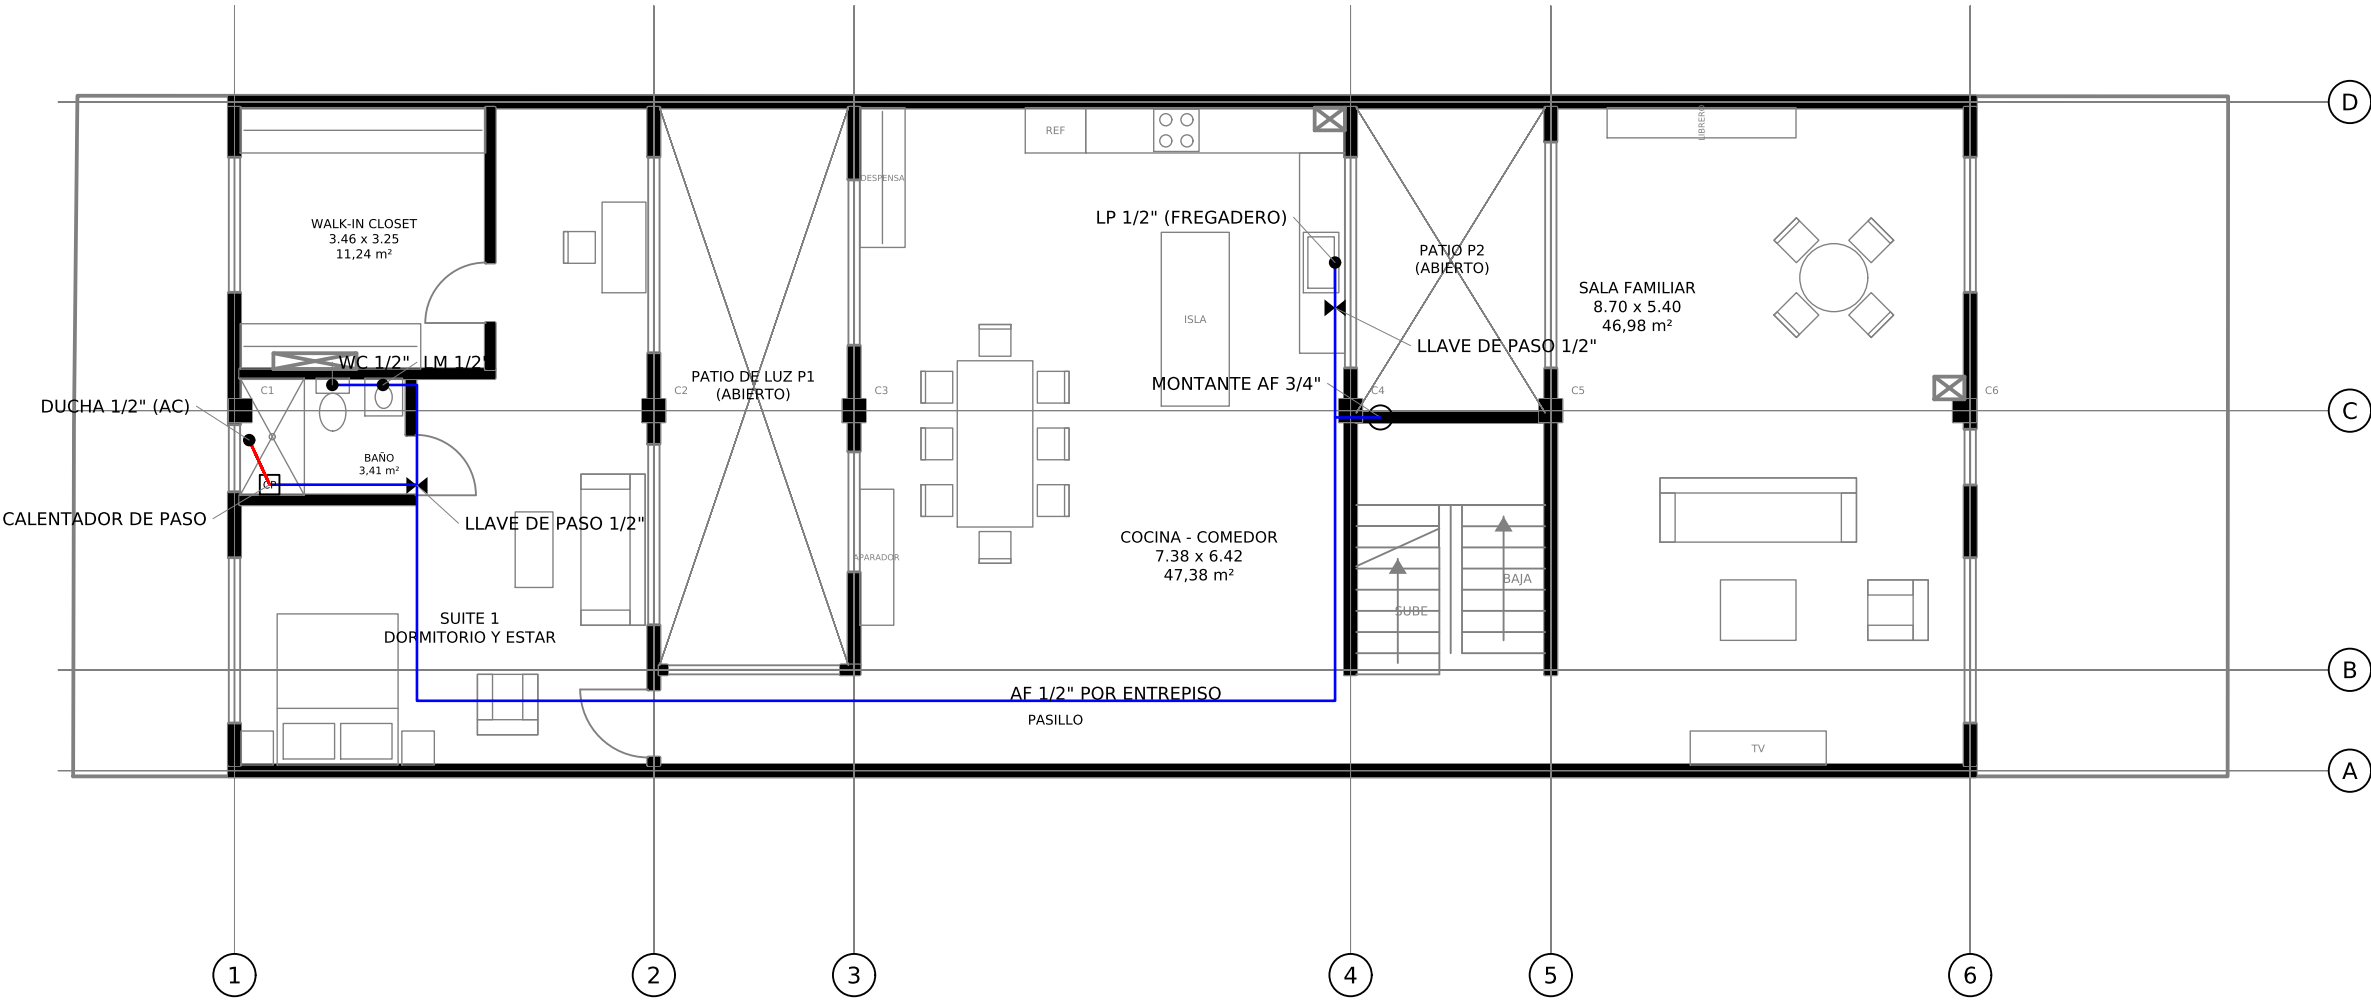

AGUA POTABLE - NIVEL 2
Esc. 1:100

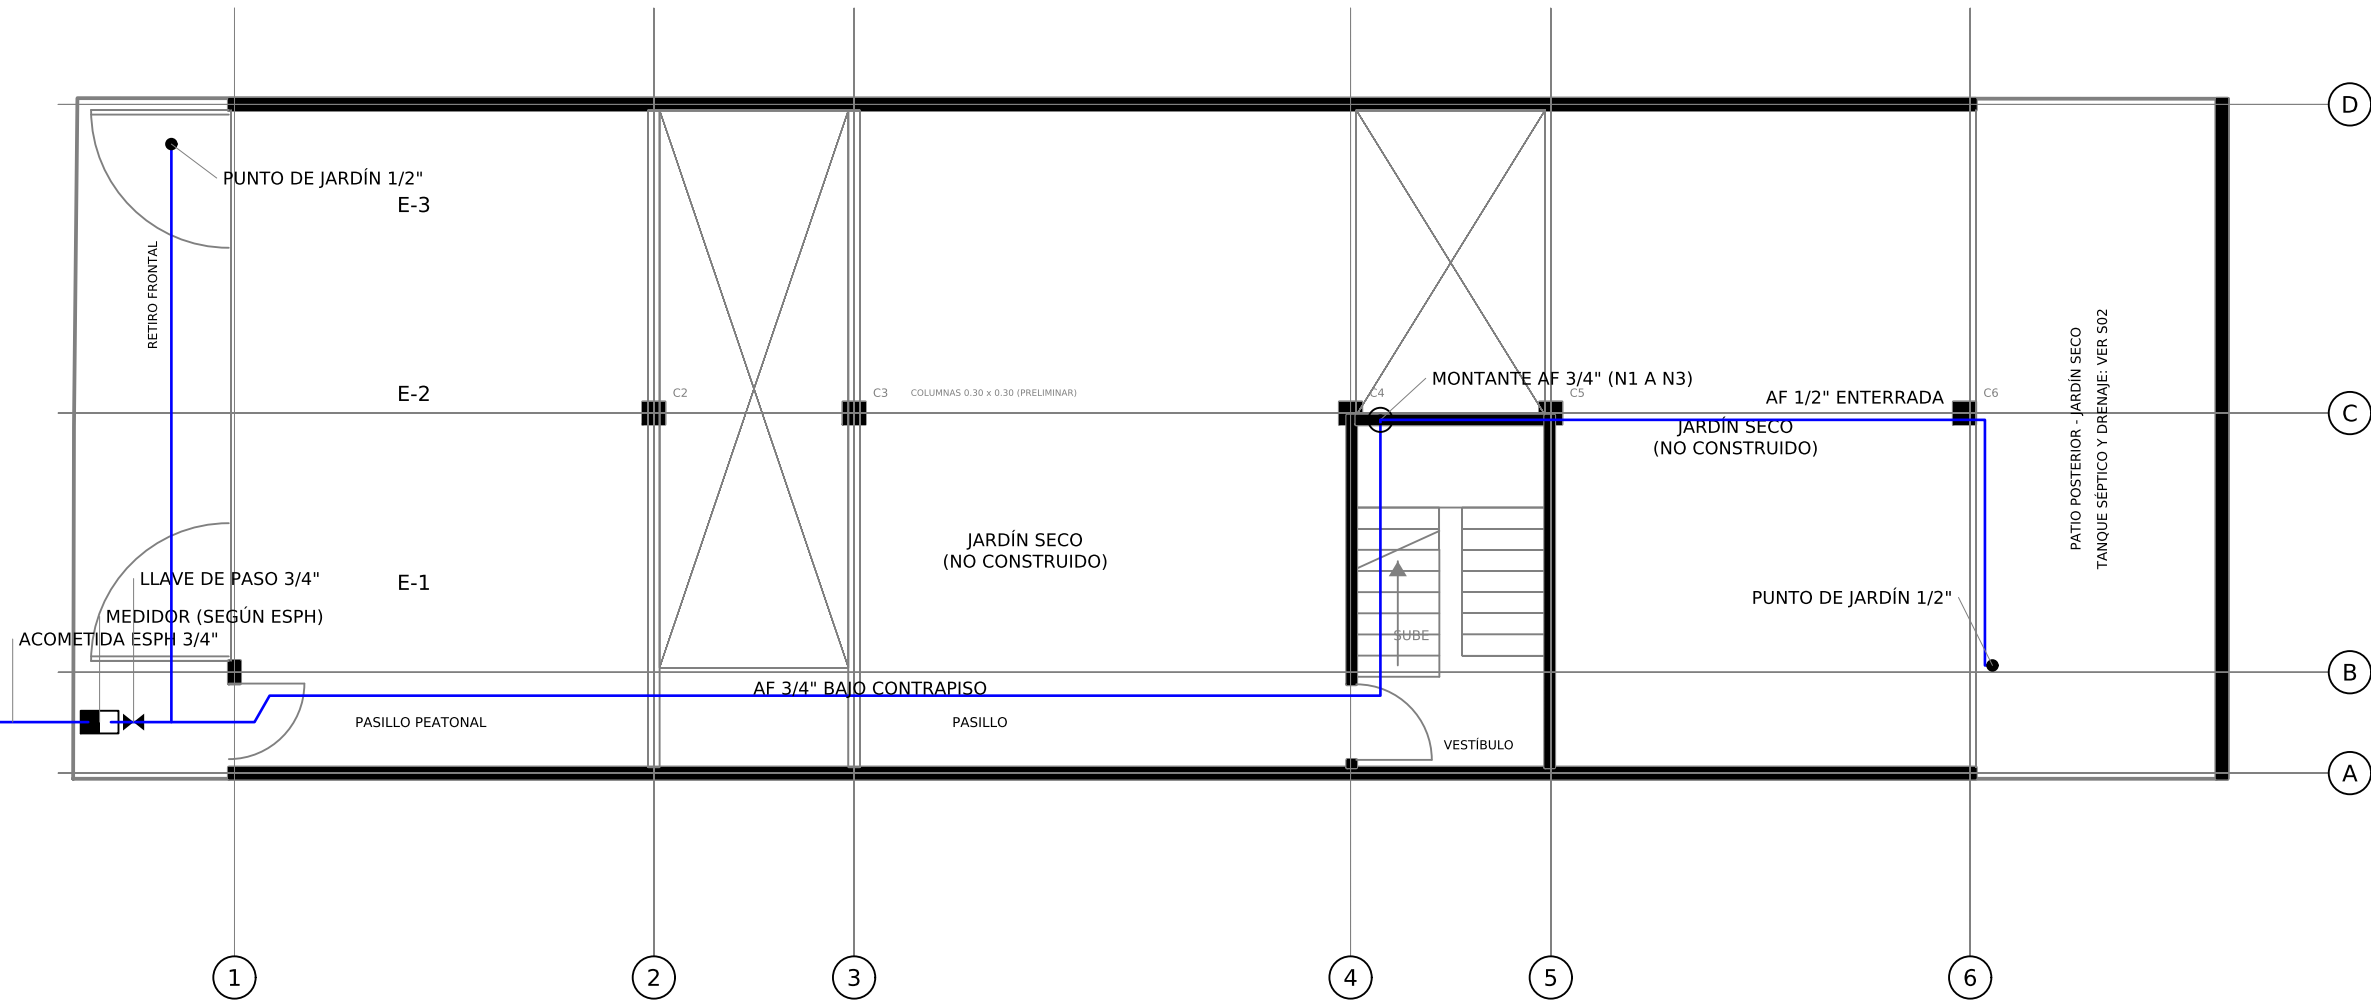


AGUA POTABLE - NIVEL 1
Esc. 1:100


DIAGRAMA VERTICAL DE AGUA POTABLE (ESQUEMÁTICO)



DETALLE 1 - ACOMETIDA Y MEDIDOR
S/E

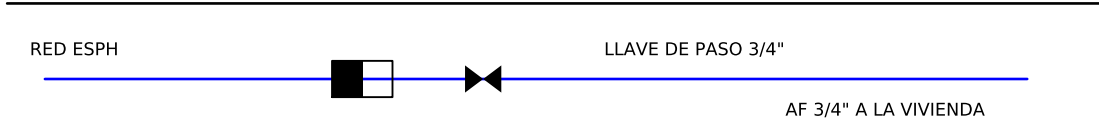

DETALLE 2 - CALENTADOR DE PASO EN DUCHA
ELEVACIÓN - S/E

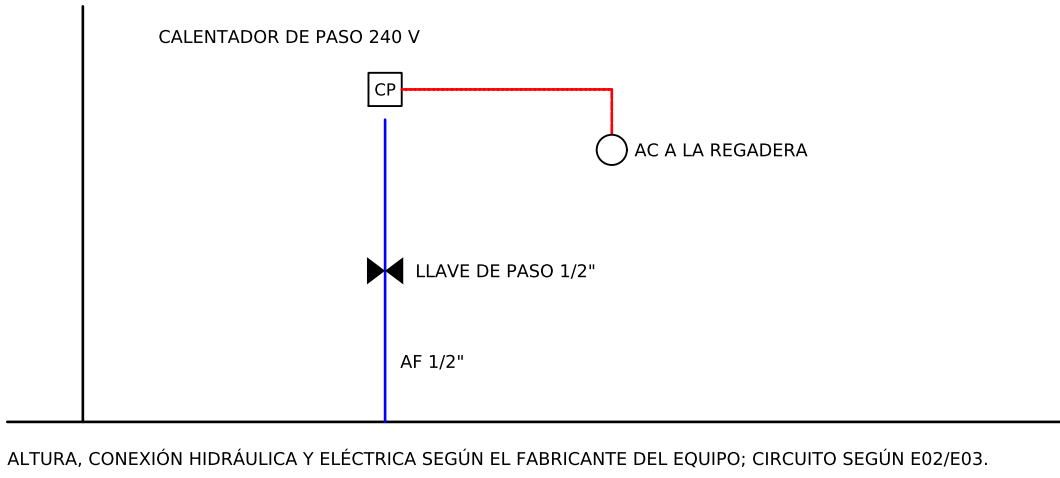

SIMBOLOGÍA

	TUBERÍA DE AGUA FRÍA (PVC A PRESIÓN)
	TUBERÍA DE AGUA CALIENTE (CPVC), SOLO DUCHAS
	LLAVE DE PASO
	SALIDA A APARATO (DIÁMETRO INDICADO)
	MONTANTE
	MEDIDOR DE AGUA (SEGÚN ESPH)
	CALENTADOR DE PASO ELÉCTRICO

LM: LAVATORIO; WC: INODORO; LP: FREGADERO; AF / AC: AGUA FRÍA / CALIENTE.

NOTAS:

- 1.- TODAS LAS MEDIDAS ESTÁN DADAS EN METROS, SALVO ALGUNA EXCEPCIÓN INDICADA.
- 2.- EL AGUA POTABLE PROVIENE DEL SISTEMA PÚBLICO (ESPH), DIRECTAMENTE DE LA CONEXIÓN DE LA CALLE, SIN TANQUE DE ALMACENAMIENTO NI EQUIPO DE BOMBEO.
- 3.- DIÁMETROS: ACOMETIDA, TRAMO PRINCIPAL Y MONTANTE 3/4"; RAMALES Y SALIDAS 1/2". LLAVE DE PASO EN CADA BAÑO Y EN LA COCINA.
- 4.- AGUA CALIENTE ÚNICAMENTE EN LAS DUCHAS, MEDIANTE UN CALENTADOR DE PASO ELÉCTRICO POR BAÑO (CIRCUITOS EN E02 Y E03).
- 5.- TUBERÍA DE AGUA FRÍA PVC A PRESIÓN Y DE AGUA CALIENTE CPVC.
- 6.- EL MONTANTE SUBE EMBEBIDO EN EL MURO DEL EJE C (ESCALERA / PATIO P2); LOS RAMALES DE LOS NIVELES 2 Y 3 VIAJAN POR EL ENTREPISO.
- 7.- PROBAR LA RED A PRESIÓN ANTES DE CERRAR PAREDES Y CIELOS.

ESPACIO PARA SELLOS Y TIMBRES

CivilCon Diseño y Construcción SRLTDA
Céd. Jurídica: 3-102-762712

PROFESIONAL RESPONSABLE:
DIRECTOR TÉCNICO:
Steven Viales (Civil) IC-40759
David Barrantes (Electricidad) IE-27499

PROYECTO:
VIVIENDA UNIFAMILIAR
DISTRITO 03 SANTIAGO, CANTÓN 05 SAN RAFAEL,
PROVINCIA 04 HEREDIA, COSTA RICA.

INFORMACIÓN REGISTRO PÚBLICO:
FOLIO REAL: 4-041200-000
PLANO CATASTRADO: 4-57389-2023
ÁREA SEGÚN CATASTRO: 256 m²

CONTENIDO:
AGUA POTABLE
PLANTAS NIVELES 1, 2 Y 3.
DIAGRAMA VERTICAL.
DETALLES.
SIMBOLOGÍA.
NOTAS.

ESCALAS: 1:100 / S/E


CONTROL DE REVISIONES

REV.	FECHA	DESCRIPCIÓN
0	06-10-2026	VERSIÓN DE TRABAJO PARA REVISIÓN
1	07-10-2026	PUNTO DE JARDÍN POSTERIOR TRASLADADO (S02)
2	07-10-2026	LISTA DEFINITIVA (22); PARA TRÁMITE


ESTADO:

PARA TRÁMITE
CFIA Y MUNICIPALIDAD


LUGAR	LÁMINA
COSTA RICA	S01
OCT 2026	TOTAL 22

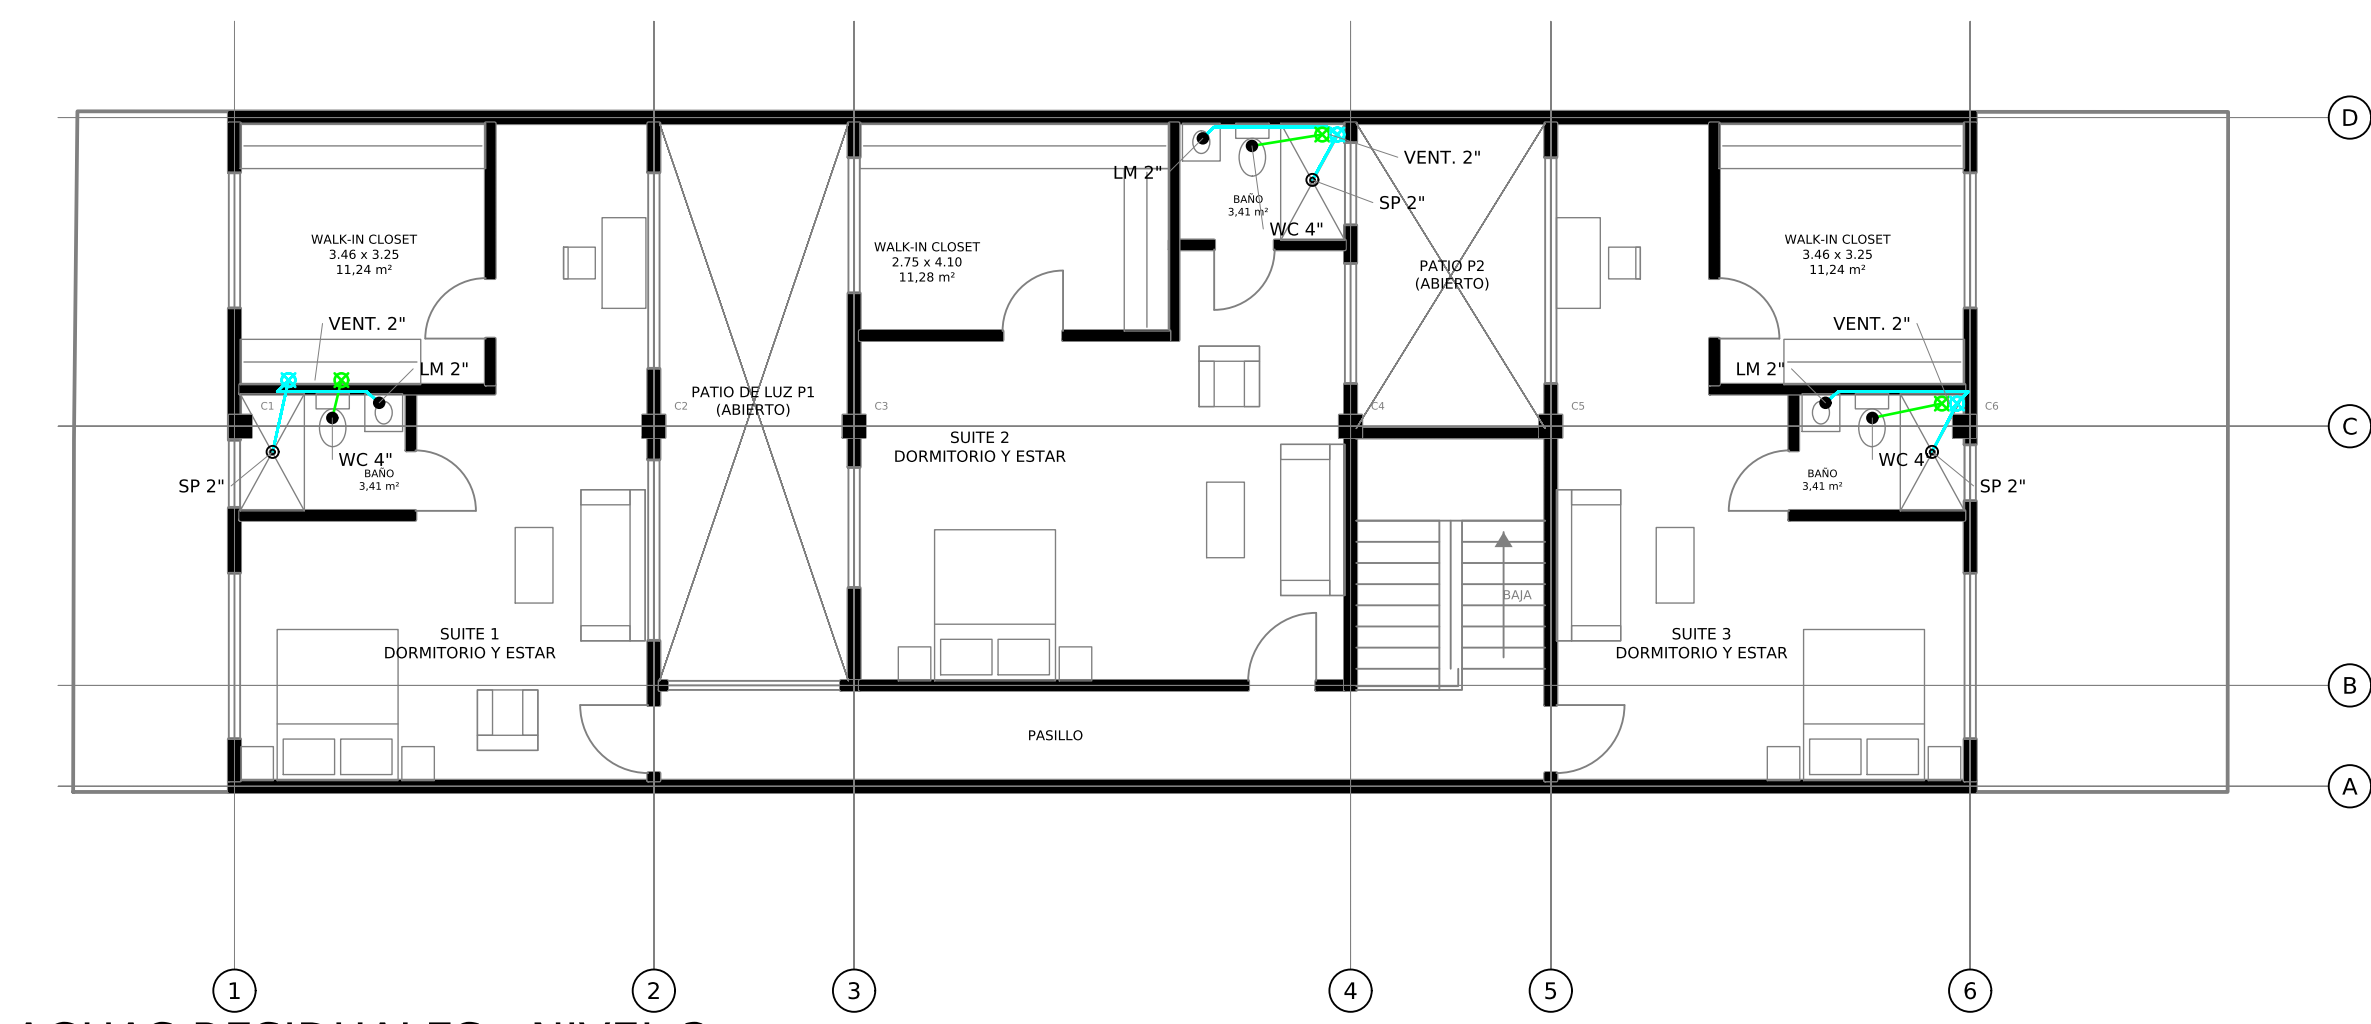

AGUAS RESIDUALES - NIVEL 3
Esc. 1:100

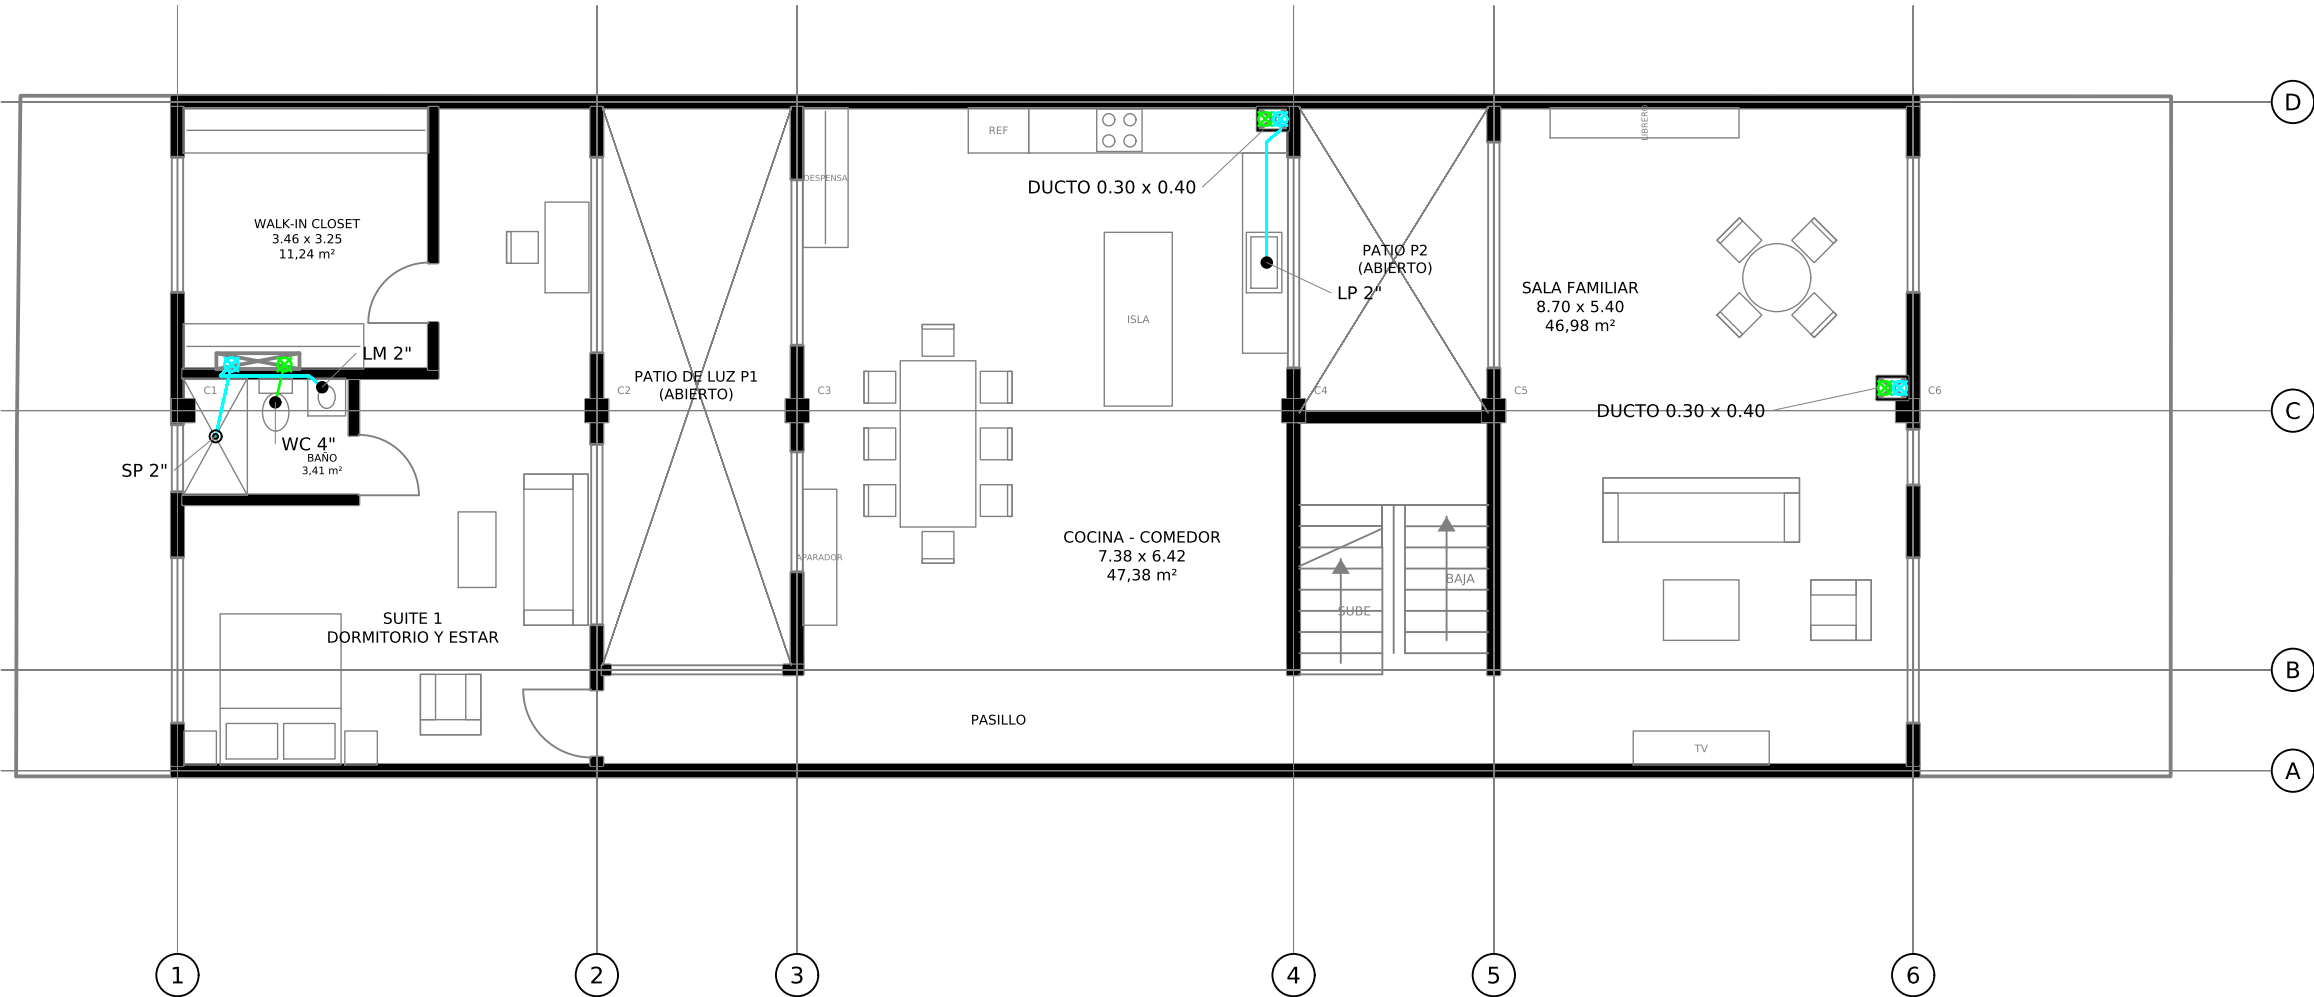


AGUAS RESIDUALES - NIVEL 2
Esc. 1:100

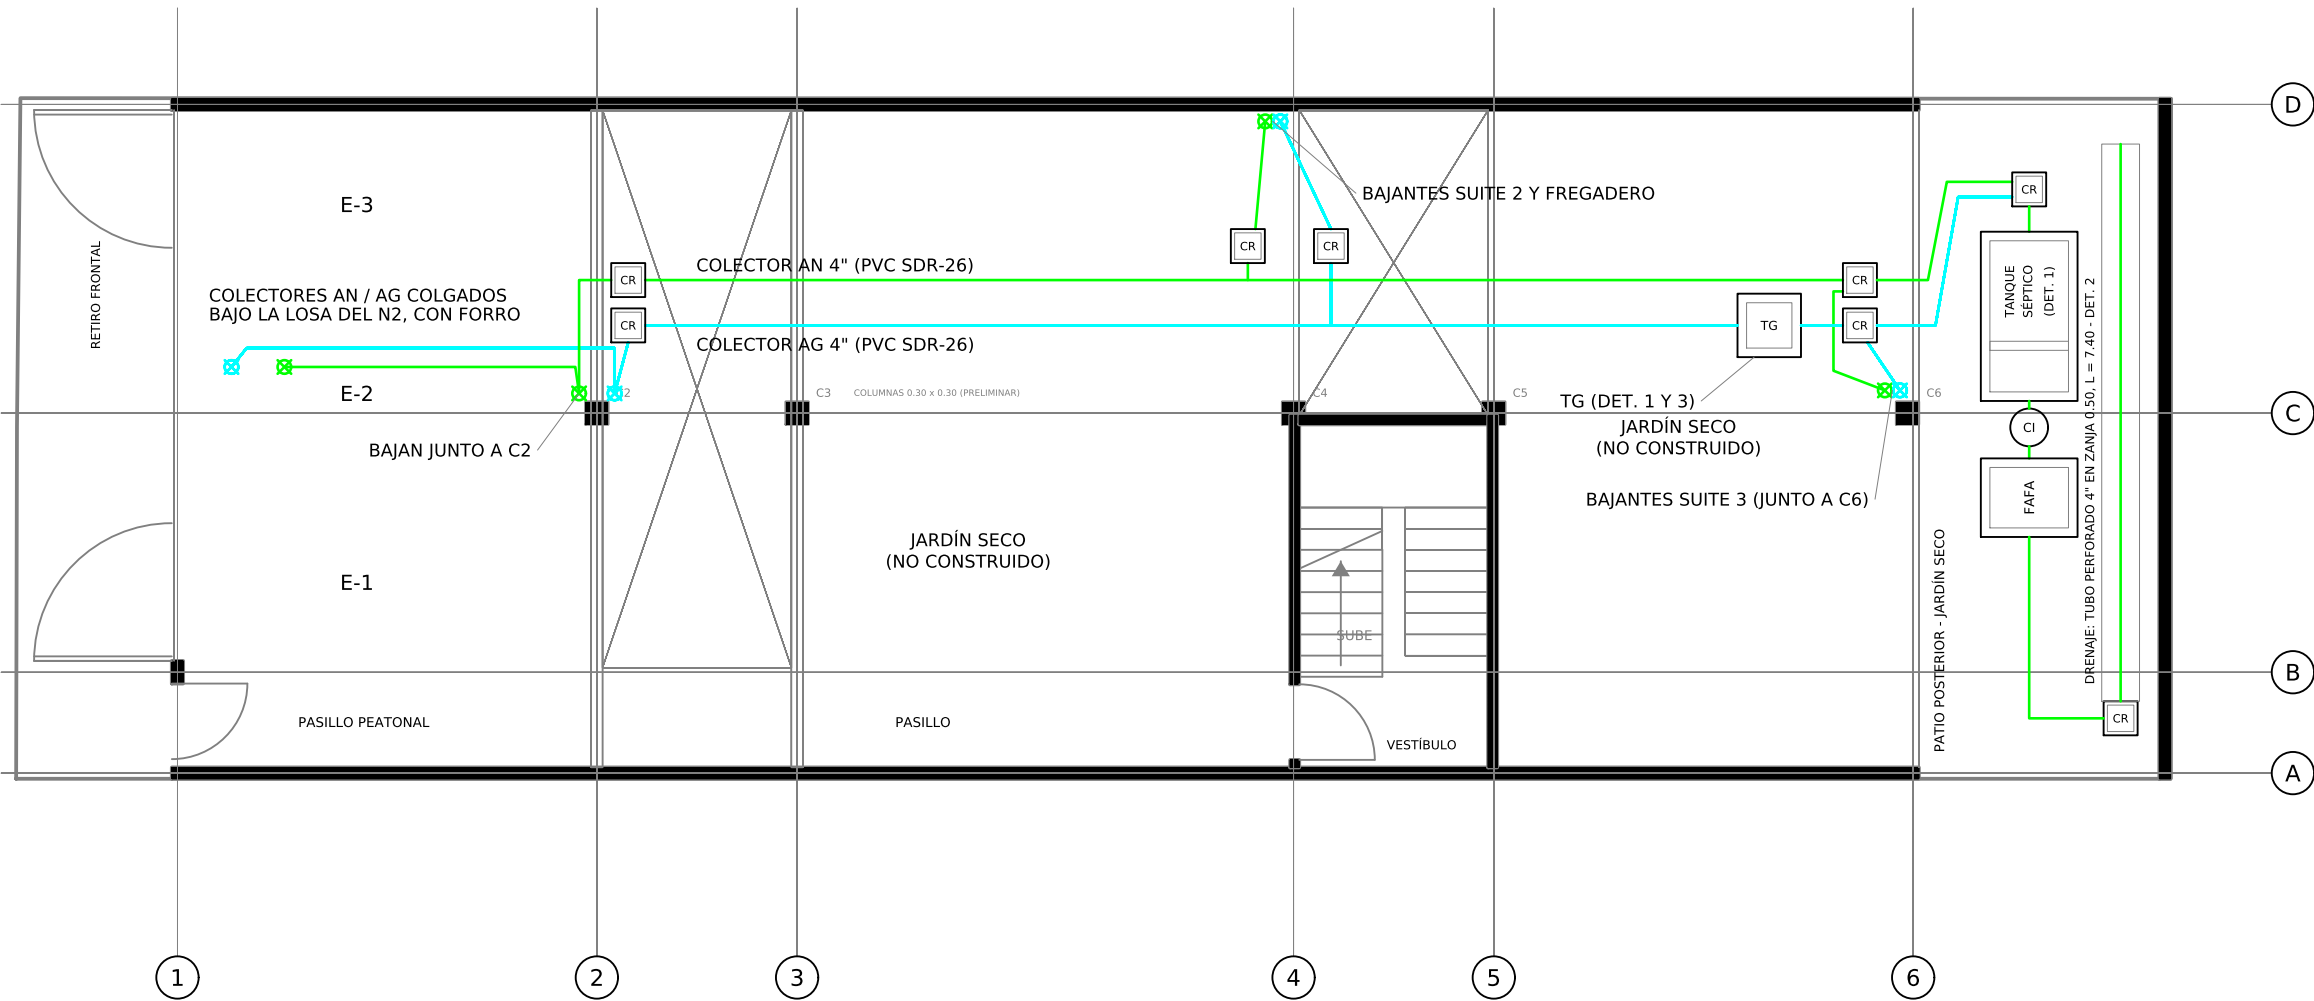


AGUAS RESIDUALES - NIVEL 1
Esc. 1:100

DETALLE 1 - TANQUE SÉPTICO
Esc. 1:30 - COTAS EN METROS

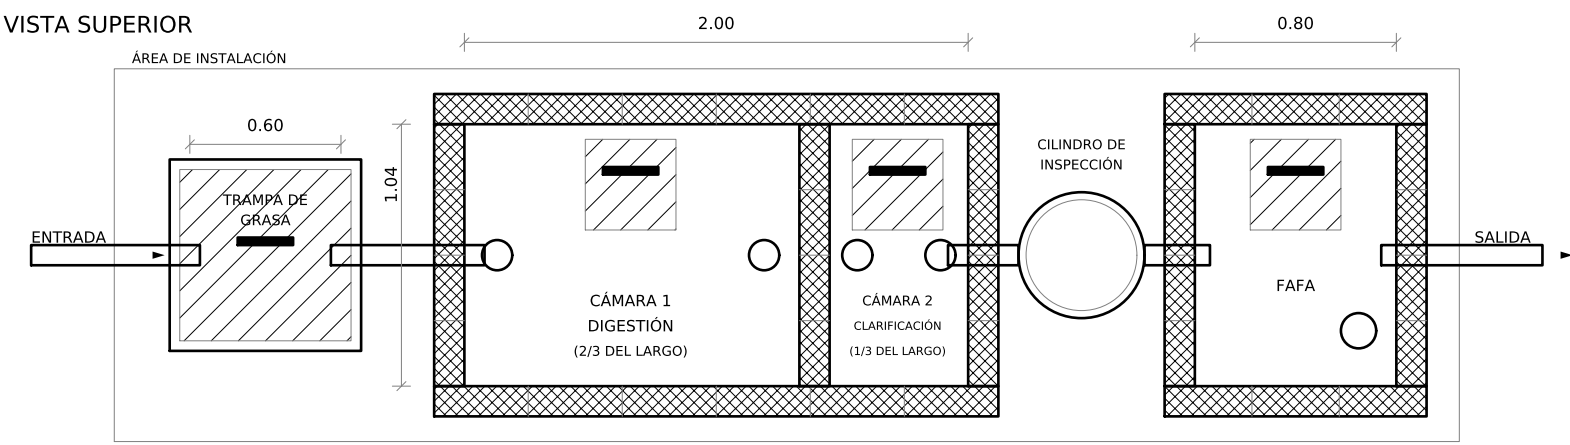


VISTA LATERAL

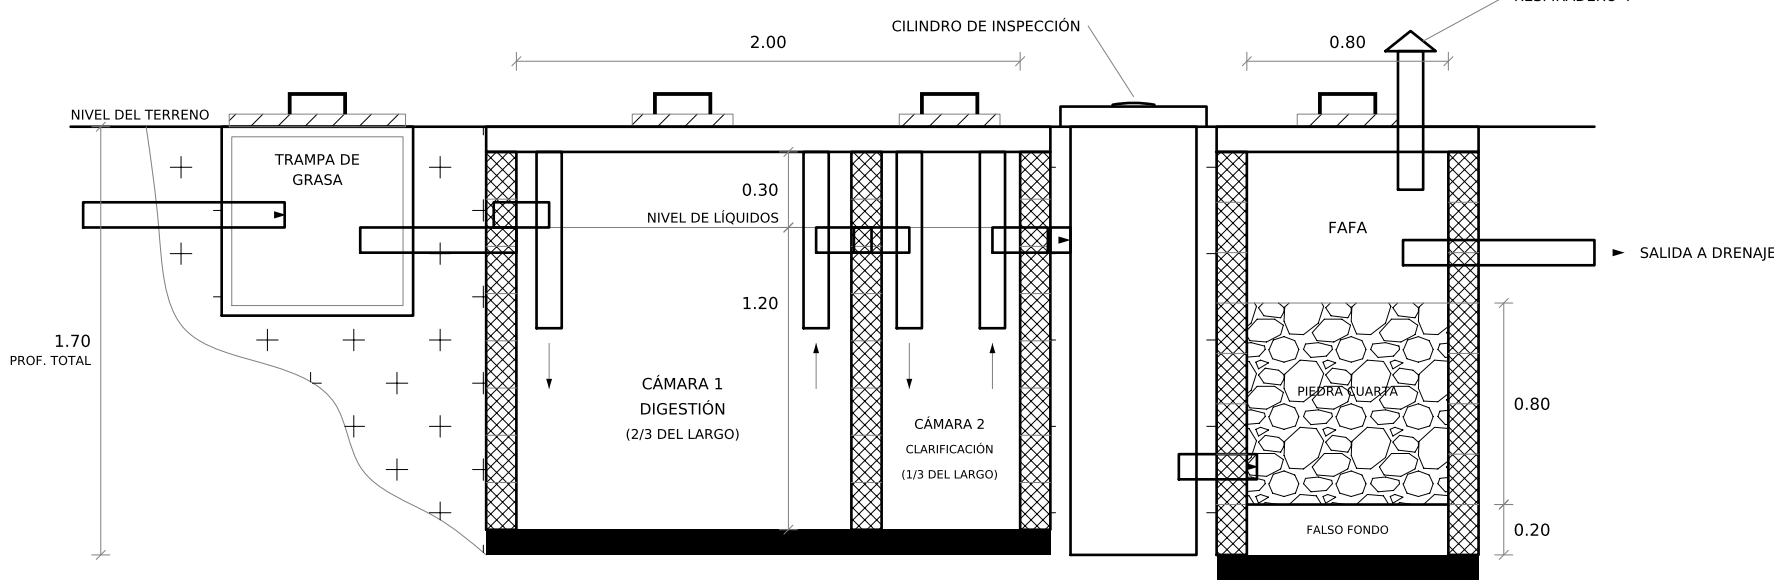


ESQUEMA: LA TRAMPA DE GRASA SE UBICA EN EL COLECTOR AG Y LAS AGUAS NEGRAS ENTRAN POR LA CR DE ENTRADA (VER PLANTA N1).


DETALLE 3 - CAJA DE REGISTRO Y TRAMPA DE GRASA
SECCIONES - S/E

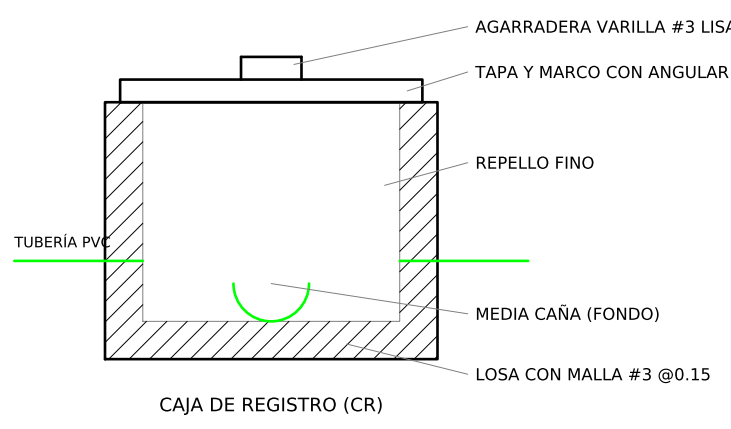

DETALLE 4 - BAÑO TÍPICO
SUITE 1 (N2 Y N3), SUITE 3 EN ESPEJO - Esc. 1:40

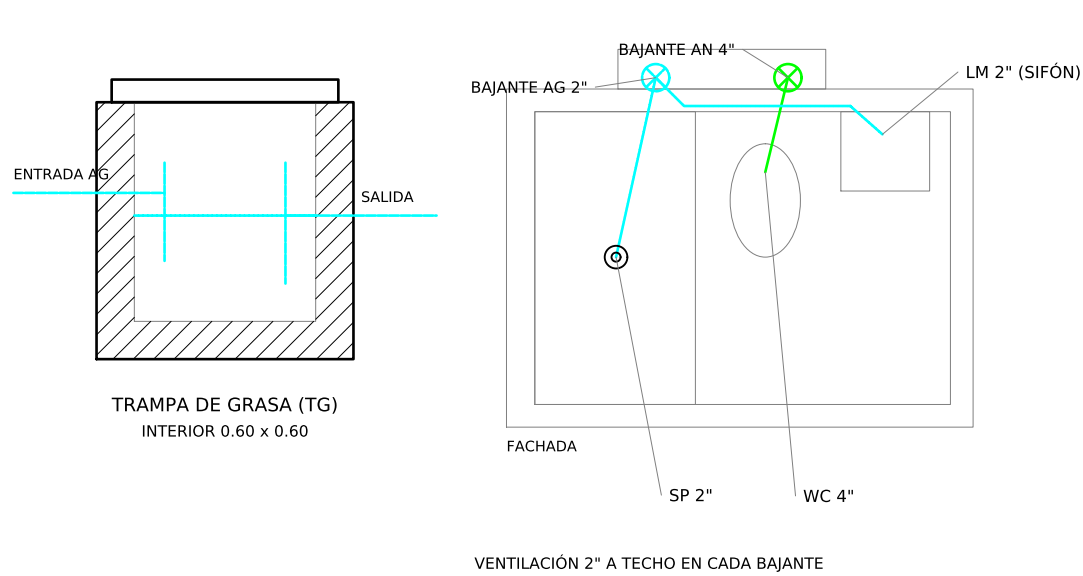

DETALLE 2 - SECCIÓN DE DRENAJE
Esc. 1:10

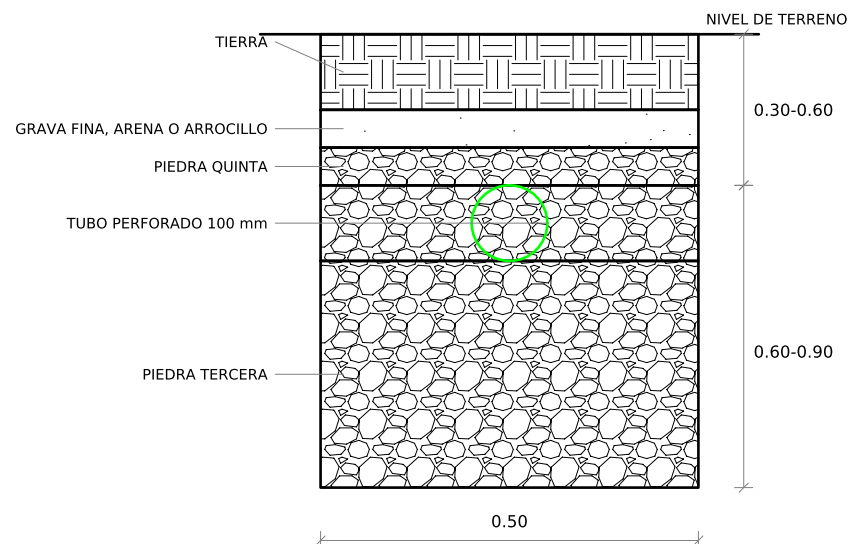

SIMBOLOGÍA

	AGUAS NEGRAS (PVC)
	AGUAS GRISES (PVC)
	BAJANTE DE AGUAS NEGRAS 4"
	BAJANTE DE AGUAS GRISES 2"
	SIFÓN DE PISO (DUCHA) 2"
	SALIDA DE APARATO (WC / LM / LP)
	CAJA DE REGISTRO (DET. 3)
	DRENAJE EN ZANJA (DET. 2)

AN / AG: AGUAS NEGRAS / GRISES; TG: TRAMPA DE GRASA; FAF: FILTRO ANAEROBIO DE FLUJO ASCENDENTE.

NOTAS:

- 1.- TODAS LAS MEDIDAS ESTÁN DADAS EN METROS; LAS DIMENSIONES DEL TANQUE Y DEL FAF SON INTERIORES, SALVO INDICACIÓN CONTRARIA.
- 2.- VERIFICAR EN SITIO LA UBICACIÓN, LOS NIVELES Y LAS CONDICIONES DEL TERRENO ANTES DE INICIAR LA CONSTRUCCIÓN.
- 3.- NO HAY ALCANTARILLADO SANITARIO: LAS AGUAS RESIDUALES SE TRATAN EN TANQUE SÉPTICO CON FAF Y SE DISPONEN EN EL DRENAJE DEL PATIO POSTERIOR.
- 4.- AGUAS NEGRAS (INODOROS) EN 4" Y AGUAS GRISES (LAVATORIOS, DUCHAS Y FREGADERO) EN 2", CON BAJANTES Y CAJAS DE REGISTRO SEPARADAS.
- 5.- TUBERÍA ENTERRADA EN PVC SDR-26 O SUPERIOR, DIÁMETRO MÍNIMO 100 MM (4"). ACCESORIOS SANITARIOS EN TODOS LOS CAMBIOS DE DIRECCIÓN.
- 6.- LAS AGUAS GRISES PASAN POR LA TRAMPA DE GRASA Y SE UNEN A LAS AGUAS NEGRAS EN LA CAJA DE REGISTRO DE ENTRADA AL TANQUE.
- 7.- BAJANTES: SUITE 1 EN FORRO DEL MURO BAÑO / WALK-IN, CON COLECTORES COLGADOS BAJO LA LOSA DEL N2 HASTA C2; SUITE 2 Y FREGADERO EN DUCTO DE LA COCINA (ESQUINA D/4); SUITE 3 EN DUCTO JUNTO A C6 EN LA SALA. DUCTOS DE 0.30 x 0.40 Y FORRO DE 0.20.
- 8.- CADA BAJANTE SE PROLONGA COMO VENTILACIÓN DE 2" SOBRE LA CUBIERTA.
- 9.- LAS TUBERÍAS PASAN SOBRE LAS PLACAS DE CIMENTACIÓN SIN ATRAVESAR PEDESTALES; CRUCES CON VIGAS RÍOSTRA CON CAMISA. EL TANQUE Y LAS CAJAS SE UBICAN FUERA DE LAS PLACAS (VER C01).
- 10.- TANQUE Y FAF: CONCRETO DE 210 KG/CM2; LOSAS INFERIOR Y SUPERIOR DE 0.10 M MÍNIMO CON MALLA #3 @20 CM; MUROS DE BLOQUE 12x20x40 CON JUNTAS LLENAS Y REPELLO IMPERMEABLE INTERIOR; REFUERZO VERTICAL #3 @40 CM Y HORIZONTAL #3 CADA DOS HILADAS; RECUBRIMIENTO 4 CM; CURADO 7 DÍAS.
- 11.- CÁMARA 1 (DIGESTIÓN) = 2/3 Y CÁMARA 2 (CLARIFICACIÓN) = 1/3 DEL LARGO. TEES SANITARIAS DE PVC 100 MM, 0.30 M SOBRE Y 0.40 M BAJO EL NIVEL DE LÍQUIDOS. BORDE LIBRE 0.30 M Y PROFUNDIDAD ÚTIL 1.20 M.
- 12.- FAF: 1.04 x 0.80 M INTERIOR, PROFUNDIDAD ÚTIL 1.20 M, FALSO FONDO A 0.20 M CON LOSA PERFORADA, MEDIO FILTRANTE DE PIEDRA CUARTA LAVADA (5-7 CM) DE 0.80 M SIN COMPACTAR Y ESPACIO LIBRE SUPERIOR DE 0.20 M.
- 13.- RESPIRADEROS DE PVC 100 MM, 0.30 M SOBRE EL TERRENO, CON SOMBRERETE. CILINDRO DE INSPECCIÓN DE CONCRETO, DIÁMETRO INTERIOR MÍNIMO 0.30 M. TAPAS DE CONCRETO REFORZADO DE 0.60 x 0.60 M MÍNIMO, CON AGARRADERAS.
- 14.- DRENAJE: TUBO PERFORADO DE 100 MM EN ZANJA DE 0.50 M (DETALLE 2). LONGITUD 7.40 M.
- 15.- NO RELLENAR HASTA QUE EL CONCRETO ALCANCE SU RESISTENCIA; COMPACTAR EN CAPAS DE 20 CM MÁXIMO Y EVITAR EL PASO DE VEHÍCULOS SOBRE EL SISTEMA.
- 16.- ANTES DEL RELLENO, VERIFICAR LA ESTANQUEIDAD DEL TANQUE Y DEL FAF; LIMPIAR EL SISTEMA ANTES DE COLOCAR EL MEDIO FILTRANTE Y LLENAR EL FAF CON AGUA ANTES DE INICIAR LA OPERACIÓN.
- 17.- MANTENIMIENTO: RETIRAR LOS LODOS DEL TANQUE CUANDO OCUPEN APROXIMADAMENTE 1/3 DEL VOLUMEN DE LA PRIMERA CÁMARA.
- 18.- NO SE PERMITE MODIFICAR DIMENSIONES, NIVELES, DIÁMETROS NI MATERIALES SIN AUTORIZACIÓN DEL PROFESIONAL RESPONSABLE.

ESPACIO PARA SELLOS Y TIMBRES

CivilCon Diseño y Construcción SRLTDA
Céd. Jurídica: 3-102-762712

PROFESIONAL RESPONSABLE:

DIRECTOR TÉCNICO:
Steven Viales (Civil) IC-40759
David Barrantes (Electricidad) IE-27499

PROYECTO:

VIVIENDA UNIFAMILIAR
DISTRITO 03 SANTIAGO, CANTÓN 05 SAN RAFAEL,
PROVINCIA 04 HEREDIA, COSTA RICA.

INFORMACIÓN REGISTRO PÚBLICO:

FOLIO REAL: 4-041200-000
PLANO CATASTRADO: 4-57389-2023
ÁREA SEGÚN CATASTRO: 256 m²

CONTENIDO:

AGUAS RESIDUALES
PLANTAS NIVELES 1, 2 Y 3.
TANQUE SÉPTICO, FAF Y DRENAJE.
CAJA DE REGISTRO,
TRAMPA DE GRASA Y BAÑO TÍPICO.
SIMBOLOGÍA Y NOTAS.

ESCALAS: 1:100 / INDICADAS


CONTROL DE REVISIONES

REV.	FECHA	DESCRIPCIÓN
0	06-10-2026	VERSIÓN DE TRABAJO PARA REVISIÓN
1	07-10-2026	DETALLE DE TANQUE SEGÚN LA REFERENCIA
2	07-10-2026	LISTA DEFINITIVA (22); PARA TRÁMITE


ESTADO:

PARA TRÁMITE
CFIA Y MUNICIPALIDAD

LUGAR	LÁMINA
COSTA RICA	S02
OCT 2026	TOTAL 22

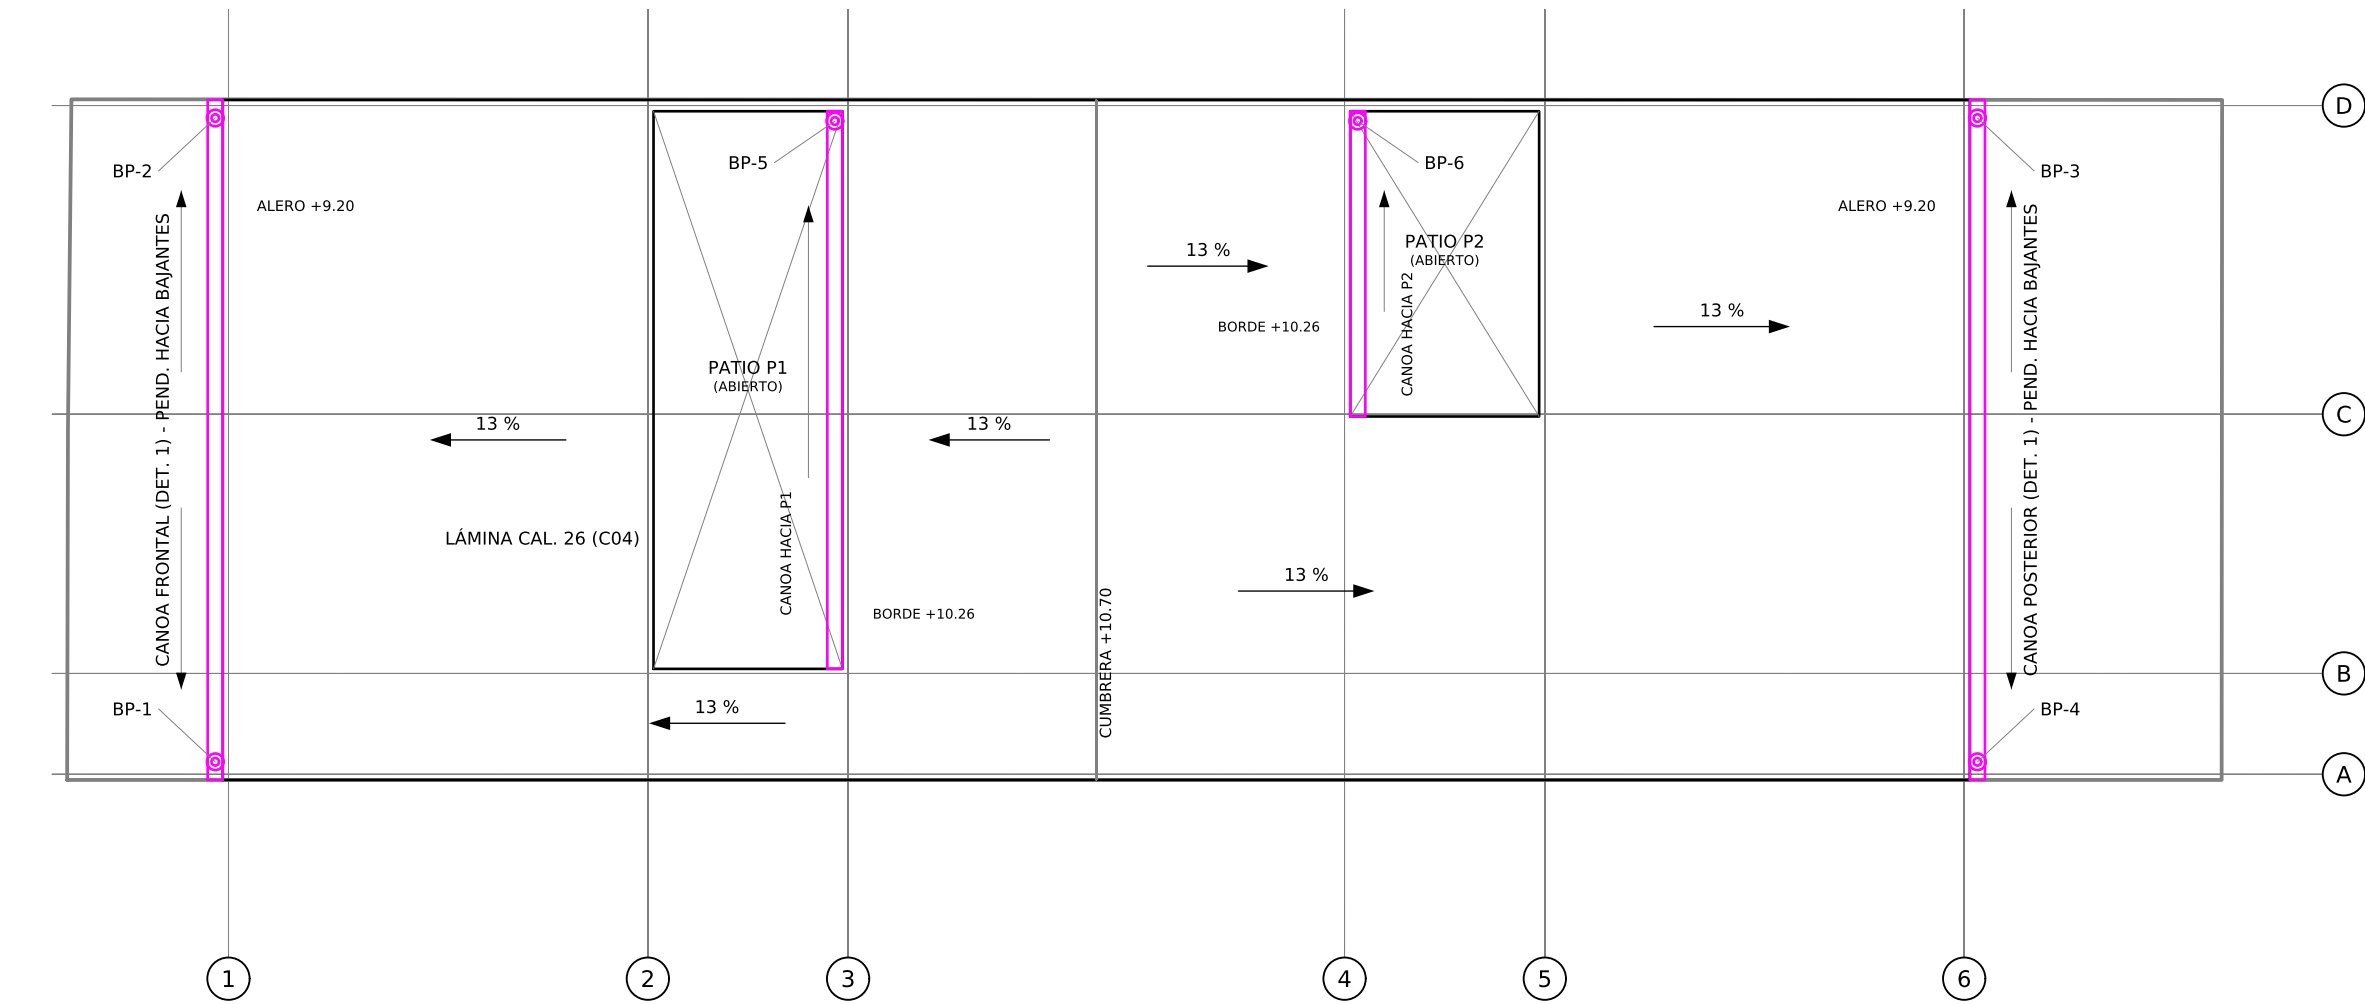


AGUAS PLUVIALES - PLANTA DE TECHO
Esc. 1:100

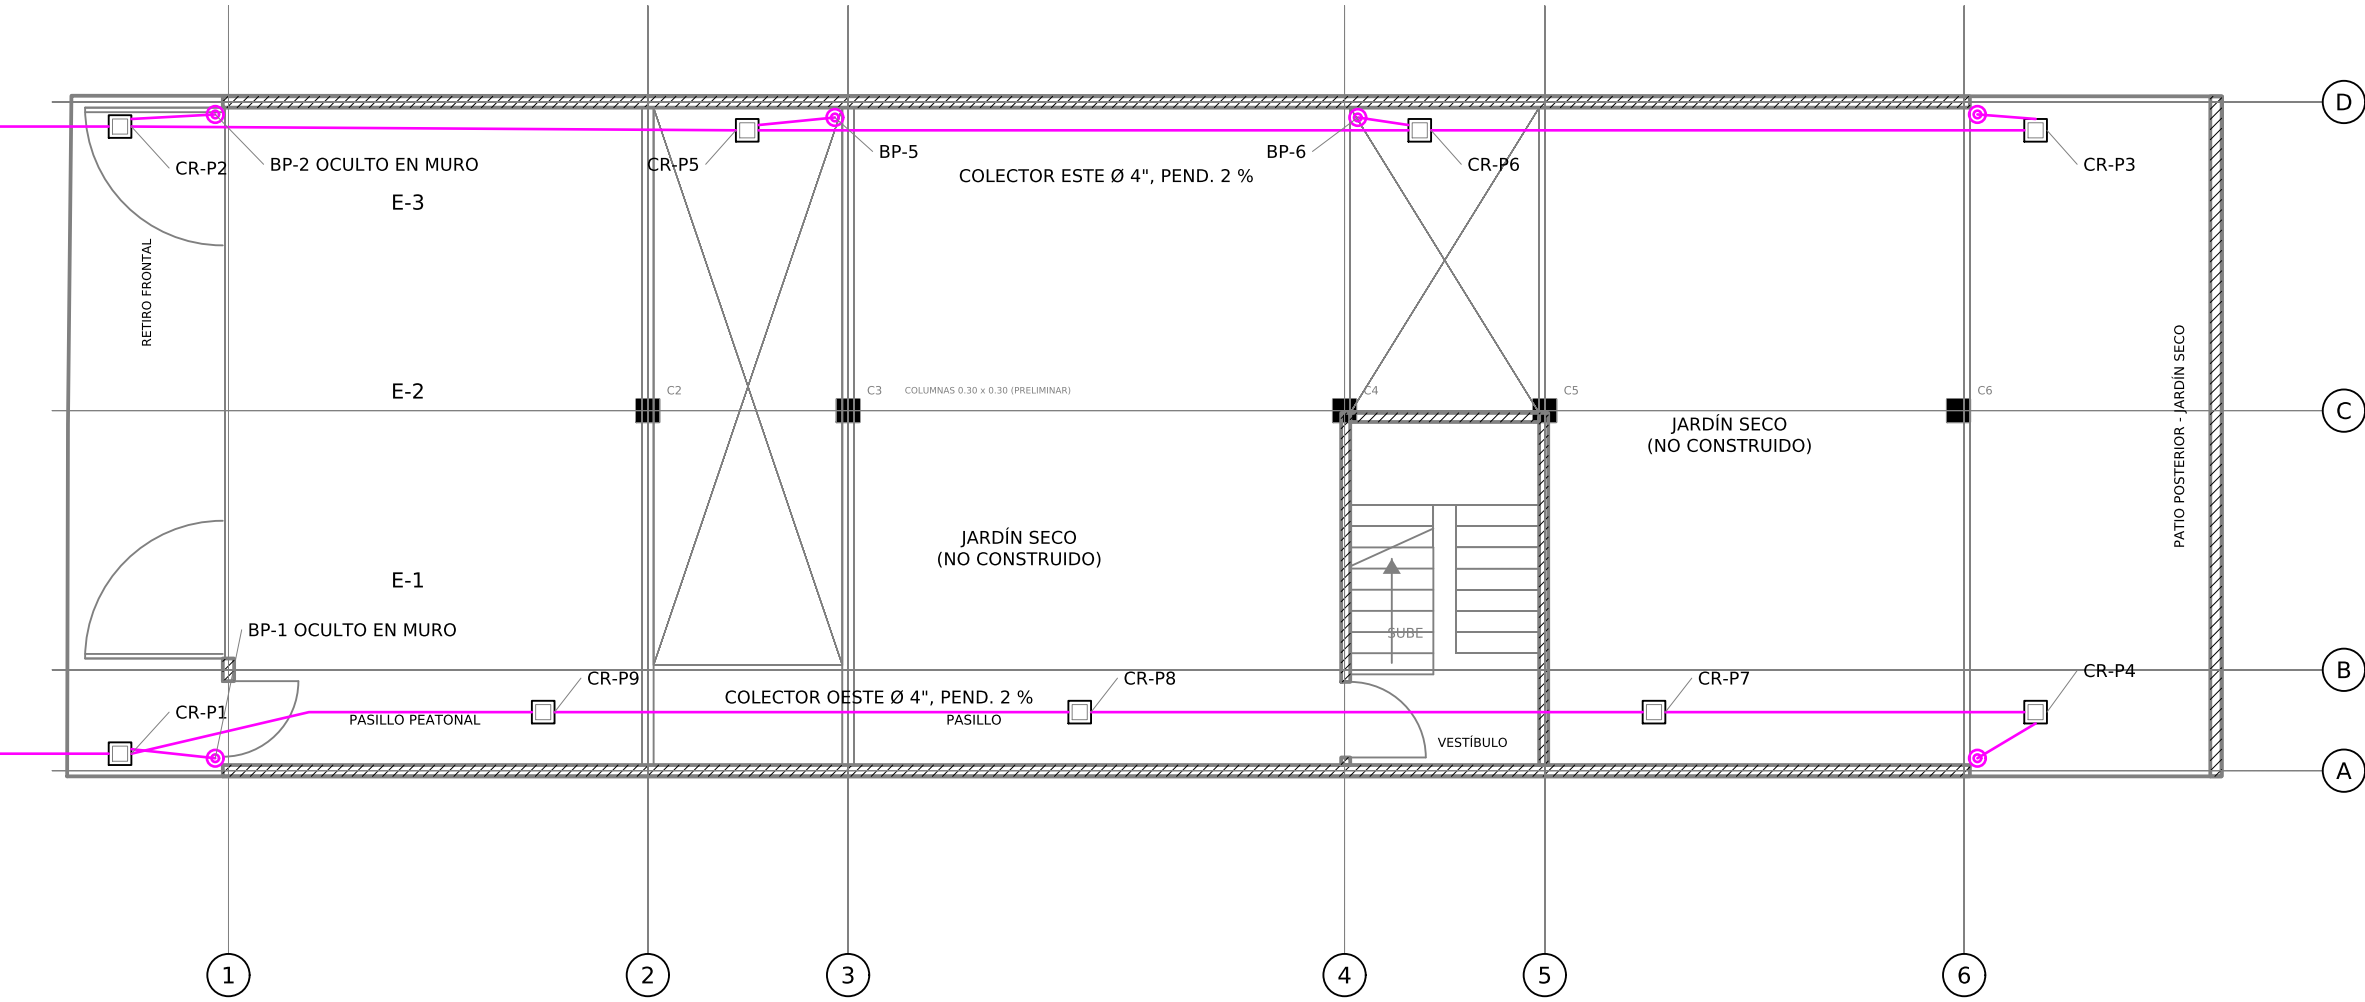

AGUAS PLUVIALES - NIVEL 1
Esc. 1:100

DETALLE 1 - CANOA (SECCIÓN TÍPICA)
Esc. 1:10 - FRONTAL, POSTERIOR Y HACIA PATIOS

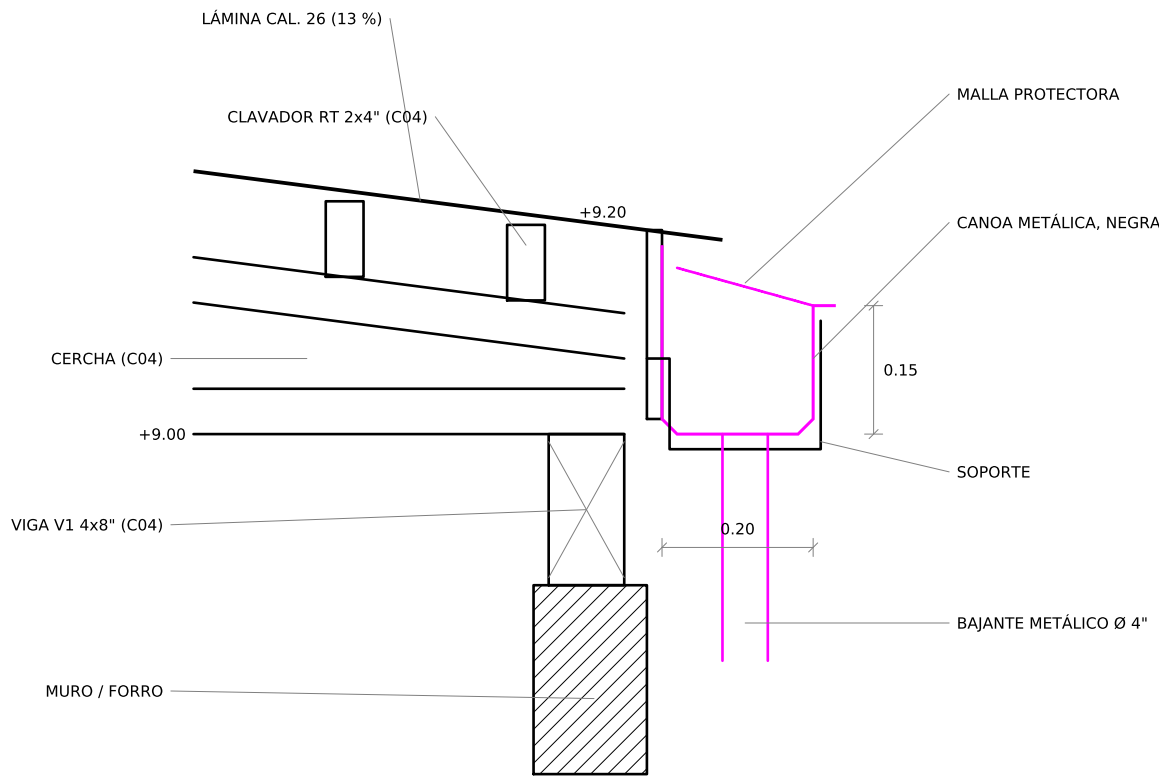

ÁREAS TRIBUTARIAS DE CUBIERTA (PROYECCIÓN HORIZONTAL)


CANOA	ÁREA (m²)	BAJANTES	m² POR BAJANTE
FRONTAL	60.79	BP-1, BP-2	30.40
HACIA P1	24.80	BP-5	24.80
HACIA P2	13.57	BP-6	13.57
POSTERIOR	80.37	BP-3, BP-4	40.18
TOTAL CUBIERTA	179.53	6	

ÁREAS CALCULADAS CON LA GEOMETRÍA DE LA C04 (CUMBRERA EN y = 13.62). LOS PATIOS P1 (18.45 m²) Y P2 (10.10 m²) SON ABIERTOS: LA LLUVIA DIRECTA CAE SOBRE LA GRAVA DEL NIVEL 1.


NOTAS:

- 1.- TODAS LAS MEDIDAS ESTÁN DADAS EN METROS, SALVO INDICACIÓN CONTRARIA.
- 2.- LAS AGUAS PLUVIALES SE DIRIGEN HACIA LA CUNETA PÚBLICA DEL FRENTE. NO SE CONECTAN AL TANQUE SÉPTICO NI AL DRENAJE (S02).
- 3.- CUBIERTA SEGÚN LA C04: LÁMINA CAL. 26 A DOS AGUAS, PENDIENTE 13 %, ALERO +9.20 Y CUMBRERA +10.70.
- 4.- CANOAS FRONTAL Y POSTERIOR CON DOS BAJANTES CADA UNA, UNO EN CADA EXTREMO; CANOAS HACIA LOS PATIOS P1 Y P2 CON UN BAJANTE CADA UNA, EN EL EXTREMO ESTE.
- 5.- CANOAS Y BAJANTES VISIBLES METÁLICOS, ACABADO NEGRO (A5). BAJANTES FRONTALES BP-1 Y BP-2 OCULTOS EN EL MURO FRONTAL DEL NIVEL 1.
- 6.- LAS CANOAS TENDRÁN MALLA PROTECTORA PARA EVITAR EL ACCESO DE BASURA.
- 7.- DIRIGIR LAS PENDIENTES HACIA BAJANTES O CANOAS; EVITAR DEPRESIONES QUE PROVOQUEN EMPOZAMIENTOS.
- 8.- BAJANTES Y COLECTORES PLUVIALES DE 4": COLECTORES ENTERRADOS CON PENDIENTE DEL 2 %, CANOAS CON PENDIENTE HACIA LOS BAJANTES.
- 9.- COLECTORES ENTERRADOS DE PVC CON CAJAS PLUVIALES DE 0.30 x 0.30 (DETALLE 2) AL PIE DE CADA BAJANTE Y EN LOS CAMBIOS DE DIRECCIÓN.
- 10.- COLECTOR OESTE POR EL PASILLO PEATONAL, ENTRE LOS ALIMENTADORES ELÉCTRICOS (E01) Y LA TUBERÍA DE AGUA POTABLE (S01); CRUZA BAJO LOS DUCTOS ELÉCTRICOS FRENTE A CR-P9.
- 11.- COLECTOR ESTE JUNTO AL MURO D; CRUZA LOS RAMALES SANITARIOS DE LA SUITE 2 (S02) ENTRE CR-P6 Y CR-P5.
- 12.- LAS TUBERÍAS PASAN SOBRE LAS PLACAS DE CIMENTACIÓN SIN ATRAVESAR PEDESTALES; CRUCES CON VIGAS RIOSTRON CON CAMISA. LAS CAJAS SE UBICAN FUERA DE LAS PLACAS (C01).
- 13.- DESCARGA A LA CUNETA SEGÚN EL DETALLE 3.
- 14.- LIMPIAR CANOAS, MALLAS Y CAJAS PLUVIALES PERIÓDICAMENTE.

DETALLE 2 - CAJA PLUVIAL
S/E - INTERIOR 0.30 x 0.30

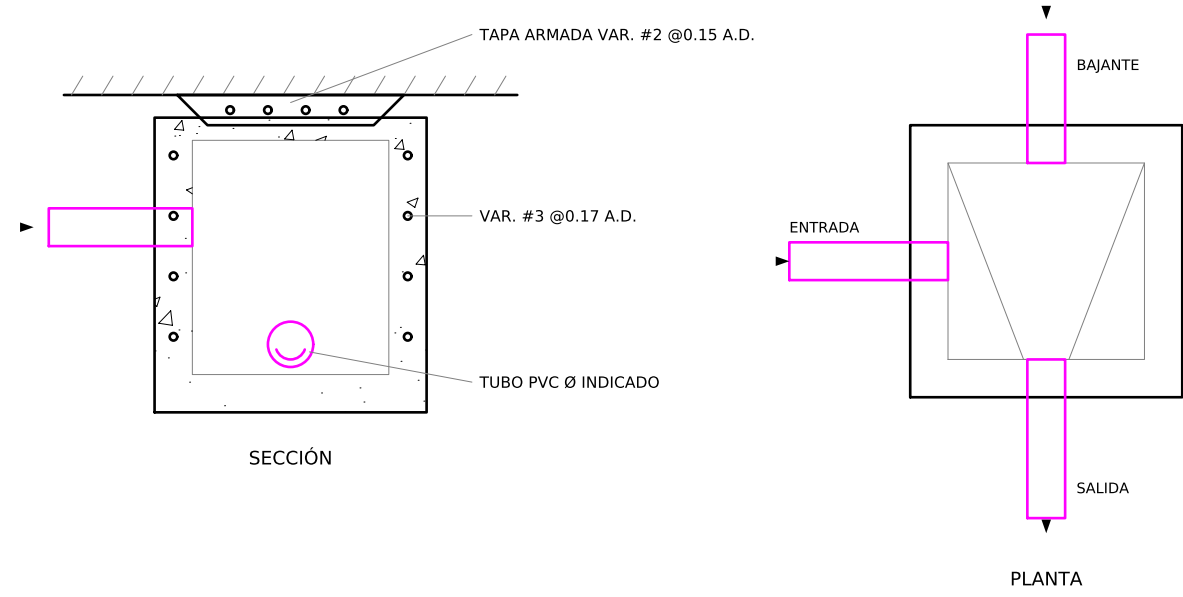

DETALLE 3 - DESCARGA A CUNETA (ESQUEMÁTICO)
S/E

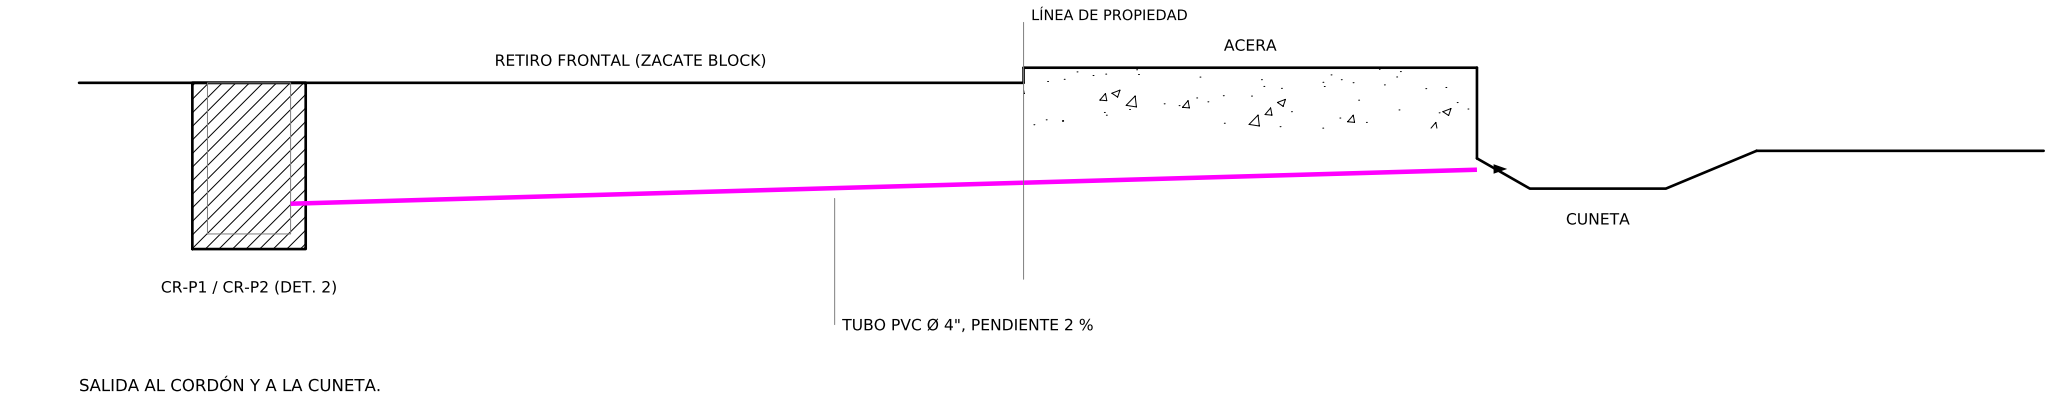

SIMBOLOGÍA

	CANOA METÁLICA (DET. 1)
	BAJANTE PLUVIAL (BP-n)
	COLECTOR PLUVIAL ENTERRADO (PVC)
	CAJA PLUVIAL 0.30 x 0.30 (DET. 2)
	PENDIENTE DE CUBIERTA / CANOA

ESPACIO PARA SELLOS Y TIMBRES

CivilCon Diseño y Construcción SRLTDA
Céd. Jurídica: 3-102-762712

PROFESIONAL RESPONSABLE:
DIRECTOR TÉCNICO:
Steven Viales (Civil) IC-40759
David Barrantes (Electricidad) IE-27499

PROYECTO:
VIVIENDA UNIFAMILIAR
DISTRITO 03 SANTIAGO, CANTÓN 05 SAN RAFAEL,
PROVINCIA 04 HEREDIA, COSTA RICA.

INFORMACIÓN REGISTRO PÚBLICO:
FOLIO REAL: 4-041200-000
PLANO CATASTRADO: 4-57389-2023
ÁREA SEGÚN CATASTRO: 256 m²

CONTENIDO:
AGUAS PLUVIALES
PLANTA DE TECHO.
PLANTA DEL NIVEL 1.
DETALLE DE CANOA.
CAJA PLUVIAL Y DESCARGA
A CUNETA. ÁREAS TRIBUTARIAS.
SIMBOLOGÍA Y NOTAS.

ESCALAS: 1:100 / INDICADAS

CONTROL DE REVISIONES

REV.	FECHA	DESCRIPCIÓN
0	07-10-2026	VERSIÓN DE TRABAJO PARA REVISIÓN
1	07-10-2026	LISTA DEFINITIVA (22); PARA TRÁMITE

ESTADO:

PARA TRÁMITE
CFIA Y MUNICIPALIDAD

LUGAR	LÁMINA
COSTA RICA	S03
OCT 2026	TOTAL 22