



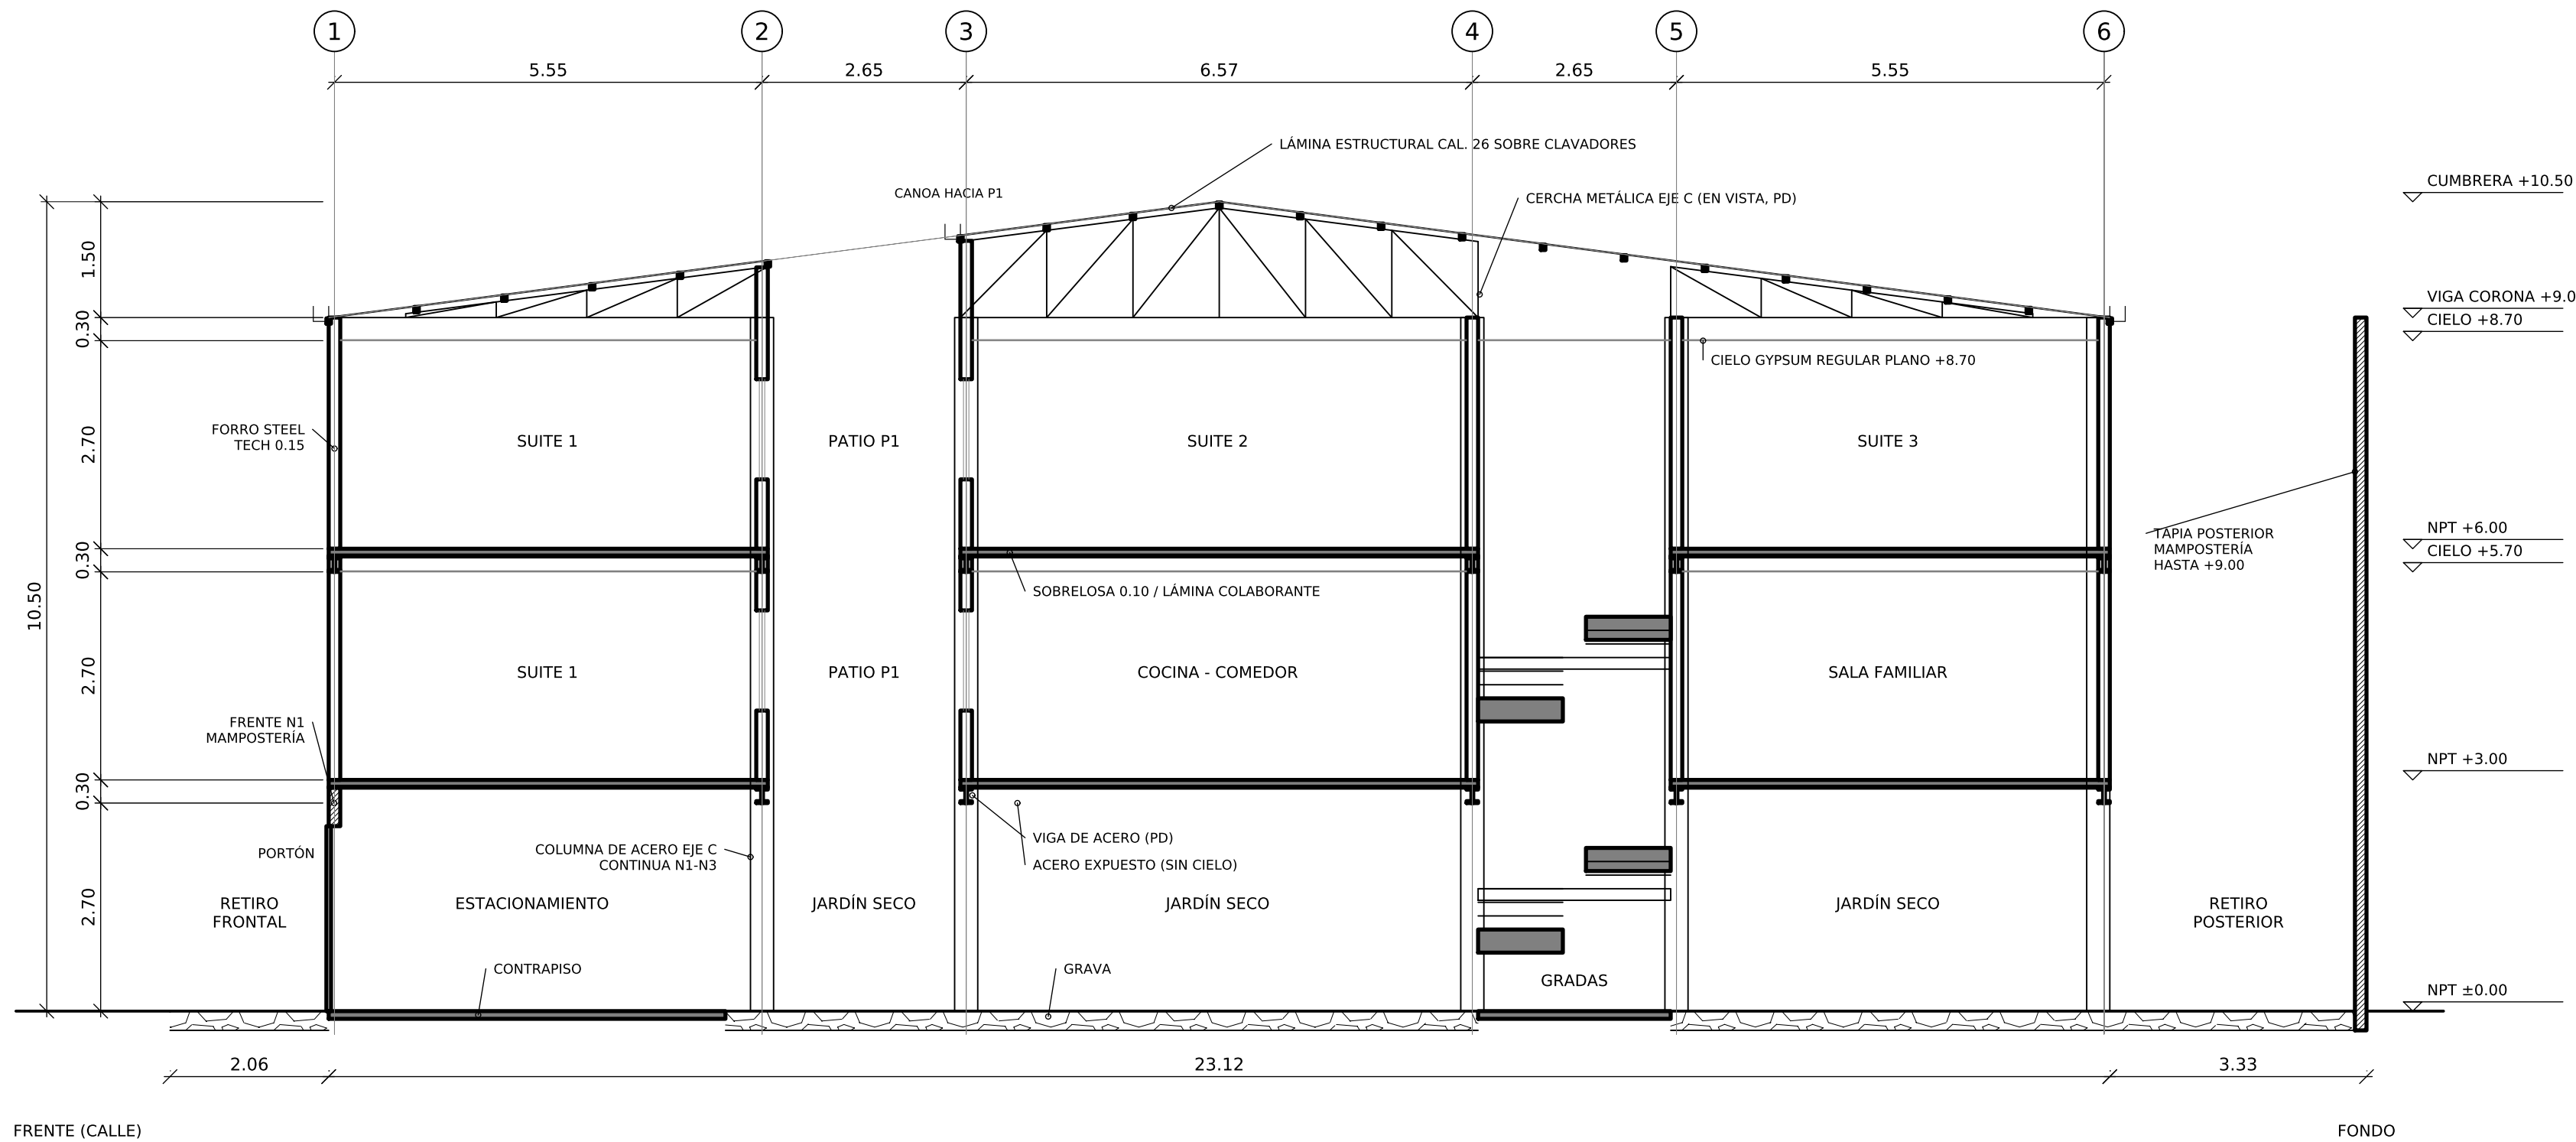

CORTE A-A

CORTE LONGITUDINAL EN x = 3.00 (VISTA HACIA EL ESTE)
Esc. 1:75

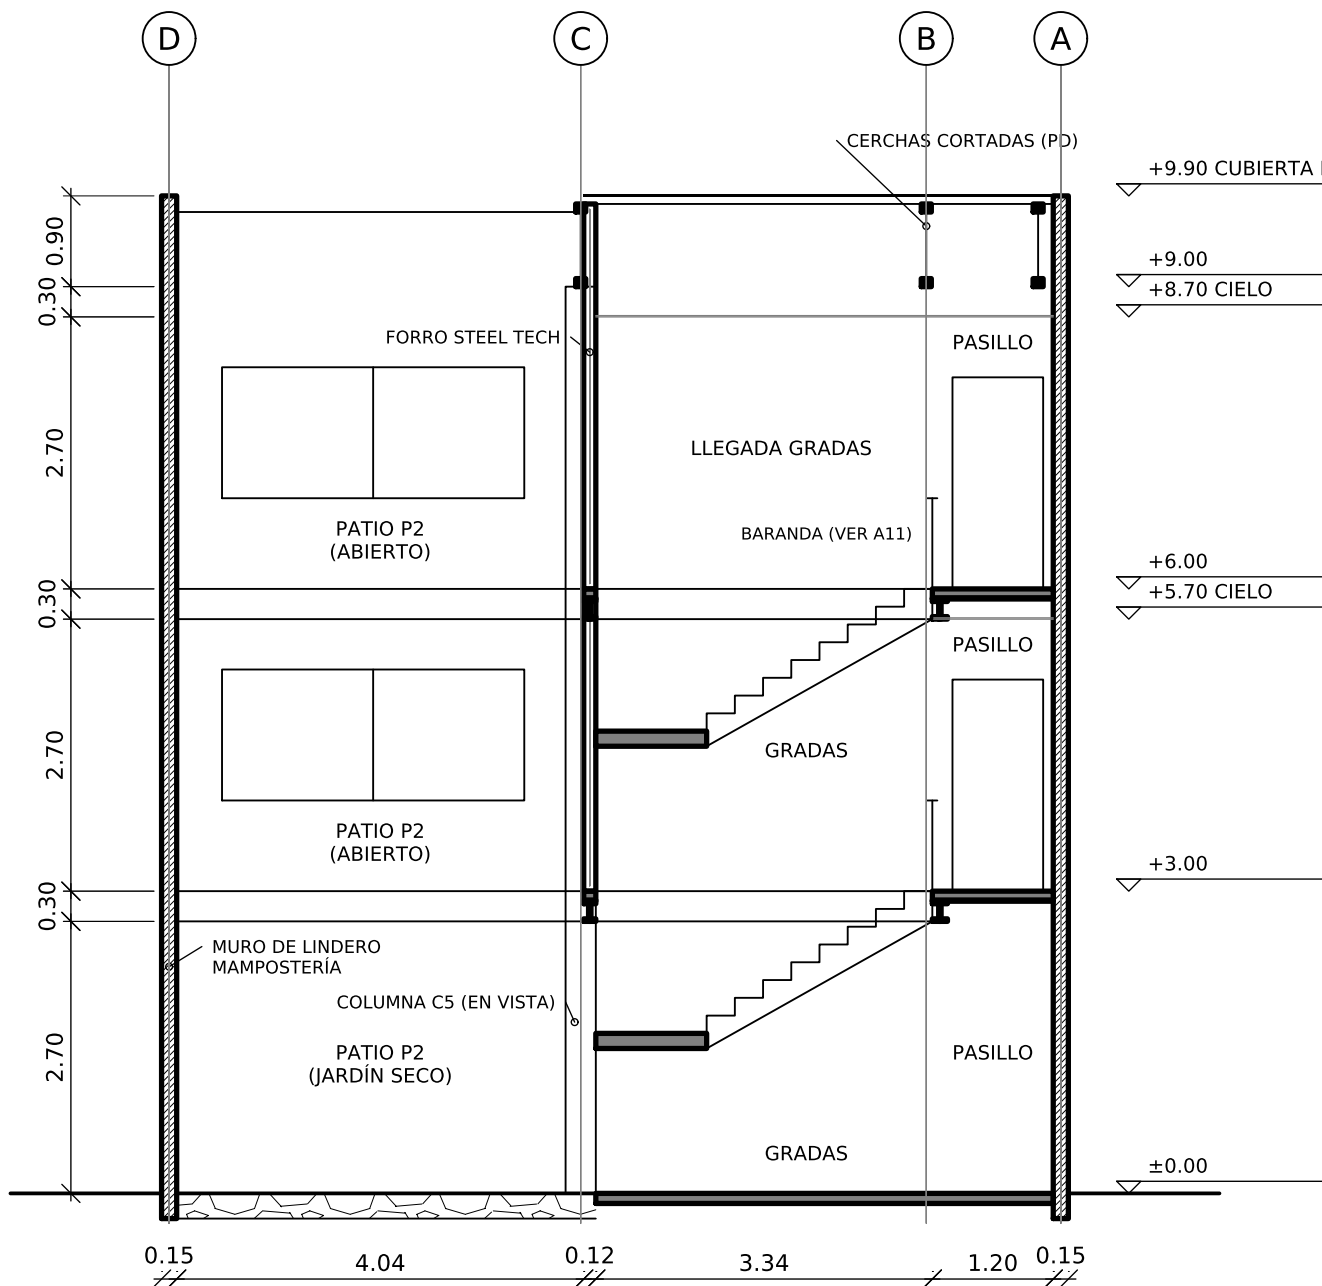

CORTE B-B

CORTE TRANSVERSAL EN y = 18.25 (VISTA HACIA EL FONDO)
Esc. 1:75



NOTAS:

- TODAS LAS MEDIDAS ESTÁN DADAS EN METROS, SALVO INDICACIÓN CONTRARIA. [PR]
- LA TAPIA COLINDANTE DE MAMPOSTERÍA DEBERÁ PROLONGARSE HASTA EL NIVEL DE LA VIGA CORONA DEL ÚLTIMO NIVEL, GARANTIZANDO EL APANTALLAMIENTO VISUAL PERMANENTE HACIA LA PROPIEDAD COLINDANTE.
- LOS BAÑOS CONTARÁN CON EXTRACTOR MECÁNICO DE AIRE.
- NIVELES: NPT N1 ±0.00 (ACERA), N2 +3.00, N3 +6.00; ALTURA DE PISO A PISO 3.00 m.
- ESTRUCTURA PRINCIPAL: MARCOS RÍGIDOS DE ACERO. COLUMNAS DEL EJE C CONTINUAS Y A PLOMO DEL NIVEL 1 AL NIVEL 3. COLUMNAS DE LOS EJES A Y D, PERFILES, SECCIONES Y CONEXIONES SEGÚN PLANOS ESTRUCTURALES.
- ENTREPISOS: SOBRELOSA DE 0.10 m SOBRE LÁMINA COLABORANTE Y VIGAS DE ACERO (PERALTE 0.20 m PRELIMINAR, PD).
- CIELOS: GYPSUM REGULAR PLANO SUSPENDIDO A 2.70 m SOBRE NPT EN LOS NIVELES 2 Y 3. NIVEL 1 (ESTACIONAMIENTOS) CON ESTRUCTURA DE ACERO EXPUESTA.
- CERRAMIENTOS: FORRO DEL EDIFICIO EN PAREDES LIVIANAS STEEL TECH (0.15 m). MUROS DE LINDERO, TAPIA POSTERIOR Y FRENTE DEL NIVEL 1 (PORTÓN) EN MAMPOSTERÍA. PAREDES INTERIORES 0.12 m.
- CUBIERTA: LÁMINA ESTRUCTURAL CAL. 26 SOBRE CLAVADORES Y CERCHAS METÁLICAS EN LA DIRECCIÓN DE LA PENDIENTE (13 %). CORDÓN INFERIOR A +9.00 Y CUMBREIRA +10.50. GEOMETRÍA Y PERFILES DE CERCHAS Y CLAVADORES SEGÚN PLANOS ESTRUCTURALES (PD). CANOAS EN FRENTE, FONDO Y BORDES HACIA LOS PATIOS DONDE SE REQUIERA.
- NIVEL 1: CONTRAPISO EN ESTACIONAMIENTOS, PASILLO Y GRADAS (ESPESOR SEGÚN ESTRUCTURAL); EL RESTO EN GRAVA (JARDÍN SECO).
- ESCALERA EN U: 17 CONTRAHUELLAS DE 0.176 m Y HUELLA DE 0.28 m POR NIVEL; DESCANSOS A +1.59 Y +4.59. BARANDAS Y PASAMANOS EN LÁMINA A11.
- ALTURAS PRELIMINARES (PD): PUERTAS 2.10 m; VENTANAS HACIA LOS PATIOS CON ANTEPECHO 0.90 m Y DINTEL 2.20 m. TIPOS EN LÁMINAS A7 A A9.
- CIMENTACIÓN SEGÚN PLANOS ESTRUCTURALES (NO SE DIBUJA EN ESTA LÁMINA).
- TRAZO DE LOS CORTEES SEGÚN LÁMINAS A2 A A4.
- [PR] = NOTA TOMADA DEL PROYECTO DE REFERENCIA, PENDIENTE DE REVISIÓN.

SIMBOLOGÍA:

- | | | | |
|--|--|--|--|
| | ACERO CORTADO (COLUMNAS, VIGAS, CERCHAS, CLAVADORES) | | CONCRETO CORTADO (SOBRELOSA, CONTRAPISO, GRADAS) |
| | MAMPOSTERÍA (MUROS DE LINDERO, TAPIA, FRENTE N1) | | FORRO STEEL TECH |
| | PARED INTERIOR | | GRAVA (JARDÍN SECO) |
| | CIELO GYPSUM REGULAR PLANO | | |

ESPACIO PARA SELLOS Y TIMBRES

CivilCon Diseño y Construcción SRLTDA
Céd. Jurídica: 3-102-762712

PROFESIONAL RESPONSABLE:
DIRECTOR TÉCNICO:
Steven Viales (Civil) IC-40759
David Barrantes (Electricidad) IE-27499

PROYECTO:
VIVIENDA UNIFAMILIAR
DISTRITO 03 SANTIAGO, CANTÓN 05 SAN RAFAEL,
PROVINCIA 04 HEREDIA, COSTA RICA.

INFORMACIÓN REGISTRO PÚBLICO:
FOLIO REAL: 4-041200-000
PLANO CATASTRADO: 4-57389-2023
ÁREA SEGÚN CATASTRO: 256 m²

CONTENIDO:
CORTES
CORTE A-A.
CORTE B-B.
NOTAS.
SIMBOLOGÍA.

ESCALAS: 1:75

CONTROL DE REVISIONES		
REV.	FECHA	DESCRIPCIÓN
0	06-10-2026	VERSIÓN DE TRABAJO PARA REVISIÓN
1	06-10-2026	SISTEMA CONSTRUCTIVO, CERCHAS, MATERIALES

ESTADO:
VERSIÓN DE TRABAJO
NO APTA PARA CONSTRUCCIÓN NI TRÁMITE

LUGAR	LÁMINA
COSTA RICA	A6
OCT 2026	TOTAL --