


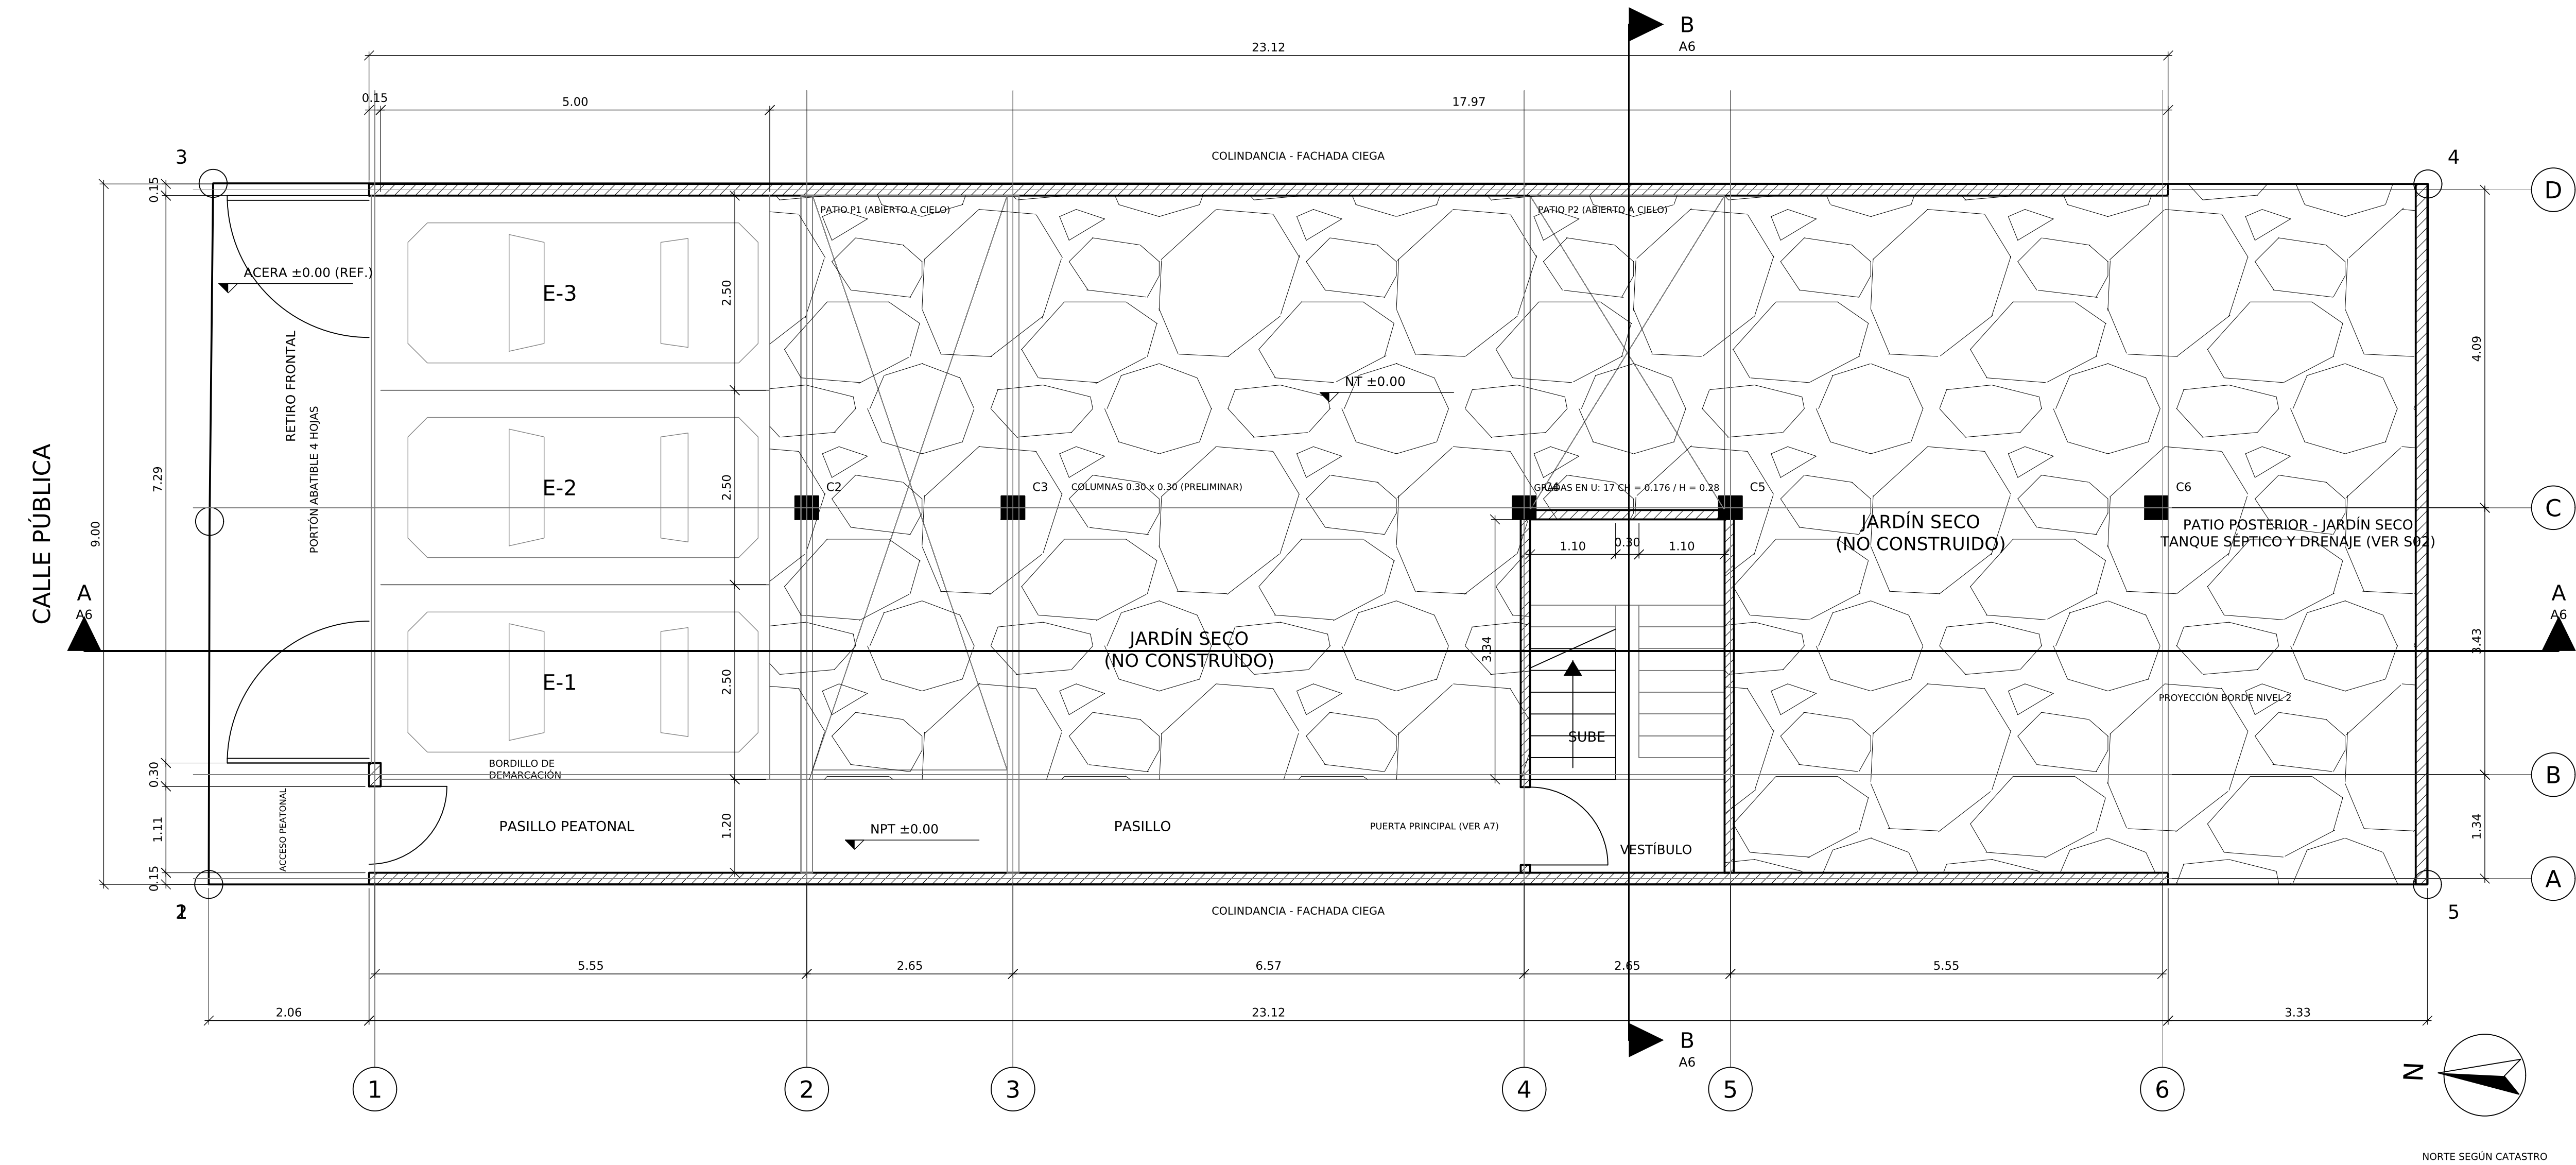

PLANTA NIVEL 1

PARQUEOS, ACCESO, GRADAS Y JARDÍN SECO
Esc. 1:50



DERROTERO

LÍNEA	ACIMUT		DISTANCIA	
	°	'	m	cm
1 - 2	87	25	4	66
2 - 3	87	53	4	34
3 - 4	177	18	28	46
4 - 5	267	20	9	00
5 - 1	357	17	28	51
AMARRE	ACIMUT		DISTANCIA	
	°	'	m	cm
3 - P.I.	101	22	75	71

VER CUADRO DE COORDENADAS CRTM05 EN LÁMINA A1.

CUADRO DE ÁREAS NIVEL 1

ESPACIO	ÁREA
ESTACIONAMIENTOS E-1 A E-3 (7,50 x 5,00)	37,50 m²
PASILLO PEATONAL (1,20 x 17,27)	20,72 m²
GRADAS (3,34 x 2,50)	8,35 m²
ÁREA CONSTRUIDA NIVEL 1	66,57 m²

EL RESTO DEL NIVEL 1 ES JARDÍN SECO NO CONSTRUIDO. ÁREAS DE LOS NIVELES 2 Y 3 EN LÁMINAS A3 Y A4.

PORCENTAJE DE COBERTURA

CONCEPTO	VALOR
ÁREA DE LOTE (SEGÚN CATASTRO)	256,00 m²
HUELLA CONSTRUCTIVA (PROYECCIÓN NIVELES 2 Y 3)	179,53 m²
% COBERTURA	70,13 %

CÁLCULO: (HUELLA / ÁREA DE LOTE) x 100 = (179,53 / 256,00) x 100 = 70,13 %

NOTAS:

- TODAS LAS MEDIDAS ESTÁN DADAS EN METROS, SALVO INDICACIÓN CONTRARIA.
- LA TAPIA COLINDANTE DE MAMPOSTERÍA DEBERÁ PROLONGARSE HASTA EL NIVEL DE LA VIGA CORONA DEL ÚLTIMO NIVEL, GARANTIZANDO EL APANTALLAMIENTO VISUAL PERMANENTE HACIA LA PROPIEDAD COLINDANTE.
- LOS DATOS DEL LOTE (VÉRTICES, DERROTERO Y ÁREA) SE TOMARON DEL PLANO CATASTRADO 4-57389-2023, SISTEMA CRTM05. NO SUSTITUYEN UN LEVANTAMIENTO TOPOGRÁFICO.
- RETIROS DE DISEÑO: FRONTAL 2.00 m MEDIDO DESDE EL VÉRTICE 3; POSTERIOR MÍNIMO 3.00 m; LATERALES 0.00 m. CONFIRMADOS CON EL ALINEAMIENTO Y EL USO DE SUELO MUNICIPAL.
- LAS FACHADAS LATERALES SE UBICAN SOBRE COLINDANCIA Y SERÁN CIEGAS (SIN VENTANAS NI VANOS).
- LOS BAÑOS CONTARÁN CON EXTRACTOR MECÁNICO DE AIRE.
- LAS CANOAS TENDRÁN MALLA PROTECTORA PARA EVITAR EL ACCESO DE BASURA.
- EL AGUA POTABLE PROVIENE DEL SISTEMA PÚBLICO (ESPH), DIRECTAMENTE DE LA CONEXIÓN DE LA CALLE (VER S01).
- LAS AGUAS PLUVIALES SE DIRIGEN HACIA LA CUNETA PÚBLICA (VER S03).
- LAS AGUAS RESIDUALES SE TRATARÁN MEDIANTE TANQUE SÉPTICO Y DRENAJE EN EL PATIO POSTERIOR (VER S02).
- LA COBERTURA SE CALCULA SOBRE EL ÁREA SEGÚN CATASTRO (256 m²). LOS PATIOS P1 Y P2 SON ABIERTOS DESDE EL NIVEL 1 HASTA EL CIELO Y NO SE CONTABILIZAN EN LA HUELLA.
- PATIOS DE LUZ P1 Y P2 DE 2.50 m DE LADO MÍNIMO, DIMENSIÓN ACEPTADA POR LA MUNICIPALIDAD (ALTURA MEDIDA DESDE EL NIVEL 1).
- NIVEL 1: 3 ESTACIONAMIENTOS INDEPENDIENTES DE 2.50 x 5.00 m (E-1 A E-3), CON ACCESO RECTO DESDE LA CALLE.
- PORTÓN VEHICULAR ABATIBLE DE 4 HOJAS PLEGABLES (2 POR LADO), CLARO LIBRE 7.29 m, CON APERTURA HACIA EL RETIRO FRONTAL SIN INVADIR LA VÍA PÚBLICA. ACCESO PEATONAL DE 1.00 m.
- COLUMNAS SOBRE EL EJE C EN LOS EJES 2 A 6 (SECCIÓN 0.30 x 0.30 PRELIMINAR, CARA OESTE ALINEADA CON LA ESCALERA; C6 AL RAS DE LA FACHADA POSTERIOR). SIN COLUMNA EN C1 PARA NO OBSTRUIR EL ACCESO VEHICULAR. SECCIONES Y REFUERZO EN C01 A C06.
- LAS ÁREAS NO INDICADAS COMO ESTACIONAMIENTO, PASILLO O GRADAS SON JARDÍN SECO NO CONSTRUIDO: BAJO LOS NIVELES 2 Y 3, EN LOS PATIOS P1 Y P2 Y EN EL PATIO POSTERIOR.
- NPT ±0.00 = NIVEL DE ACERA (TERRENO PLANO). PENDIENTES Y DESAGÜES SEGÚN LÁMINAS S01 A S03.
- LOS MUROS DE COLINDANCIA DE LA VIVIENDA SON LA DIVISIÓN CON LOS PREDIOS VECINOS. EN EL NIVEL 1 SON MUROS CONTINUOS HASTA EL NIVEL DE ENTREPISO (+3.00). NO SE CONSTRUYEN TAPIAS LATERALES EN LOS RETIROS.
- VESTIBULO DE ESCALERA CERRADO CON PAREDES STEEL TECH DE 0.12 m EN LOS EJES 4, C Y 5; PUERTA PRINCIPAL P-01 DE MADERA EN EL PASILLO. PUERTAS, VENTANAS Y ACABADOS EN LÁMINA A7.

ESPACIO PARA SELLOS Y TIMBRES

CivilCon Diseño y Construcción SRLTDA
Céd. Jurídica: 3-102-762712

PROFESIONAL RESPONSABLE:
DIRECTOR TÉCNICO:
Steven Viales (Civil) IC-40759
David Barrantes (Electricidad) IE-27499

PROYECTO:
VIVIENDA UNIFAMILIAR
DISTRITO 03 SANTIAGO, CANTÓN 05 SAN RAFAEL,
PROVINCIA 04 HEREDIA, COSTA RICA.

INFORMACIÓN REGISTRO PÚBLICO:
FOLIO REAL: 4-041200-000
PLANO CATASTRADO: 4-57389-2023
ÁREA SEGÚN CATASTRO: 256 m²

CONTENIDO:
PLANTA NIVEL 1
PARQUEOS, ACCESO Y GRADAS.
DERROTERO.
CUADRO DE ÁREAS.
PORCENTAJE DE COBERTURA.
NOTAS.

ESCALAS: 1:50 / INDICADAS

CONTROL DE REVISIONES		
REV.	FECHA	DESCRIPCIÓN
3	06-10-2026	VESTIBULO DE ESCALERA Y PUERTA PRINCIPAL
4	07-10-2026	REFERENCIAS A C01-C06 Y S01-S03
5	07-10-2026	LISTA DEFINITIVA (22); PARA TRÁMITE

ESTADO:
PARA TRÁMITE
CFIA Y MUNICIPALIDAD

LUGAR	LÁMINA
COSTA RICA	A2
OCT 2026	TOTAL 22