



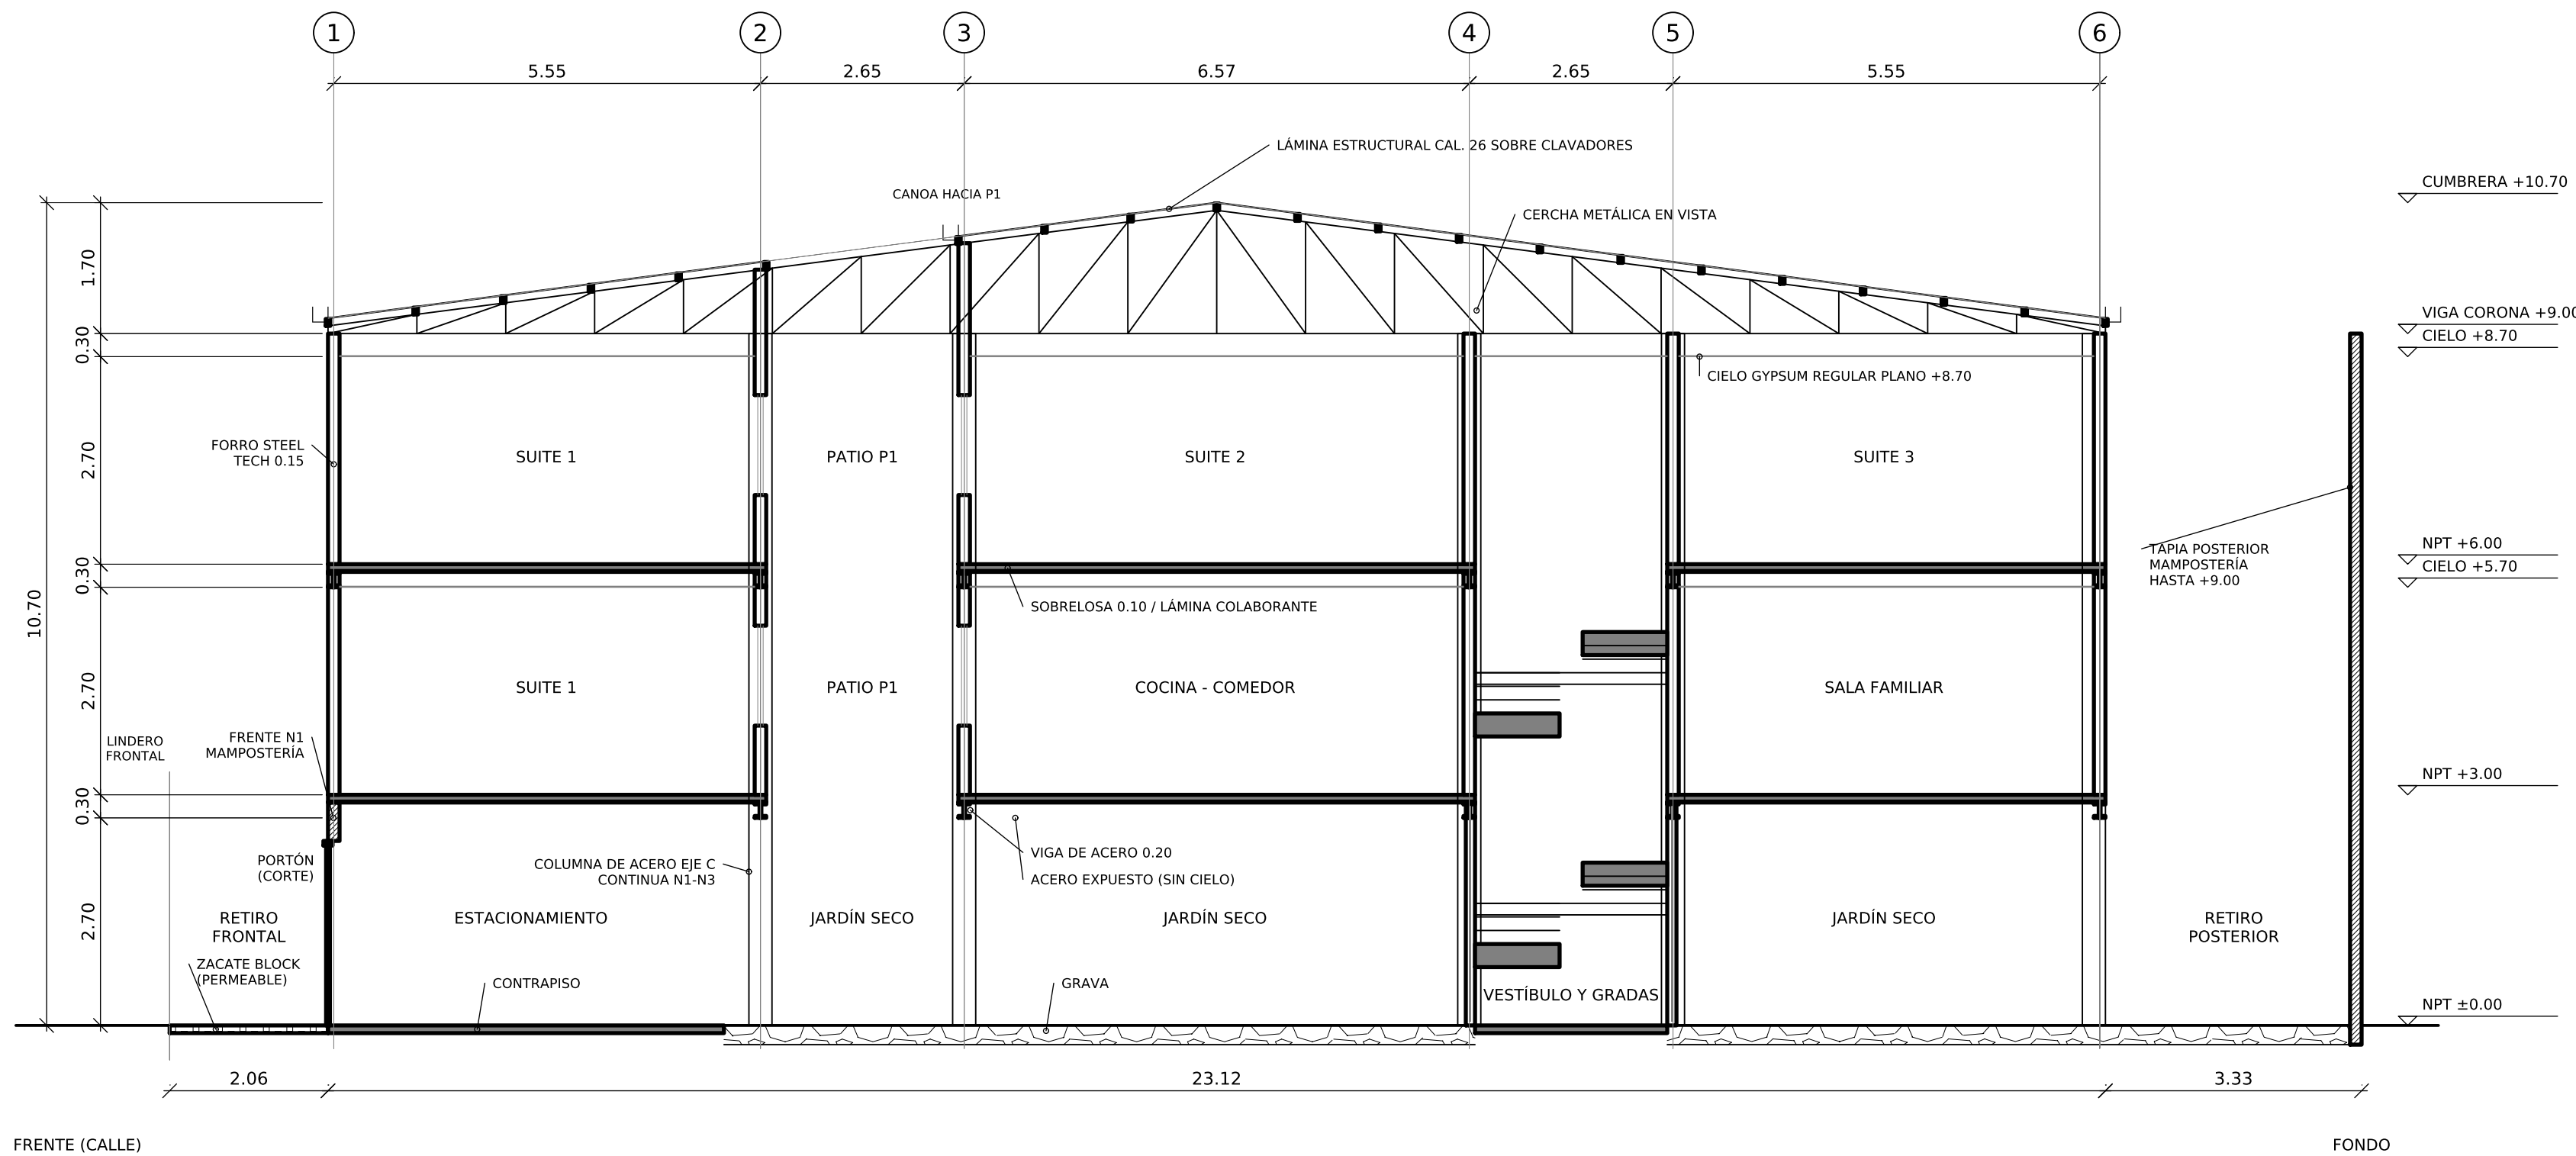

CORTE A-A

CORTE LONGITUDINAL EN x = 3.00 (VISTA HACIA EL ESTE)
Esc. 1:75

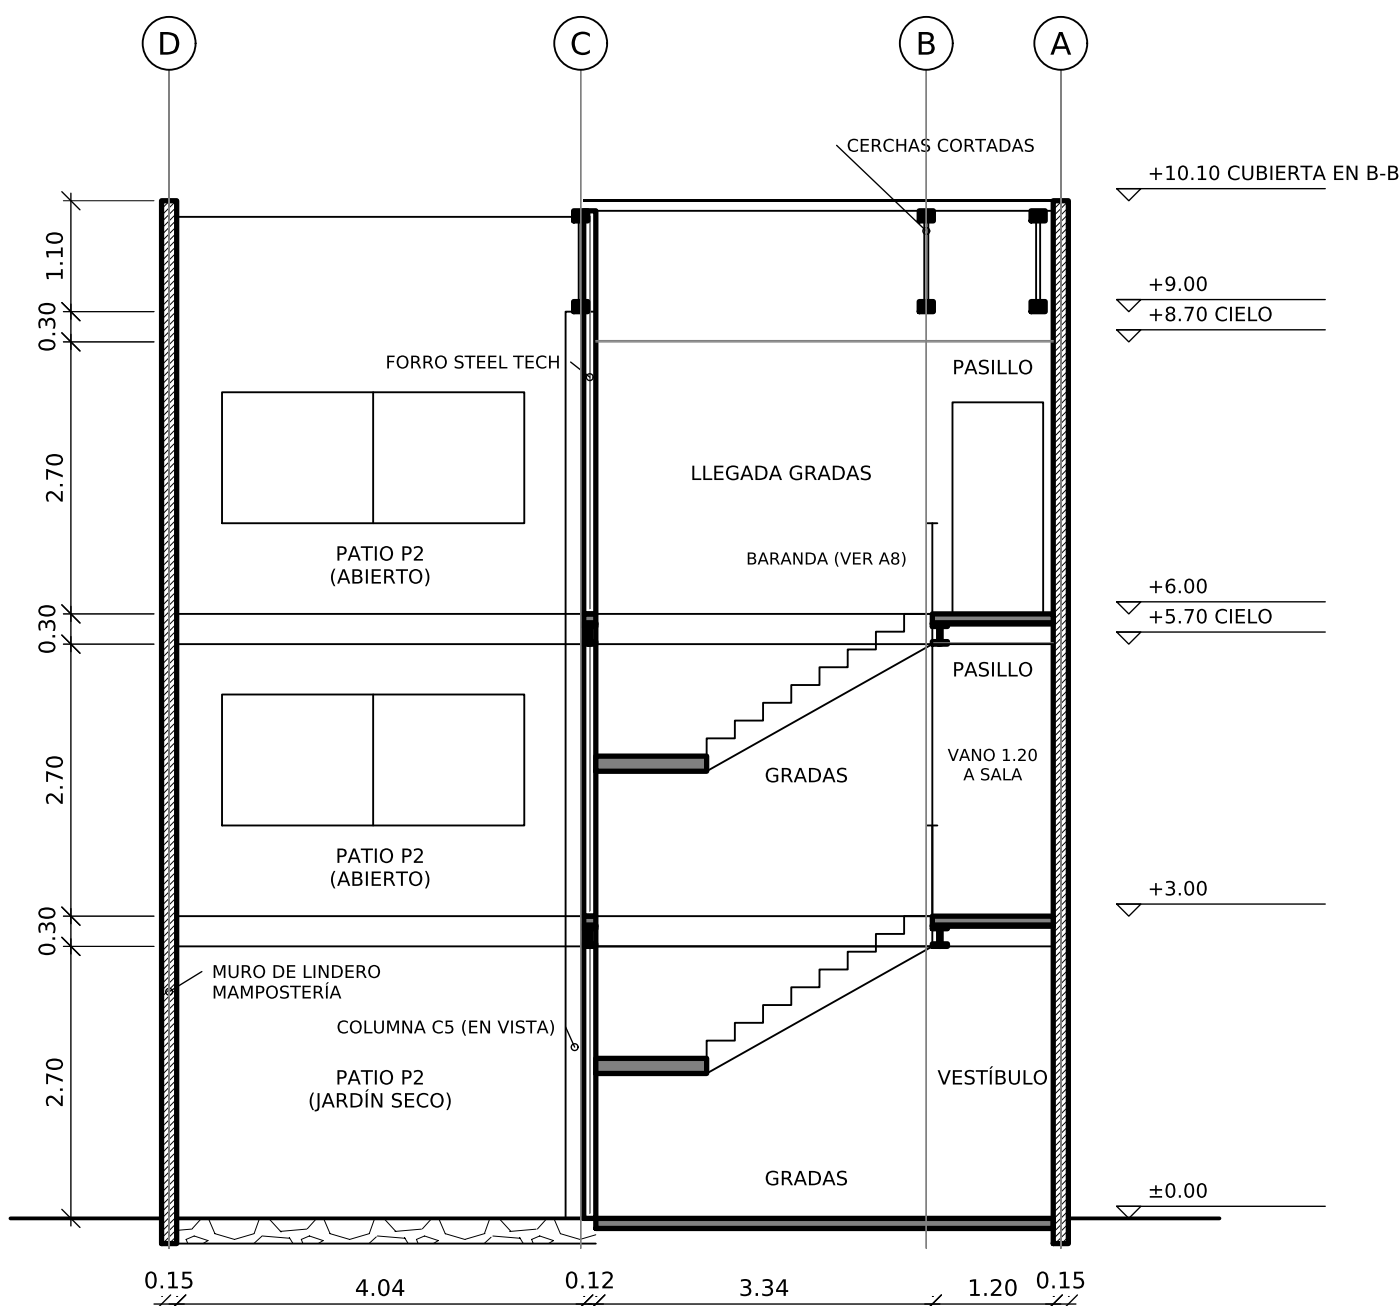

CORTE B-B

CORTE TRANSVERSAL EN y = 18.25 (VISTA HACIA EL FONDO)
Esc. 1:75



NOTAS:

- TODAS LAS MEDIDAS ESTÁN DADAS EN METROS, SALVO INDICACIÓN CONTRARIA.
- LA TAPIA COLINDANTE DE MAMPOSTERÍA DEBERÁ PROLONGARSE HASTA EL NIVEL DE LA VIGA CORONA DEL ÚLTIMO NIVEL, GARANTIZANDO EL APANTALLAMIENTO VISUAL PERMANENTE HACIA LA PROPIEDAD COLINDANTE.
- LOS BAÑOS CONTARÁN CON EXTRACTOR MECÁNICO DE AIRE.
- NIVELES: NPT N1 ±0.00 (ACERA), N2 +3.00, N3 +6.00; ALTURA DE PISO A PISO 3.00 m.
- ESTRUCTURA PRINCIPAL: MARCOS RÍGIDOS DE ACERO. COLUMNAS DEL EJE C CONTINUAS Y A PLOMO DEL NIVEL 1 AL NIVEL 3. COLUMNAS DE LOS EJES A Y D, PERFILES, SECCIONES Y CONEXIONES EN C01 A C06.
- ENTREPISOS: PAQUETE DE 0.30 m = SOBRELOSA DE 0.10 m SOBRE LÁMINA COLABORANTE + VIGAS DE ACERO DE 0.20 m. PERFILES Y REFUERZO EN C03.
- CIELOS: GYPSUM REGULAR PLANO SUSPENDIDO A 2.70 m SOBRE NPT EN LOS NIVELES 2 Y 3. NIVEL 1 (ESTACIONAMIENTOS) CON ESTRUCTURA DE ACERO EXPUESTA.
- CERRAMIENTOS: FORRO DEL EDIFICIO EN PAREDES LIVIANAS STEEL TECH (0.15 m). MUROS DE LINDERO, TAPIA POSTERIOR Y FRENTE DEL NIVEL 1 (PORTÓN) EN MAMPOSTERÍA. PAREDES INTERIORES STEEL TECH DE 0.12 m.
- CUBIERTA: LÁMINA ESTRUCTURAL CAL 26 SOBRE CLAVADORES Y CERCHAS METÁLICAS EN LA DIRECCIÓN DE LA PENDIENTE (13 %), CORDÓN INFERIOR A +9.00 Y CUMBRERA +10.70 (LÁMINA +9.20 EN EL ALERO, VER C04). EN EL CORTE A-A SE DIBUJA LA CERCHA DEL FONDO EN VISTA, COMPLETA. GEOMETRÍA Y PERFILES DE CERCHAS Y CLAVADORES EN C04, CANOAS EN FRENTE, FONDO Y BORDES HACIA LOS PATIOS P1 Y P2 (VER S03).
- NIVEL 1: CONTRAPISO DE 0.10 m EN ESTACIONAMIENTOS, PASILLO Y GRADAS; RETIRO FRONTAL EN ZACATE BLOCK (PERMEABLE); EL RESTO EN GRAVA (JARDÍN SECO).
- ESCALERA EN U: 17 CONTRAHUELLAS DE 0.176 m Y HUELLA DE 0.28 m POR NIVEL; DESCANSOS A +1.59 Y +4.59. BARANDAS Y PASAMANOS EN LÁMINA A8.
- ALTURAS: PUERTAS 2.10 m; VENTANAS HACIA LOS PATIOS CON ANTEPECHO 0.90 m Y DINTEL 2.20 m. TIPOS EN LÁMINA A7.
- CIMENTACIÓN EN C01 Y C02 (NO SE DIBUJA EN ESTA LÁMINA).
- TRAZO DE LOS CORTES SEGÚN LÁMINAS A2 A A4.

SIMBOLOGÍA:

- | | |
|--|---|
| ACERO CORTADO (COLUMNAS, VIGAS, CERCHAS, CLAVADORES) | CONCRETO CORTADO (SOBRELOSA, CONTRAPISO, GRADAS) |
| MAMPOSTERÍA (MUROS DE LINDERO, TAPIA, FRENTE N1) | PAREDES STEEL TECH (FORRO 0.15 / INTERIORES 0.12) |
| ZACATE BLOCK (PERMEABLE) | GRAVA (JARDÍN SECO) |
| CIELO GYPSUM REGULAR PLANO | |

ESPACIO PARA SELLOS Y TIMBRES

CivilCon Diseño y Construcción SRLTDA
Céd. Jurídica: 3-102-762712

PROFESIONAL RESPONSABLE:
DIRECTOR TÉCNICO:
Steven Viales (Civil) IC-40759
David Barrantes (Electricidad) IE-27499

PROYECTO:
VIVIENDA UNIFAMILIAR
DISTRITO 03 SANTIAGO, CANTÓN 05 SAN RAFAEL,
PROVINCIA 04 HEREDIA, COSTA RICA.

INFORMACIÓN REGISTRO PÚBLICO:
FOLIO REAL: 4-041200-000
PLANO CATASTRADO: 4-57389-2023
ÁREA SEGÚN CATASTRO: 256 m²

CONTENIDO:
CORTES
CORTE A-A.
CORTE B-B.
NOTAS.
SIMBOLOGÍA.

ESCALAS: 1:75

CONTROL DE REVISIONES		
REV.	FECHA	DESCRIPCIÓN
4	06-10-2026	LÁMINA +9.20 ALERO / +10.70 CUMBRERA (C04)
5	07-10-2026	REFERENCIAS A C01-C04 Y S03
6	07-10-2026	LISTA DEFINITIVA (22); PARA TRÁMITE

ESTADO:

PARA TRÁMITE
CFIA Y MUNICIPALIDAD

LUGAR	LÁMINA
COSTA RICA	A6
OCT 2026	TOTAL 22