



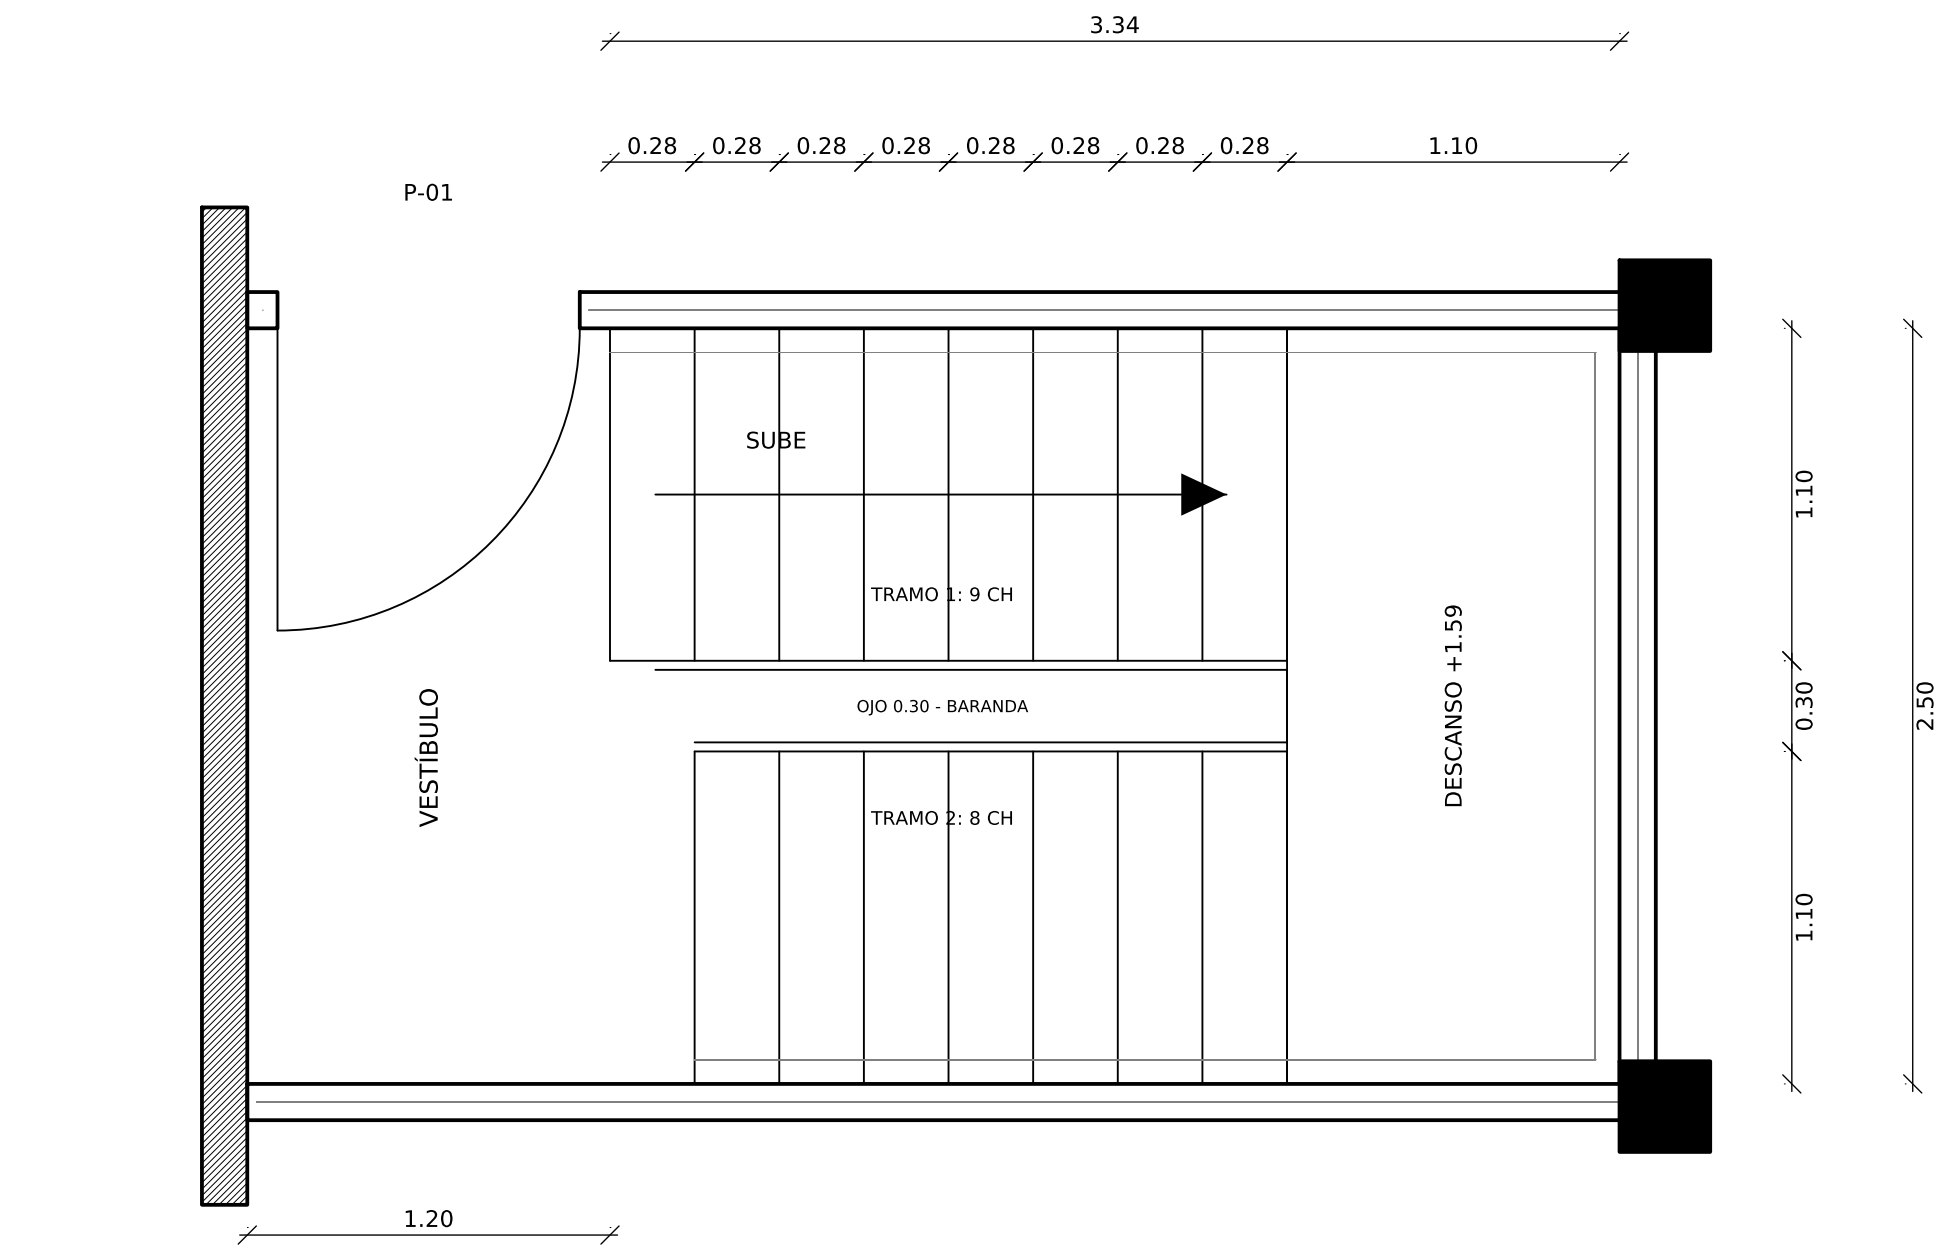


PLANTA DE ESCALERA

NIVEL 1 (VESTÍBULO); NIVELES 2 Y 3 IGUALES
Esc. 1:25

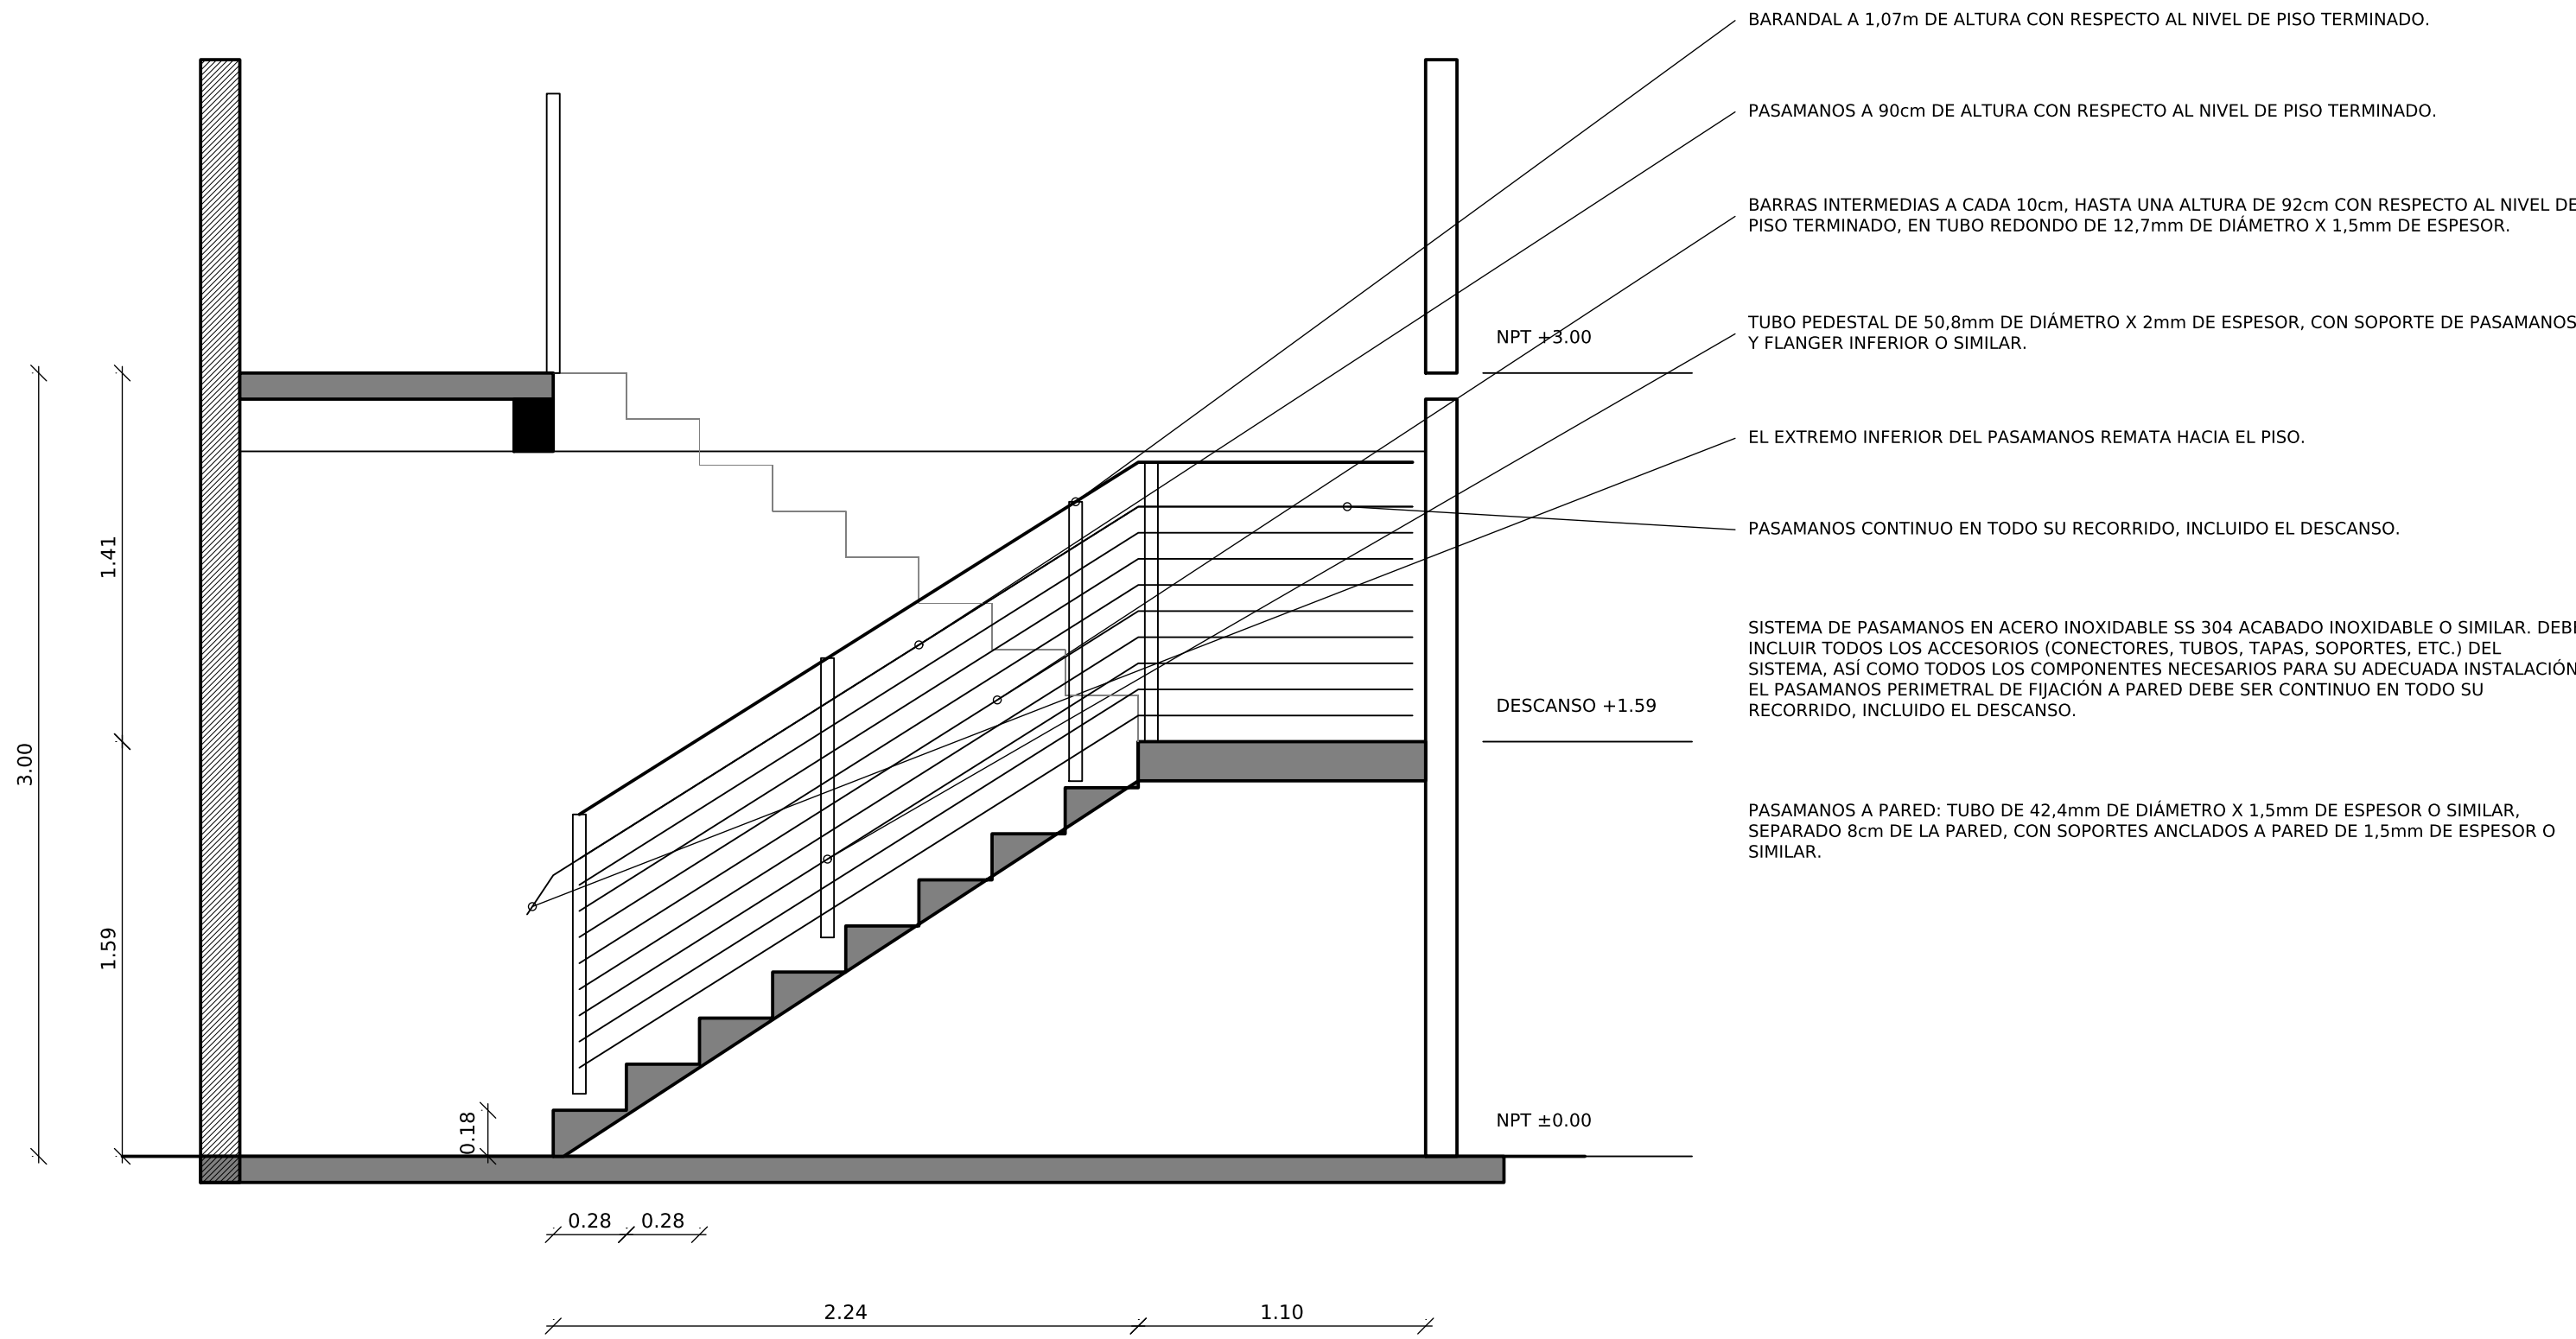


CORTE DE ESCALERA (EN EL OJO, VISTA HACIA EL EJE 4)

TRAMO NIVEL 1 A NIVEL 2; TRAMO NIVEL 2 A NIVEL 3 IGUAL
Esc. 1:25

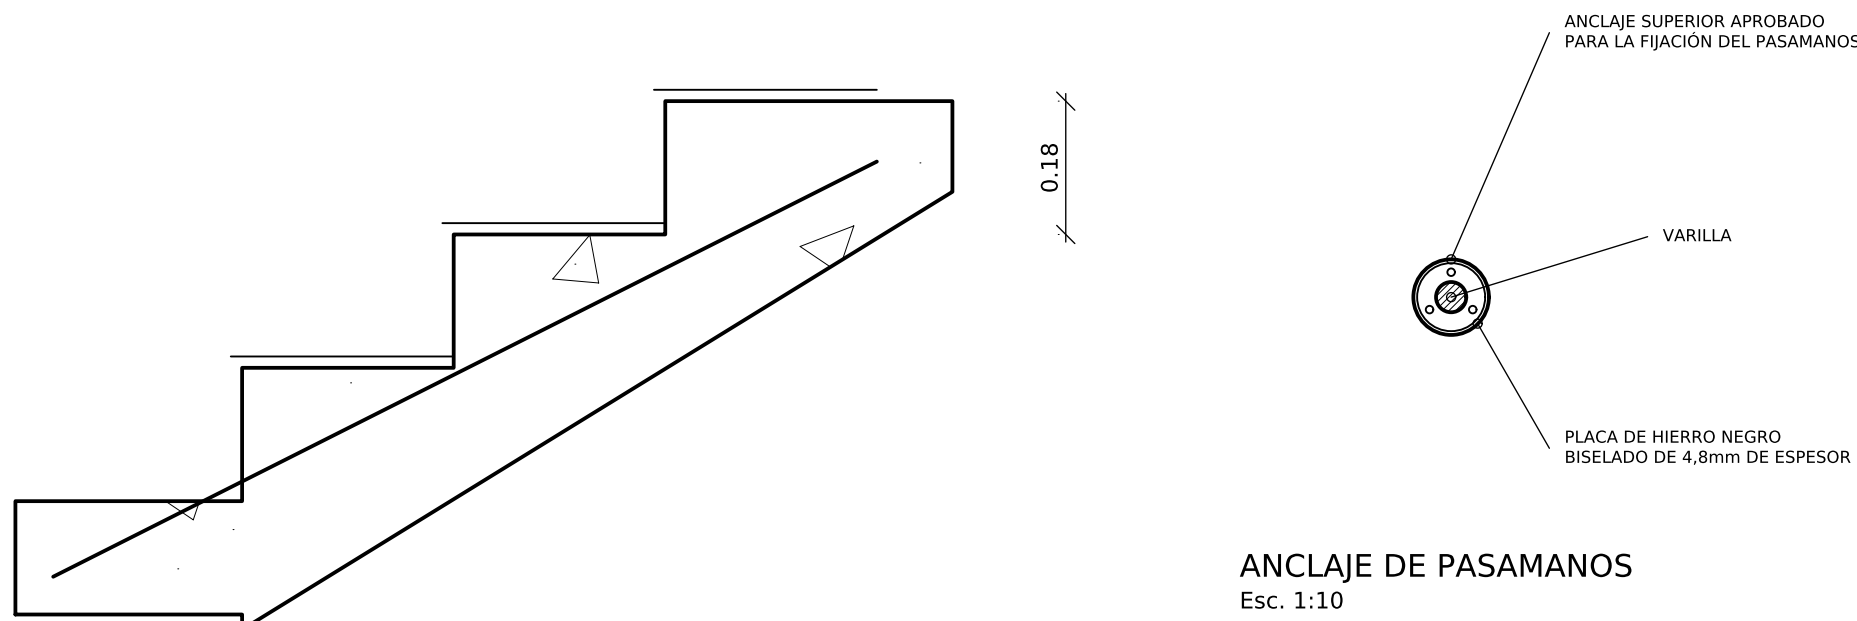

DETALLE DE ESCALÓN

LOSA DE ESCALERA DE CONCRETO ARMADO; ESPESOR Y REFUERZO SEGÚN PLANOS ESTRUCTURALES .
CONTRAHUELLA 0,176 m Y HUELLA 0,28 m. ACABADO DE GRADAS: PORCELANATO PI-A ANTIDESLIZANTE
CON NARIZ (VER A7).

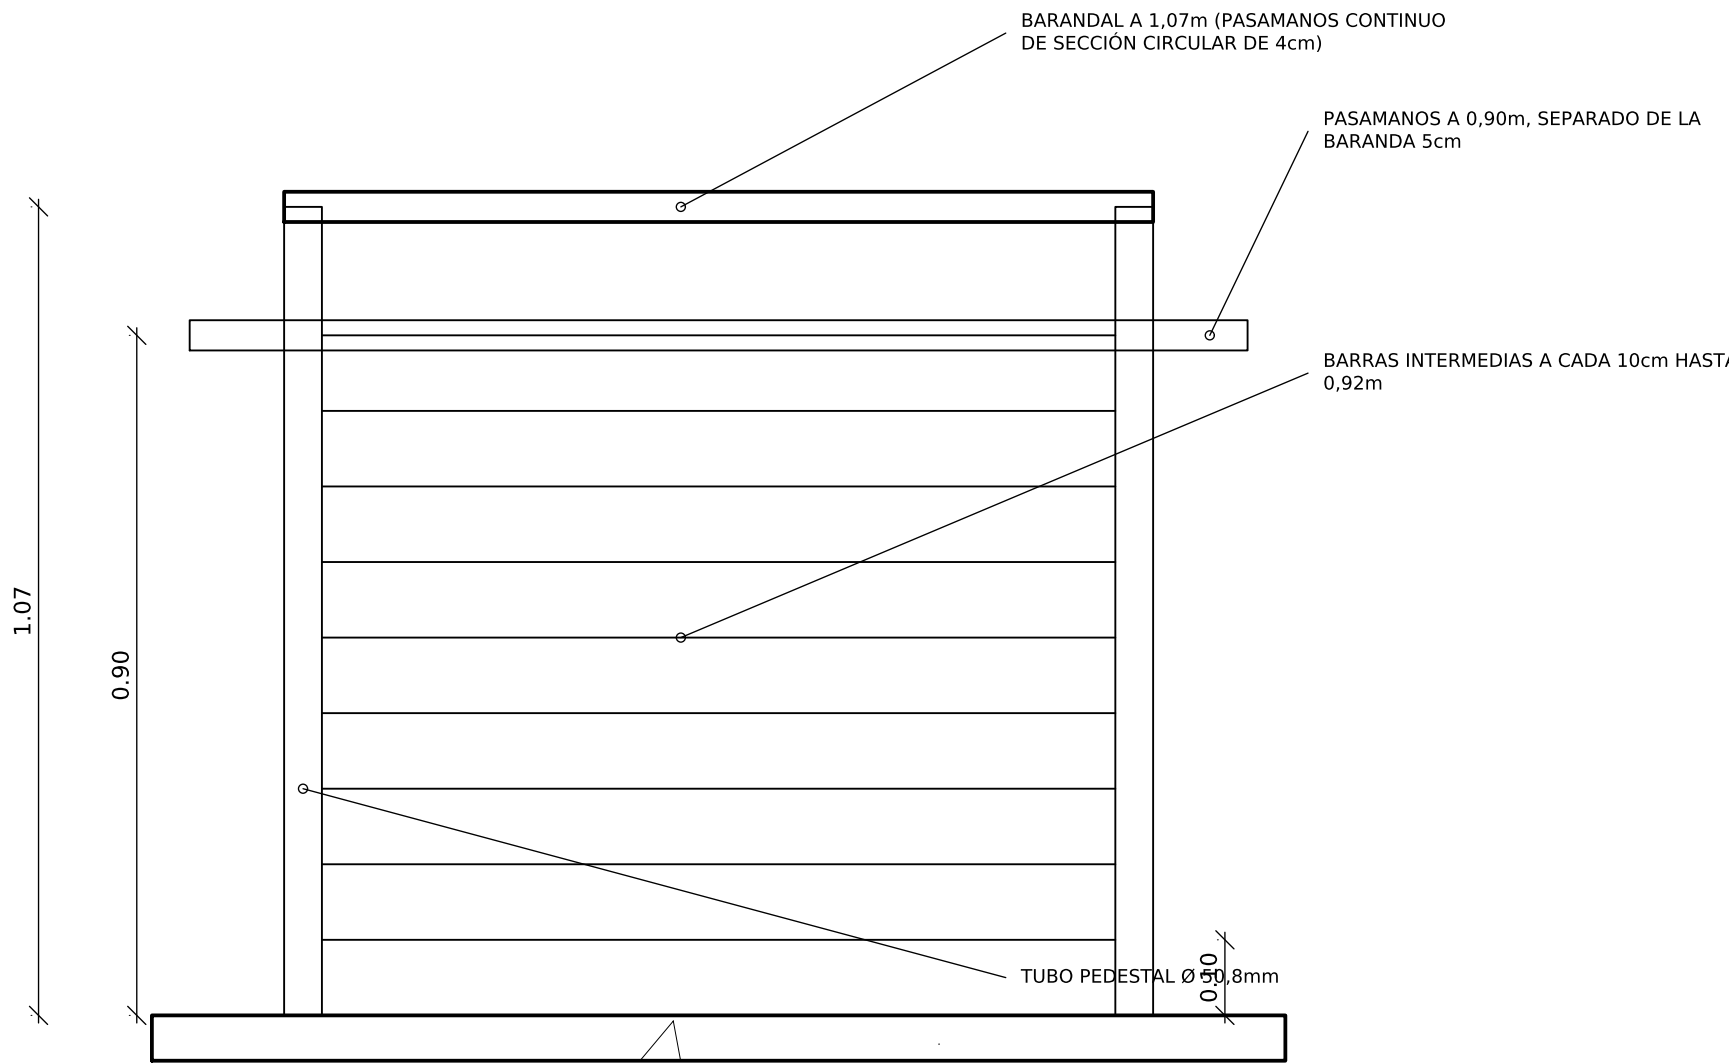

DETALLE DE BARANDA Y PASAMANOS

DISEÑO DE LAS BARANDAS Y PASAMANOS DE FORMA TAL QUE NO HAYA PROYECCIONES QUE PUEDAN ENGANCHARSE A LAS ROPAS SUELTAS.

NOTAS:

- TODAS LAS MEDIDAS ESTÁN DADAS EN METROS, SALVO INDICACIÓN CONTRARIA.
- ESCALERA EN U ENTRE EL NIVEL 1 Y EL NIVEL 3; 1,7 CONTRAHUELLAS DE 0,176 m Y HUELLA DE 0,28 m POR NIVEL (TRAMO 1: 9 CH; TRAMO 2: 8 CH); ANCHO DE TRAMO 1,10 m; OJO 0,30 m; DESCANSO 1,10 x 2,50 m A +1,59 (N1-N2) Y +4,59 (N2-N3).
- EN EL NIVEL 1 LA ESCALERA QUEDA EN EL VESTIBULO CERRADO (PAREDES STEEL TECH 0,12 m, PUERTA PRINCIPAL P-01). BARANDA EN EL OJO DE LA ESCALERA Y EN EL BORDE DEL PASILLO HACIA EL VACÍO EN LOS NIVELES 2 Y 3; PASAMANOS A PARED EN EL LADO EXTERIOR DE LOS TRAMOS.
- GRADAS Y DESCANSOS CON ACABADO DE PORCELANATO PI-A ANTIDESLIZANTE CON NARIZ.
- ESTRUCTURA DE LA ESCALERA SEGÚN PLANOS ESTRUCTURALES.

ESPACIO PARA SELLOS Y TIMBRES

CivilCon Diseño y Construcción SRLTDA
Céd. Jurídica: 3-102-762712

PROFESIONAL RESPONSABLE:
DIRECTOR TÉCNICO:
Steven Viales (Civil) IC-40759
David Barrantes (Electricidad) IE-27499

PROYECTO:
VIVIENDA UNIFAMILIAR
DISTRITO 03 SANTIAGO, CANTÓN 05 SAN RAFAEL,
PROVINCIA 04 HEREDIA, COSTA RICA.

INFORMACIÓN REGISTRO PÚBLICO:
FOLIO REAL: 4-041200-000
PLANO CATASTRADO: 4-57389-2023
ÁREA SEGÚN CATASTRO: 256 m²

CONTENIDO:
ESCALERA
PLANTA.
CORTE.
DETALLES DE ESCALÓN, BARANDA
Y PASAMANOS.
NOTAS.

ESCALAS: INDICADAS

CONTROL DE REVISIONES

REV.	FECHA	DESCRIPCIÓN
0	06-10-2026	VERSIÓN DE TRABAJO PARA REVISIÓN
1	06-10-2026	ACABADO DE GRADAS; SIN CITAS NI MARCAS
2	07-10-2026	LISTA DEFINITIVA (22); PARA TRÁMITE

ESTADO:

PARA TRÁMITE
CFIA Y MUNICIPALIDAD

LUGAR	LÁMINA
COSTA RICA	A8
OCT 2026	TOTAL 22