


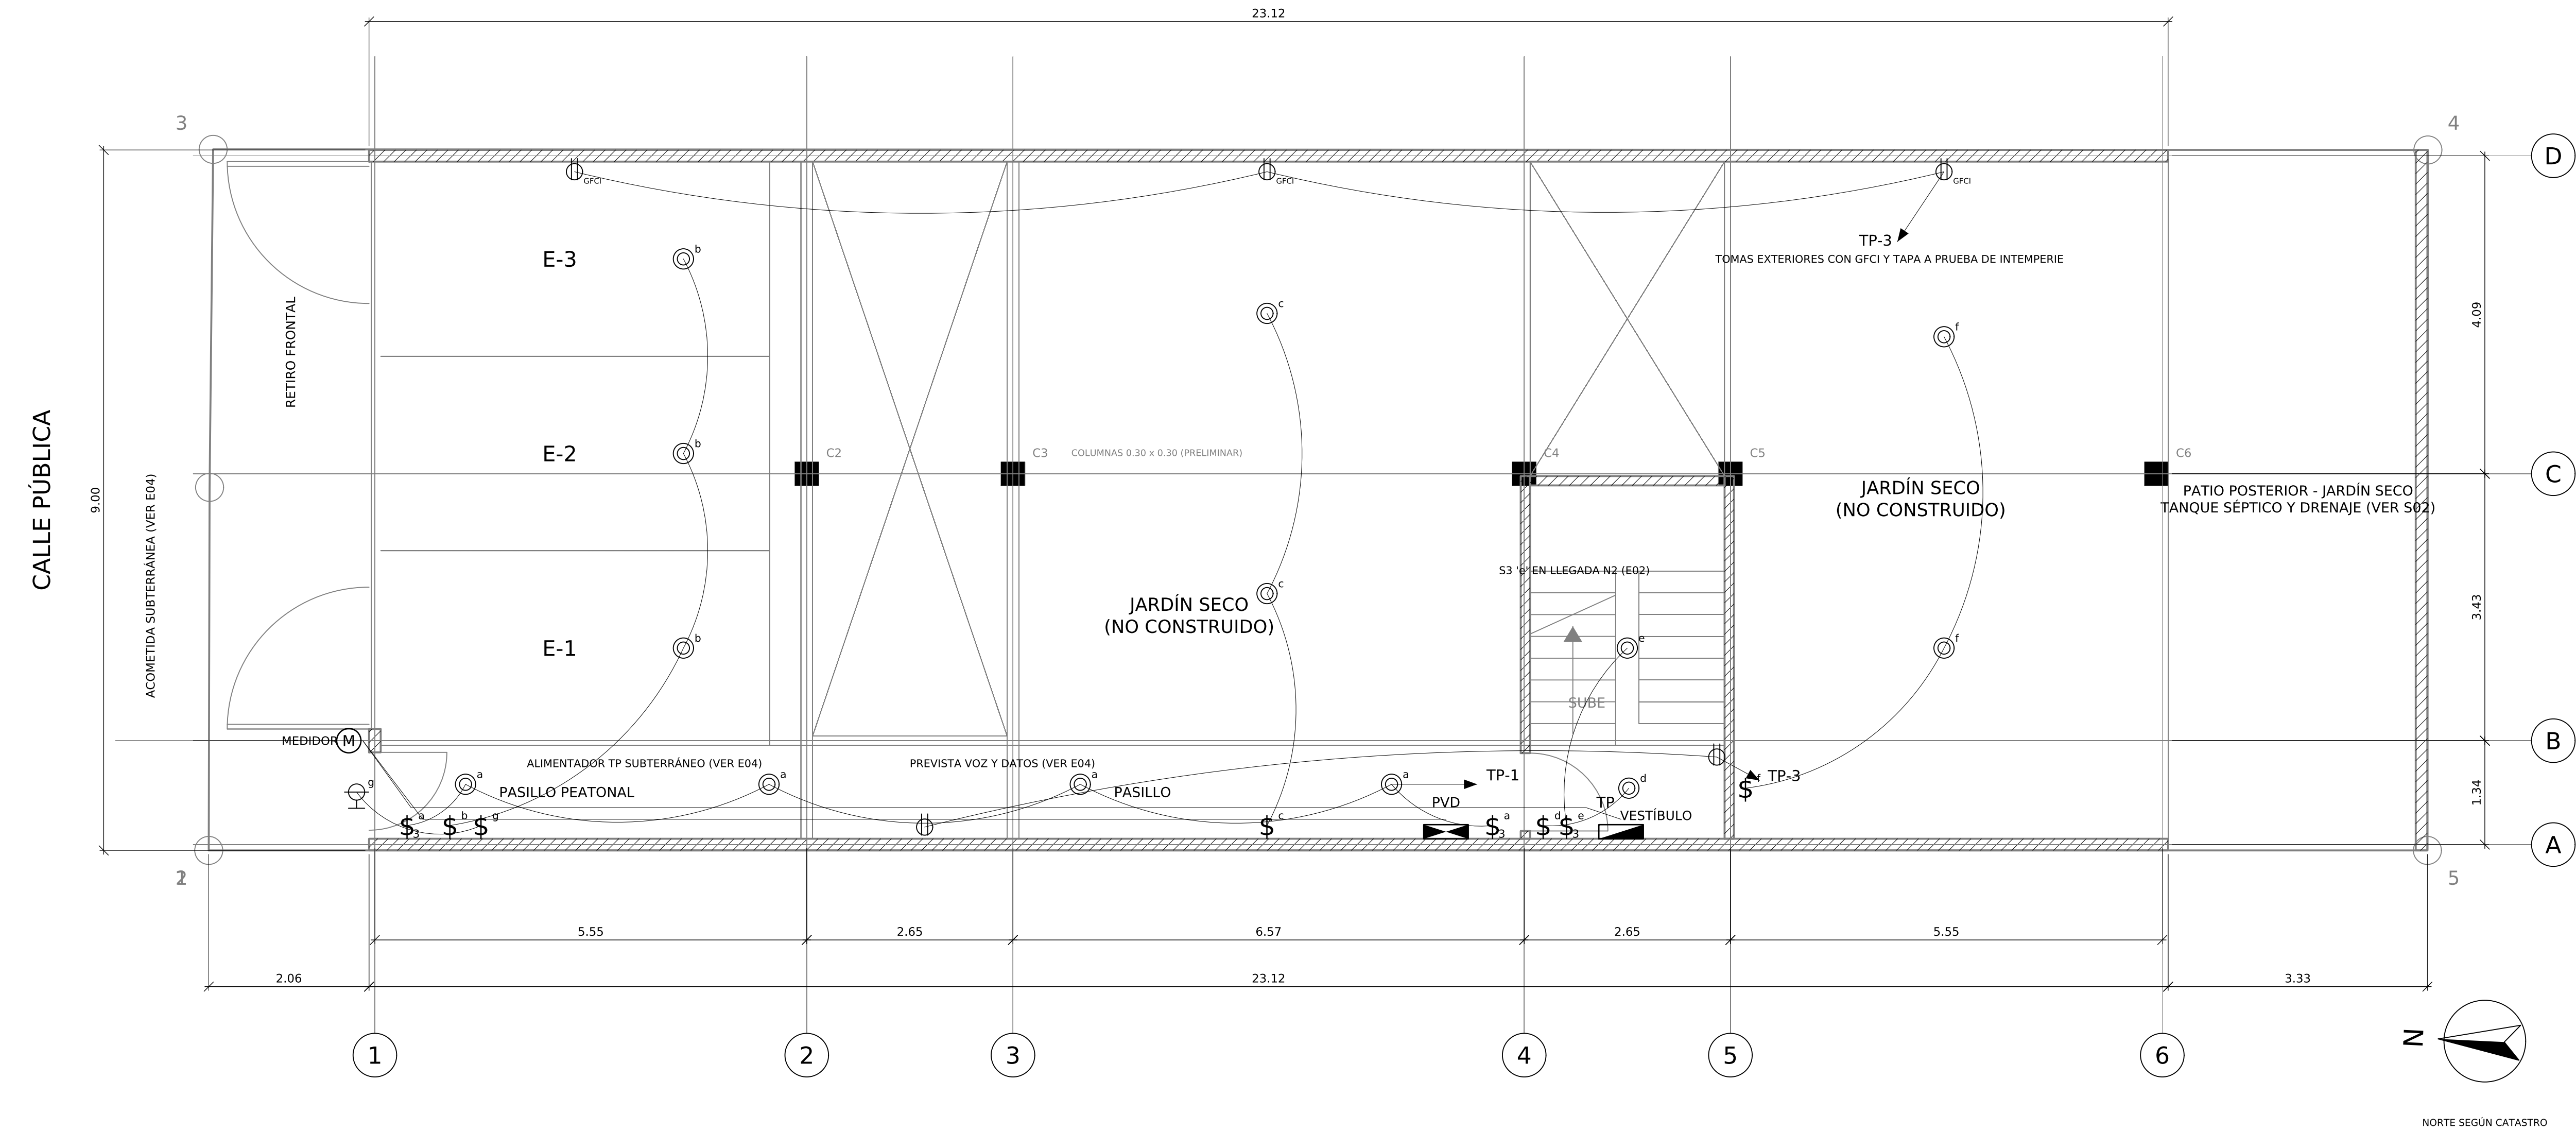

PLANTA ELÉCTRICA NIVEL 1
ILUMINACIÓN, TOMACORRIENTES Y VOZ/DATOS
Esc. 1:50



SIMBOLOGÍA ELÉCTRICA

	MEDIDOR ELÉCTRICO A 1,90 m S.N.P.T.
	TABLERO DE DISTRIBUCIÓN ELÉCTRICA
	TABLERO DE DISTRIBUCIÓN DE VOZ Y DATOS
	LUMINARIA EN SUPERFICIE DE CIELO
	LUMINARIA EMPOTRADA EN CIELO DE GYPSUM
	LUMINARIA EN PARED (APLIQUE)
	APAGADOR SENCILLO 15 A, 120 V, A 1,30 m S.N.P.T.
	APAGADOR DE TRES VÍAS 20 A, 120 V, A 1,30 m S.N.P.T.
	TOMACORRIENTE DOBLE POLARIZADO 120 V, 20 A, A 0,30 m S.N.P.T.
	TOMACORRIENTE DOBLE POLARIZADO 120 V, 20 A, A 1,50 m S.N.P.T.
	TOMACORRIENTE DOBLE 120 V, 20 A, CON PROTECCIÓN GFCI
	SALIDA ESPECIAL 240 V (VER CUADRO DE TABLEROS, E04)
	SALIDA DE TELEVISIÓN
	SALIDA DE VOZ Y DATOS

CIRCUITOS DEL NIVEL 1 (TABLERO TP)

CIRC.	DESCRIPCIÓN	DISYUNTOR	CONDUCTORES THHN
TP-1	ILUMINACIÓN NIVEL 1 (a-g)	1P-20 A	2 #12 + #12 T
TP-3	TOMACORRIENTES NIVEL 1 (GFCI EN EXTERIOR)	1P-20 A	2 #12 + #12 T

LETRAS a-g: AGRUPACIÓN DE LUMINARIAS POR APAGADOR. ALIMENTADORES DE TN2 Y TN3, DEMÁS CIRCUITOS DEL TP: VER E04.

NOTAS:

- TODAS LAS MEDIDAS ESTÁN DADAS EN METROS.
- LAS MEDIDAS DEBEN SER VERIFICADAS EN SITIO.
- TODA LA INSTALACIÓN SE REALIZARÁ EN TUBERÍA SEGÚN SE INDICA EN EL TABLERO. EN EL NIVEL 1 (ESTRUCTURA EXPUESTA, SIN CIELO) LA TUBERÍA EXPUESTA A MENOS DE 2,5 m DE ALTURA SERÁ METÁLICA (EMT).
- TODAS LAS SALIDAS, TANTO ELÉCTRICAS COMO DE TV Y DATOS, SERÁN POR MEDIO DE CAJAS DE CONEXIÓN RECTANGULARES U OCTOGONALES CON SUS RESPECTIVAS TAPAS.
- SE IDENTIFICARÁN EN EL TABLERO LOS DIFERENTES CIRCUITOS Y SE DEJARÁN AL MENOS DOS TUBOS PREVISTOS COMO ADICIONALES.
- TOMACORRIENTES EN ESTACIONAMIENTOS Y EXTERIORES CON PROTECCIÓN GFCI Y TAPA A PRUEBA DE INTEMPERIE.
- DIAGRAMA UNIFILAR, CUADROS DE TABLEROS, NOTAS GENERALES Y DETALLES EN LA LÁMINA E04.

ESPACIO PARA SELLOS Y TIMBRES

CivilCon Diseño y Construcción SRLTDA
Céd. Jurídica: 3-102-762712

PROFESIONAL RESPONSABLE:
DIRECTOR TÉCNICO:
Steven Viales (Civil) IC-40759
David Barrantes (Electricidad) IE-27499

PROYECTO:
VIVIENDA UNIFAMILIAR
DISTRITO 03 SANTIAGO, CANTÓN 05 SAN RAFAEL,
PROVINCIA 04 HEREDIA, COSTA RICA.

INFORMACIÓN REGISTRO PÚBLICO:
FOLIO REAL: 4-041200-000
PLANO CATASTRADO: 4-57389-2023
ÁREA SEGÚN CATASTRO: 256 m²

CONTENIDO:
ELECTRICIDAD
PLANTA ELÉCTRICA NIVEL 1.
ILUMINACIÓN Y TOMACORRIENTES.
VOZ Y DATOS.
SIMBOLOGÍA.
NOTAS.

ESCALAS: 1:50

CONTROL DE REVISIONES		
REV.	FECHA	DESCRIPCIÓN
0	06-10-2026	VERSIÓN DE TRABAJO PARA REVISIÓN
1	06-10-2026	SIN MENCIÓN A SECADORA
2	07-10-2026	LISTA DEFINITIVA (22); PARA TRÁMITE

ESTADO:
PARA TRÁMITE
CFIA Y MUNICIPALIDAD

LUGAR	LÁMINA
COSTA RICA	E01
OCT 2026	TOTAL 22