


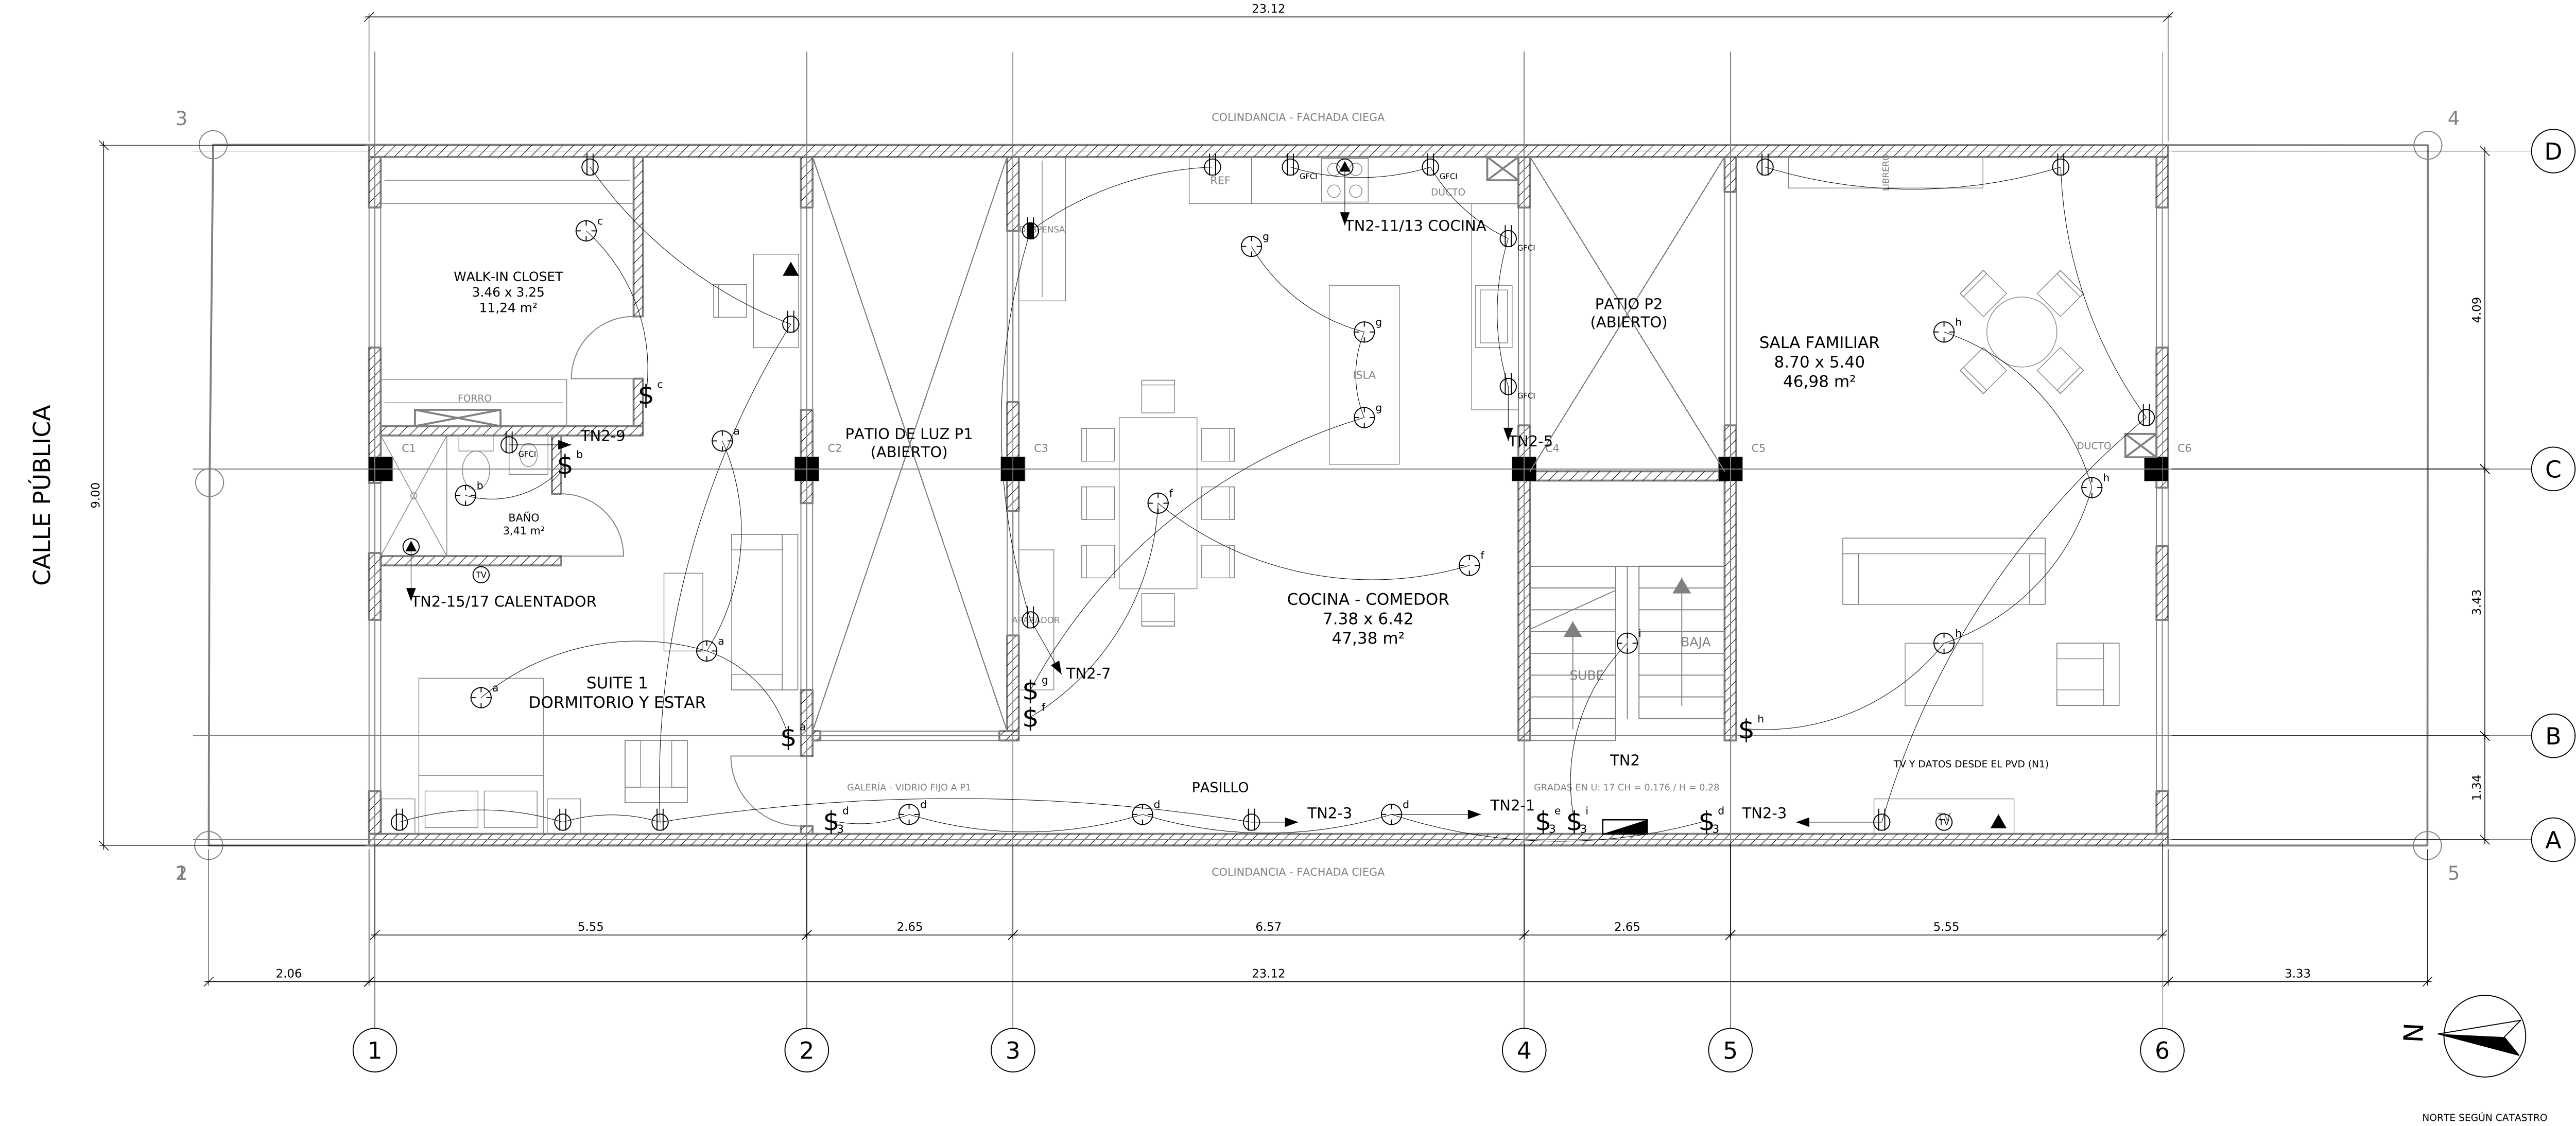

PLANTA ELÉCTRICA NIVEL 2  
ILUMINACIÓN, TOMACORRIENTES Y VOZ/DATOS  
Esc. 1:50



SIMBOLOGÍA ELÉCTRICA

|  |                                                               |
|--|---------------------------------------------------------------|
|  | MEDIDOR ELÉCTRICO A 1,90 m S.N.P.T.                           |
|  | TABLERO DE DISTRIBUCIÓN ELÉCTRICA                             |
|  | TABLERO DE DISTRIBUCIÓN DE VOZ Y DATOS                        |
|  | LUMINARIA EN SUPERFICIE DE CIELO                              |
|  | LUMINARIA EMPOTRADA EN CIELO DE GYPSUM                        |
|  | LUMINARIA EN PARED (APLIQUE)                                  |
|  | APAGADOR SENCILLO 15 A, 120 V, A 1,30 m S.N.P.T.              |
|  | APAGADOR DE TRES VÍAS 20 A, 120 V, A 1,30 m S.N.P.T.          |
|  | TOMACORRIENTE DOBLE POLARIZADO 120 V, 20 A, A 0,30 m S.N.P.T. |
|  | TOMACORRIENTE DOBLE POLARIZADO 120 V, 20 A, A 1,50 m S.N.P.T. |
|  | TOMACORRIENTE DOBLE 120 V, 20 A, CON PROTECCIÓN GFCI          |
|  | SALIDA ESPECIAL 240 V (VER CUADRO DE TABLEROS, E04)           |
|  | SALIDA DE TELEVISIÓN                                          |
|  | SALIDA DE VOZ Y DATOS                                         |

CIRCUITOS DEL NIVEL 2 (SUBTABLERO TN2)

| CIRC.     | DESCRIPCIÓN                               | DISYUNTOR | CONDUCTORES THHN |
|-----------|-------------------------------------------|-----------|------------------|
| TN2-1     | ILUMINACIÓN NIVEL 2 (a-i)                 | 1P-20 A   | 2 #12 + #12 T    |
| TN2-3     | TOMACORRIENTES GENERALES NIVEL 2          | 1P-20 A   | 2 #12 + #12 T    |
| TN2-5     | TOMAS DE COCINA 1 (GFCI)                  | 1P-20 A   | 2 #12 + #12 T    |
| TN2-7     | TOMAS DE COCINA 2 (REFRIGERADORA Y OTROS) | 1P-20 A   | 2 #12 + #12 T    |
| TN2-9     | TOMAS DE BAÑO (GFCI)                      | 1P-20 A   | 2 #12 + #12 T    |
| TN2-11/13 | COCINA ELÉCTRICA 240 V                    | 2P-40 A   | 2 #8 + #10 T     |
| TN2-15/17 | CALENTADOR DE PASO BAÑO SUITE 1, 240 V    | 2P-40 A   | 2 #10 + #10 T    |

LETRAS a-i: AGRUPACIÓN DE LUMINARIAS POR APAGADOR, CARGAS, CAÍDAS DE TENSIÓN Y ALIMENTADOR DEL TN2: VER E04.

NOTAS:

- TODAS LAS MEDIDAS ESTÁN DADAS EN METROS.
- LAS MEDIDAS DEBEN SER VERIFICADAS EN SITIO.
- TODA LA INSTALACIÓN SE REALIZARÁ EN TUBERÍA SEGÚN SE INDICA EN EL TABLERO; EN NINGÚN CASO SE USARÁ TUBERÍA EXPUESTA (TUBERÍA SOBRE CIELO DE GYPSUM Y EN PAREDES).
- TODAS LAS SALIDAS, TANTO ELÉCTRICAS COMO DE TV Y DATOS, SERÁN POR MEDIO DE CAJAS DE CONEXIÓN RECTANGULARES U OCTOGONALES CON SUS RESPECTIVAS TAPAS.
- SE IDENTIFICARÁN EN EL TABLERO LOS DIFERENTES CIRCUITOS Y SE DEJARÁN AL MENOS DOS TUBOS PREVISTOS COMO ADICIONALES.
- TOMACORRIENTES DE COCINA SOBRE MUEBLE Y DE BAÑO CON PROTECCIÓN GFCI.
- SALIDAS ESPECIALES 240 V: COCINA ELÉCTRICA Y CALENTADOR DE PASO DEL BAÑO; ALTURA Y CONEXIÓN SEGÚN EL FABRICANTE DEL EQUIPO.
- GRADAS: EL S3 'g' CONTROLA, CON EL DEL VESTÍBULO, LA LUZ DE GRADAS DEL NIVEL 1 (E01); EL S3 'i' CONTROLA, CON EL DEL NIVEL 3, LA LUZ DE GRADAS DEL NIVEL 2 (E03).
- SALIDAS DE TV Y DATOS CON TUBERÍA INDEPENDIENTE DESDE EL PVD DEL NIVEL 1.
- DIAGRAMA UNIFILAR, ALIMENTADOR DEL TN2, CUADROS DE TABLEROS, NOTAS GENERALES Y DETALLES EN LA LÁMINA E04.

ESPACIO PARA SELLOS Y TIMBRES

CivilCon Diseño y Construcción SRLTDA  
Céd. Jurídica: 3-102-762712

PROFESIONAL RESPONSABLE:  
DIRECTOR TÉCNICO:  
Steven Viales (Civil) IC-40759  
David Barrantes (Electricidad) IE-27499

PROYECTO:  
**VIVIENDA UNIFAMILIAR**  
DISTRITO 03 SANTIAGO, CANTÓN 05 SAN RAFAEL,  
PROVINCIA 04 HEREDIA, COSTA RICA.

INFORMACIÓN REGISTRO PÚBLICO:  
FOLIO REAL: 4-041200-000  
PLANO CATASTRADO: 4-57389-2023  
ÁREA SEGÚN CATASTRO: 256 m²

CONTENIDO:  
**ELECTRICIDAD**  
PLANTA ELÉCTRICA NIVEL 2.  
ILUMINACIÓN Y TOMACORRIENTES.  
VOZ Y DATOS.  
SIMBOLOGÍA.  
NOTAS.

ESCALAS: 1:50

CONTROL DE REVISIONES

| REV. | FECHA      | DESCRIPCIÓN                         |
|------|------------|-------------------------------------|
| 0    | 06-10-2026 | VERSIÓN DE TRABAJO PARA REVISIÓN    |
| 1    | 07-10-2026 | LISTA DEFINITIVA (22); PARA TRÁMITE |

ESTADO:

PARA TRÁMITE  
CFIA Y MUNICIPALIDAD

| LUGAR      | LÁMINA   |
|------------|----------|
| COSTA RICA | E02      |
| OCT 2026   | TOTAL 22 |