
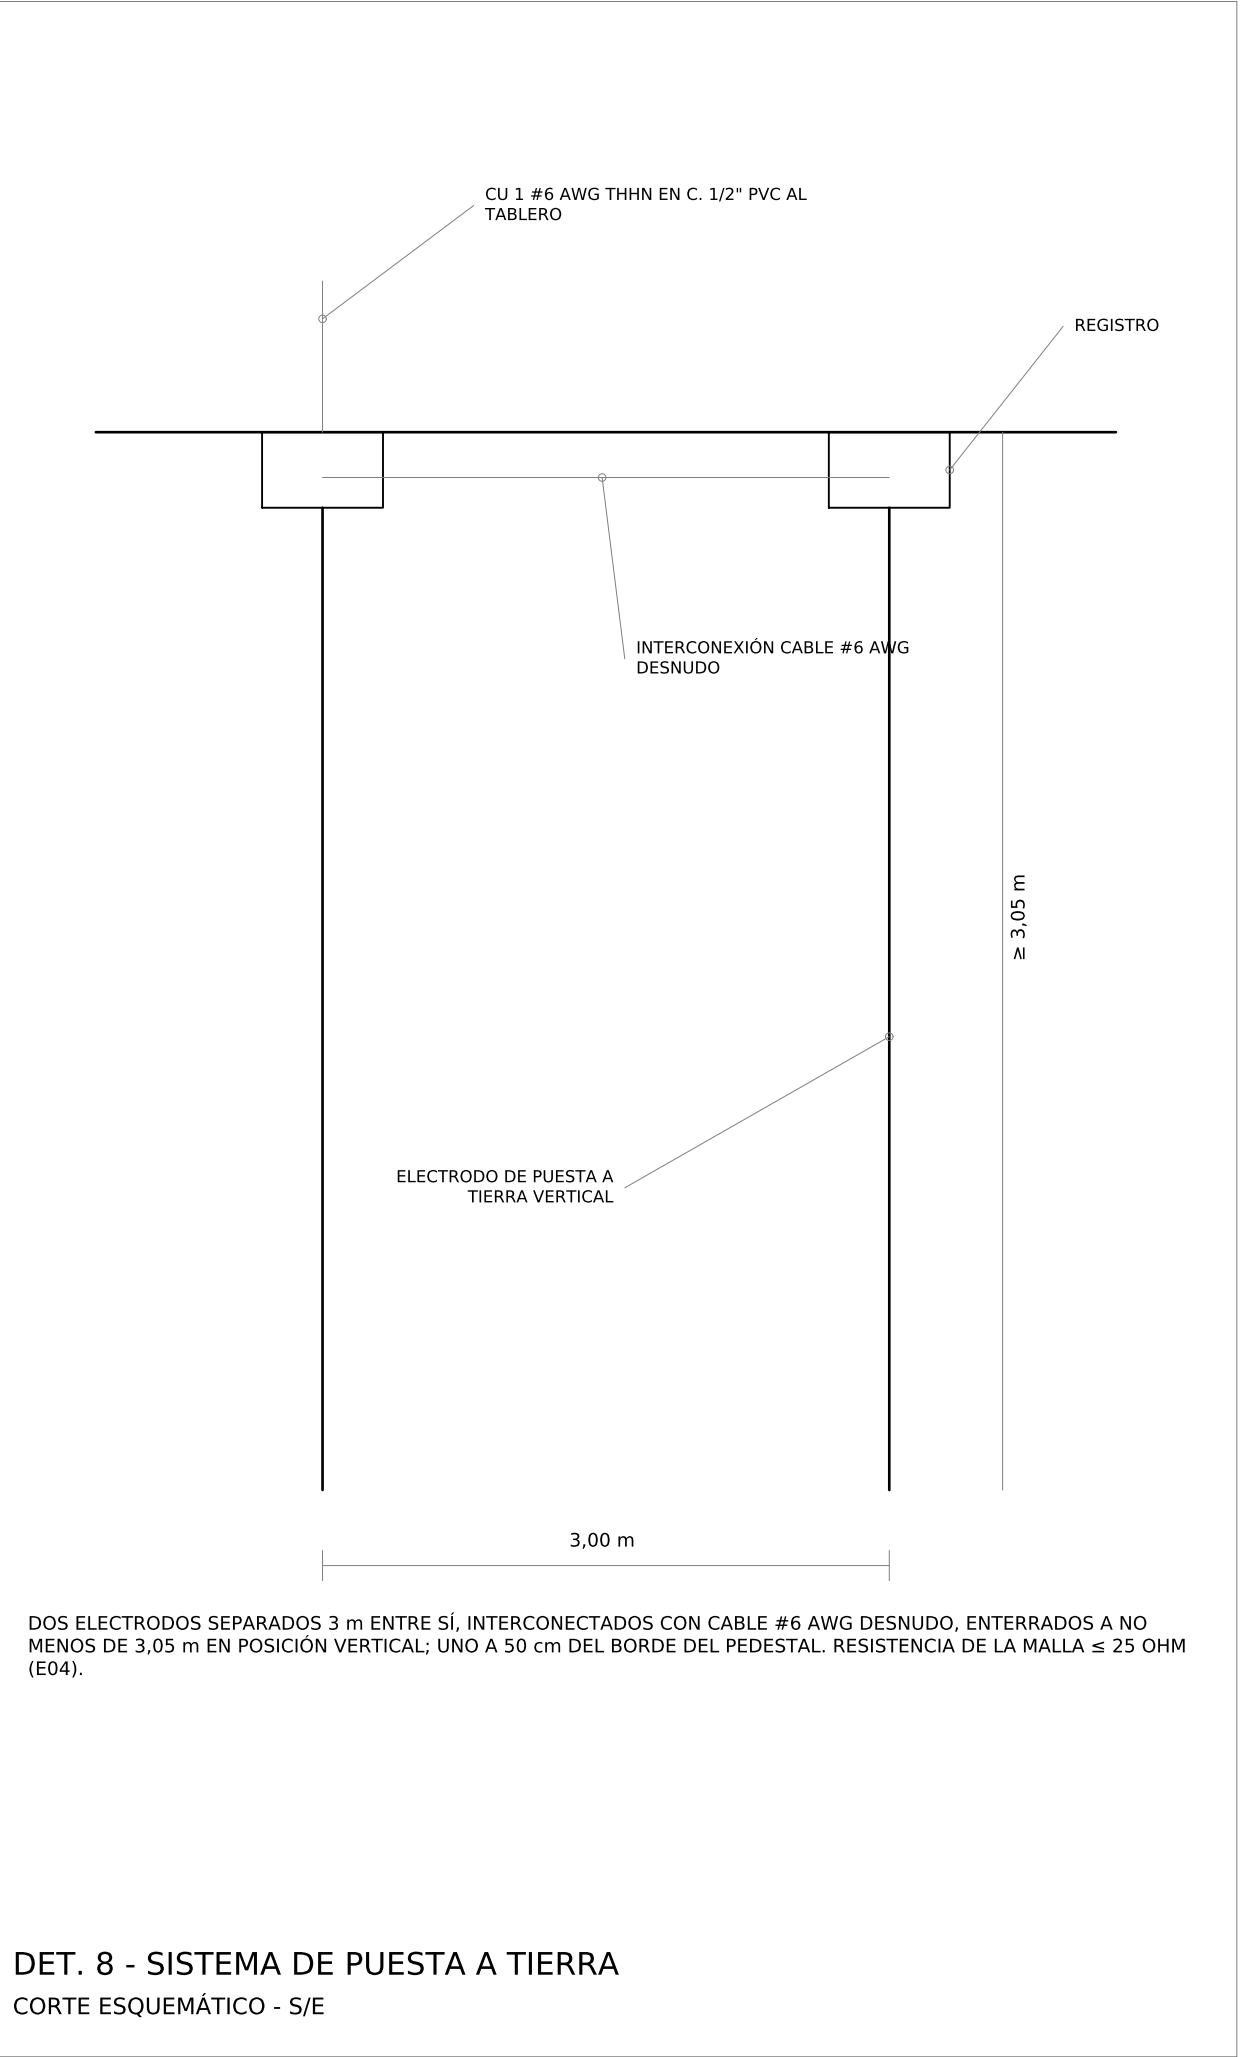
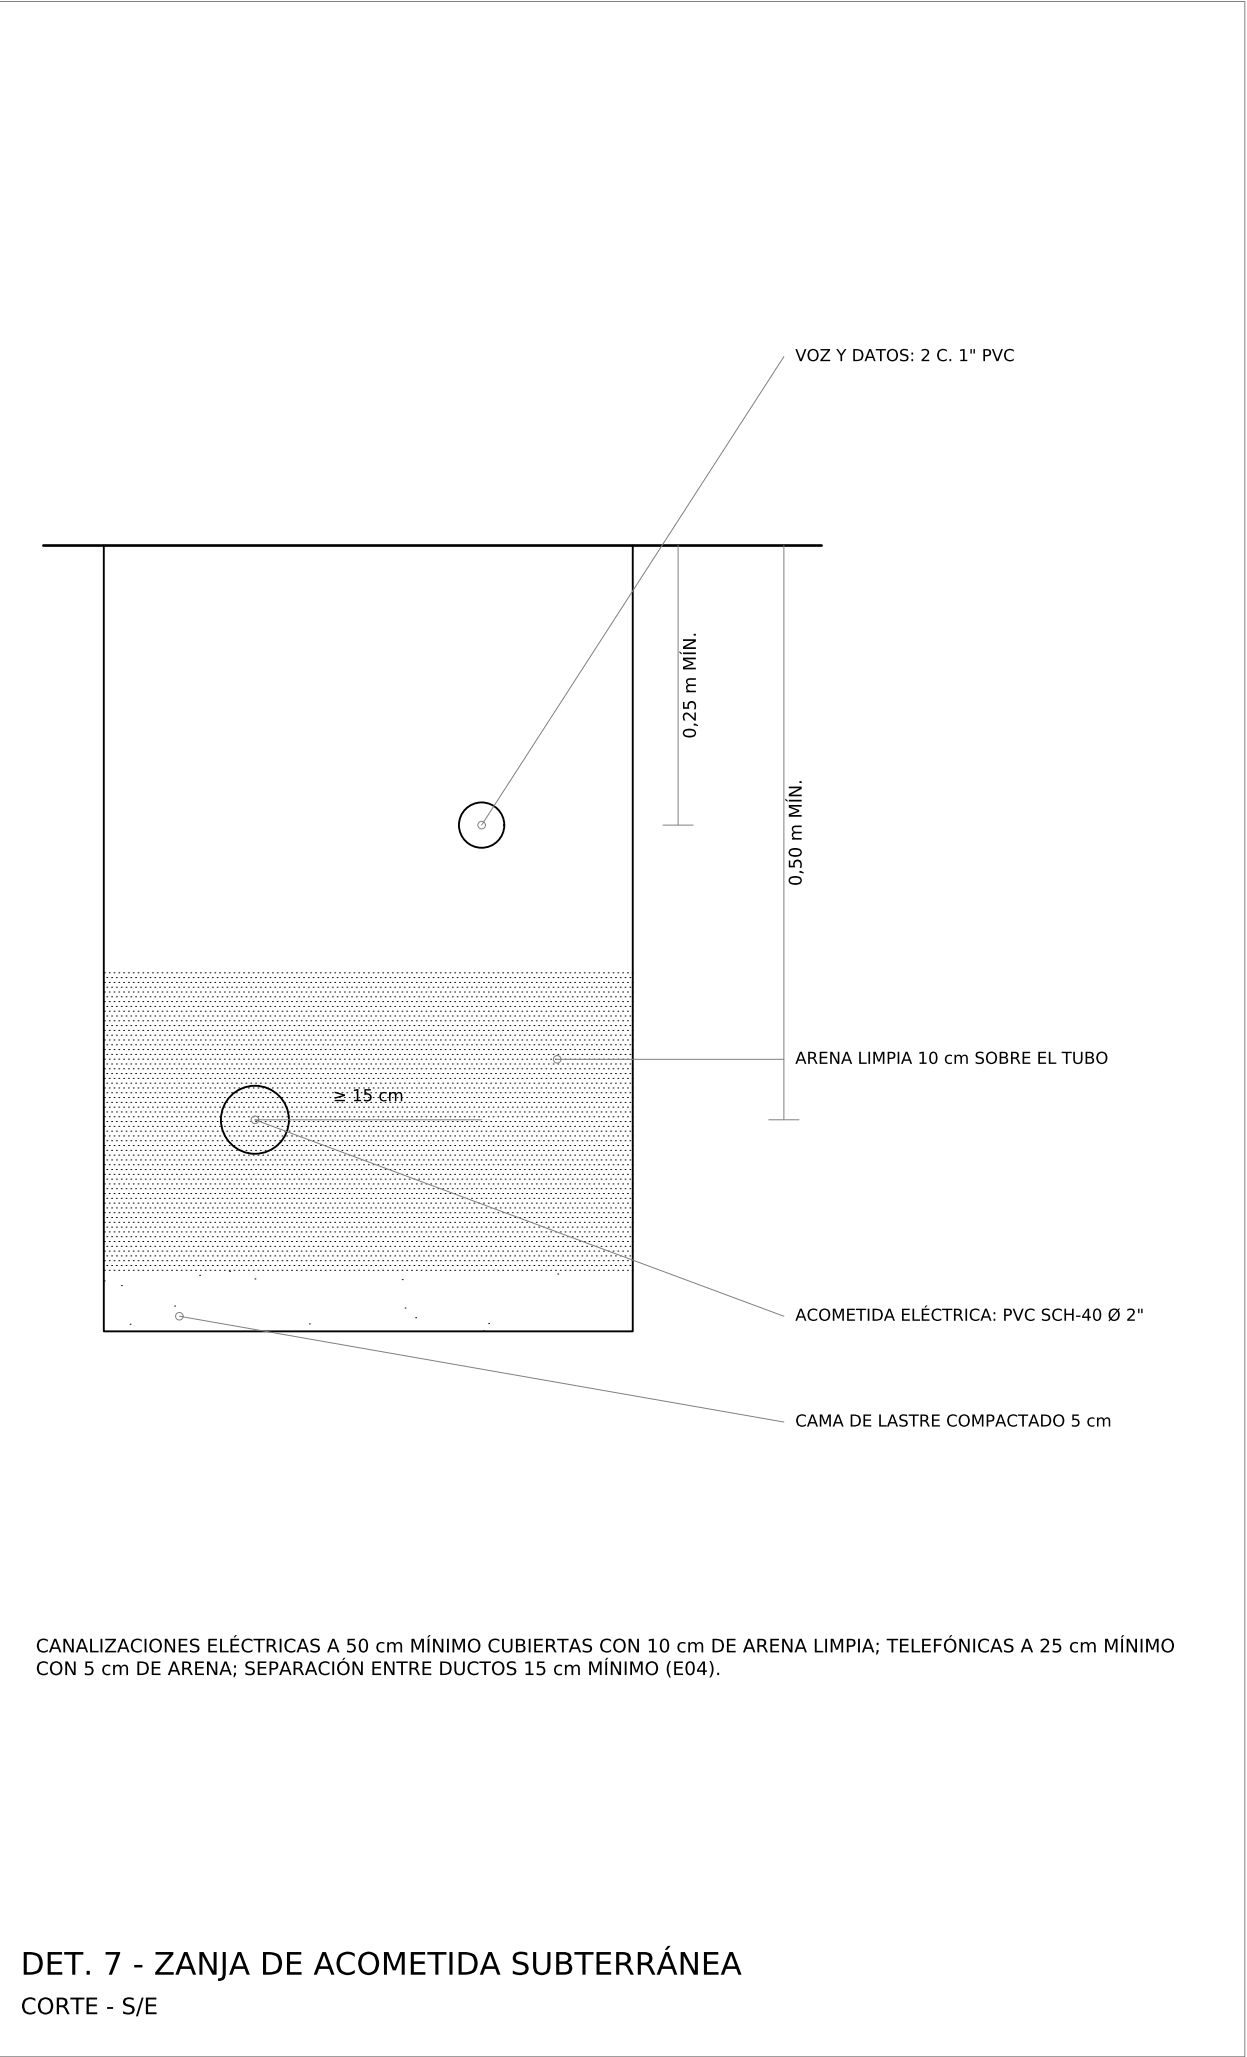
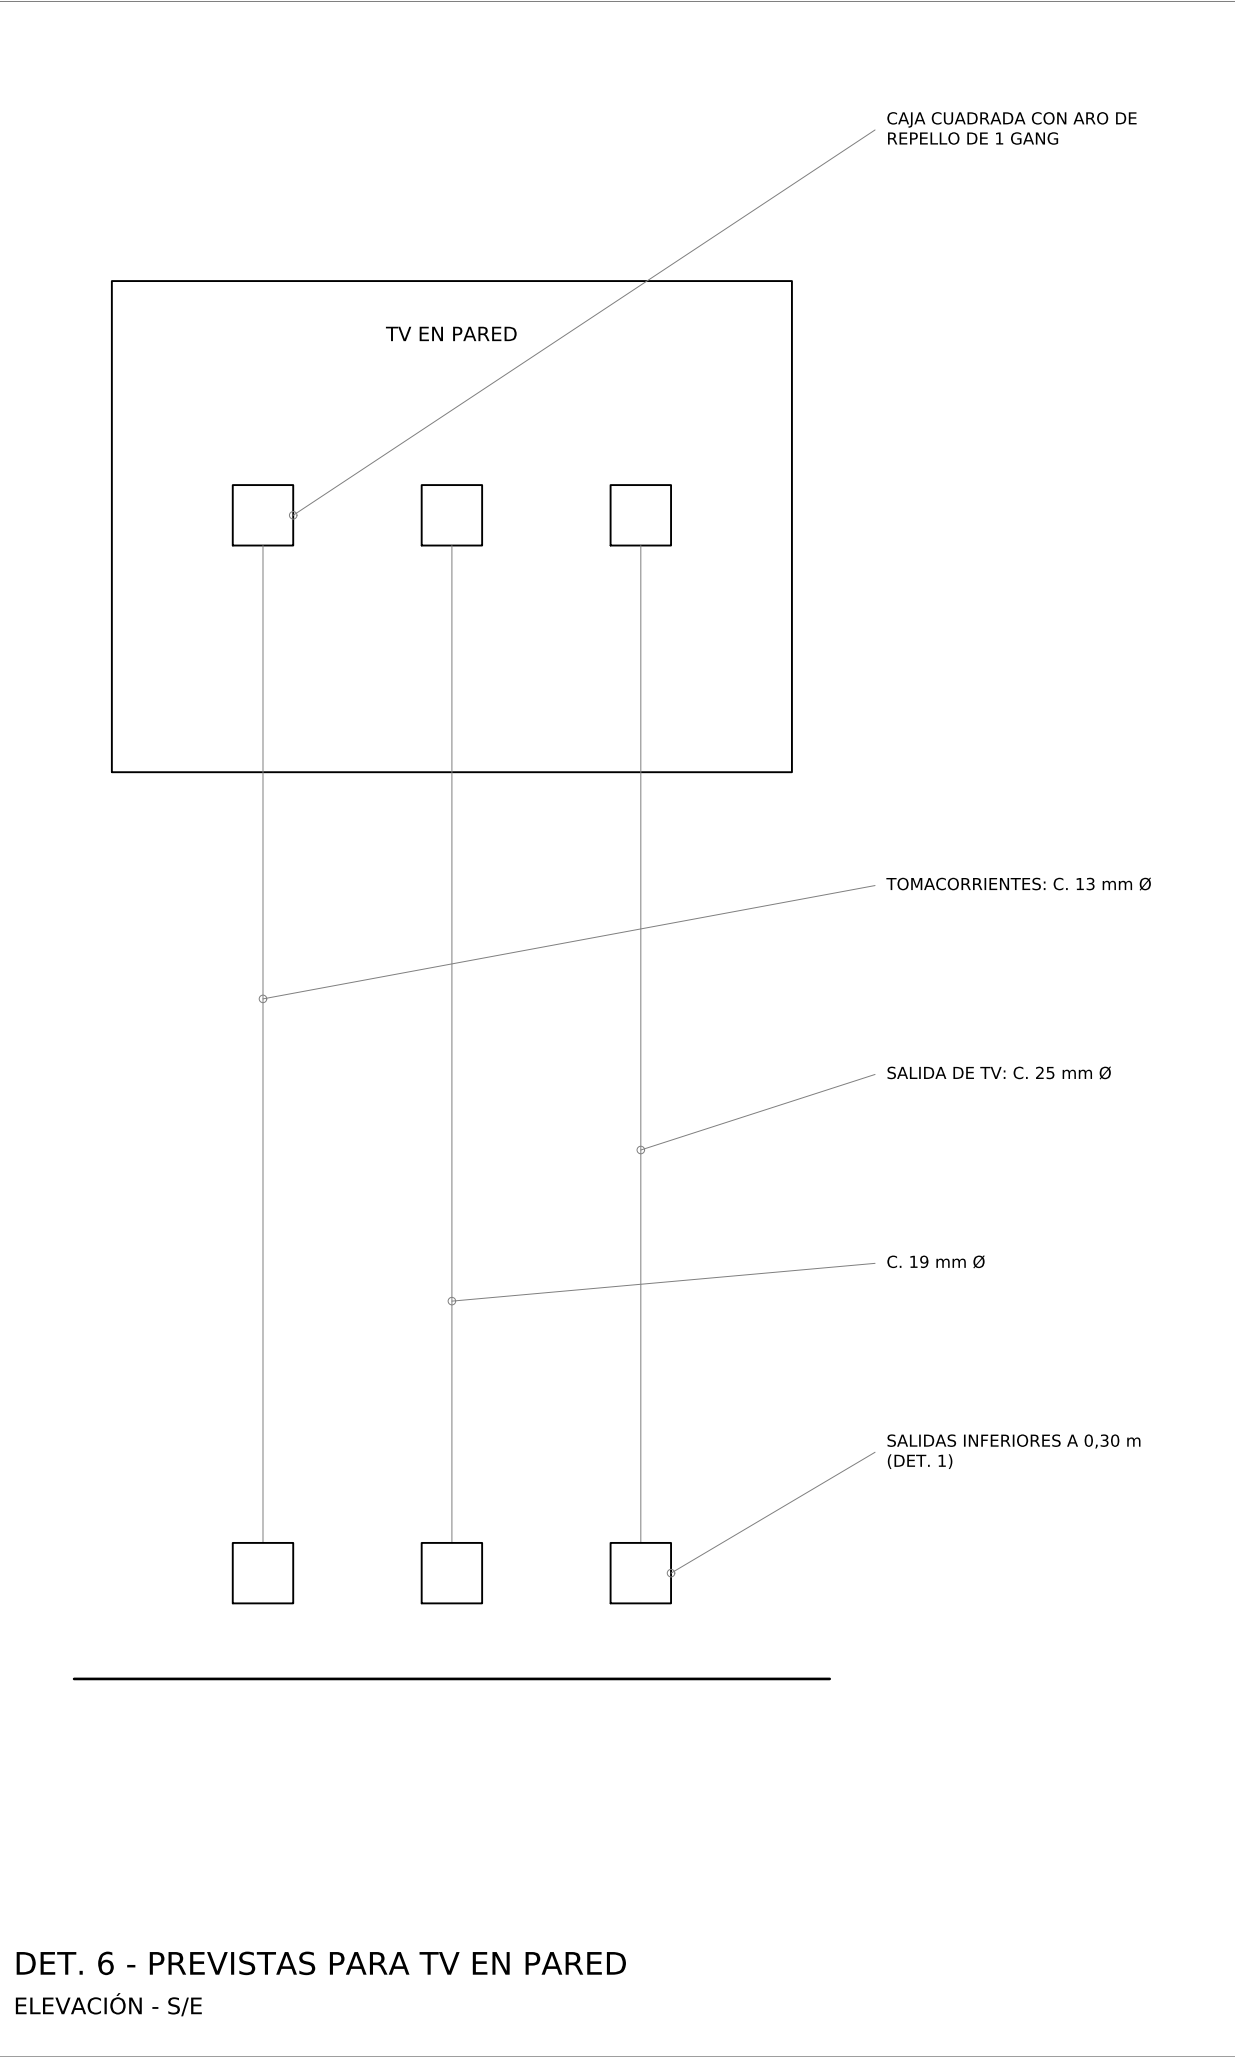
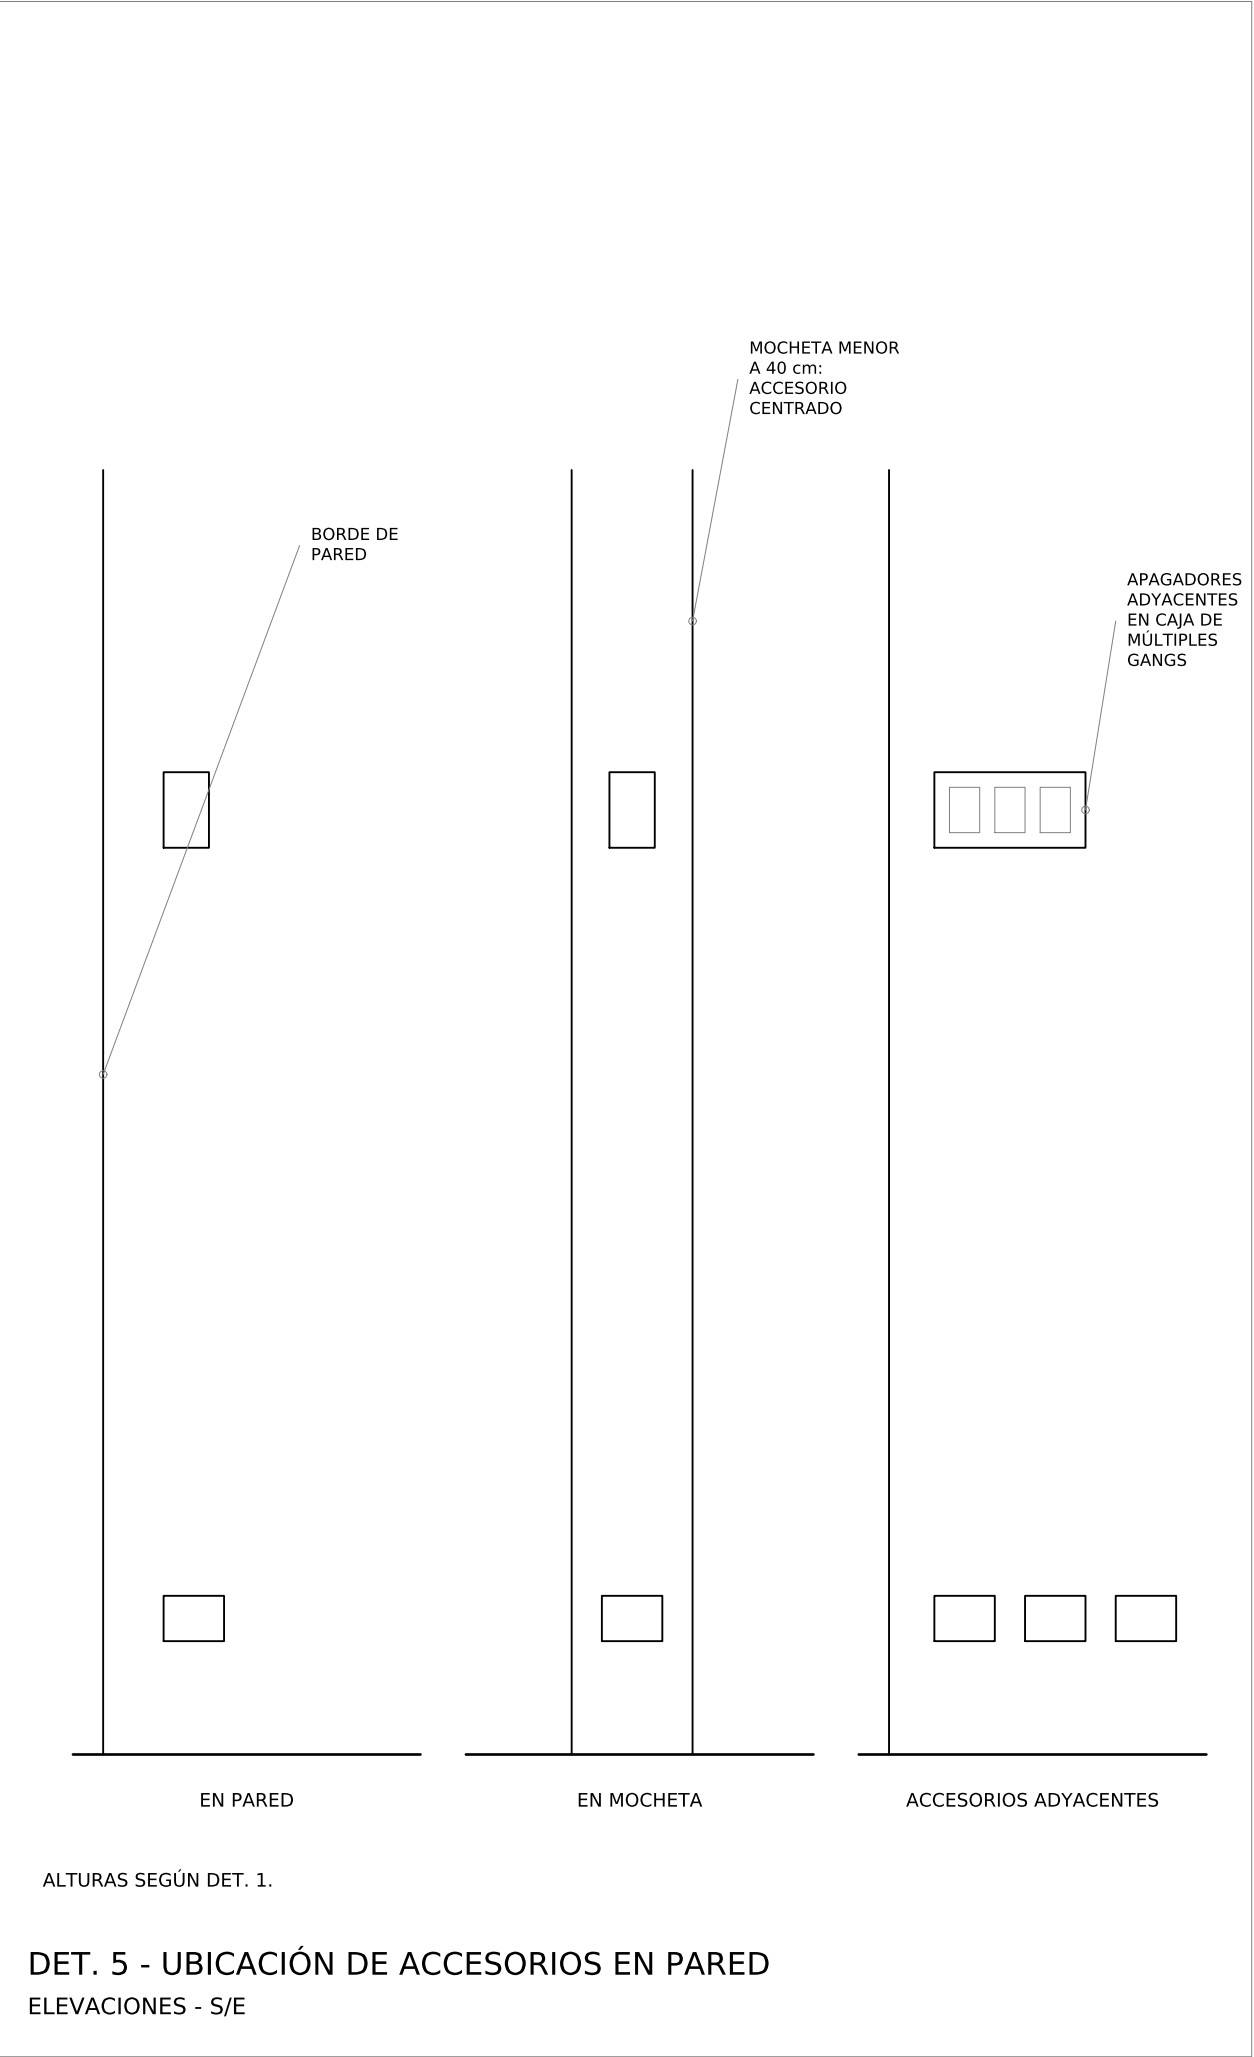
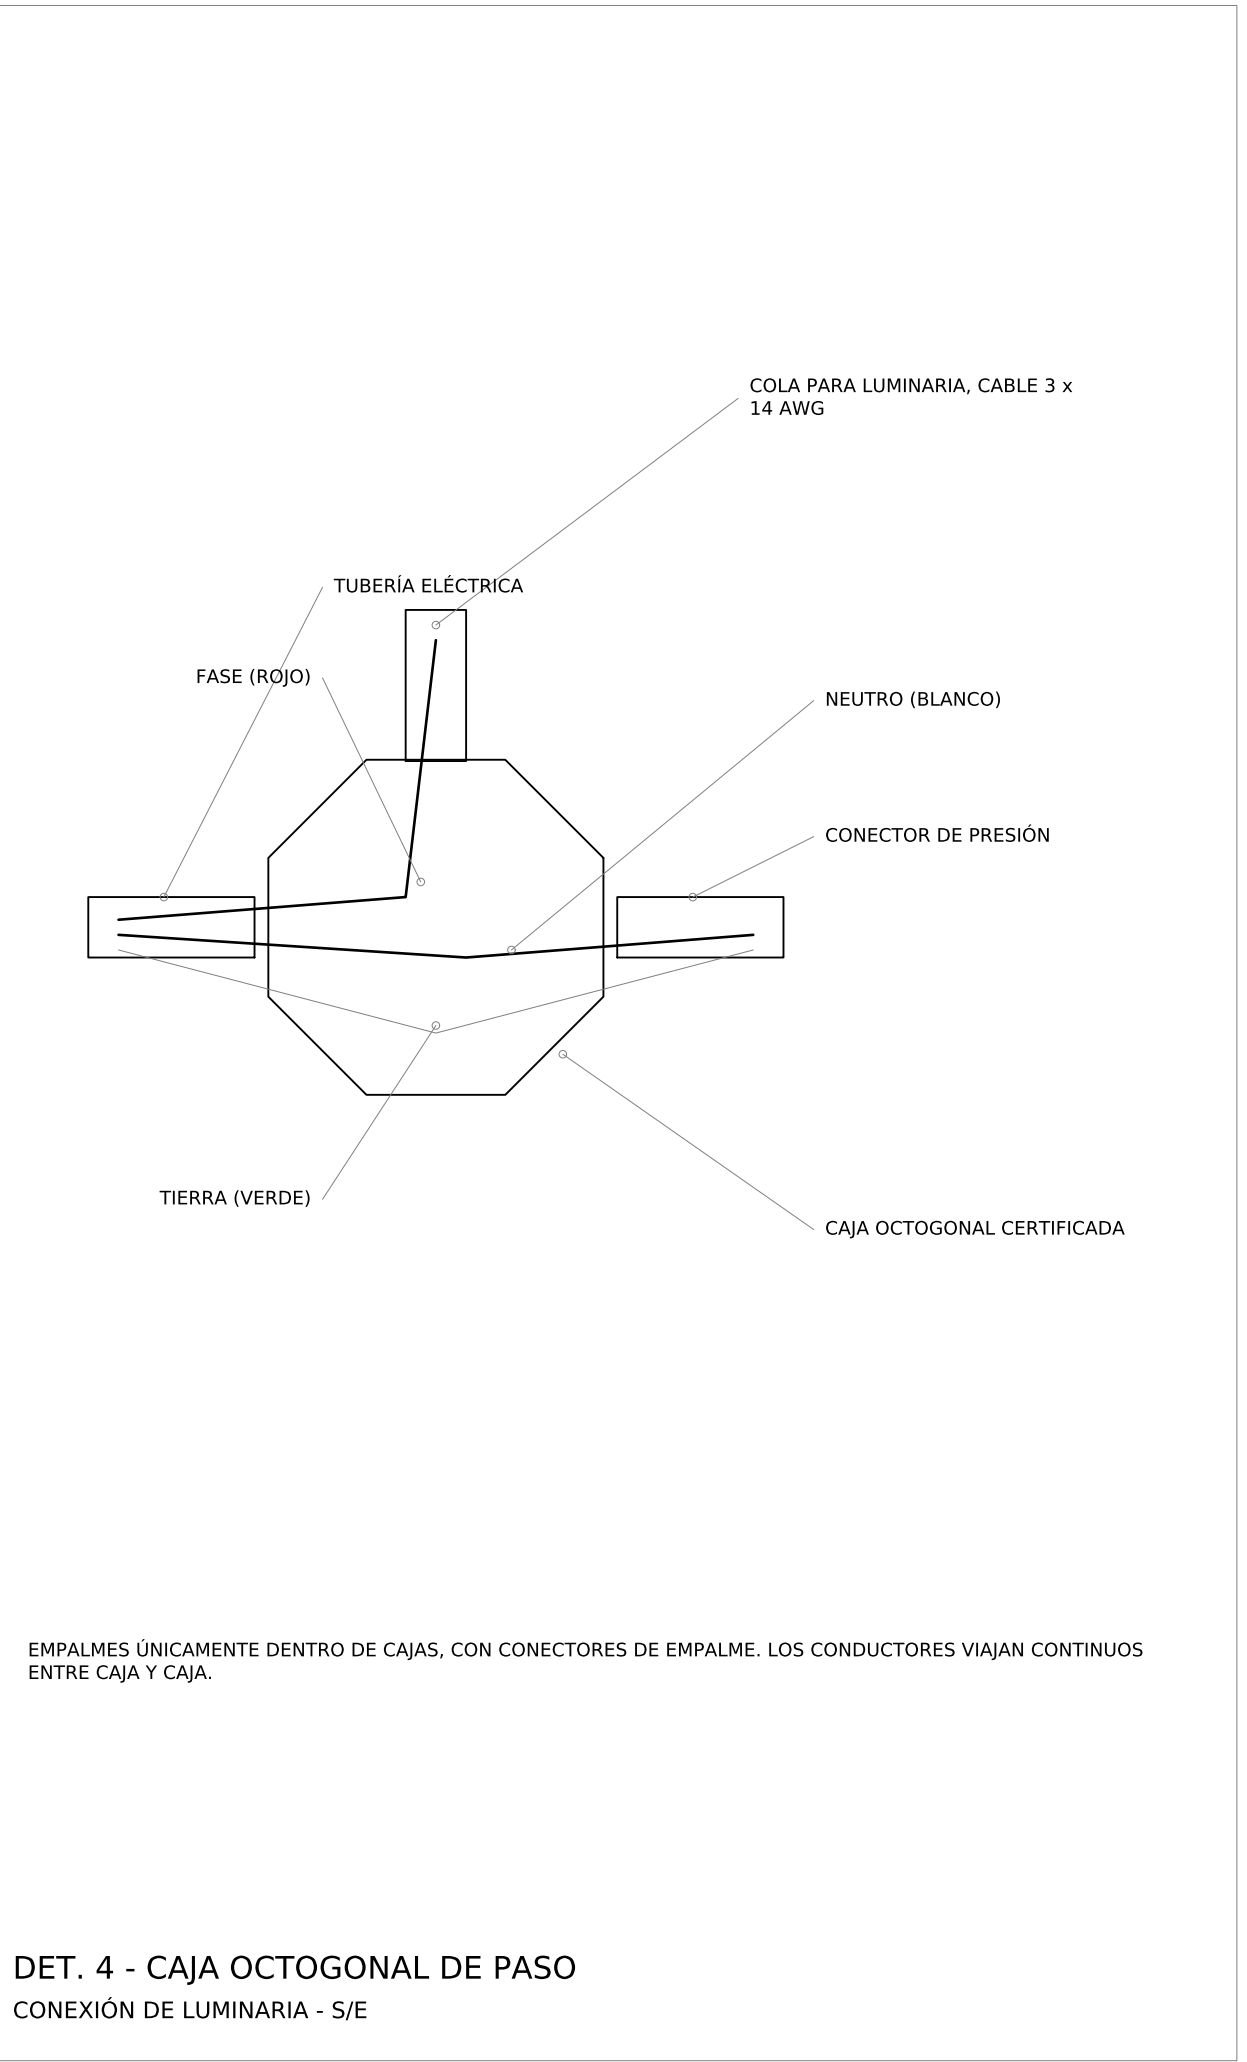
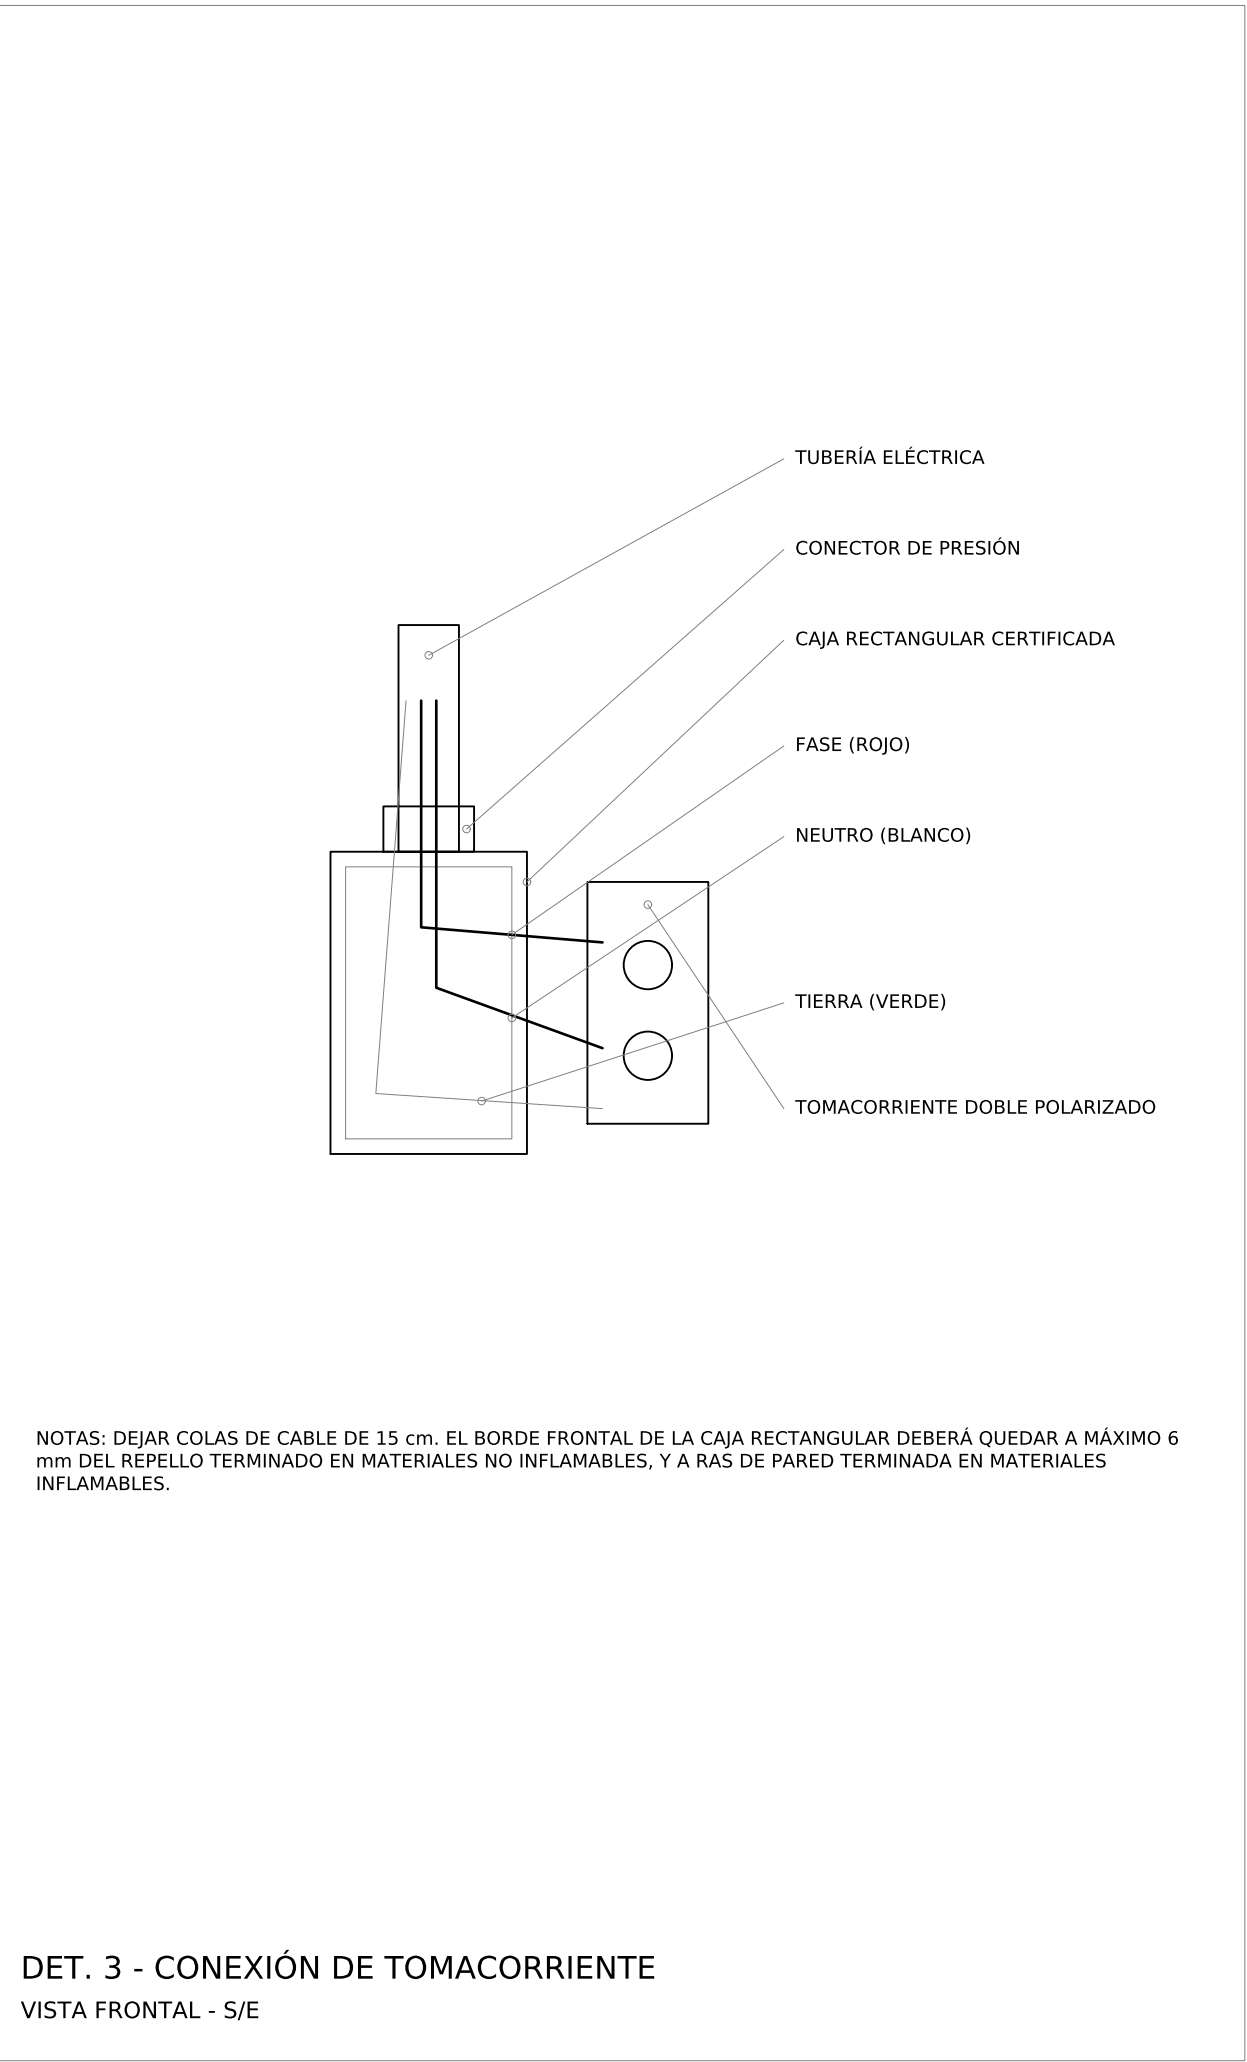
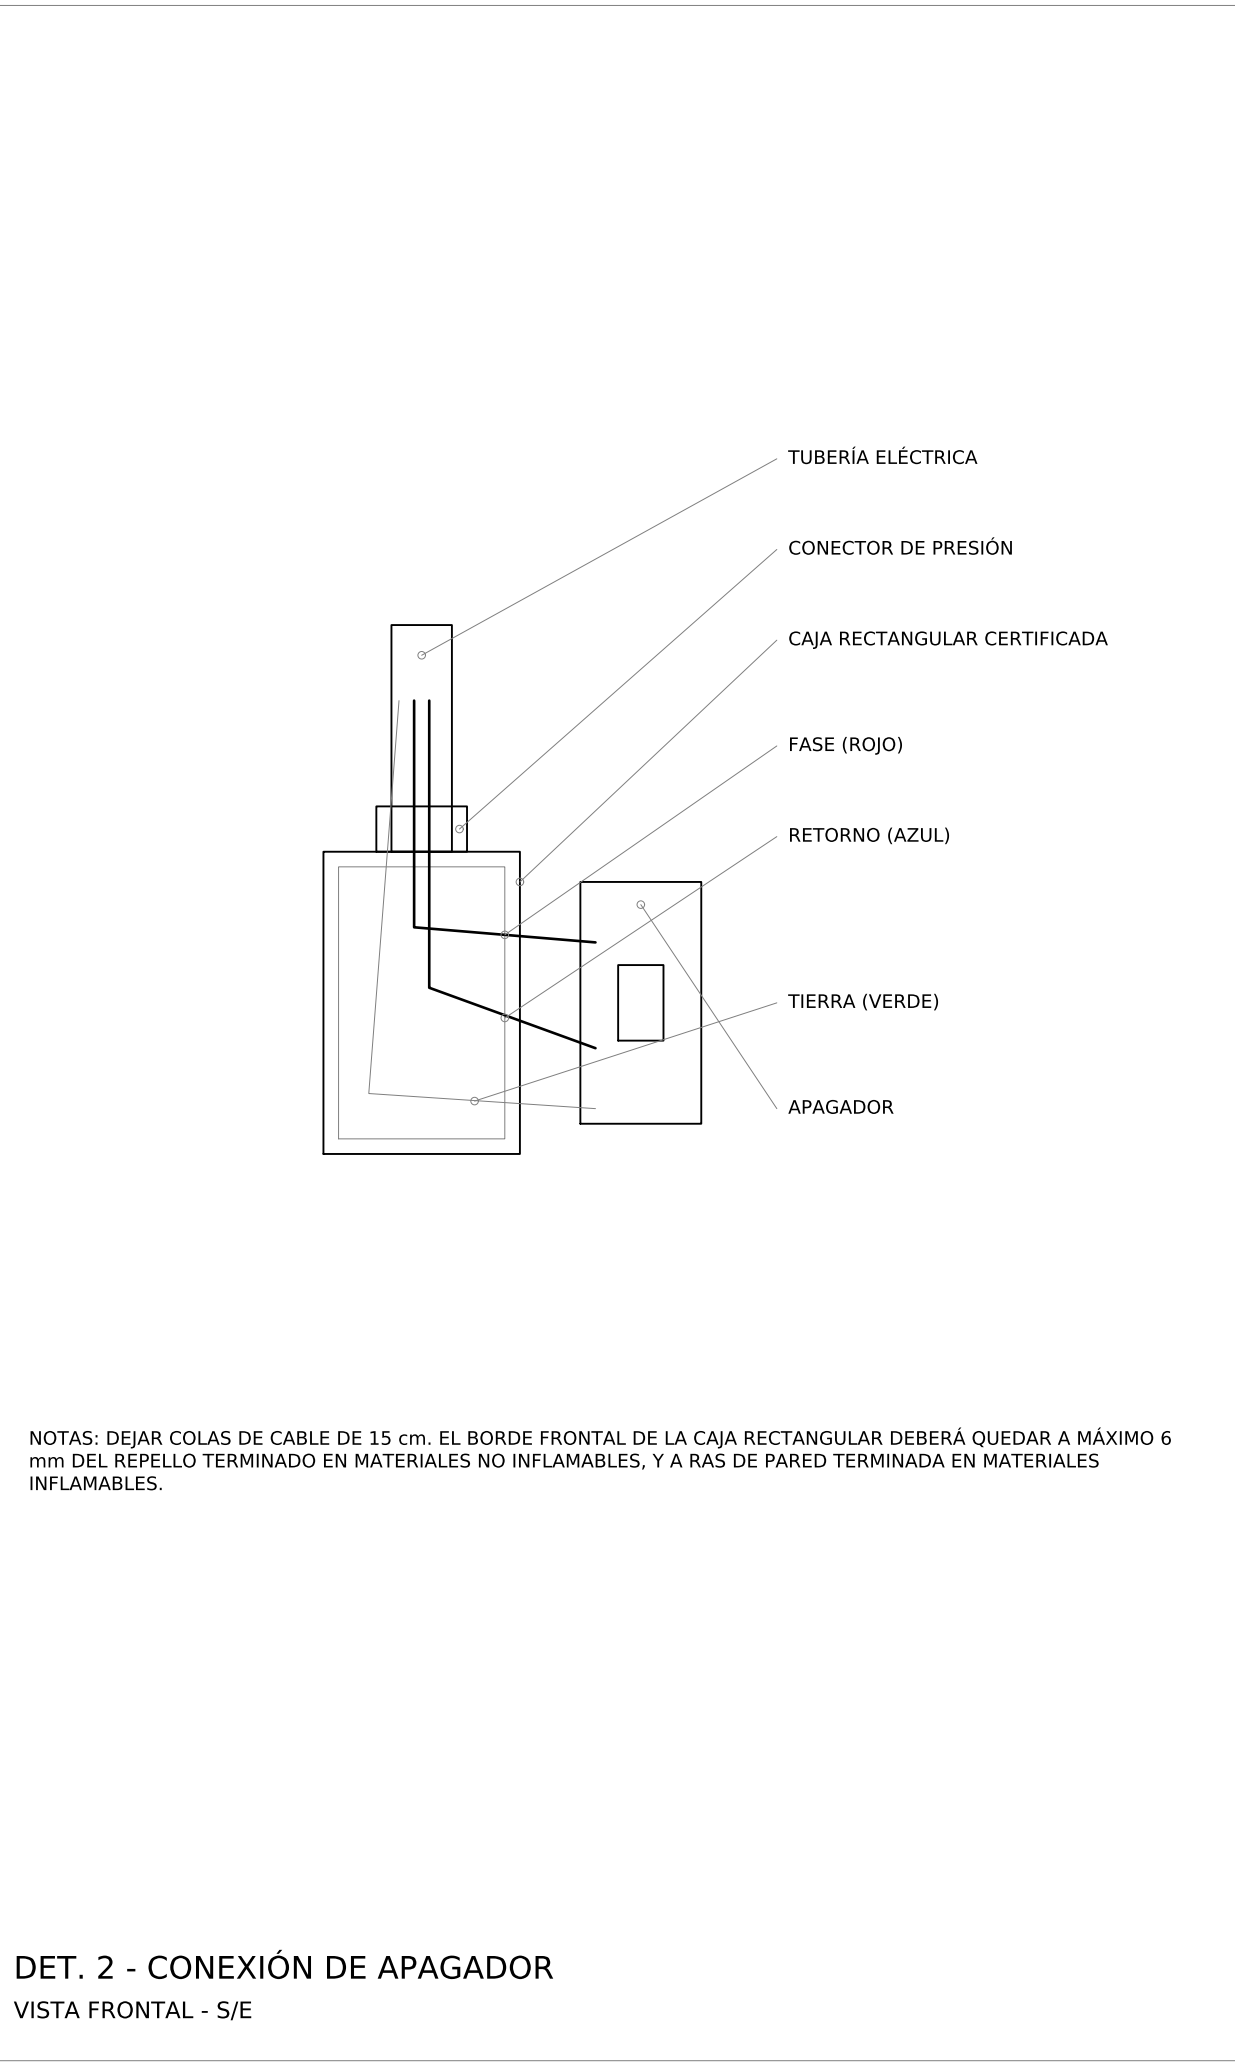


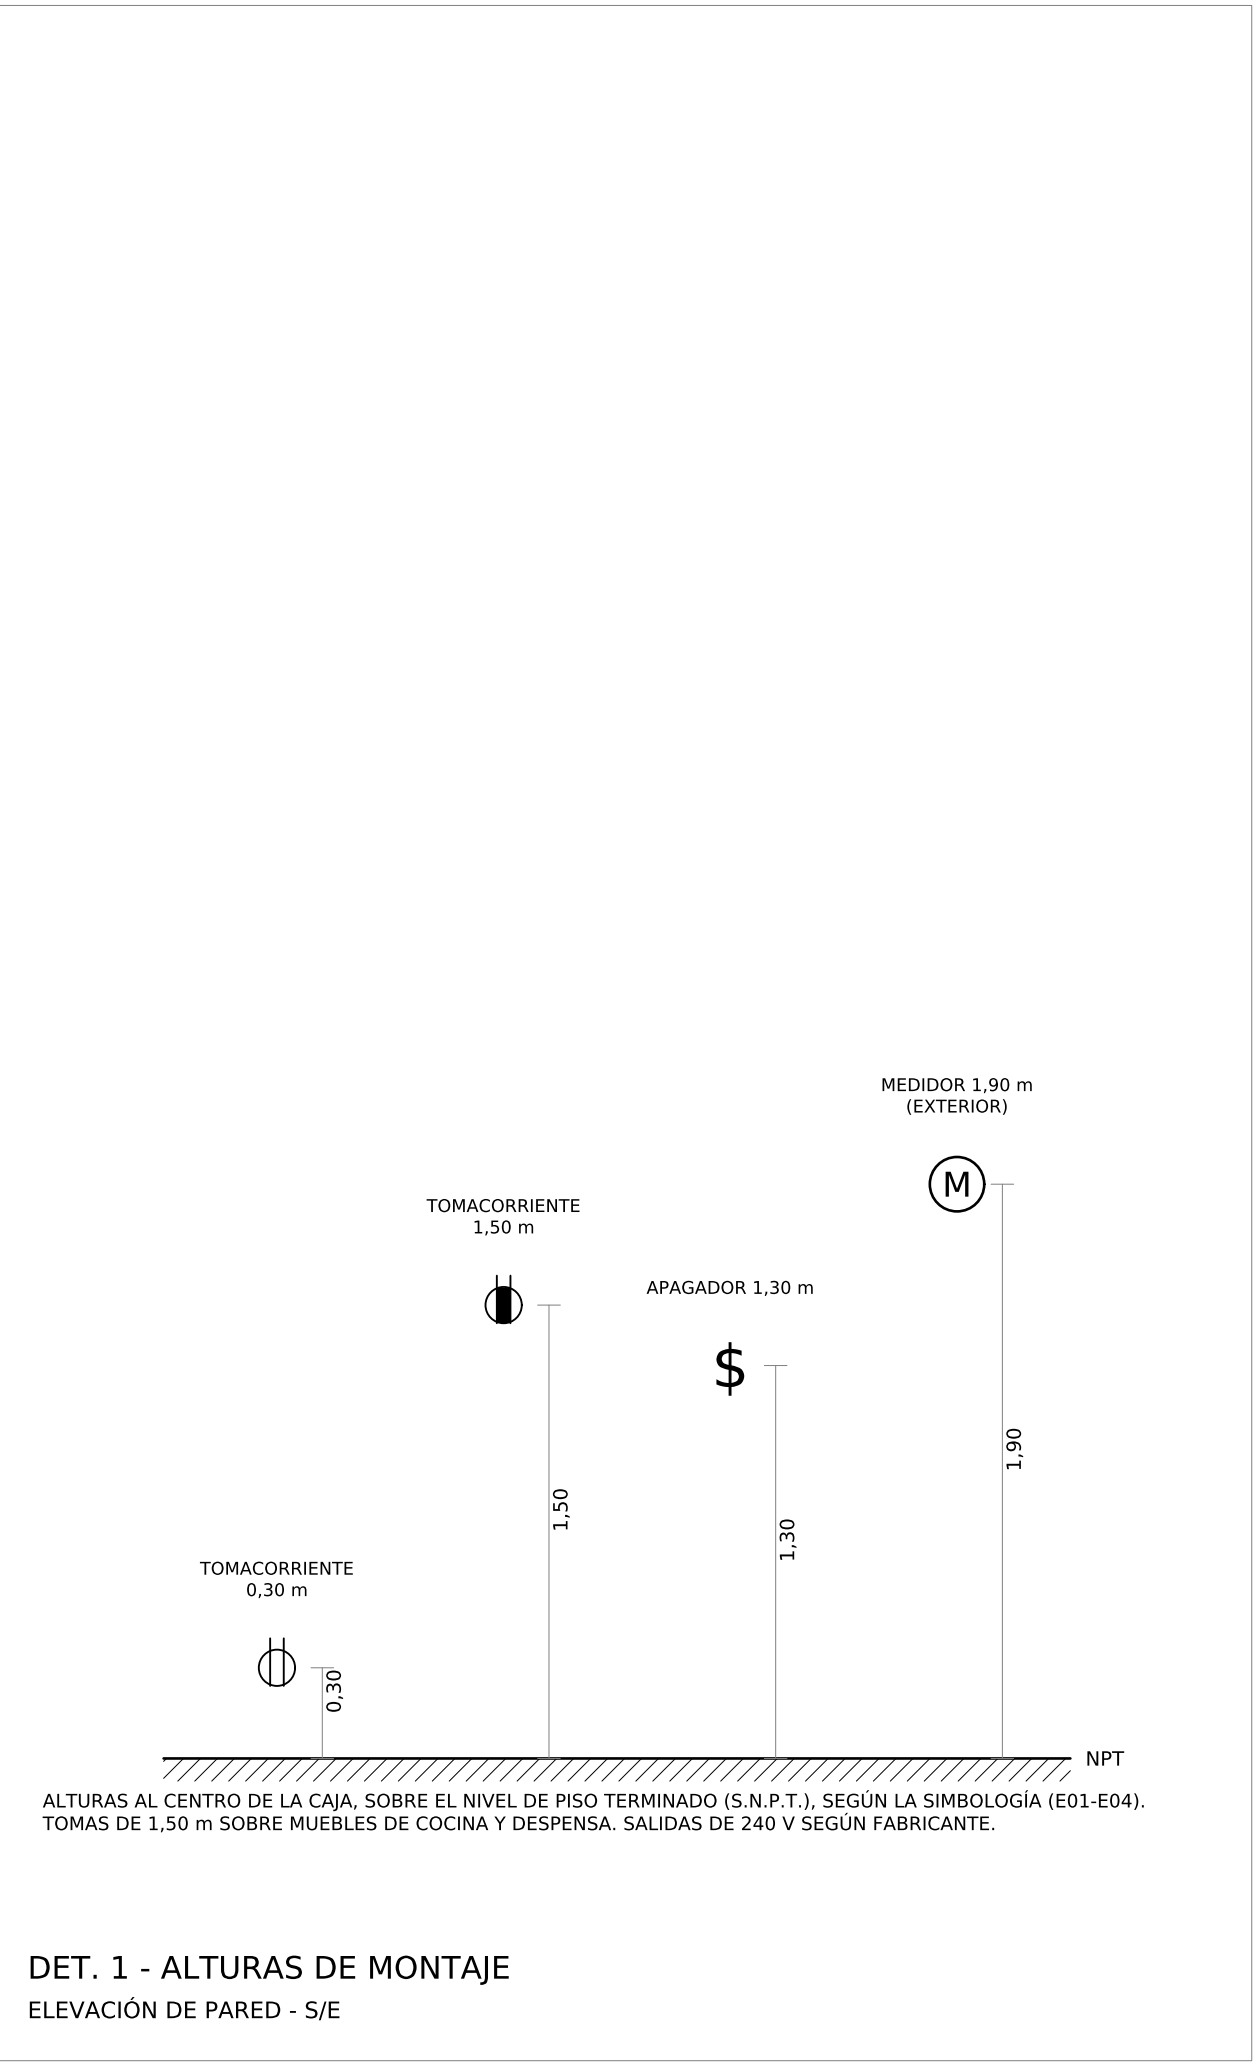

ESPACIO PARA SELLOS Y TIMBRES

CivilCon Diseño y Construcción SRLTDA
Céd. Jurídica: 3-102-762712

PROFESIONAL RESPONSABLE:
DIRECTOR TÉCNICO:
Steven Viales (Civil) IC-40759
David Barrantes (Electricidad) IE-27499

PROYECTO:
VIVIENDA UNIFAMILIAR
DISTRITO 03 SANTIAGO, CANTÓN 05 SAN RAFAEL,
PROVINCIA 04 HEREDIA, COSTA RICA.

INFORMACIÓN REGISTRO PÚBLICO:
FOLIO REAL: 4-041200-000
PLANO CATASTRADO: 4-57389-2023
ÁREA SEGÚN CATASTRO: 256 m²

CONTENIDO:
ELECTRICIDAD
DETALLES ELÉCTRICOS.
CONEXIONES Y ACCESORIOS.
ALTURAS DE MONTAJE.
ZANJA DE ACOMETIDA.
PUESTA A TIERRA.

ESCALAS: S/E

CONTROL DE REVISIONES		
REV.	FECHA	DESCRIPCIÓN
0	06-10-2026	VERSIÓN DE TRABAJO PARA REVISIÓN
1	07-10-2026	LISTA DEFINITIVA (22); PARA TRÁMITE

ESTADO:

PARA TRÁMITE CFIA Y MUNICIPALIDAD	
LUGAR	LÁMINA
COSTA RICA	E05
OCT 2026	TOTAL 22