




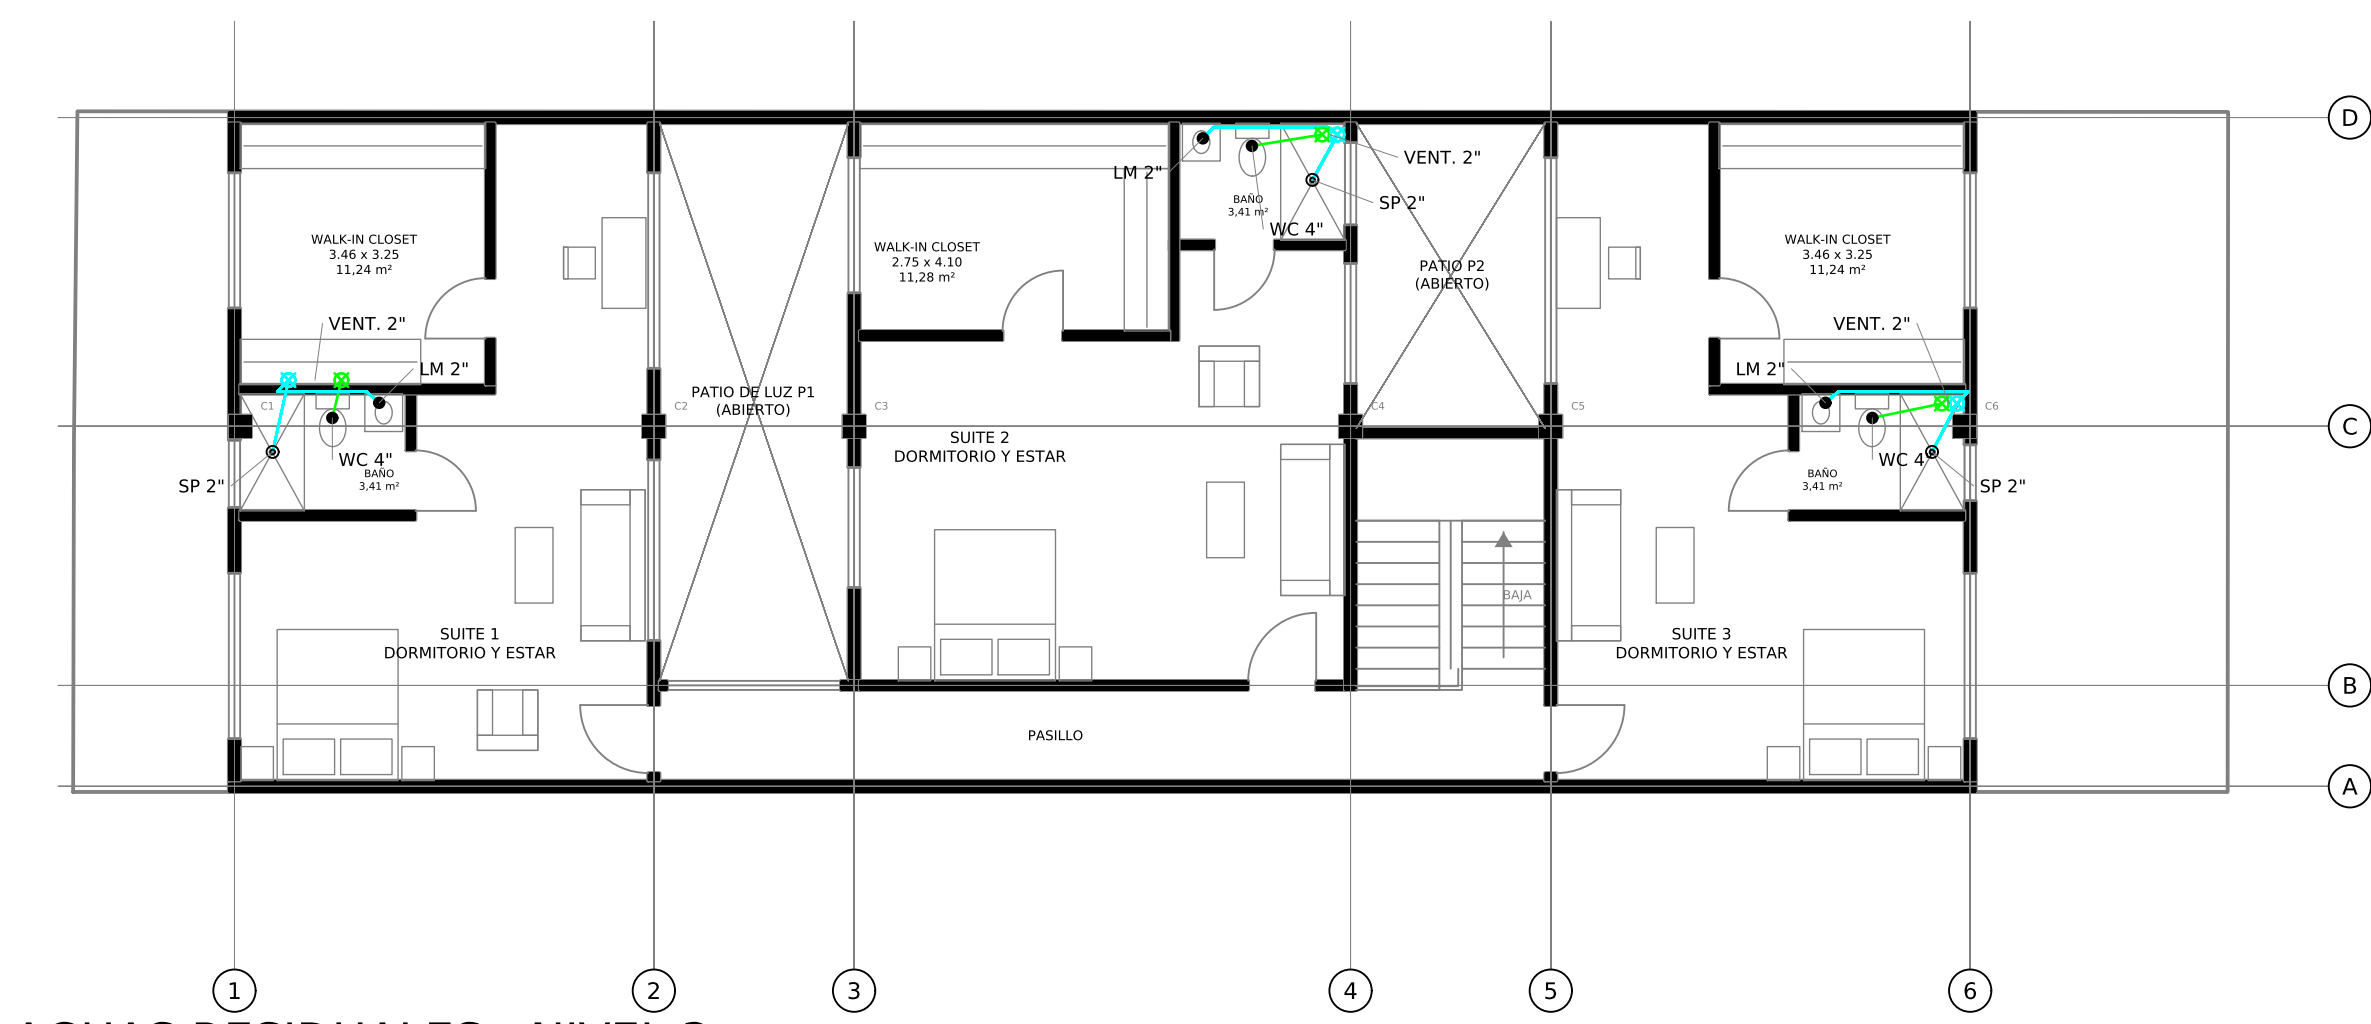

AGUAS RESIDUALES - NIVEL 3
Esc. 1:100

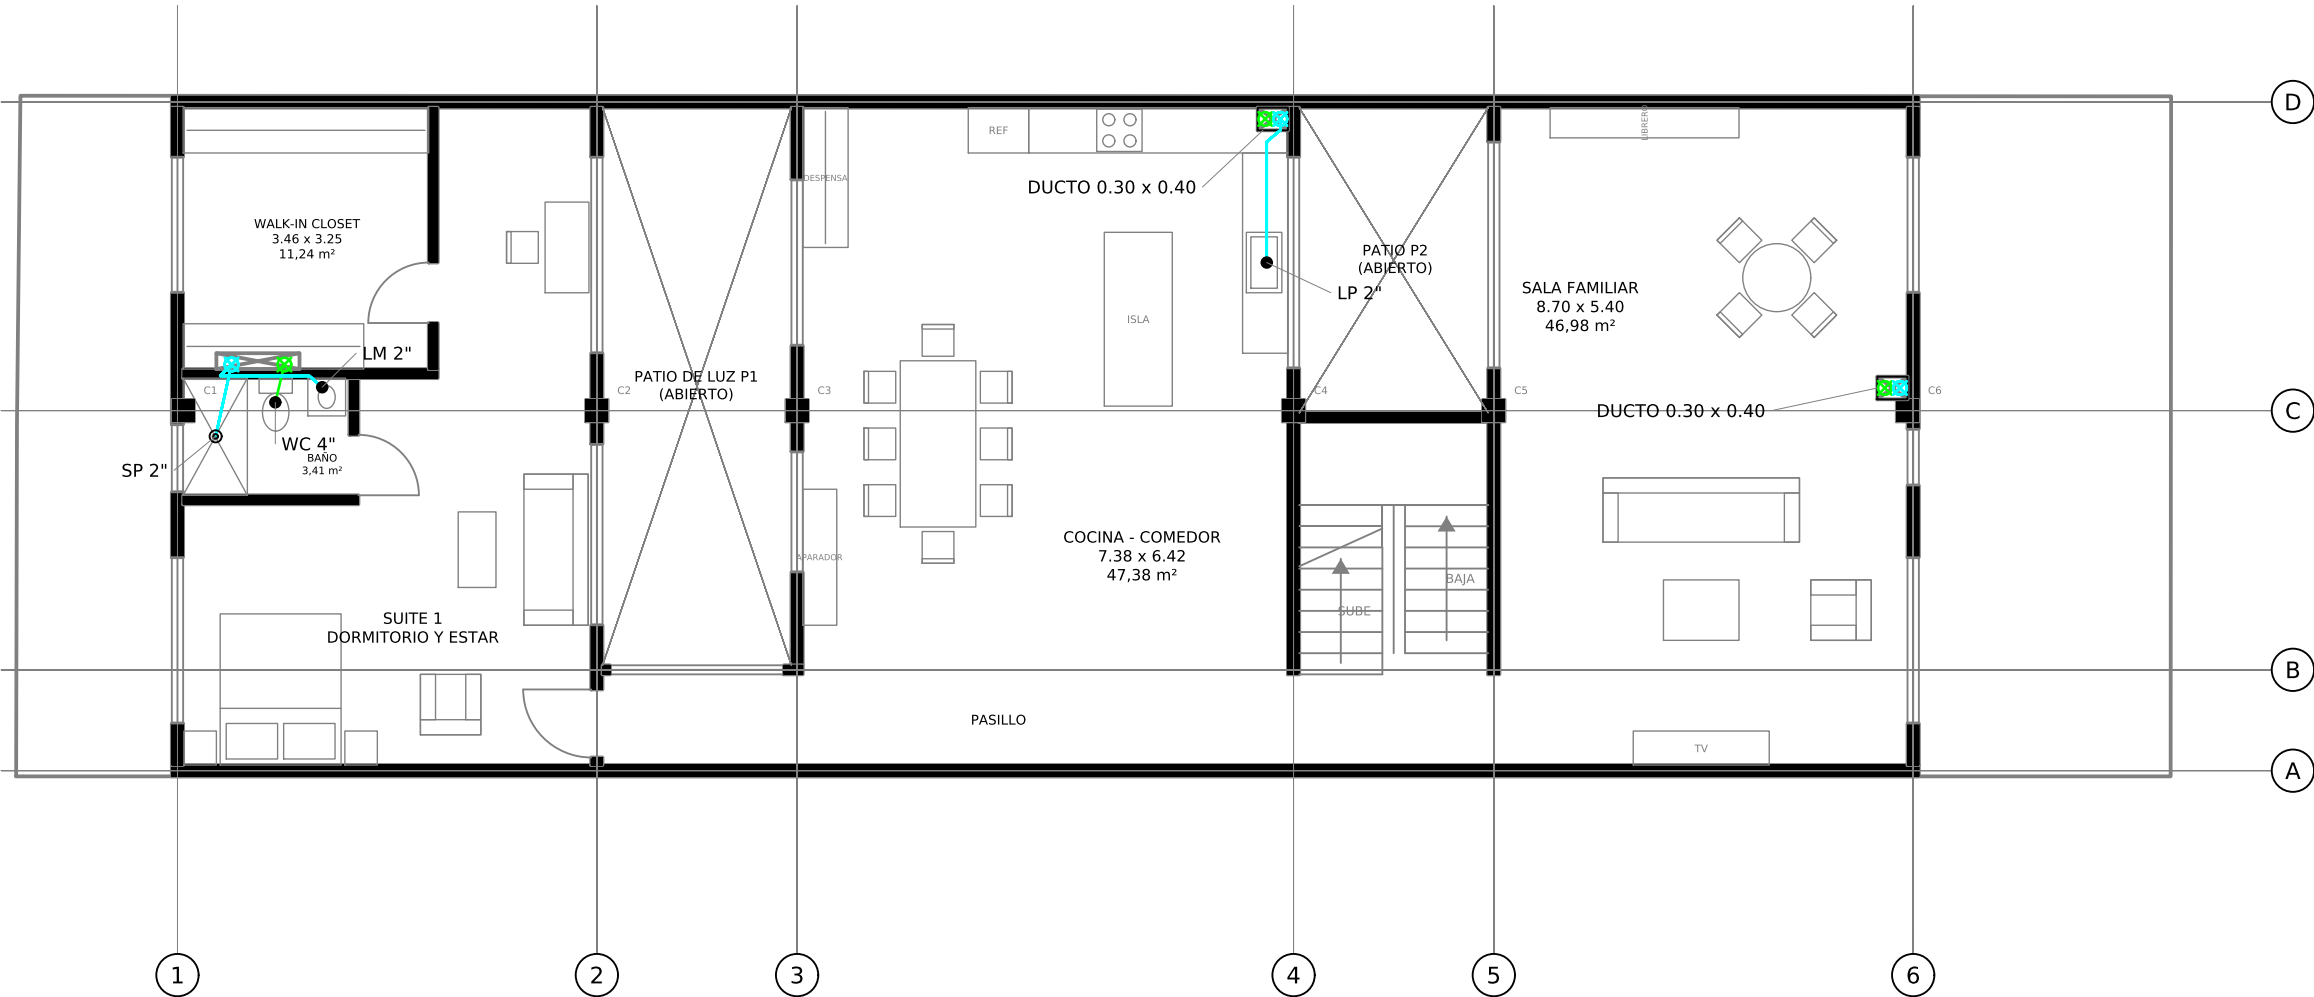


AGUAS RESIDUALES - NIVEL 2
Esc. 1:100

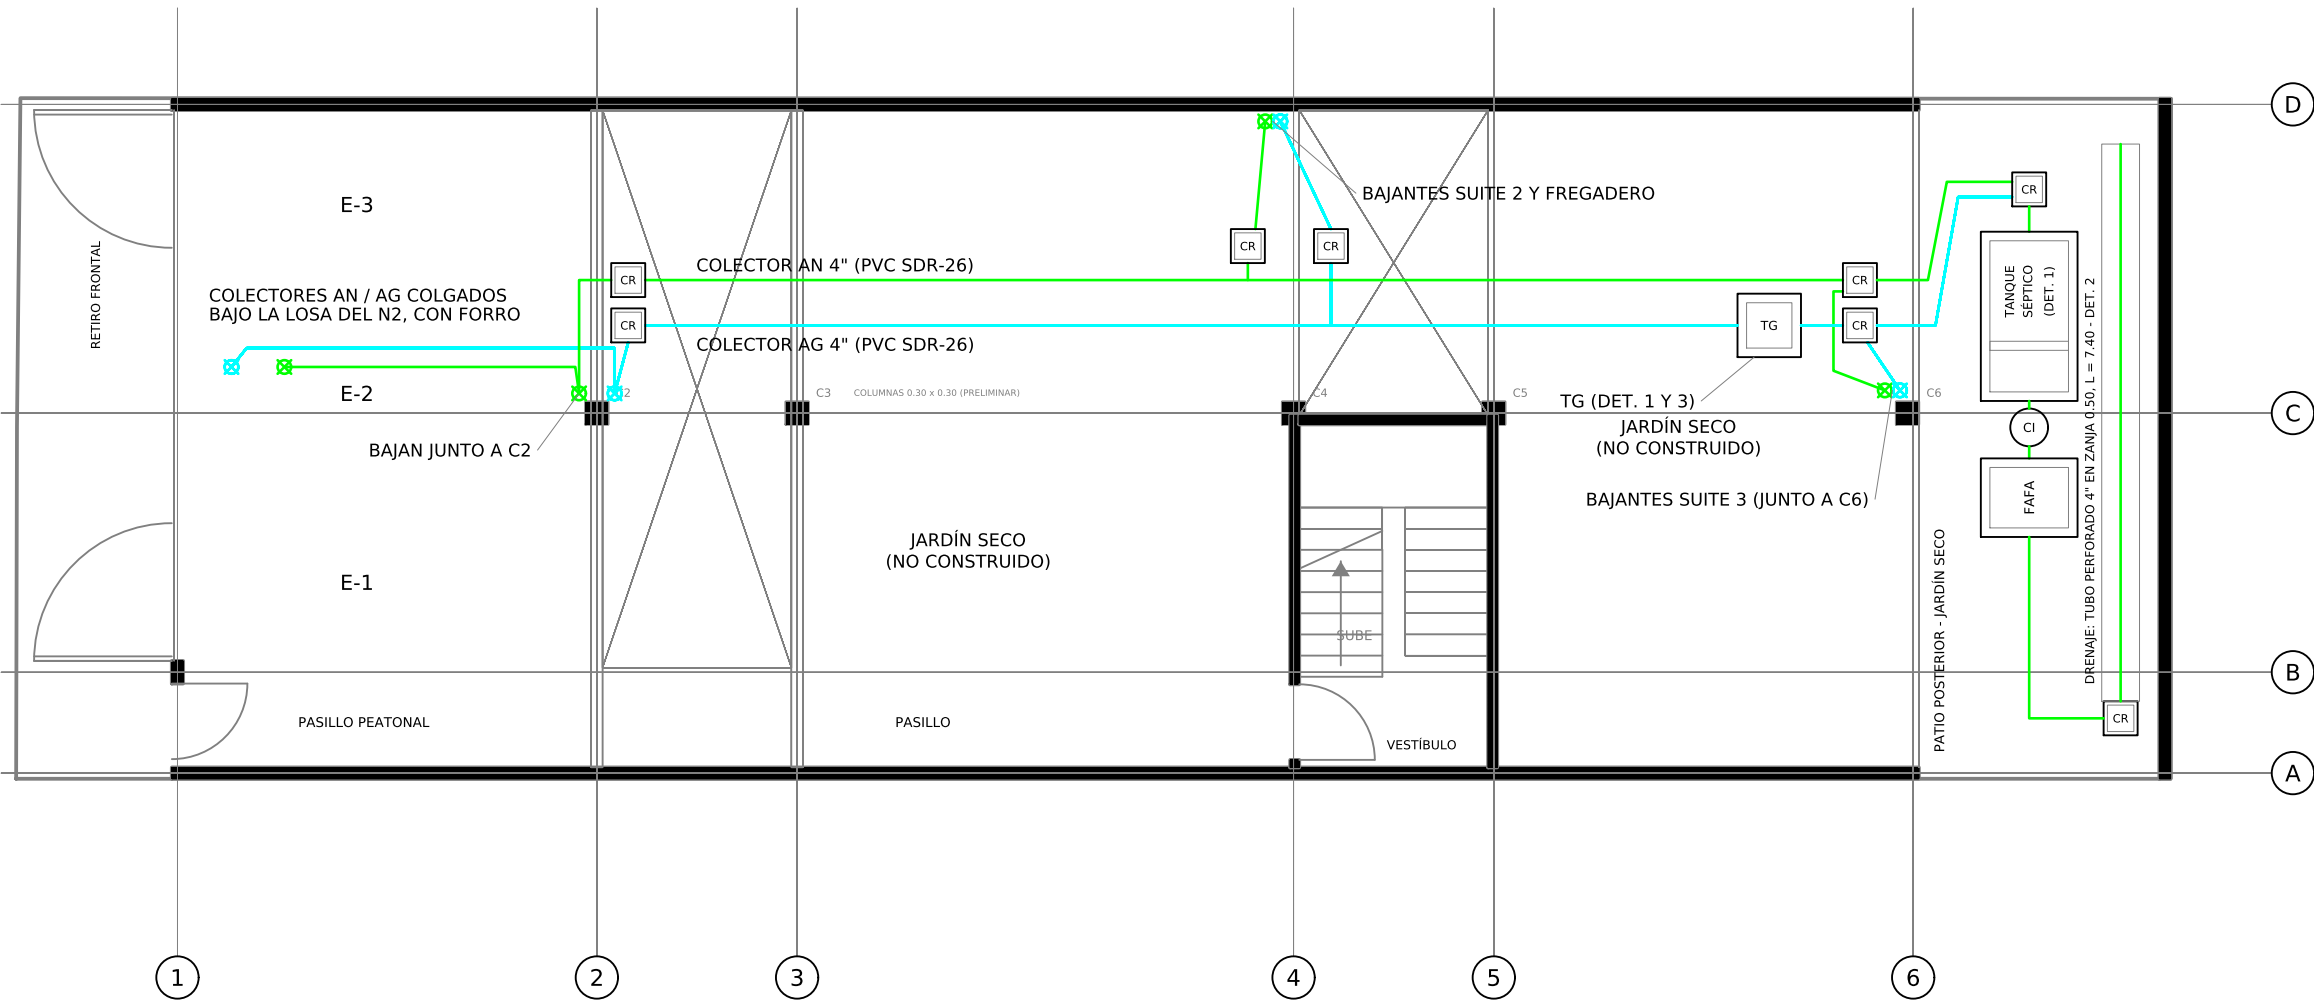


AGUAS RESIDUALES - NIVEL 1
Esc. 1:100

DETALLE 1 - TANQUE SÉPTICO
Esc. 1:30 - COTAS EN METROS

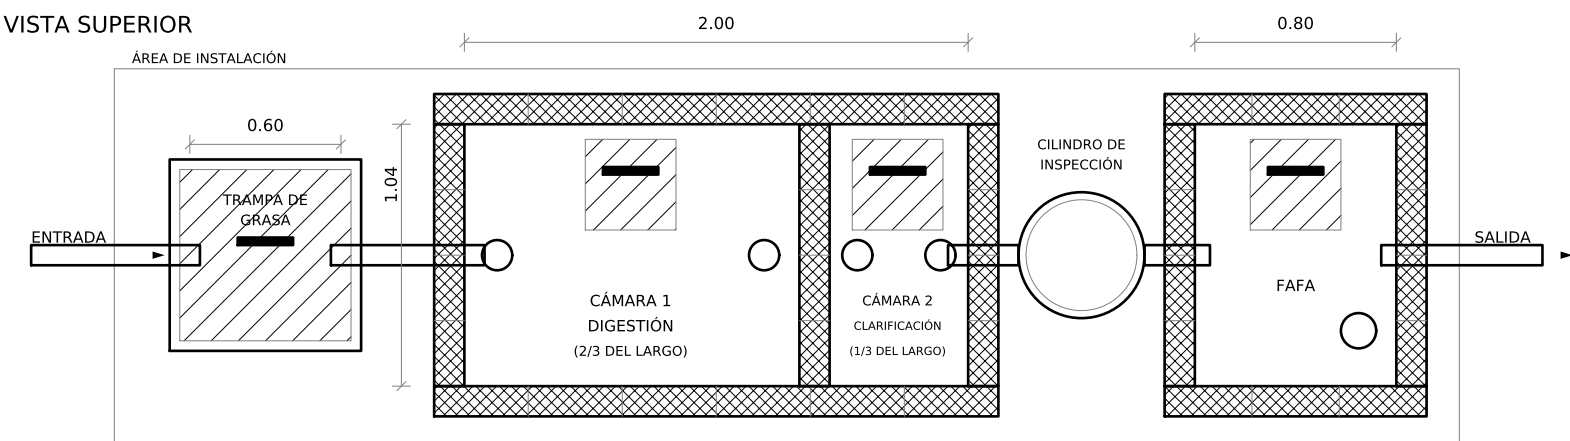


VISTA LATERAL

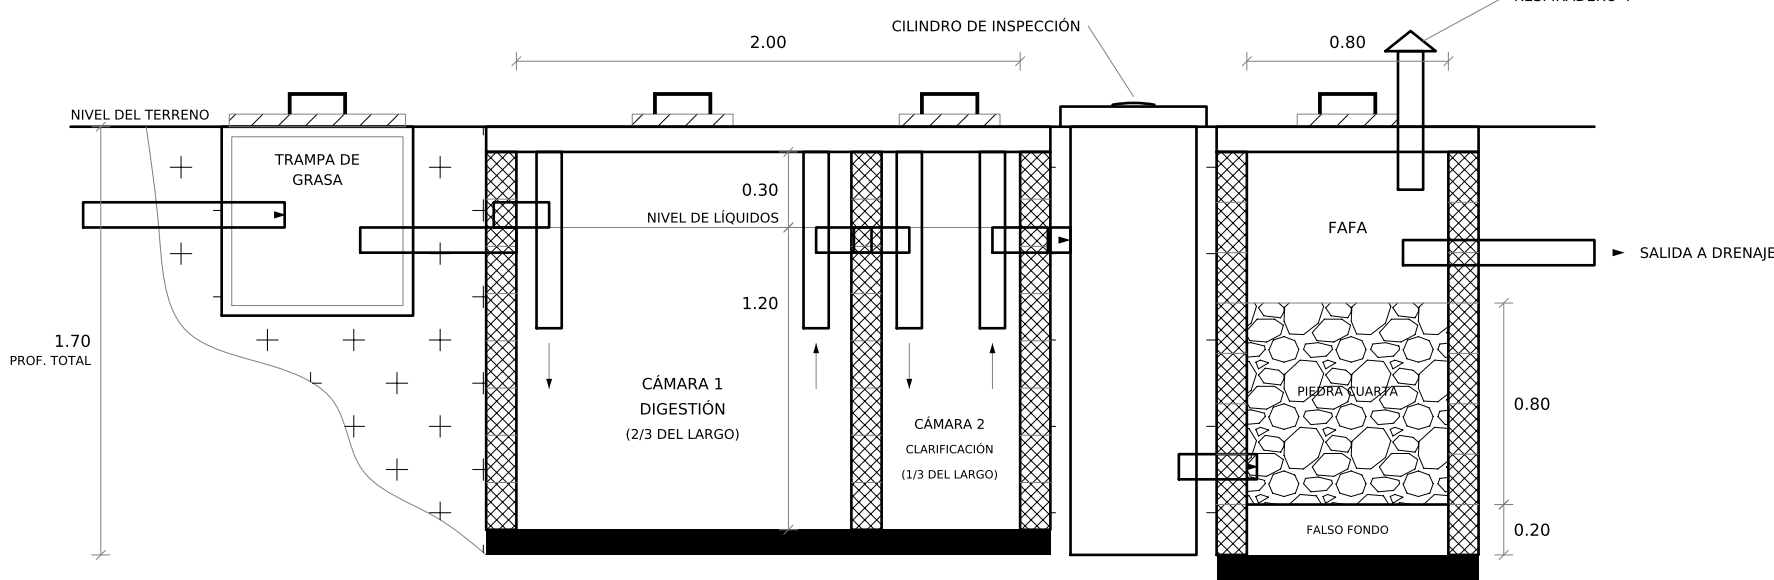


ESQUEMA: LA TRAMPA DE GRASA SE UBICA EN EL COLECTOR AG Y LAS AGUAS NEGRAS ENTRAN POR LA CR DE ENTRADA (VER PLANTA N1).


DETALLE 3 - CAJA DE REGISTRO Y TRAMPA DE GRASA
SECCIONES - S/E

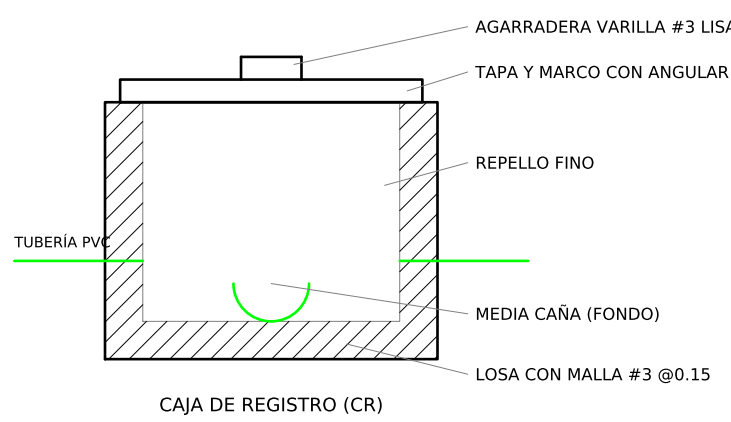

DETALLE 4 - BAÑO TÍPICO
SUITE 1 (N2 Y N3), SUITE 3 EN ESPEJO - Esc. 1:40

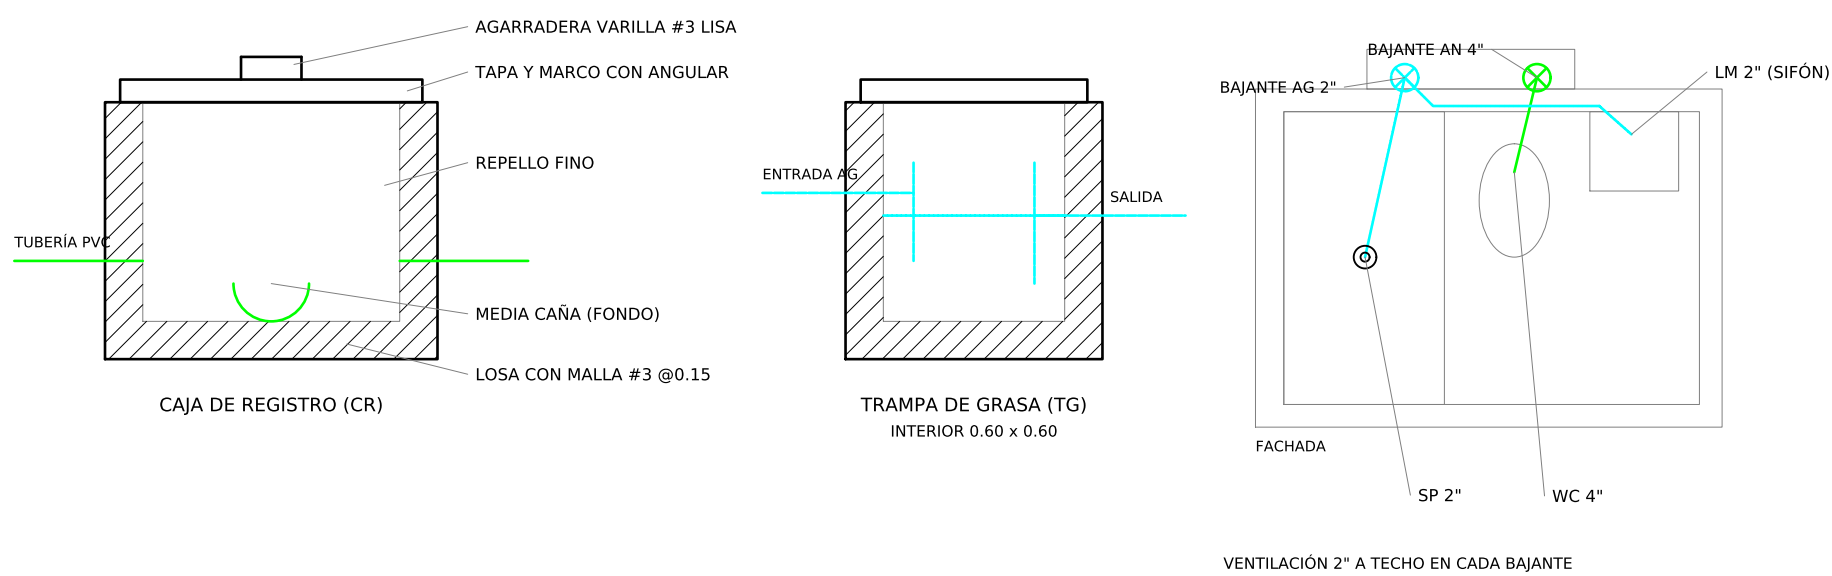

DETALLE 2 - SECCIÓN DE DRENAJE
Esc. 1:10

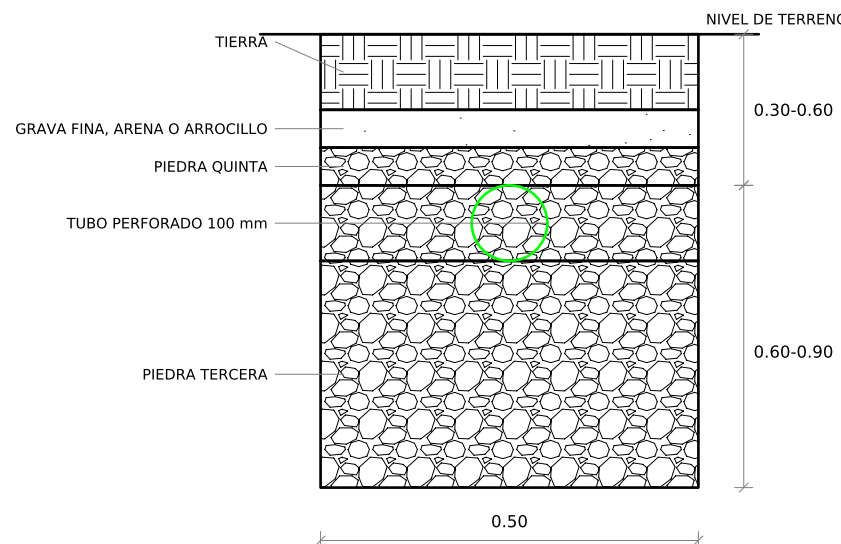

SIMBOLOGÍA

	AGUAS NEGRAS (PVC)
	AGUAS GRISES (PVC)
	BAJANTE DE AGUAS NEGRAS 4"
	BAJANTE DE AGUAS GRISES 2"
	SIFÓN DE PISO (DUCHA) 2"
	SALIDA DE APARATO (WC / LM / LP)
	CAJA DE REGISTRO (DET. 3)
	DRENAJE EN ZANJA (DET. 2)

AN / AG: AGUAS NEGRAS / GRISES; TG: TRAMPA DE GRASA; FAFA: FILTRO ANAEROBIO DE FLUJO ASCENDENTE.

NOTAS:

- 1.- TODAS LAS MEDIDAS ESTÁN DADAS EN METROS; LAS DIMENSIONES DEL TANQUE Y DEL FAFA SON INTERIORES, SALVO INDICACIÓN CONTRARIA.
- 2.- VERIFICAR EN SITIO LA UBICACIÓN, LOS NIVELES Y LAS CONDICIONES DEL TERRENO ANTES DE INICIAR LA CONSTRUCCIÓN.
- 3.- NO HAY ALCANTARILLADO SANITARIO: LAS AGUAS RESIDUALES SE TRATAN EN TANQUE SÉPTICO CON FAFA Y SE DISPONEN EN EL DRENAJE DEL PATIO POSTERIOR.
- 4.- AGUAS NEGRAS (INODOROS) EN 4" Y AGUAS GRISES (LAVATORIOS, DUCHAS Y FREGADERO) EN 2", CON BAJANTES Y CAJAS DE REGISTRO SEPARADAS.
- 5.- TUBERÍA ENTERRADA EN PVC SDR-26 O SUPERIOR, DIÁMETRO MÍNIMO 100 MM (4"). ACCESORIOS SANITARIOS EN TODOS LOS CAMBIOS DE DIRECCIÓN.
- 6.- LAS AGUAS GRISES PASAN POR LA TRAMPA DE GRASA Y SE UNEN A LAS AGUAS NEGRAS EN LA CAJA DE REGISTRO DE ENTRADA AL TANQUE.
- 7.- BAJANTES: SUITE 1 EN FORRO DEL MURO BAÑO / WALK-IN, CON COLECTORES COLGADOS BAJO LA LOSA DEL N2 HASTA C2; SUITE 2 Y FREGADERO EN DUCTO DE LA COCINA (ESQUINA D/4); SUITE 3 EN DUCTO JUNTO A C6 EN LA SALA. DUCTOS DE 0.30 x 0.40 Y FORRO DE 0.20.
- 8.- CADA BAJANTE SE PROLONGA COMO VENTILACIÓN DE 2" SOBRE LA CUBIERTA.
- 9.- LAS TUBERÍAS PASAN SOBRE LAS PLACAS DE CIMENTACIÓN SIN ATRAVESAR PEDESTALES; CRUCES CON VIGAS RIOSTRA CON CAMISA. EL TANQUE Y LAS CAJAS SE UBICAN FUERA DE LAS PLACAS (VER C01).
- 10.- TANQUE Y FAFA: CONCRETO DE 210 KG/CM2; LOSAS INFERIOR Y SUPERIOR DE 0.10 M MÍNIMO CON MALLA #3 @20 CM; MUROS DE BLOQUE 12x20x40 CON JUNTAS LLENAS Y REPELLO IMPERMEABLE INTERIOR; REFUERZO VERTICAL #3 @40 CM Y HORIZONTAL #3 CADA DOS HILADAS; RECUBRIMIENTO 4 CM; CURADO 7 DÍAS.
- 11.- CÁMARA 1 (DIGESTIÓN) = 2/3 Y CÁMARA 2 (CLARIFICACIÓN) = 1/3 DEL LARGO. TEES SANITARIAS DE PVC 100 MM, 0.30 M SOBRE Y 0.40 M BAJO EL NIVEL DE LÍQUIDOS. BORDE LIBRE 0.30 M Y PROFUNDIDAD ÚTIL 1.20 M.
- 12.- FAFA: 1.04 x 0.80 M INTERIOR, PROFUNDIDAD ÚTIL 1.20 M, FALSO FONDO A 0.20 M CON LOSA PERFORADA, MEDIO FILTRANTE DE PIEDRA CUARTA LAVADA (5-7 CM) DE 0.80 M SIN COMPACTAR Y ESPACIO LIBRE SUPERIOR DE 0.20 M.
- 13.- RESPIRADORES DE PVC 100 MM, 0.30 M SOBRE EL TERRENO, CON SOMBRERETE. CILINDRO DE INSPECCIÓN DE CONCRETO, DIÁMETRO INTERIOR MÍNIMO 0.30 M. TAPAS DE CONCRETO REFORZADO DE 0.60 x 0.60 M MÍNIMO, CON AGARRADERAS.
- 14.- DRENAJE: TUBO PERFORADO DE 100 MM EN ZANJA DE 0.50 M (DETALLE 2). LONGITUD 7.40 M.
- 15.- NO RELLENAR HASTA QUE EL CONCRETO ALCANZE SU RESISTENCIA; COMPACTAR EN CAPAS DE 20 CM MÁXIMO Y EVITAR EL PASO DE VEHÍCULOS SOBRE EL SISTEMA.
- 16.- ANTES DEL RELLENO, VERIFICAR LA ESTANQUEIDAD DEL TANQUE Y DEL FAFA; LIMPIAR EL SISTEMA ANTES DE COLOCAR EL MEDIO FILTRANTE Y LLENAR EL FAFA CON AGUA ANTES DE INICIAR LA OPERACIÓN.
- 17.- MANTENIMIENTO: RETIRAR LOS LODOS DEL TANQUE CUANDO OCUPEN APROXIMADAMENTE 1/3 DEL VOLUMEN DE LA PRIMERA CÁMARA.
- 18.- NO SE PERMITE MODIFICAR DIMENSIONES, NIVELES, DIÁMETROS NI MATERIALES SIN AUTORIZACIÓN DEL PROFESIONAL RESPONSABLE.

ESPACIO PARA SELLOS Y TIMBRES

CivilCon Diseño y Construcción SRLTDA
Céd. Jurídica: 3-102-762712

PROFESIONAL RESPONSABLE:
DIRECTOR TÉCNICO:
Steven Viales (Civil) IC-40759
David Barrantes (Electricidad) IE-27499

PROYECTO:
VIVIENDA UNIFAMILIAR
DISTRITO 03 SANTIAGO, CANTÓN 05 SAN RAFAEL,
PROVINCIA 04 HEREDIA, COSTA RICA.

INFORMACIÓN REGISTRO PÚBLICO:
FOLIO REAL: 4-041200-000
PLANO CATASTRADO: 4-57389-2023
ÁREA SEGÚN CATASTRO: 256 m²

CONTENIDO:
AGUAS RESIDUALES
PLANTAS NIVELES 1, 2 Y 3.
TANQUE SÉPTICO, FAFA Y DRENAJE.
CAJA DE REGISTRO,
TRAMPA DE GRASA Y BAÑO TÍPICO.
SIMBOLOGÍA Y NOTAS.

ESCALAS: 1:100 / INDICADAS

CONTROL DE REVISIONES		
REV.	FECHA	DESCRIPCIÓN
0	06-10-2026	VERSIÓN DE TRABAJO PARA REVISIÓN
1	07-10-2026	DETALLE DE TANQUE SEGÚN LA REFERENCIA
2	07-10-2026	LISTA DEFINITIVA (22); PARA TRÁMITE

ESTADO:
PARA TRÁMITE
CFIA Y MUNICIPALIDAD

LUGAR	LÁMINA
COSTA RICA	S02
OCT 2026	TOTAL 22