


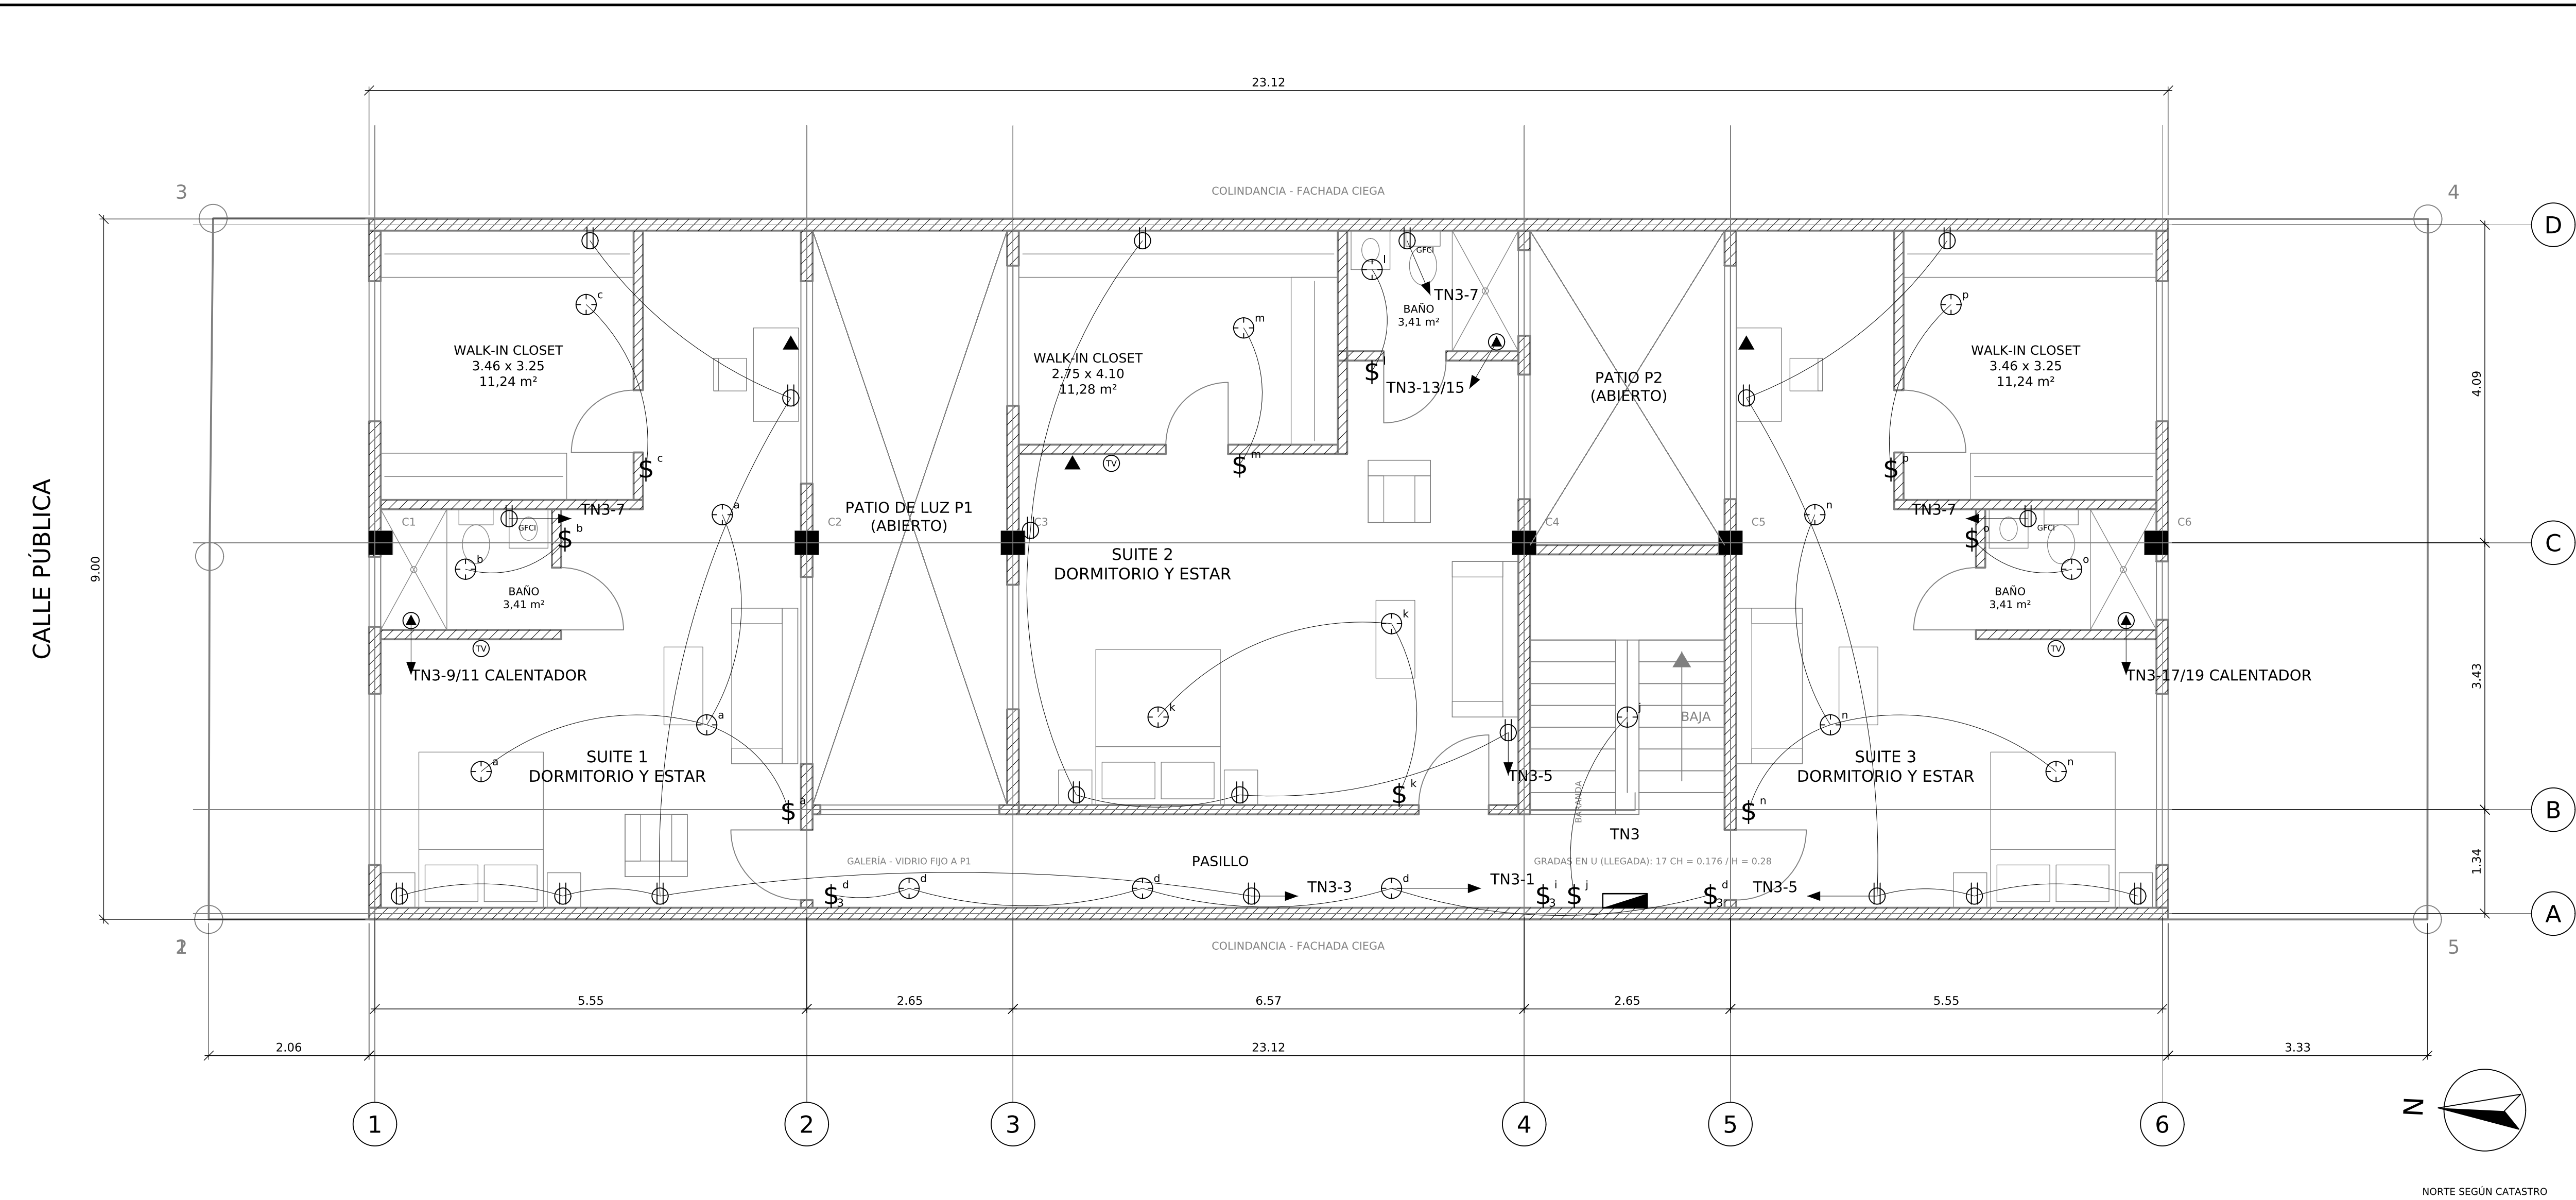

PLANTA ELÉCTRICA NIVEL 3
ILUMINACIÓN, TOMACORRIENTES Y VOZ/DATOS
Esc. 1:50



SIMBOLOGÍA ELÉCTRICA

	MEDIDOR ELÉCTRICO A 1,90 m S.N.P.T. [PR]
	TABLERO DE DISTRIBUCIÓN ELÉCTRICA
	TABLERO DE DISTRIBUCIÓN DE VOZ Y DATOS
	LUMINARIA EN SUPERFICIE DE CIELO
	LUMINARIA EMPOTRADA EN CIELO DE GYPSUM
	LUMINARIA EN PARED (APLIQUE)
	APAGADOR SENCILLO 15 A, 120 V, A 1,30 m S.N.P.T. [PR]
	APAGADOR DE TRES VÍAS 20 A, 120 V, A 1,30 m S.N.P.T. [PR]
	TOMACORRIENTE DOBLE POLARIZADO 120 V, 20 A, A 0,30 m S.N.P.T. [PR]
	TOMACORRIENTE DOBLE POLARIZADO 120 V, 20 A, A 1,50 m S.N.P.T. [PR]
	TOMACORRIENTE DOBLE 120 V, 20 A, CON PROTECCIÓN GFCI [PR]
	SALIDA ESPECIAL 240 V (VER CUADRO DE TABLEROS, E04)
	SALIDA DE TELEVISIÓN
	SALIDA DE VOZ Y DATOS

CIRCUITOS DEL NIVEL 3 (SUBTABLERO TN3)

CIRC.	DESCRIPCIÓN	DISYUNTOR	CONDUCTORES THHN [PR]
TN3-1	ILUMINACIÓN NIVEL 3 (a-p)	1P-20 A	2 #12 + #12 T
TN3-3	TOMAS GENERALES SUITE 1 Y PASILLO	1P-20 A	2 #12 + #12 T
TN3-5	TOMAS GENERALES SUITES 2 Y 3	1P-20 A	2 #12 + #12 T
TN3-7	TOMAS DE BAÑOS (GFCI)	1P-20 A	2 #12 + #12 T
TN3-9/11	CALENTADOR DE PASO BAÑO SUITE 1, 240 V	2P-40 A	2 #10 + #10 T
TN3-13/15	CALENTADOR DE PASO BAÑO SUITE 2, 240 V	2P-40 A	2 #10 + #10 T
TN3-17/19	CALENTADOR DE PASO BAÑO SUITE 3, 240 V	2P-40 A	2 #10 + #10 T

LETRAS a-p: AGRUPACIÓN DE LUMINARIAS POR APAGADOR. CARGAS, CAÍDAS DE TENSIÓN Y ALIMENTADOR DEL TN3: VER E04.

NOTAS:

- 1.- TODAS LAS MEDIDAS ESTÁN DADAS EN METROS. [PR]
 - 2.- LAS MEDIDAS DEBEN SER VERIFICADAS EN SITIO. [PR]
 - 3.- TODA LA INSTALACIÓN SE REALIZARÁ EN TUBERÍA SEGÚN SE INDICA EN EL TABLERO; EN NINGÚN CASO SE USARÁ TUBERÍA EXPUESTA (TUBERÍA SOBRE CIELO DE GYPSUM Y EN PAREDES). [PR]
 - 4.- TODAS LAS SALIDAS, TANTO ELÉCTRICAS COMO DE TV Y DATOS, SERÁN POR MEDIO DE CAJAS DE CONEXIÓN RECTANGULARES U OCTOGONALES CON SUS RESPECTIVAS TAPAS. [PR]
 - 5.- SE IDENTIFICARÁN EN EL TABLERO LOS DIFERENTES CIRCUITOS Y SE DEJARÁN AL MENOS DOS TUBOS PREVISTOS COMO ADICIONALES. [PR]
 - 6.- TOMACORRIENTES DE BAÑO CON PROTECCIÓN GFCI.
 - 7.- SALIDAS ESPECIALES 240 V: UN CALENTADOR DE PASO POR BAÑO; ALTURA Y CONEXIÓN SEGÚN EL FABRICANTE DEL EQUIPO.
 - 8.- GRADAS: EL S3 'I' CONTROLA, CON EL DEL NIVEL 2, LA LUZ DE GRADAS DEL NIVEL 2 (E02); LA LUZ 'J' ILUMINA LA LLEGADA AL NIVEL 3.
 - 9.- SALIDAS DE TV Y DATOS CON TUBERÍA INDEPENDIENTE DESDE EL PVD DEL NIVEL 1.
 - 10.- DIAGRAMA UNIFILAR, ALIMENTADOR DEL TN3, CUADROS DE TABLEROS, NOTAS GENERALES Y DETALLES EN LA LÁMINA E04.
- [PR] = NOTA TOMADA DEL PROYECTO DE REFERENCIA. PENDIENTE DE REVISIÓN.

ESPACIO PARA SELLOS Y TIMBRES

CivilCon Diseño y Construcción SRLTDA
Céd. Jurídica: 3-102-762712

PROFESIONAL RESPONSABLE:
DIRECTOR TÉCNICO:
Steven Viales (Civil) IC-40759
David Barrantes (Electricidad) IE-27499

PROYECTO:
VIVIENDA UNIFAMILIAR
DISTRITO 03 SANTIAGO, CANTÓN 05 SAN RAFAEL,
PROVINCIA 04 HEREDIA, COSTA RICA.

INFORMACIÓN REGISTRO PÚBLICO:
FOLIO REAL: 4-041200-000
PLANO CATASTRADO: 4-57389-2023
ÁREA SEGÚN CATASTRO: 256 m²

CONTENIDO:
ELECTRICIDAD
PLANTA ELÉCTRICA NIVEL 3.
ILUMINACIÓN Y TOMACORRIENTES.
VOZ Y DATOS.
SIMBOLOGÍA.
NOTAS.

ESCALAS: 1:50

CONTROL DE REVISIONES		
REV.	FECHA	DESCRIPCIÓN
0	06-10-2026	VERSIÓN DE TRABAJO PARA REVISIÓN

ESTADO:
VERSIÓN DE TRABAJO
NO APTA PARA CONSTRUCCIÓN NI TRÁMITE

LUGAR	LÁMINA
COSTA RICA	E03
OCT 2026	TOTAL --