




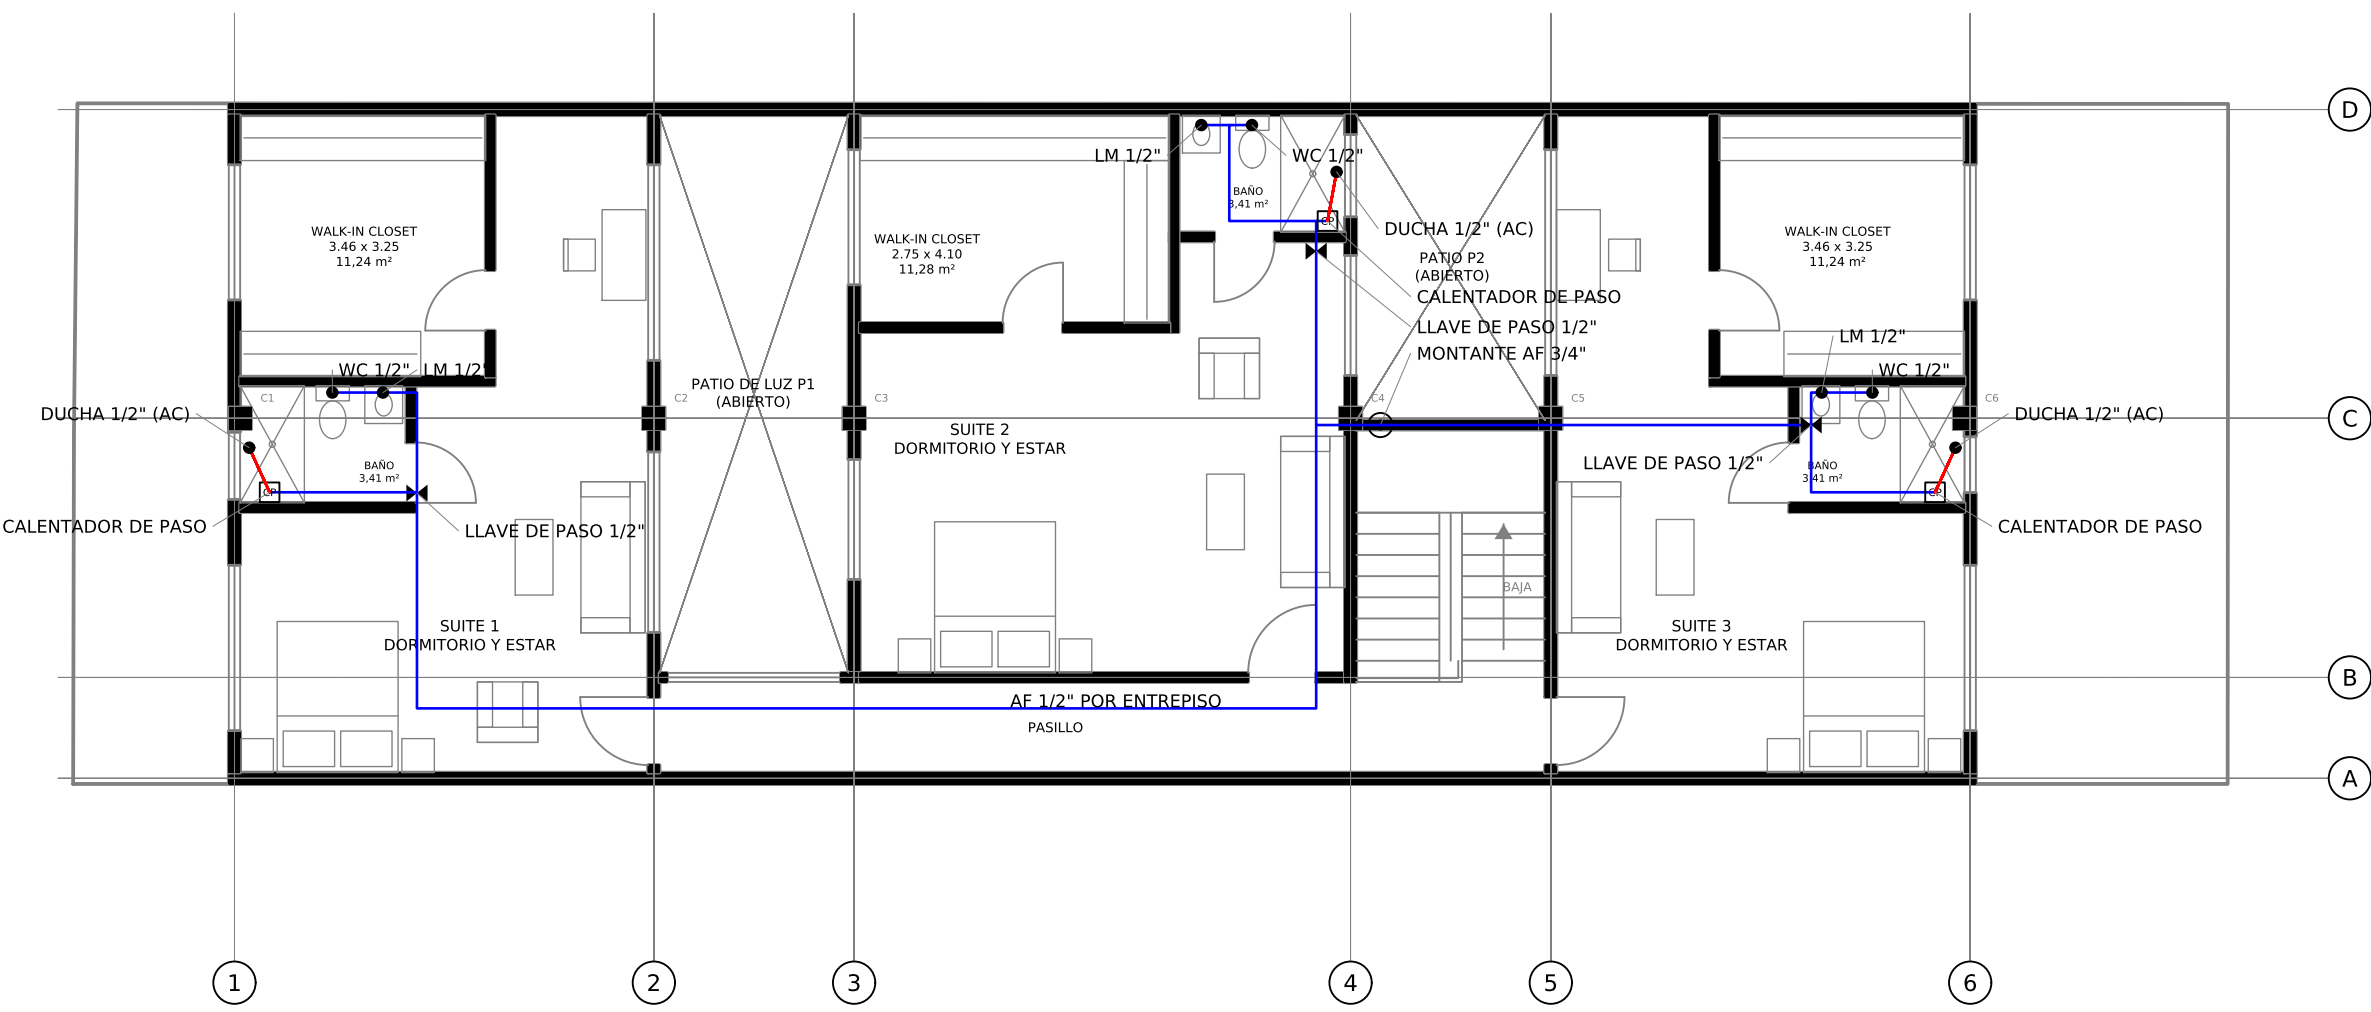

AGUA POTABLE - NIVEL 3
Esc. 1:100

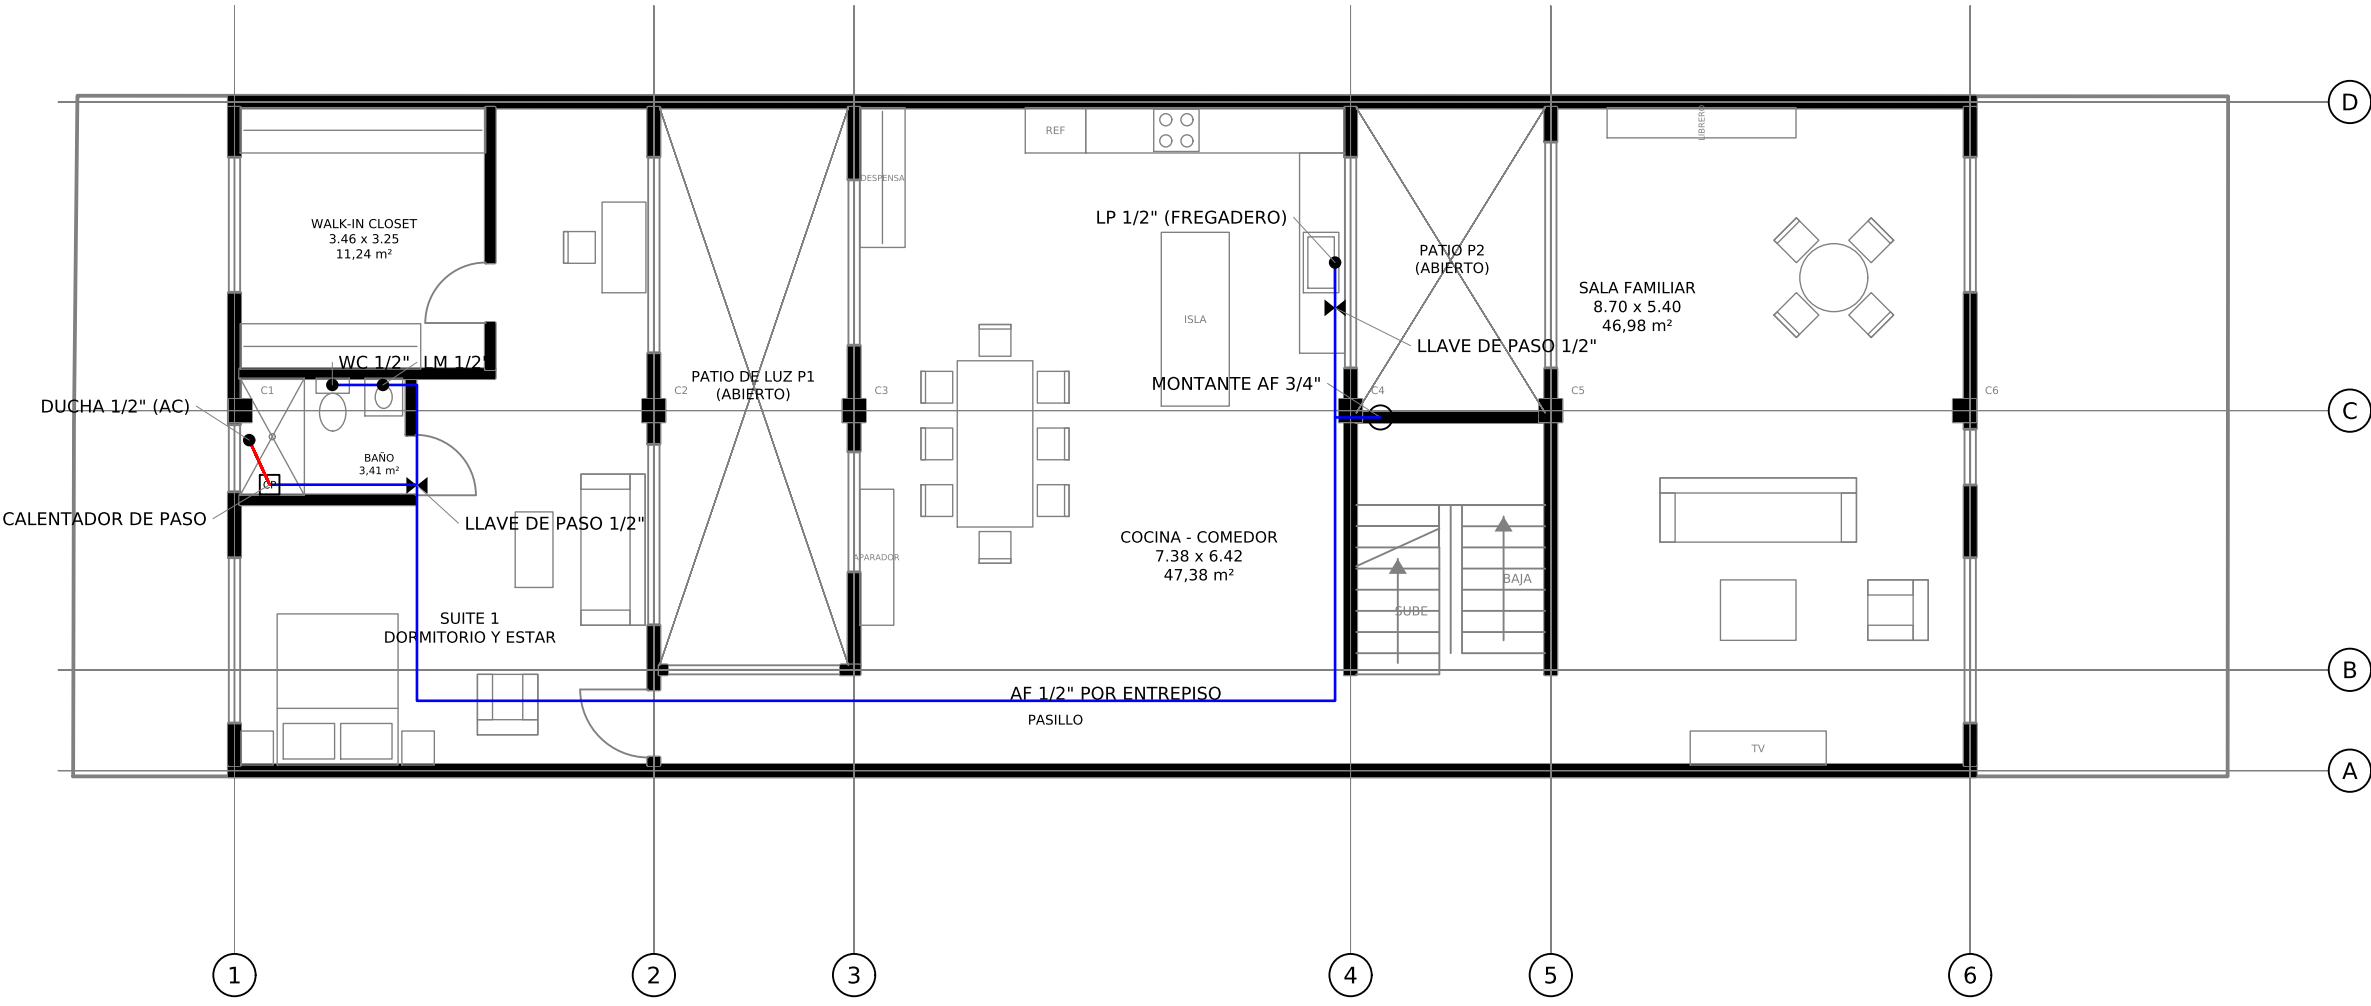

AGUA POTABLE - NIVEL 2
Esc. 1:100

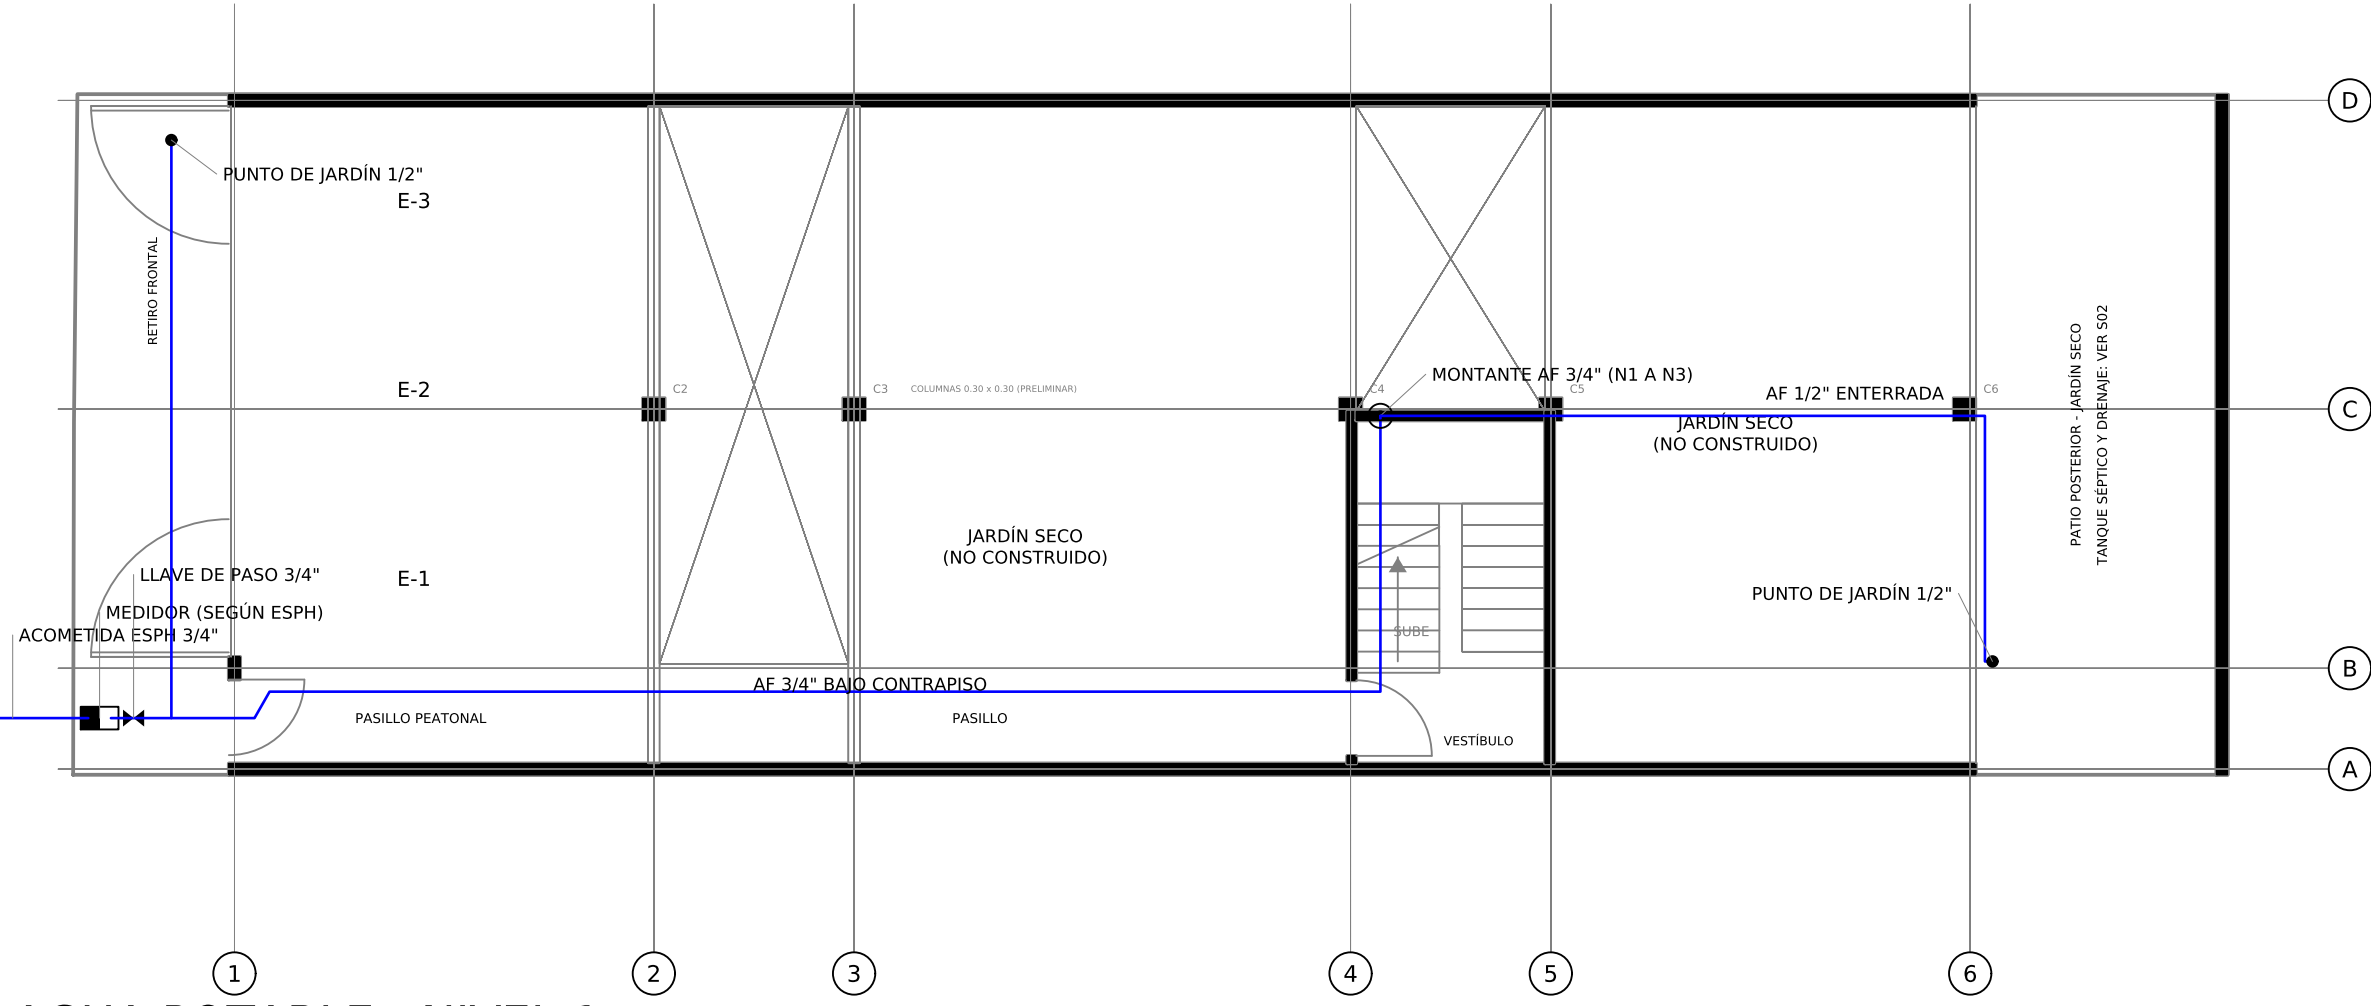


AGUA POTABLE - NIVEL 1
Esc. 1:100


DIAGRAMA VERTICAL DE AGUA POTABLE (ESQUEMÁTICO)



DETALLE 1 - ACOMETIDA Y MEDIDOR [PR]
S/E

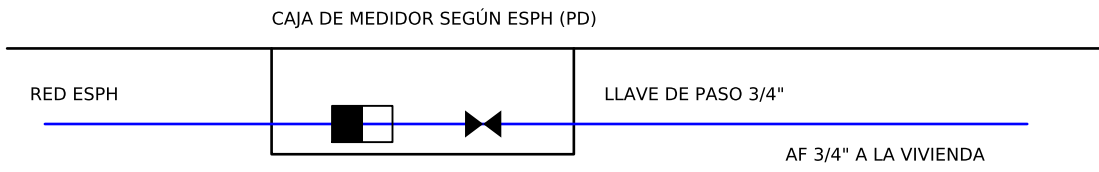

DETALLE 2 - CALENTADOR DE PASO EN DUCHA
ELEVACIÓN - S/E

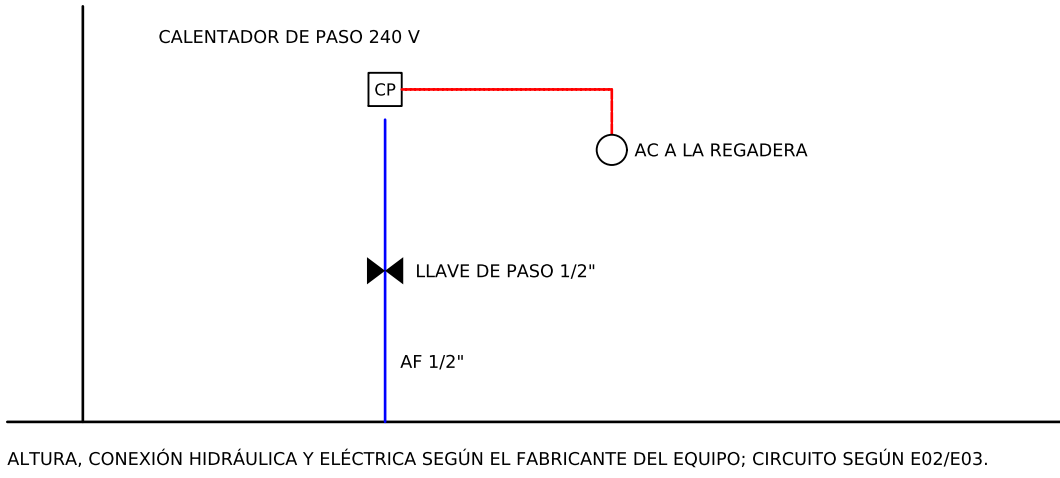

SIMBOLOGÍA

	TUBERÍA DE AGUA FRÍA (PVC A PRESIÓN) [PR]
	TUBERÍA DE AGUA CALIENTE (CPVC), SOLO DUCHAS
	LLAVE DE PASO
	SALIDA A APARATO (DIÁMETRO INDICADO)
	MONTANTE
	MEDIDOR DE AGUA (SEGÚN ESPH)
	CALENTADOR DE PASO ELÉCTRICO

LM: LAVATORIO; WC: INODORO; LP: FREGADERO; AF / AC: AGUA FRÍA / CALIENTE.

NOTAS:

- TODAS LAS MEDIDAS ESTÁN DADAS EN METROS, SALVO ALGUNA EXCEPCIÓN INDICADA. [PR]
 - EL AGUA POTABLE PROVIENE DEL SISTEMA PÚBLICO (ESPH), DIRECTAMENTE DE LA CONEXIÓN DE LA CALLE, SIN TANQUE DE ALMACENAMIENTO NI EQUIPO DE BOMBEO. [PR]
 - UBICACIÓN Y CARACTERÍSTICAS DEL MEDIDOR Y DE LA CAJA SEGÚN LA ESPH (PD).
 - DIÁMETROS DE LA REFERENCIA [PR]: ACOMETIDA, TRAMO PRINCIPAL Y MONTANTE 3/4"; RAMALES Y SALIDAS 1/2". LLAVE DE PASO EN CADA BAÑO Y EN LA COCINA.
 - AGUA CALIENTE ÚNICAMENTE EN LAS DUCHAS, MEDIANTE UN CALENTADOR DE PASO ELÉCTRICO POR BAÑO (CIRCUITOS EN E02 Y E03).
 - TUBERÍA DE AGUA FRÍA PVC A PRESIÓN Y DE AGUA CALIENTE CPVC; CLASE O SDR SEGÚN CÁLCULO (PD).
 - EL MONTANTE SUBE EMBEBIDO EN EL MURO DEL EJE C (ESCALERA / PATIO P2); LOS RAMALES DE LOS NIVELES 2 Y 3 VIAJAN POR EL ENTREPISO.
 - PROBAR LA RED A PRESIÓN ANTES DE CERRAR PAREDES Y CIELOS (PD).
- [PR] = NOTA TOMADA DEL PROYECTO DE REFERENCIA, PENDIENTE DE REVISIÓN.

ESPACIO PARA SELLOS Y TIMBRES

CivilCon Diseño y Construcción SRLTDA Céd. Jurídica: 3-102-762712	
PROFESIONAL RESPONSABLE: DIRECTOR TÉCNICO: Steven Viales (Civil) IC-40759 David Barrantes (Electricidad) IE-27499	
PROYECTO: VIVIENDA UNIFAMILIAR DISTRITO 03 SANTIAGO, CANTÓN 05 SAN RAFAEL, PROVINCIA 04 HEREDIA, COSTA RICA.	
INFORMACIÓN REGISTRO PÚBLICO: FOLIO REAL: 4-041200-000 PLANO CATASTRADO: 4-57389-2023 ÁREA SEGÚN CATASTRO: 256 m²	
CONTENIDO: AGUA POTABLE PLANTAS NIVELES 1, 2 Y 3. DIAGRAMA VERTICAL. DETALLES. SIMBOLOGÍA. NOTAS.	
ESCALAS: 1:100 / S/E	
CONTROL DE REVISIONES	
REV.	FECHA DESCRIPCIÓN
0	06-10-2026 VERSIÓN DE TRABAJO PARA REVISIÓN
1	07-10-2026 PUNTO DE JARDÍN POSTERIOR TRASLADADO (S02)
ESTADO:	
VERSIÓN DE TRABAJO NO APTA PARA CONSTRUCCIÓN NI TRÁMITE	
LUGAR	LÁMINA
COSTA RICA	S01
OCT 2026	TOTAL --