




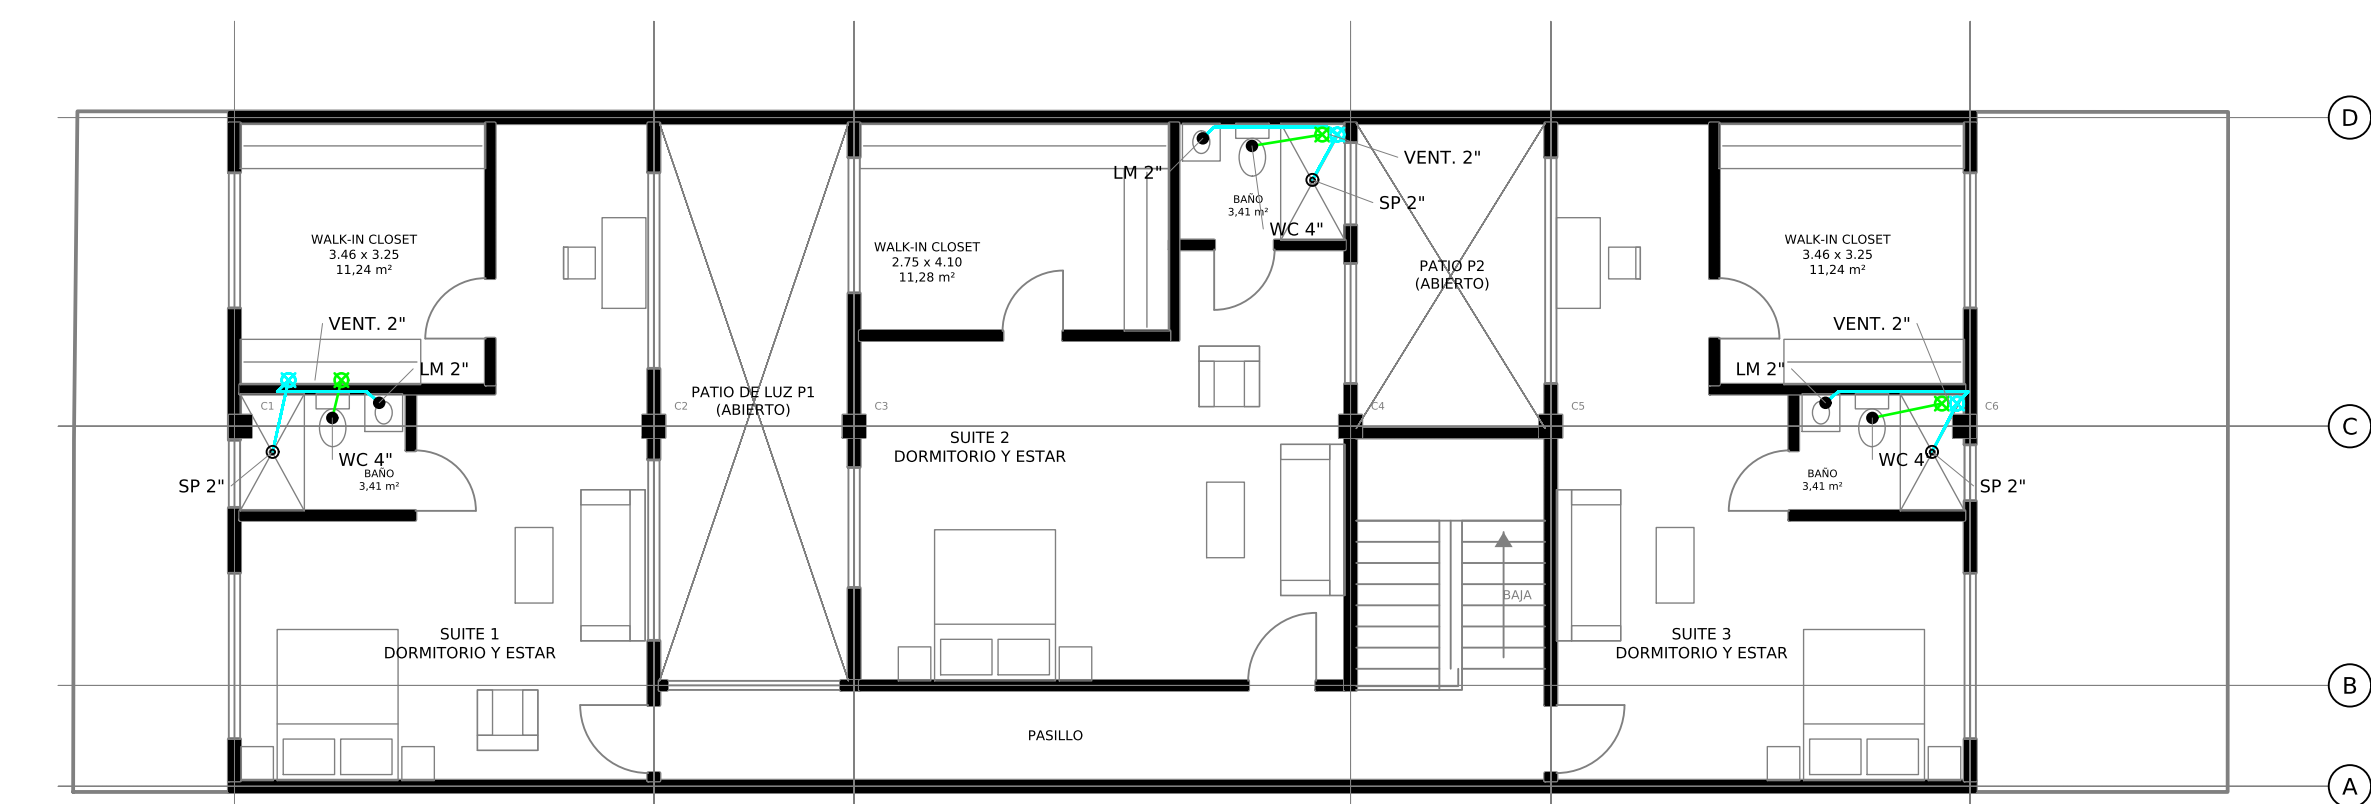

AGUAS RESIDUALES - NIVEL 3
Esc. 1:100

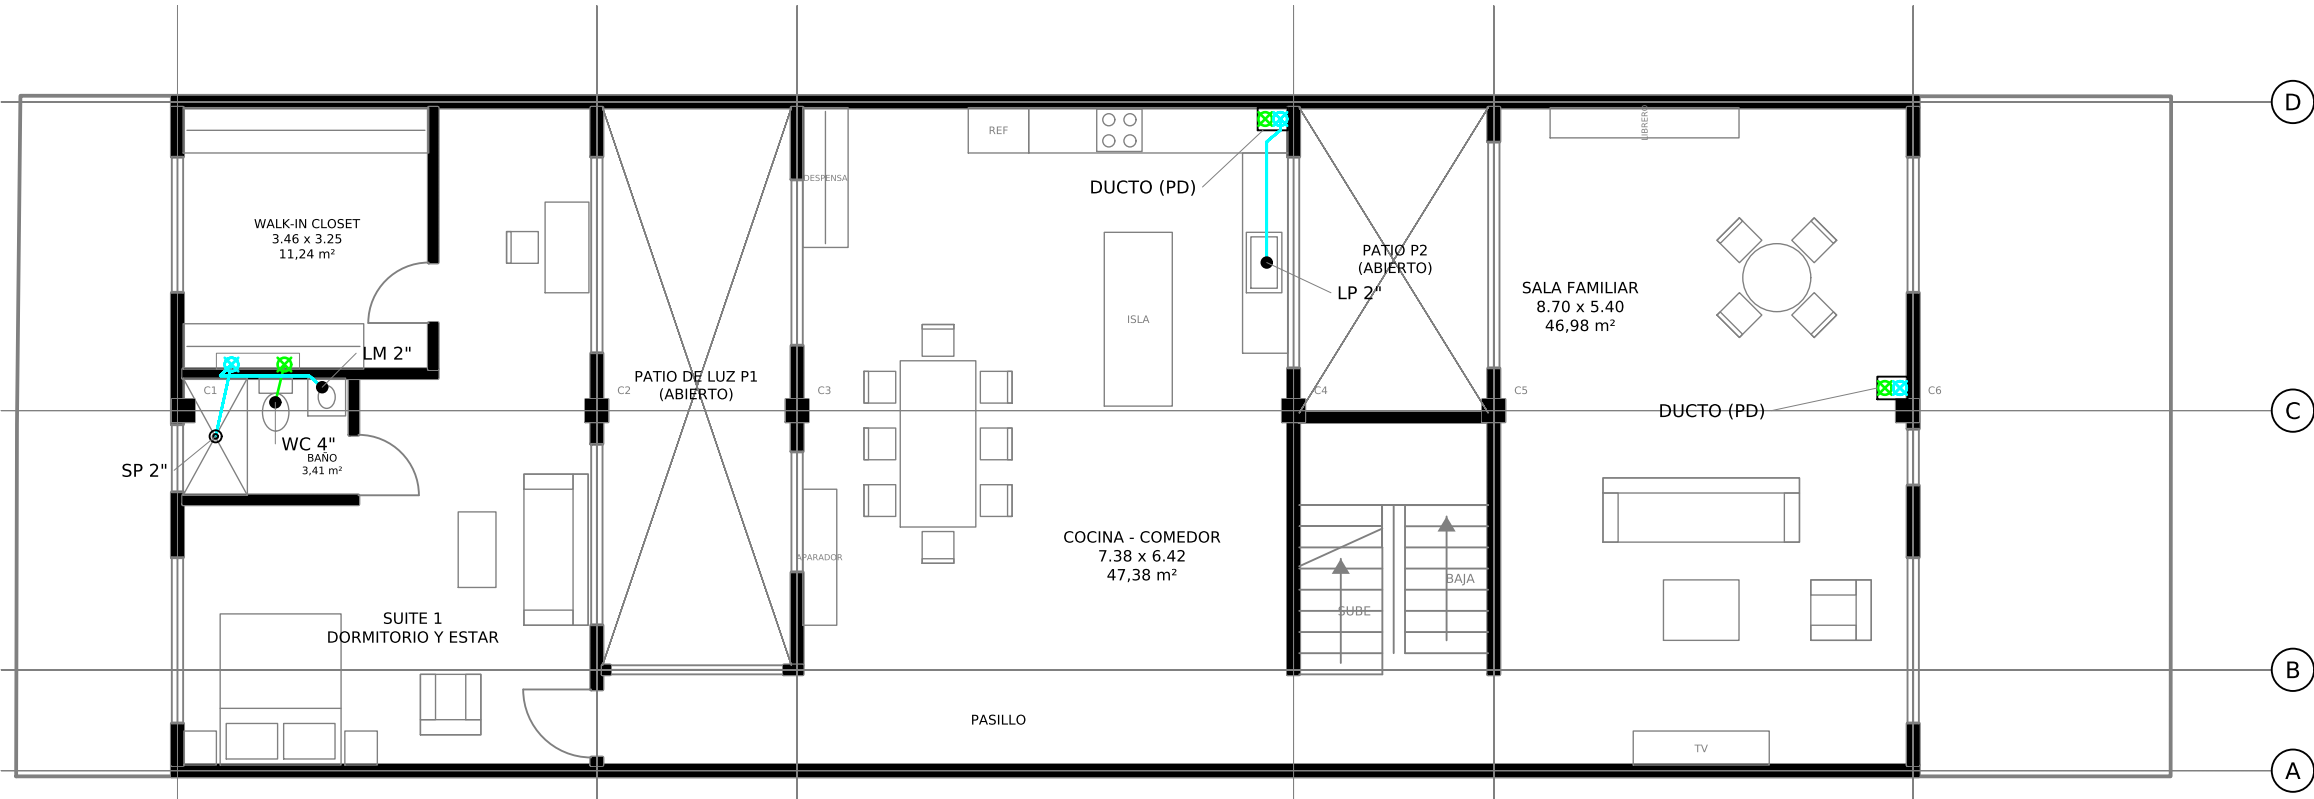

AGUAS RESIDUALES - NIVEL 2
Esc. 1:100

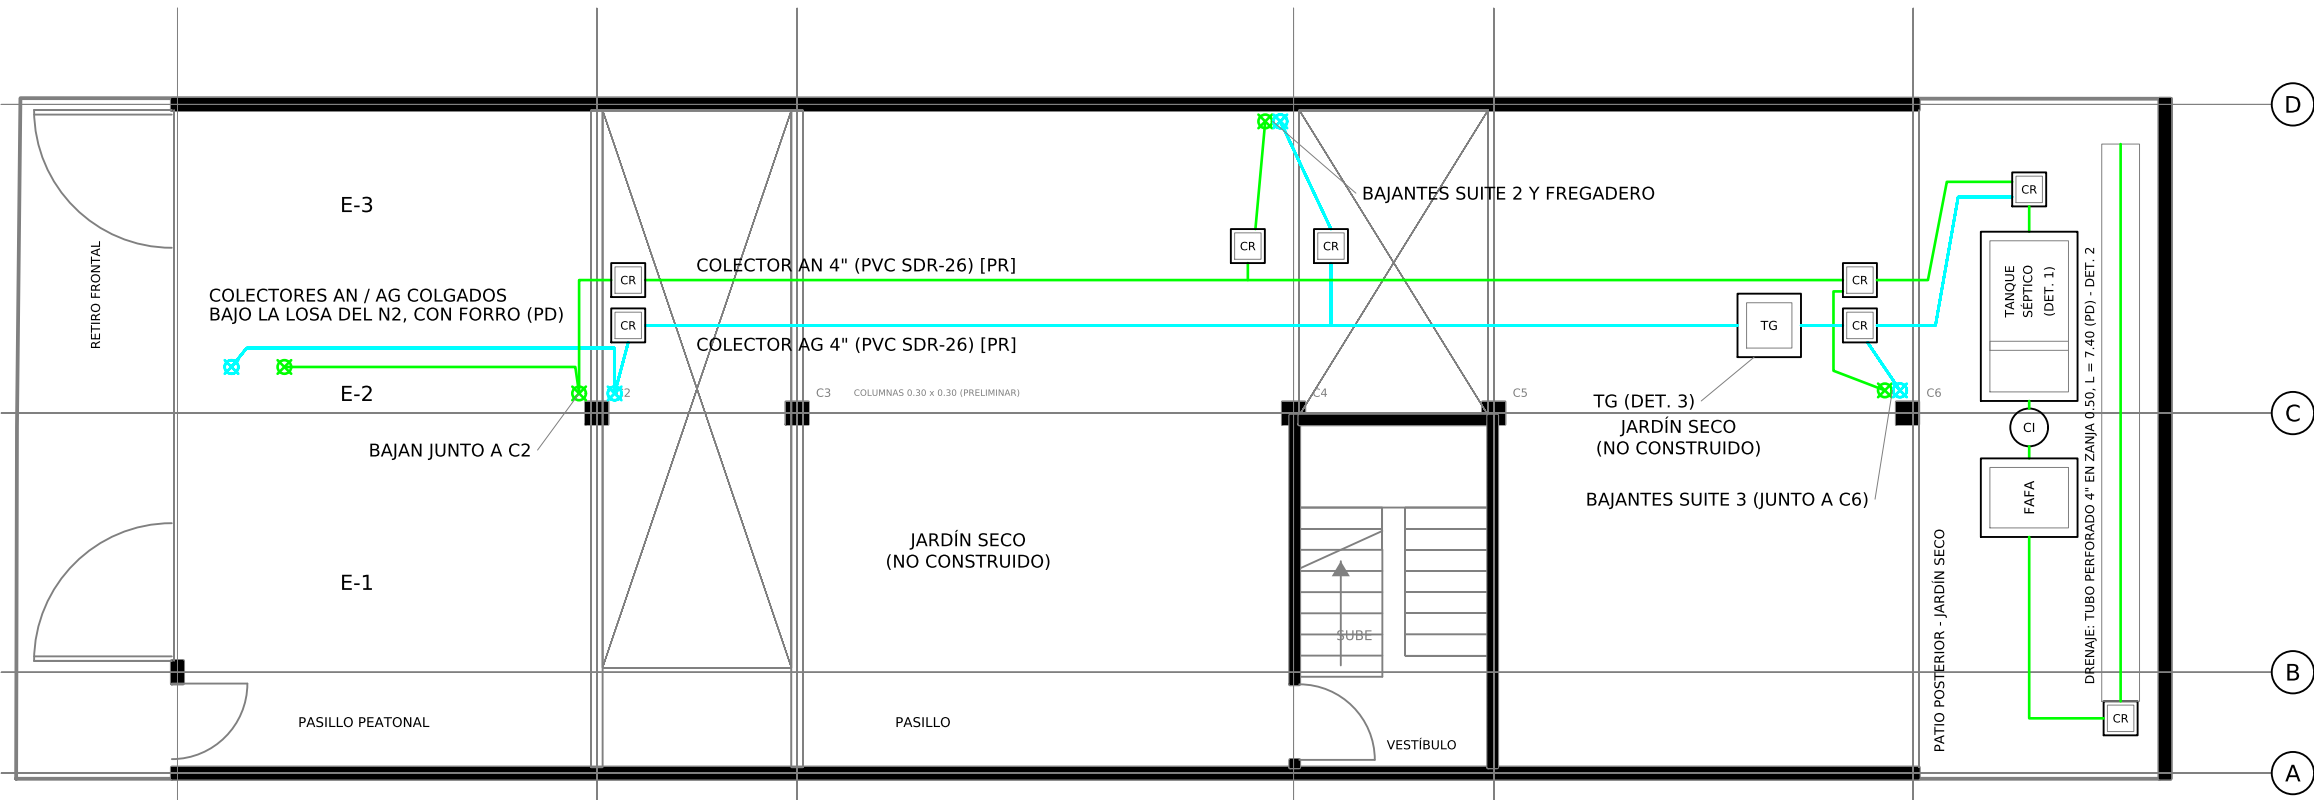


AGUAS RESIDUALES - NIVEL 1
Esc. 1:100


DETALLE 1 - TANQUE SÉPTICO CON FAFA [PR]

Esc. 1:25 - DIMENSIONES INTERIORES

VISTA SUPERIOR

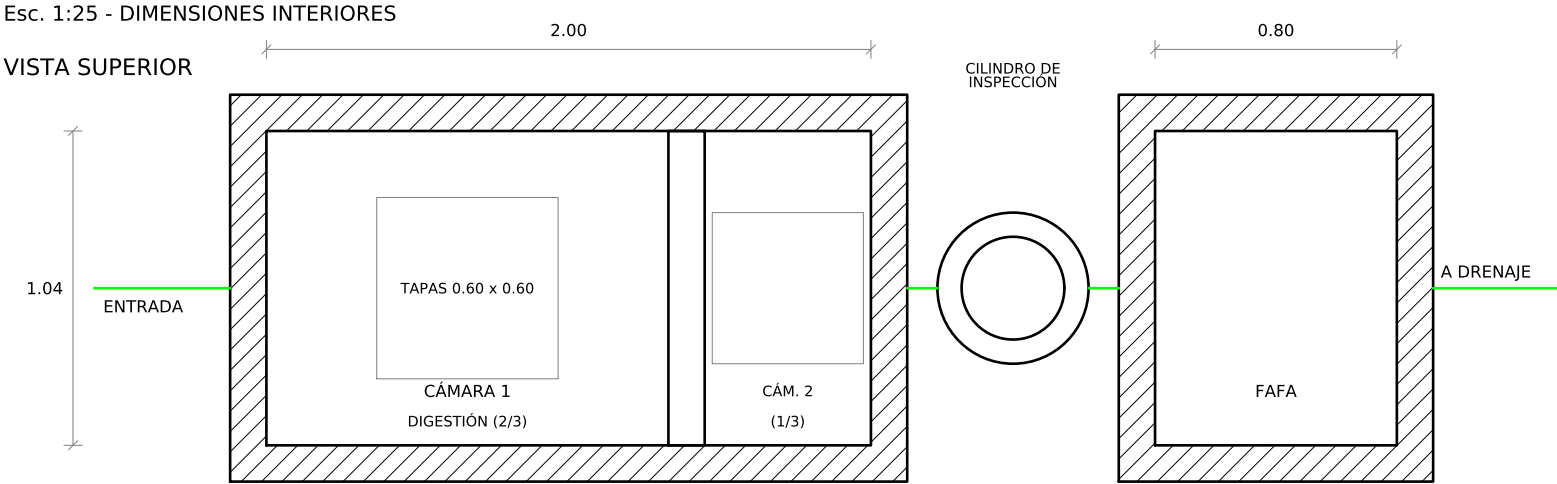


VISTA LATERAL

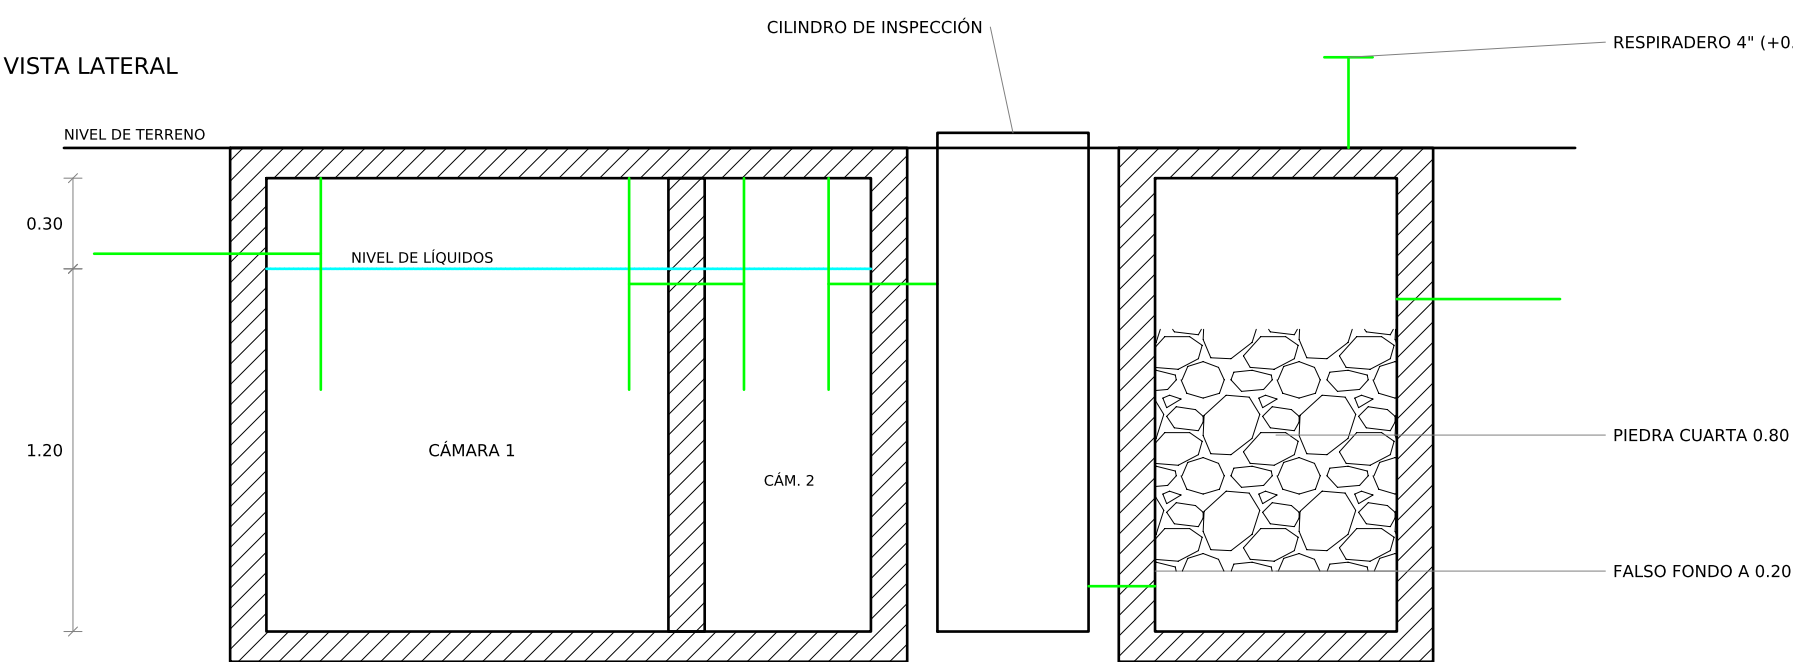


DETALLE 2 - SECCIÓN DE DRENAJE [PR]

Esc. 1:10

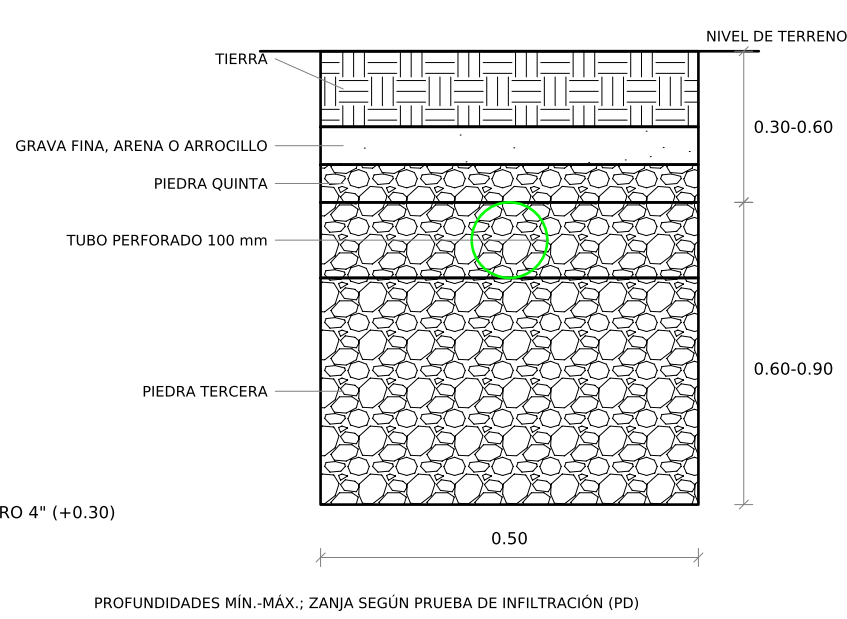


DETALLE 3 - CAJA DE REGISTRO Y TRAMPA DE GRASA [PR]

SECCIONES - S/E

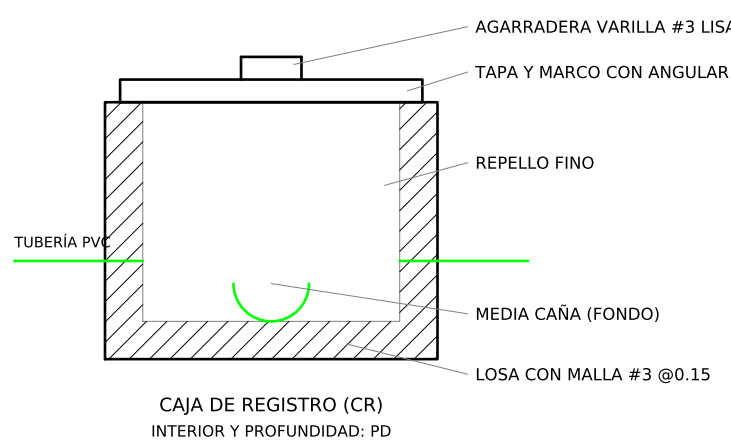

DETALLE 4 - BAÑO TÍPICO

SUITE 1 (N2 Y N3), SUITE 3 EN ESPEJO - Esc. 1:40

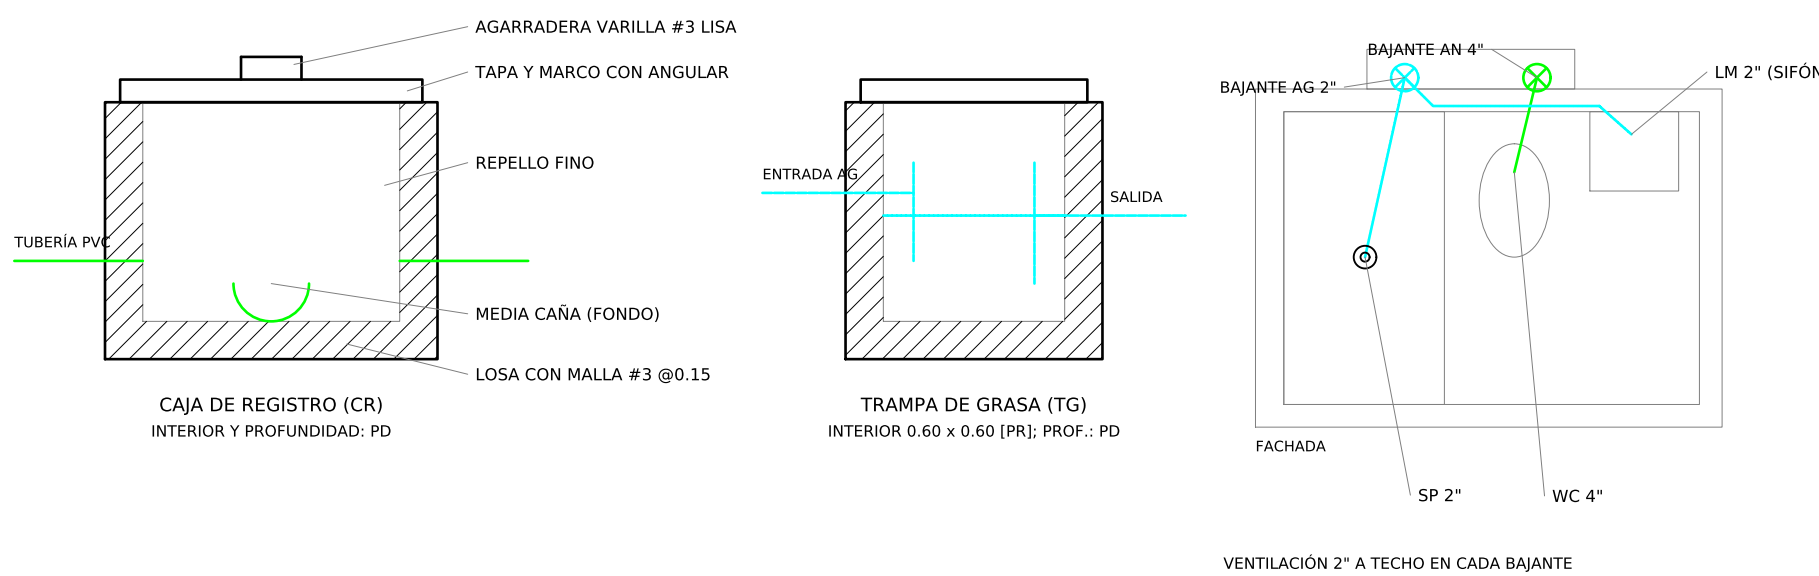

SIMBOLOGÍA

	AGUAS NEGRAS (PVC) [PR]
	AGUAS GRISES (PVC) [PR]
	BAJANTE DE AGUAS NEGRAS 4"
	BAJANTE DE AGUAS GRISES 2"
	SIFÓN DE PISO (DUCHA) 2"
	SALIDA DE APARATO (WC / LM / LP)
	CAJA DE REGISTRO (DET. 3)
	DRENAJE EN ZANJA (DET. 2)

AN / AG: AGUAS NEGRAS / GRISES; TG: TRAMPA DE GRASA; FAFA: FILTRO ANAEROBIO DE FLUJO ASCENDENTE.

NOTAS:

- 1.- TODAS LAS MEDIDAS ESTÁN DADAS EN METROS; LAS DIMENSIONES DEL TANQUE Y DEL FAFA SON INTERIORES, SALVO INDICACIÓN CONTRARIA. [PR]
 - 2.- VERIFICAR IN SITU LA UBICACIÓN, LOS NIVELES Y LAS CONDICIONES DEL TERRENO ANTES DE INICIAR LA CONSTRUCCIÓN. [PR]
 - 3.- NO HAY ALCANTARILLADO SANITARIO: LAS AGUAS RESIDUALES SE TRATAN EN TANQUE SÉPTICO CON FAFA Y SE DISPONEN EN EL DRENAJE DEL PATIO POSTERIOR.
 - 4.- AGUAS NEGRAS (INODOROS) EN 4" Y AGUAS GRISES (LAVATORIOS, DUCHAS Y FREGADERO) EN 2", CON BAJANTES Y CAJAS DE REGISTRO SEPARADAS. [PR]
 - 5.- TUBERÍA ENTERRADA EN PVC SDR-26 O SUPERIOR, DIÁMETRO MÍNIMO 100 MM (4"). ACCESORIOS SANITARIOS EN TODOS LOS CAMBIOS DE DIRECCIÓN. [PR] PENDIENTES DE COLECTORES Y RAMALES: PD.
 - 6.- LAS AGUAS GRISES PASAN POR LA TRAMPA DE GRASA Y SE UNEN A LAS AGUAS NEGRAS EN LA CAJA DE REGISTRO DE ENTRADA AL TANQUE.
 - 7.- BAJANTES: SUITE 1 EN FORRO DEL MURO BAÑO / WALK-IN, CON COLECTORES COLGADOS BAJO LA LOSA DEL N2 HASTA C2; SUITE 2 Y FREGADERO EN DUCTO DE LA COCINA (ESQUINA D/4); SUITE 3 EN DUCTO JUNTO A C6 EN LA SALA. DIMENSIONES DE DUCTOS Y FORROS: PD.
 - 8.- CADA BAJANTE SE PROLONGA COMO VENTILACIÓN DE 2" SOBRE LA CUBIERTA [PR]
 - 9.- LAS TUBERÍAS PASAN SOBRE LAS PLACAS DE CIMENTACIÓN SIN ATRAVESAR PEDESTALES; CRUCES CON VIGAS RIOSTRA CON CAMISA (PD). EL TANQUE Y LAS CAJAS SE UBICAN FUERA DE LAS PLACAS (VER C01).
 - 10.- TANQUE Y FAFA: CONCRETO DE 210 KG/CM2; LOSAS INFERIOR Y SUPERIOR DE 0.10 M MÍNIMO CON MALLA #3 @20 CM; MUROS DE BLOQUE 12x20x40 CON JUNTAS LLENAS Y REPELLO IMPERMEABLE INTERIOR; REFUERZO VERTICAL #3 @40 CM Y HORIZONTAL #3 CADA DOS HILADAS; RECUBRIMIENTO 4 CM; CURADO 7 DÍAS. [PR]
 - 11.- CÁMARA 1 (DIGESTIÓN) = 2/3 Y CÁMARA 2 (CLARIFICACIÓN) = 1/3 DEL LARGO. TEES SANITARIAS DE PVC 100 MM, 0.30 M SOBRE Y 0.40 M BAJO EL NIVEL DE LÍQUIDOS. BORDE LIBRE 0.30 M Y PROFUNDIDAD ÚTIL 1.20 M. [PR]
 - 12.- FAFA: 1.04 x 0.80 M INTERIOR, PROFUNDIDAD ÚTIL 1.20 M, FALSO FONDO A 0.20 M CON LOSA PERFORADA, MEDIO FILTRANTE DE PIEDRA CUARTA LAVADA (5-7 CM) DE 0.80 M SIN COMPACTAR Y ESPACIO LIBRE SUPERIOR DE 0.20 M. [PR]
 - 13.- RESPIRADEROS DE PVC 100 MM, 0.30 M SOBRE EL TERRENO, CON SOMBRERETE. CILINDRO DE INSPECCIÓN DE CONCRETO, DIÁMETRO INTERIOR MÍNIMO 0.30 M. TAPAS DE CONCRETO REFORZADO DE 0.60 x 0.60 M MÍNIMO, CON AGARRADERAS. [PR]
 - 14.- DRENAJE: TUBO PERFORADO DE 100 MM EN ZANJA DE 0.50 M (DETALLE 2). LONGITUD (7.40 M DIBUJADOS) Y PROFUNDIDAD SUJETAS A LA PRUEBA DE INFILTRACIÓN Y AL CÁLCULO (PD).
 - 15.- NO RELLENAR HASTA QUE EL CONCRETO ALCANCE SU RESISTENCIA; COMPACTAR EN CAPAS DE 20 CM MÁXIMO Y EVITAR EL PASO DE VEHÍCULOS SOBRE EL SISTEMA. [PR]
 - 16.- ANTES DEL RELLENO, VERIFICAR LA ESTANQUEIDAD DEL TANQUE Y DEL FAFA; LIMPIAR EL SISTEMA ANTES DE COLOCAR EL MEDIO FILTRANTE Y LLENAR EL FAFA CON AGUA ANTES DE INICIAR LA OPERACIÓN. [PR]
 - 17.- MANTENIMIENTO: RETIRAR LOS LODOS DEL TANQUE CUANDO OCUPEN APROXIMADAMENTE 1/3 DEL VOLUMEN DE LA PRIMERA CÁMARA. [PR]
 - 18.- NO SE PERMITE MODIFICAR DIMENSIONES, NIVELES, DIÁMETROS NI MATERIALES SIN AUTORIZACIÓN DEL PROFESIONAL RESPONSABLE. [PR]
- [PR] = NOTA TOMADA DEL PROYECTO DE REFERENCIA, PENDIENTE DE REVISIÓN.

ESPACIO PARA SELLOS Y TIMBRES

CivilCon Diseño y Construcción SRLTDA
Céd. Jurídica: 3-102-762712

PROFESIONAL RESPONSABLE:

DIRECTOR TÉCNICO:
Steven Viales (Civil) IC-40759
David Barrantes (Electricidad) IE-27499

PROYECTO:

VIVIENDA UNIFAMILIAR
DISTRITO 03 SANTIAGO, CANTÓN 05 SAN RAFAEL,
PROVINCIA 04 HEREDIA, COSTA RICA.

INFORMACIÓN REGISTRO PÚBLICO:

FOLIO REAL: 4-041200-000
PLANO CATASTRADO: 4-57389-2023
ÁREA SEGÚN CATASTRO: 256 m²

CONTENIDO:

AGUAS RESIDUALES
PLANTAS NIVELES 1, 2 Y 3.
TANQUE SÉPTICO, FAFA Y DRENAJE.
CAJA DE REGISTRO,
TRAMPA DE GRASA Y BAÑO TÍPICO.
SIMBOLOGÍA Y NOTAS.

ESCALAS: 1:100 / INDICADAS

CONTROL DE REVISIONES

REV.	FECHA	DESCRIPCIÓN
0	06-10-2026	VERSIÓN DE TRABAJO PARA REVISIÓN

ESTADO:

VERSIÓN DE TRABAJO
NO APTA PARA CONSTRUCCIÓN NI TRÁMITE

LUGAR	LÁMINA
COSTA RICA	S02
OCT 2026	TOTAL --