


CALLE PÚBLICA

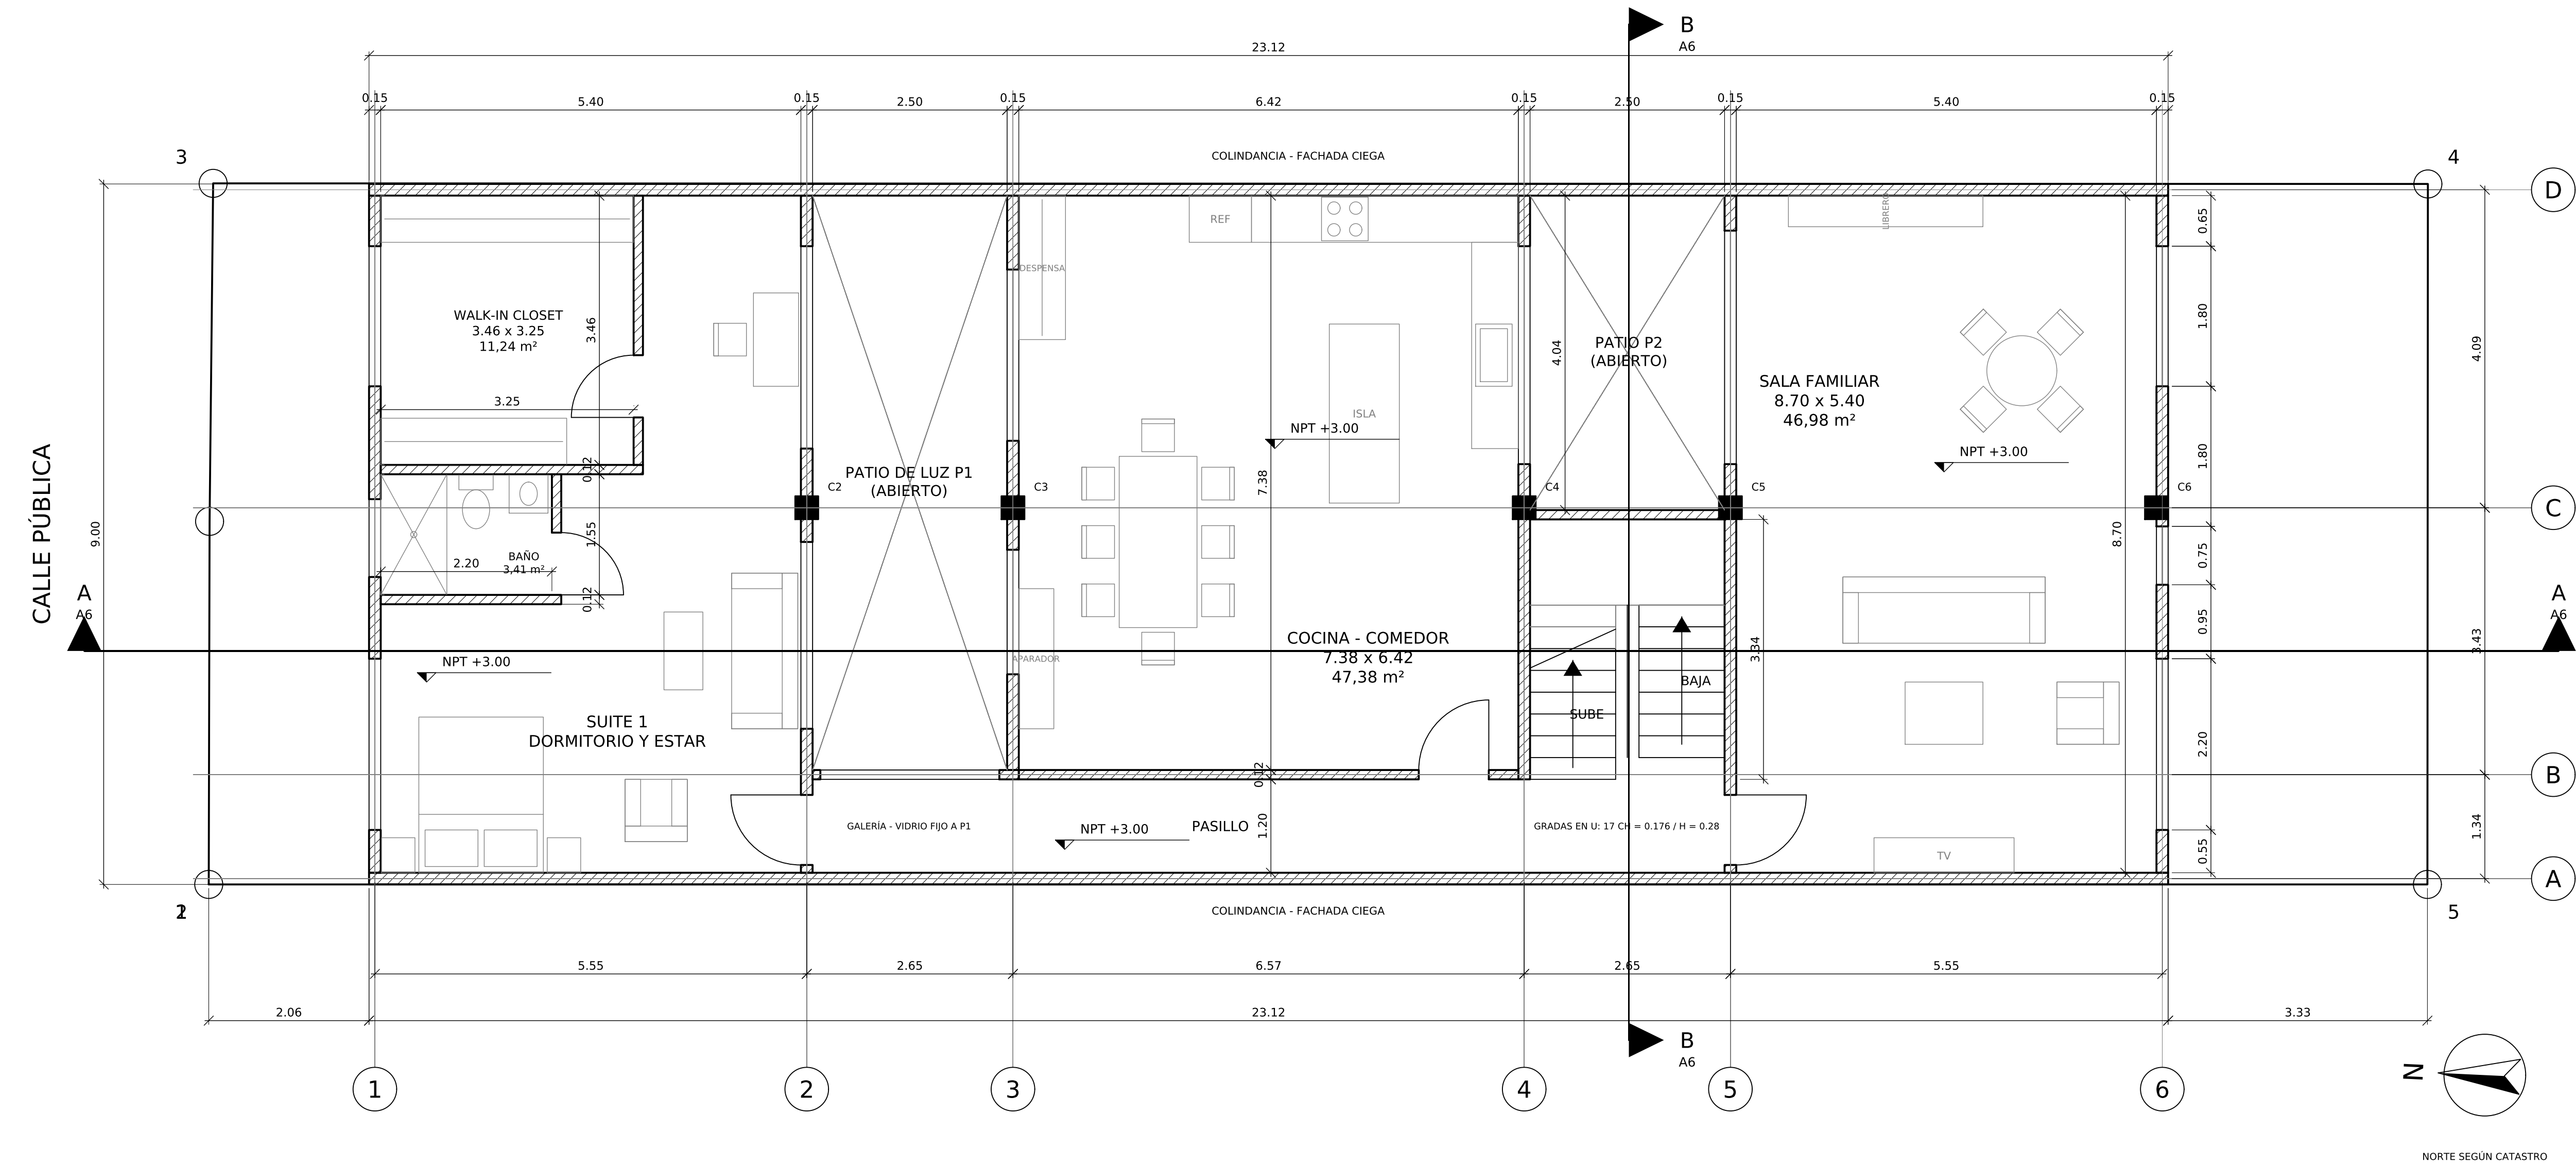

PLANTA NIVEL 2

SUITE 1, COCINA - COMEDOR Y SALA FAMILIAR
Esc. 1:50



DERROTERO

LÍNEA	ACIMUT		DISTANCIA	
	°	'	m	cm
1 - 2	87	25	4	66
2 - 3	87	53	4	34
3 - 4	177	18	28	46
4 - 5	267	20	9	00
5 - 1	357	17	28	51
AMARRE	ACIMUT		DISTANCIA	
	°	'	m	cm
3 - P.I.	101	22	75	71

VER CUADRO DE COORDENADAS CRTM05 EN LÁMINA A1.

CUADRO DE ÁREAS NIVEL 2

ESPACIO (MEDIDAS LIBRES)	ÁREA
SUITE 1 (DORMITORIO-ESTAR, BAÑO Y WALK-IN) 8,70 x 5,40	46,98 m²
BAÑO 1,55 x 2,20	3,41 m²
WALK-IN CLOSET 3,46 x 3,25	11,24 m²
COCINA - COMEDOR 7,38 x 6,42	47,38 m²
SALA FAMILIAR 8,70 x 5,40	46,98 m²
PASILLO 1,20 x 11,72	14,06 m²
GRADAS 3,34 x 2,50	8,35 m²
ÁREA CONSTRUIDA NIVEL 2 (ENVOLVENTE - PATIOS)	179,53 m²

ÁREA CONSTRUIDA INCLUYE MUROS. BAÑO Y WALK-IN ESTÁN INCLUIDOS EN LA SUITE.

RESUMEN DE ÁREAS DE CONSTRUCCIÓN

NIVEL 1 (VER A2)	66,57 m²
NIVEL 2	179,53 m²
NIVEL 3 (PRELIMINAR, VER A4)	179,53 m²
ÁREA TOTAL DE CONSTRUCCIÓN	425,63 m²

PORCENTAJE DE COBERTURA

CONCEPTO	VALOR
ÁREA DE LOTE (SEGÚN CATASTRO)	256,00 m²
HUELLA CONSTRUCTIVA (PROYECCIÓN NIVELES 2 Y 3)	179,53 m²
% COBERTURA	70,13 %

CÁLCULO: (HUELLA / ÁREA DE LOTE) x 100 = (179,53 / 256,00) x 100 = 70,13 %


NOTAS:

- TODAS LAS MEDIDAS ESTÁN DADAS EN METROS, SALVO INDICACIÓN CONTRARIA. [PR]
- LA TAPIA COLINDANTE DE MAMPOSTERÍA DEBERÁ PROLONGARSE HASTA EL NIVEL DE LA VIGA CORONA DEL ÚLTIMO NIVEL, GARANTIZANDO EL APANTALLAMIENTO VISUAL PERMANENTE HACIA LA PROPIEDAD COLINDANTE.
- LOS DATOS DEL LOTE (VÉRTICES, DERROTERO Y ÁREA) SE TOMARON DEL PLANO CATASTRADO 4-57389-2023, SISTEMA CRTM05. NO SUSTITUYEN UN LEVANTAMIENTO TOPOGRÁFICO.
- RETIROS DE DISEÑO: FRONTAL 2.00 m MEDIDO DESDE EL VÉRTICE 3; POSTERIOR MÍNIMO 3.00 m; LATERALES 0.00 m. CONFIRMAR CON ALINEAMIENTO Y USO DE SUELO MUNICIPAL.
- LAS FACHADAS LATERALES SE UBICAN SOBRE COLINDANCIA Y SERÁN CIEGAS (SIN VENTANAS NI VANOS).
- LOS BAÑOS CONTARÁN CON EXTRACTOR MECÁNICO DE AIRE.
- LAS CANOAS TENDRÁN MALLA PROTECTORA PARA EVITAR EL ACCESO DE BASURA. [PR]
- EL AGUA POTABLE PROVIENE DEL SISTEMA PÚBLICO (ESPH), DIRECTAMENTE DE LA CONEXIÓN DE LA CALLE.
- LAS AGUAS PLUVIALES SE DIRIGEN HACIA LA CUNETTA PÚBLICA.
- LAS AGUAS RESIDUALES SE TRATARÁN MEDIANTE TANQUE SÉPTICO Y DRENAJE EN EL PATIO POSTERIOR; DISEÑO Y UBICACIÓN EN LÁMINAS SANITARIAS.
- LA COBERTURA SE CALCULA SOBRE EL ÁREA SEGÚN CATASTRO (256 m²). LOS PATIOS P1 Y P2 SON ABIERTOS DESDE EL NIVEL 1 HASTA EL CIELO Y NO SE CONTABILIZAN EN LA HUELLA.
- PATIOS DE LUZ P1 Y P2 DE 2.50 m DE LADO MÍNIMO, DIMENSIÓN ACEPTADA POR LA MUNICIPALIDAD (ALTURA MEDIDA DESDE EL NIVEL 1).
- NIVEL 2: NPT +3.00 (ALTURA PISO A PISO 3.00 m).
- SUITE: BAÑO DE 1.55 x 2.20 m CON DUCHA, INODORO Y LAVATORIO EN LÍNEA Y PUERTA DE 0.80 m ABATIBLE HACIA EL DORMITORIO; WALK-IN CLOSET CON MUEBLES DE 0.60 m; SOLO EL BAÑO Y EL WALK-IN SON RECINTOS CERRADOS.
- PASILLO DE 1.20 m CERRADO HACIA EL PATIO P1 CON VIDRIO FIJO (GALERÍA). ACCESOS A LA SUITE Y A LA SALA FAMILIAR EN LOS EXTREMOS DEL PASILLO (EJES 2 Y 5).
- COCINA EN L CON ISLA; FREGADERO BAJO VENTANA HACIA EL PATIO P2. LA COCINA-COMEDOR Y LA SALA FAMILIAR NO LLEVAN BAÑO.
- VENTANAS HACIA P1 DESFASADAS ENTRE SUITE Y COCINA-COMEDOR PARA REDUCIR VISUALES CRUZADAS.
- COLUMNAS SOBRE EL EJE C SEGÚN LÁMINA A2; SECCIONES Y REFUERZO SEGÚN PLANOS ESTRUCTURALES.
- FACHADA FRONTAL: VENTANAS DE PISO A 2.20 m CON PAÑO FIJO INFERIOR HASTA 0.90 m; WALK-IN CON VIDRIOS FIJOS; BAÑO CON VIDRIO ARENADO (VER A5).
- FACHADA POSTERIOR: VENTANAS CON ANTEPECHO COMÚN DE 0.90 m Y DINTEL A 2.20 m, ALINEADAS ENTRE LOS NIVELES 2 Y 3 (VER A5).
- DIMENSIONES Y TIPOS DE PUERTAS Y VENTANAS EN LÁMINA A8.

[PR] = NOTA TOMADA DEL PROYECTO DE REFERENCIA, PENDIENTE DE REVISIÓN.

DETALLE EXTRACTOR DE AIRE

BAÑOS - CORTE ESQUEMÁTICO, Esc. S/E

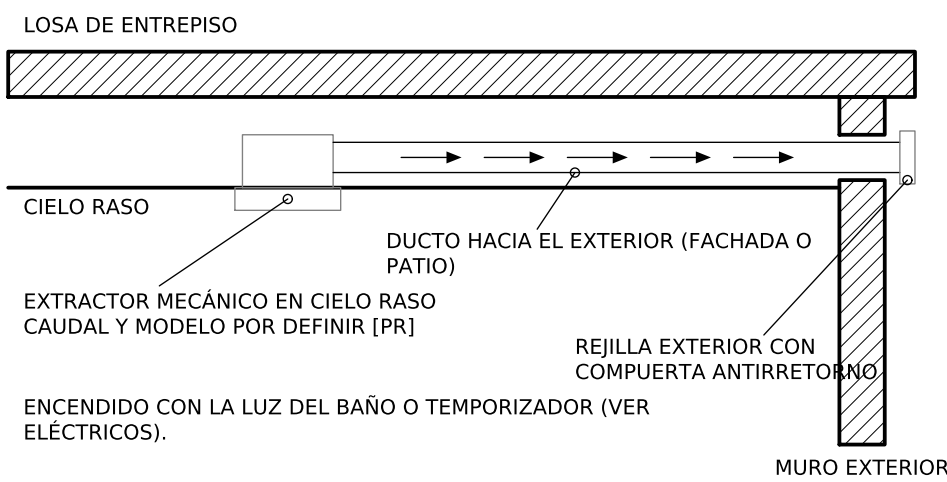

ESPACIO PARA SELLOS Y TIMBRES

CivilCon Diseño y Construcción SRLTDA
Céd. Jurídica: 3-102-762712

PROFESIONAL RESPONSABLE:
DIRECTOR TÉCNICO:
Steven Viales (Civil) IC-40759
David Barrantes (Electricidad) IE-27499

PROYECTO:
VIVIENDA UNIFAMILIAR
DISTRITO 03 SANTIAGO, CANTÓN 05 SAN RAFAEL,
PROVINCIA 04 HEREDIA, COSTA RICA.

INFORMACIÓN REGISTRO PÚBLICO:
FOLIO REAL: 4-041200-000
PLANO CATASTRADO: 4-57389-2023
ÁREA SEGÚN CATASTRO: 256 m²

CONTENIDO:
PLANTA NIVEL 2
SUITE 1, COCINA-COMEDOR, SALA.
DERROTERO.
CUADRO DE ÁREAS.
PORCENTAJE DE COBERTURA.
DETALLE EXTRACTOR DE AIRE.
NOTAS.

ESCALAS: 1:50 / INDICADAS

CONTROL DE REVISIONES		
REV.	FECHA	DESCRIPCIÓN
0	06-10-2026	VERSIÓN DE TRABAJO PARA REVISIÓN
1	06-10-2026	VENTANAS POSTERIORES ALINEADAS

ESTADO:
VERSIÓN DE TRABAJO
NO APTA PARA CONSTRUCCIÓN NI TRÁMITE

LUGAR	LÁMINA
COSTA RICA	A3
OCT 2026	TOTAL --