


CALLE PÚBLICA

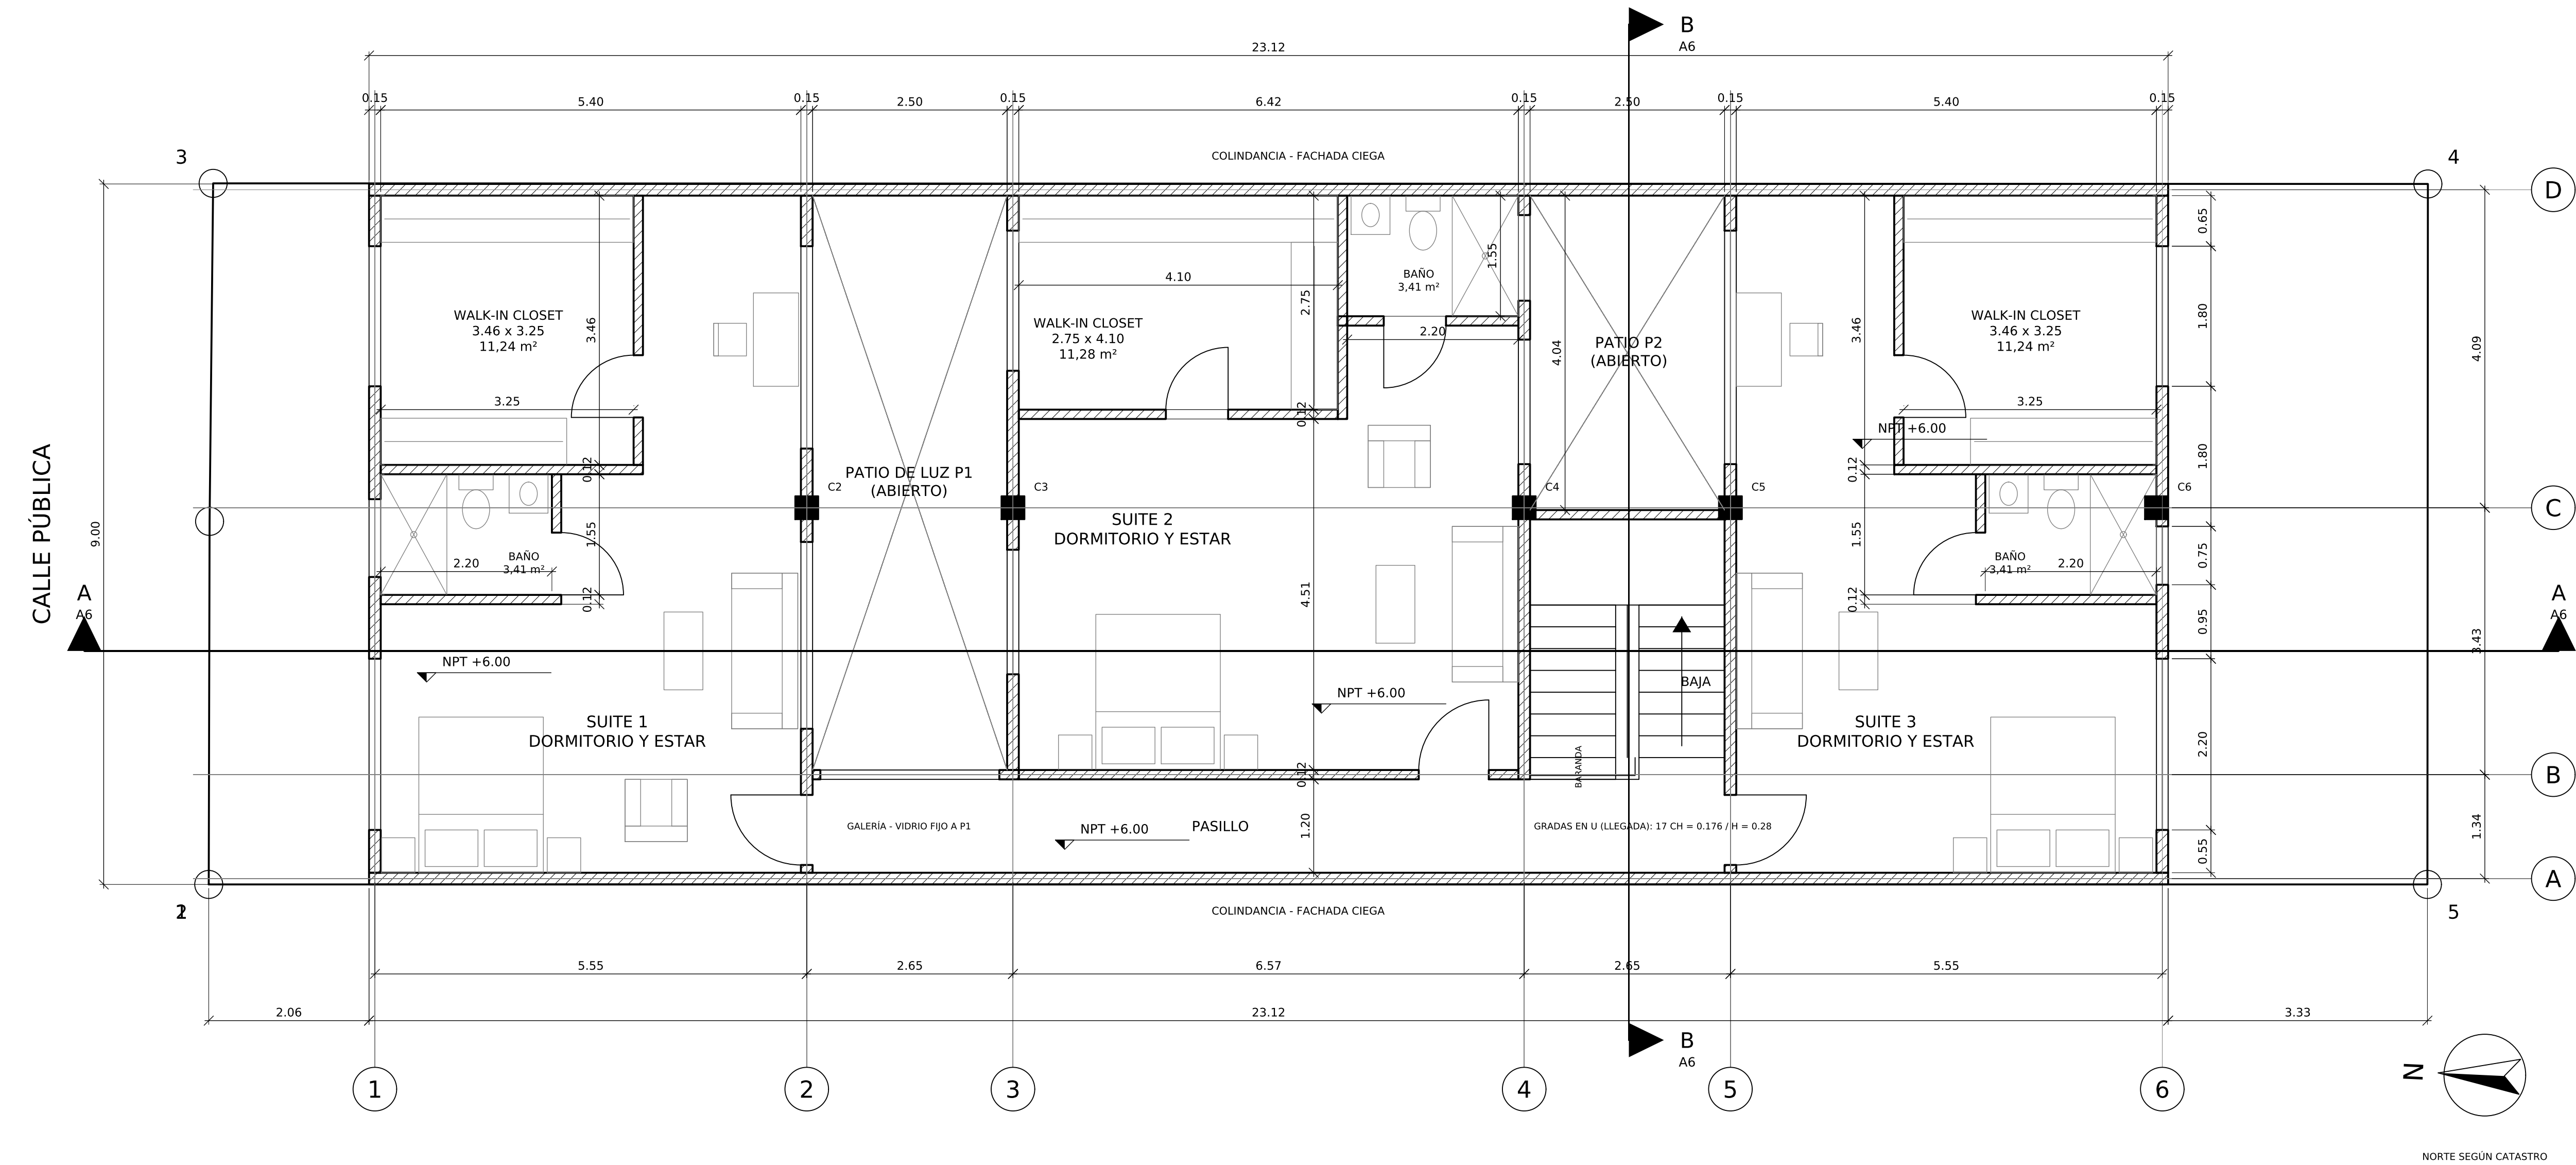

### PLANTA NIVEL 3

SUITES 1, 2 Y 3  
Esc. 1:50



#### DERROTERO

| LÍNEA    | ACIMUT |    | DISTANCIA |    |
|----------|--------|----|-----------|----|
|          | °      | '  | m         | cm |
| 1 - 2    | 87     | 25 | 4         | 66 |
| 2 - 3    | 87     | 53 | 4         | 34 |
| 3 - 4    | 177    | 18 | 28        | 46 |
| 4 - 5    | 267    | 20 | 9         | 00 |
| 5 - 1    | 357    | 17 | 28        | 51 |
| AMARRE   | ACIMUT |    | DISTANCIA |    |
|          | °      | '  | m         | cm |
| 3 - P.I. | 101    | 22 | 75        | 71 |

VER CUADRO DE COORDENADAS CRTM05 EN LÁMINA A1.

#### CUADRO DE ÁREAS NIVEL 3

| ESPACIO (MEDIDAS LIBRES)                               | ÁREA         |
|--------------------------------------------------------|--------------|
| SUITE 1 (DORMITORIO-ESTAR, BAÑO Y WALK-IN) 8,70 x 5,40 | 46,98 m²     |
| BAÑO 1,55 x 2,20 / WALK-IN 3,46 x 3,25                 | 3,41 / 11,24 |
| SUITE 2 (DORMITORIO-ESTAR, BAÑO Y WALK-IN) 7,38 x 6,42 | 47,38 m²     |
| BAÑO 1,55 x 2,20 / WALK-IN 2,75 x 4,10                 | 3,41 / 11,28 |
| SUITE 3 (DORMITORIO-ESTAR, BAÑO Y WALK-IN) 8,70 x 5,40 | 46,98 m²     |
| BAÑO 1,55 x 2,20 / WALK-IN 3,46 x 3,25                 | 3,41 / 11,24 |
| PASILLO 1,20 x 11,72                                   | 14,06 m²     |
| GRADAS 3,34 x 2,50                                     | 8,35 m²      |
| ÁREA CONSTRUIDA NIVEL 3 (ENVOLVENTE - PATIOS)          | 179,53 m²    |

ÁREA CONSTRUIDA INCLUYE MUROS. BAÑOS Y WALK-IN ESTÁN INCLUIDOS EN CADA SUITE.

#### RESUMEN DE ÁREAS DE CONSTRUCCIÓN

|                            |           |
|----------------------------|-----------|
| NIVEL 1 (VER A2)           | 66,57 m²  |
| NIVEL 2 (VER A3)           | 179,53 m² |
| NIVEL 3                    | 179,53 m² |
| ÁREA TOTAL DE CONSTRUCCIÓN | 425,63 m² |

#### PORCENTAJE DE COBERTURA

| CONCEPTO                                       | VALOR     |
|------------------------------------------------|-----------|
| ÁREA DE LOTE (SEGÚN CATASTRO)                  | 256,00 m² |
| HUELLA CONSTRUCTIVA (PROYECCIÓN NIVELES 2 Y 3) | 179,53 m² |
| % COBERTURA                                    | 70,13 %   |

CÁLCULO: (HUELLA / ÁREA DE LOTE) x 100 = (179,53 / 256,00) x 100 = 70,13 %


#### NOTAS:

- TODAS LAS MEDIDAS ESTÁN DADAS EN METROS, SALVO INDICACIÓN CONTRARIA. [PR]
- LA TAPIA COLINDANTE DE MAMPOSTERÍA DEBERÁ PROLONGARSE HASTA EL NIVEL DE LA VIGA CORONA DEL ÚLTIMO NIVEL, GARANTIZANDO EL APANTALLAMIENTO VISUAL PERMANENTE HACIA LA PROPIEDAD COLINDANTE.
- LOS DATOS DEL LOTE (VÉRTICES, DERROTERO Y ÁREA) SE TOMARON DEL PLANO CATASTRADO 4-57389-2023, SISTEMA CRTM05. NO SUSTITUYEN UN LEVANTAMIENTO TOPOGRÁFICO.
- RETIROS DE DISEÑO: FRONTAL 2,00 m MEDIDO DESDE EL VÉRTICE 3; POSTERIOR MÍNIMO 3,00 m; LATERALES 0,00 m. CONFIRMAR CON ALINEAMIENTO Y USO DE SUELO MUNICIPAL.
- LAS FACHADAS LATERALES SE UBICAN SOBRE COLINDANCIA Y SERÁN CIEGAS (SIN VENTANAS NI VANOS).
- LOS BAÑOS CONTARÁN CON EXTRACTOR MECÁNICO DE AIRE.
- LAS CANOAS TENDRÁN MALLA PROTECTORA PARA EVITAR EL ACCESO DE BASURA. [PR]
- EL AGUA POTABLE PROVIENE DEL SISTEMA PÚBLICO (ESPH), DIRECTAMENTE DE LA CONEXIÓN DE LA CALLE.
- LAS AGUAS PLUVIALES SE DIRIGEN HACIA LA CUNETTA PÚBLICA.
- LAS AGUAS RESIDUALES SE TRATARÁN MEDIANTE TANQUE SÉPTICO Y DRENAJE EN EL PATIO POSTERIOR; DISEÑO Y UBICACIÓN EN LÁMINAS SANITARIAS.
- LA COBERTURA SE CALCULA SOBRE EL ÁREA SEGÚN CATASTRO (256 m²). LOS PATIOS P1 Y P2 SON ABIERTOS DESDE EL NIVEL 1 HASTA EL CIELO Y NO SE CONTABILIZAN EN LA HUELLA.
- PATIOS DE LUZ P1 Y P2 DE 2,50 m DE LADO MÍNIMO, DIMENSIÓN ACEPTADA POR LA MUNICIPALIDAD (ALTURA MEDIDA DESDE EL NIVEL 1).
- NIVEL 3: NPT +6,00 (ALTURA PISO A PISO 3,00 m).
- TRES SUITES CON DORMITORIO Y ESTAR ABIERTOS; SOLO EL BAÑO Y EL WALK-IN SON RECINTOS CERRADOS. BAÑOS DE 1,55 x 2,20 m CON DUCHA, INODORO Y LAVATORIO EN LÍNEA Y PUERTA DE 0,80 m ABATIBLE HACIA EL DORMITORIO.
- ALINEACIÓN DE NÚCLEOS HÚMEDOS: BAÑO DE SUITE 1 SOBRE EL BAÑO DEL NIVEL 2; BAÑO DE SUITE 2 SOBRE LA ZONA HÚMEDA DE LA COCINA; BAÑO DE SUITE 3 SOBRE LA SALA FAMILIAR, CON DUCTO SANITARIO A DEFINIR EN LÁMINAS SANITARIAS.
- PASILLO DE 1,20 m CERRADO HACIA EL PATIO P1 CON VIDRIO FIJO (GALERÍA). BARANDA EN EL BORDE DE LA ESCALERA (VER A11). ACCESOS A LAS SUITES DESDE EL PASILLO (EJES 2, B Y 5).
- VENTANAS HACIA P1 DESFASADAS ENTRE SUITES PARA REDUCIR VISUALES CRUZADAS.
- COLUMNAS SOBRE EL EJE C SEGÚN LÁMINA A2; SECCIONES Y REFUERZO SEGÚN PLANOS ESTRUCTURALES.
- FACHADA FRONTAL: VENTANAS DE PISO A 2,20 m CON PAÑO FIJO INFERIOR HASTA 0,90 m; WALK-IN CON VIDRIOS FIJOS; BAÑO CON VIDRIO ARENADO (VER A5).
- FACHADA POSTERIOR: VENTANAS CON ANTEPECHO COMÚN DE 0,90 m Y DINTEL A 2,20 m, ALINEADAS ENTRE LOS NIVELES 2 Y 3 (VER A5).
- DIMENSIONES Y TIPOS DE PUERTAS Y VENTANAS EN LÁMINA A9.

[PR] = NOTA TOMADA DEL PROYECTO DE REFERENCIA, PENDIENTE DE REVISIÓN.

#### DETALLE EXTRACTOR DE AIRE

BAÑOS - CORTE ESQUEMÁTICO, Esc. S/E

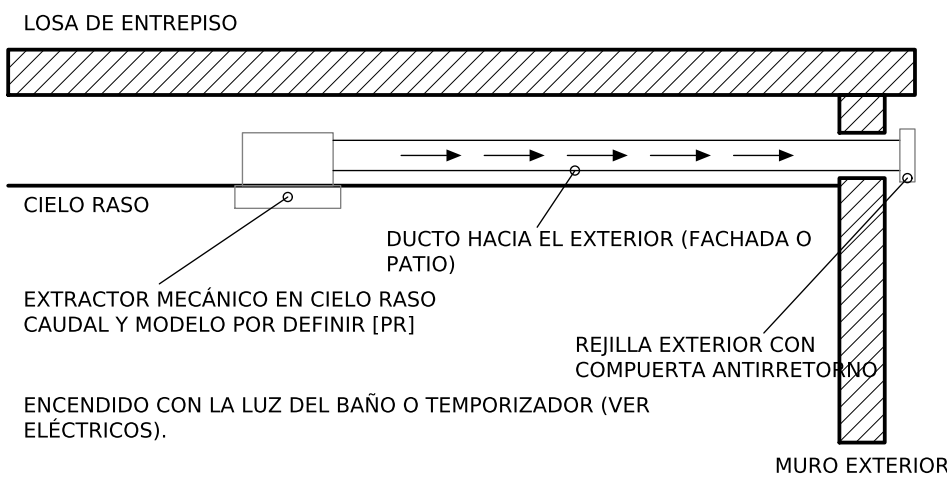

ESPACIO PARA SELLOS Y TIMBRES

CivilCon Diseño y Construcción SRLTDA  
Céd. Jurídica: 3-102-762712

PROFESIONAL RESPONSABLE:  
DIRECTOR TÉCNICO:  
Steven Viales (Civil) IC-40759  
David Barrantes (Electricidad) IE-27499

PROYECTO:  
**VIVIENDA UNIFAMILIAR**  
DISTRITO 03 SANTIAGO, CANTÓN 05 SAN RAFAEL,  
PROVINCIA 04 HEREDIA, COSTA RICA.

INFORMACIÓN REGISTRO PÚBLICO:  
FOLIO REAL: 4-041200-000  
PLANO CATASTRADO: 4-57389-2023  
ÁREA SEGÚN CATASTRO: 256 m²

CONTENIDO:  
**PLANTA NIVEL 3**  
SUITES 1, 2 Y 3.  
DERROTERO.  
CUADRO DE ÁREAS.  
PORCENTAJE DE COBERTURA.  
DETALLE EXTRACTOR DE AIRE.  
NOTAS.

ESCALAS: 1:50 / INDICADAS

| CONTROL DE REVISIONES |            |                                        |
|-----------------------|------------|----------------------------------------|
| REV.                  | FECHA      | DESCRIPCIÓN                            |
| 0                     | 06-10-2026 | VERSIÓN DE TRABAJO PARA REVISIÓN       |
| 1                     | 06-10-2026 | VENTANAS POSTERIORES; BAÑO S3 LIBRA C6 |

ESTADO:  
VERSIÓN DE TRABAJO  
NO APTA PARA CONSTRUCCIÓN NI TRÁMITE

| LUGAR      | LÁMINA   |
|------------|----------|
| COSTA RICA | A4       |
| OCT 2026   | TOTAL -- |