





FACHADA PRINCIPAL (NORTE)
VISTA DESDE LA CALLE
Esc. 1:50

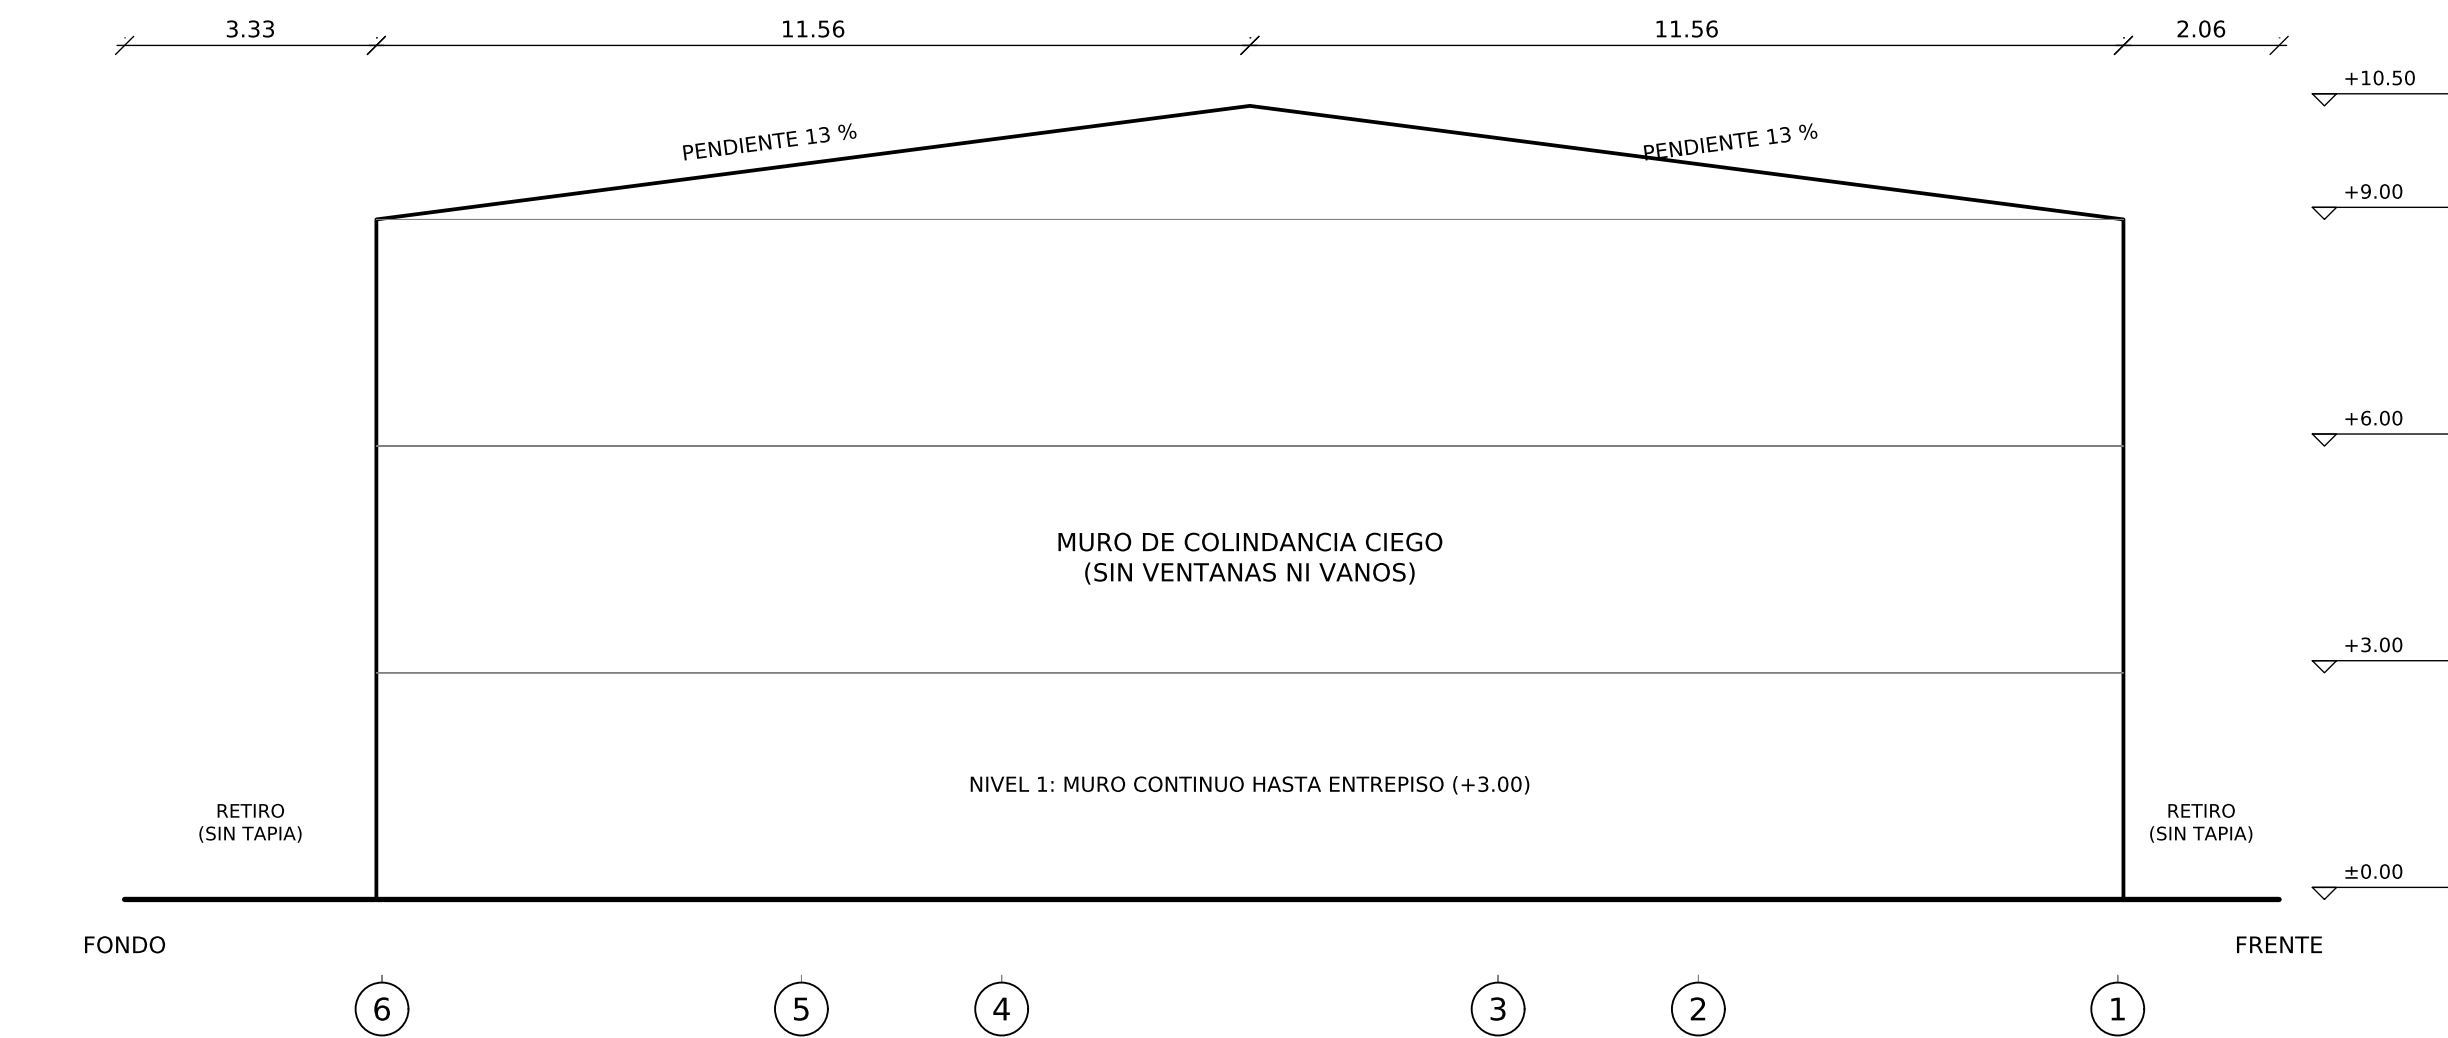

FACHADA LATERAL ESTE
MURO DE COLINDANCIA
Esc. 1:100



FACHADA POSTERIOR (SUR)
VISTA DESDE EL PATIO POSTERIOR
Esc. 1:75

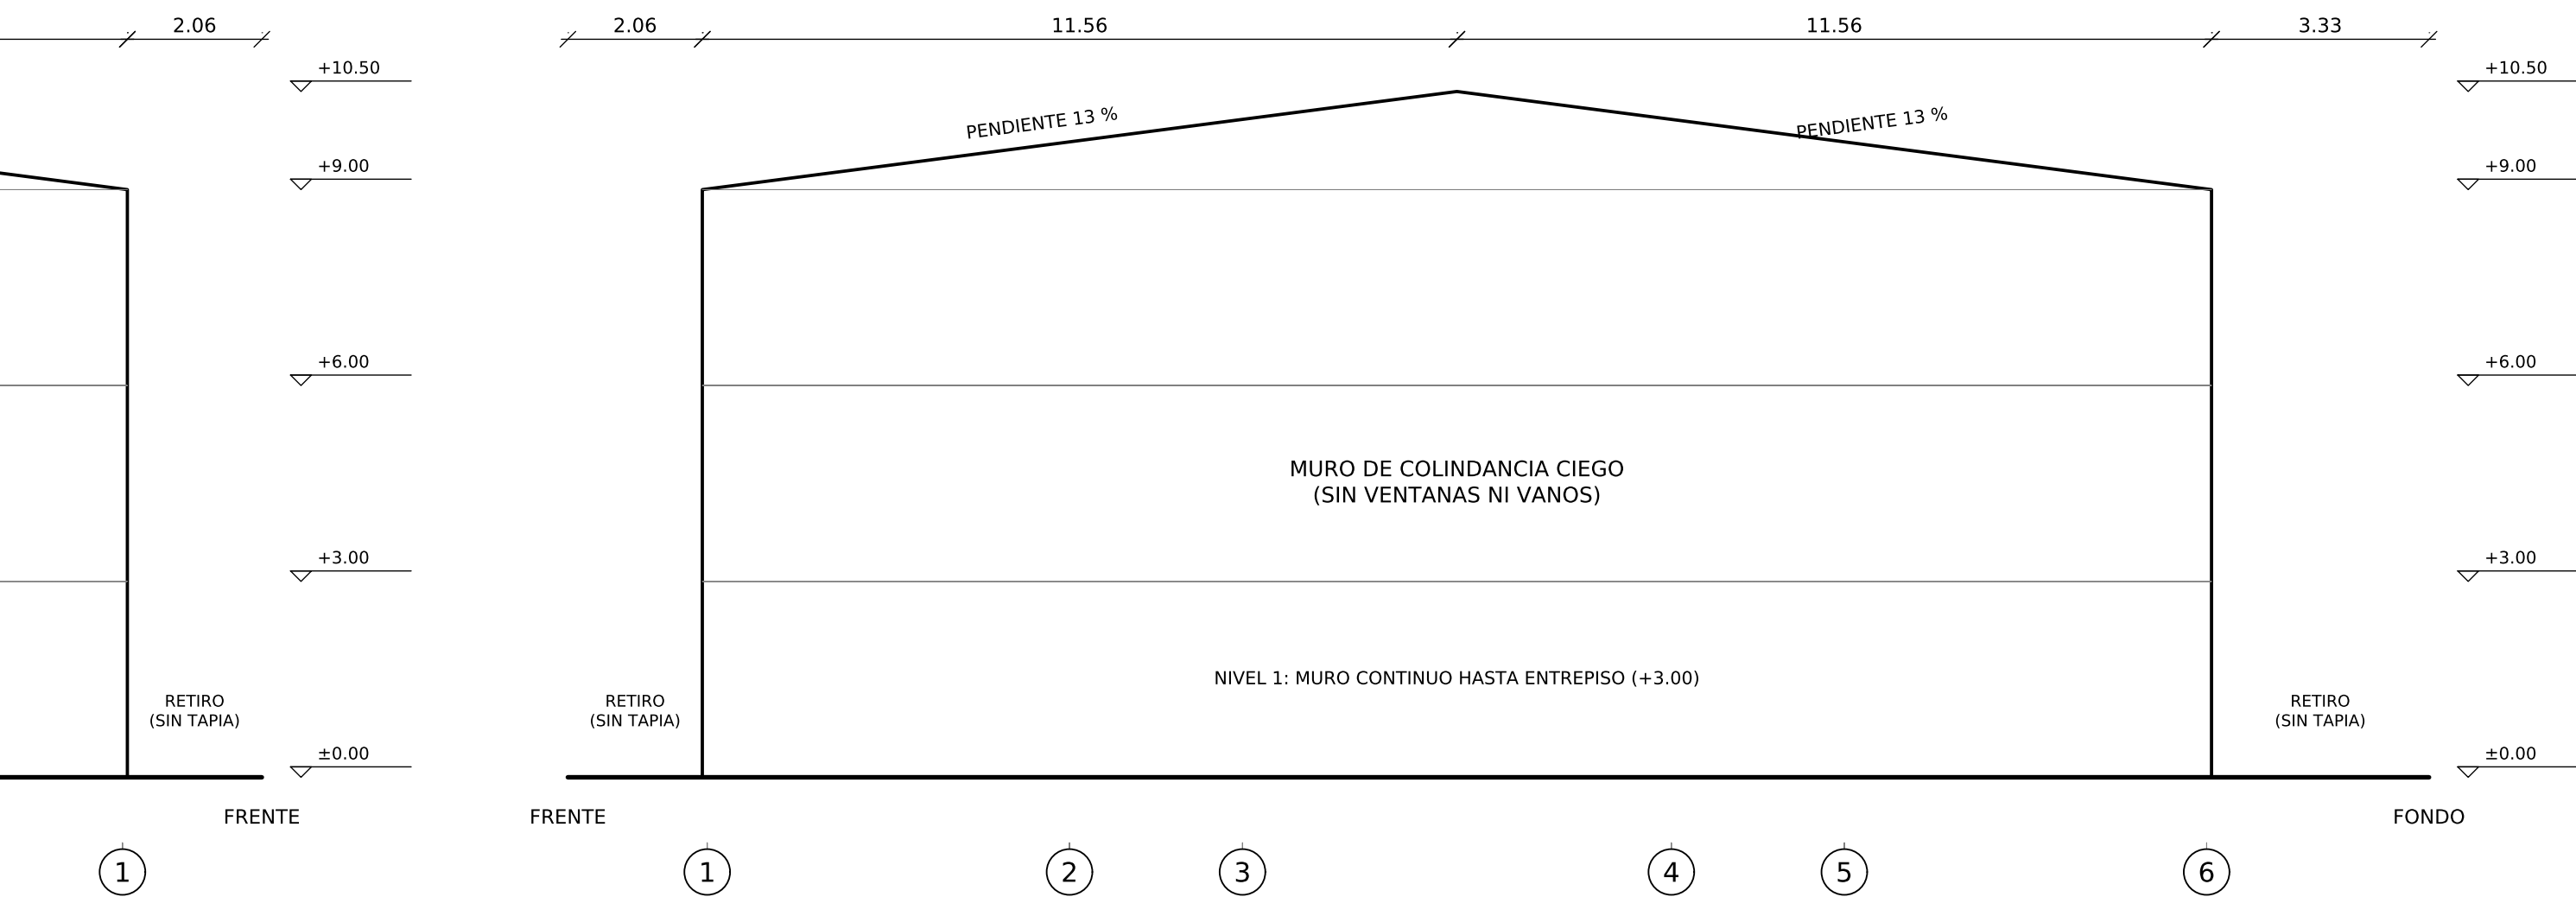

FACHADA LATERAL OESTE
MURO DE COLINDANCIA
Esc. 1:100

NOTAS:

- TODAS LAS MEDIDAS ESTÁN DADAS EN METROS, SALVO INDICACIÓN CONTRARIA. [PR]
- LA TAPIA COLINDANTE DE MAMPOSTERÍA DEBERÁ PROLONGARSE HASTA EL NIVEL DE LA VIGA CORONA DEL ÚLTIMO NIVEL, GARANTIZANDO EL APANTALLAMIENTO VISUAL PERMANENTE HACIA LA PROPIEDAD COLINDANTE.
- LOS BAÑOS CONTARÁN CON EXTRACTOR MECÁNICO DE AIRE.
- NIVELES: NPT N1 ±0.00 (ACERA), N2 +3.00, N3 +6.00; VIGA CORONA Y ARRANQUE DE CUBIERTA +9.00.
- CUBIERTA DE LÁMINA ESTRUCTURAL CALIBRE 26 A DOS AGUAS (HACIA EL FRENTE Y HACIA EL FONDO), PENDIENTE 13 %, CUMBRERA AL CENTRO DE LA VIVIENDA A +10.50 (REFERENCIAL). ESTRUCTURA DE TECHO SEGÚN PLANOS ESTRUCTURALES.
- AGUAS PLUVIALES: CANOA FRONTAL Y CANOA POSTERIOR, CADA UNA CON 2 BAJANTES (UNO EN CADA EXTREMO), CONDUCIDOS HACIA LA CUNETA DEL FRENTE. DIÁMETROS, UBICACIÓN DEFINITIVA Y TRAZADO SEGÚN LÁMINA PLUVIAL.
- FACHADA PRINCIPAL: VENTANAS DE PISO A 2.20 m SOBRE NPT, ALINEADAS ENTRE NIVELES, CON PAÑO FIJO INFERIOR HASTA 0.90 m Y FRANJA OPACA HASTA LA LOSA SUPERIOR (VIGAS).
- VENTANAS DE LOS WALK-IN: VIDRIOS FIJOS.
- BAÑOS: VIDRIO ARENADO (SANDBLAST). EN LA ZONA DE DUCHA EL VIDRIO DEBE QUEDAR SELLADO Y CON ANTEPECHO IMPERMEABLE O PANEL OPACO INTERIOR (POR DEFINIR).
- FACHADA POSTERIOR: ANTEPECHO COMÚN DE 0.90 m Y DINTEL A 2.20 m SOBRE NPT, VENTANAS ALINEADAS ENTRE LOS NIVELES 2 Y 3. LA VENTANA ANGOSTA (3.85 A 4.60) LIBERA LA COLUMNA C6.
- FACHADAS LATERALES: MUROS DE COLINDANCIA CIEGOS, CONTINUOS DESDE EL NIVEL 1 (EN EL NIVEL 1 HASTA EL ENTREPISO +3.00), CON REMATE SUPERIOR SEGÚN LA PENDIENTE DE LA CUBIERTA. NO HAY TAPIAS LATERALES EN LOS RETIROS.
- PORTÓN VEHICULAR Y PUERTA PEATONAL DE 2.40 m DE ALTURA. TIPOS DE VENTANAS Y PUERTAS EN LÁMINAS A7 A A9; ACABADOS DE FACHADA EN LÁMINA A10.
- [PR] = NOTA TOMADA DEL PROYECTO DE REFERENCIA, PENDIENTE DE REVISIÓN.

SIMBOLOGÍA:

- VIDRIO CLARO
- VIDRIO ARENADO (SANDBLAST)
- LÍNEA OCULTA (LOSA / NIVEL)

ESPACIO PARA SELLOS Y TIMBRES

CivilCon Diseño y Construcción SRLTDA
Céd. Jurídica: 3-102-762712

PROFESIONAL RESPONSABLE:
DIRECTOR TÉCNICO:
Steven Viales (Civil) IC-40759
David Barrantes (Electricidad) IE-27499

PROYECTO:
VIVIENDA UNIFAMILIAR
DISTRITO 03 SANTIAGO, CANTÓN 05 SAN RAFAEL,
PROVINCIA 04 HEREDIA, COSTA RICA.

INFORMACIÓN REGISTRO PÚBLICO:
FOLIO REAL: 4-041200-000
PLANO CATASTRADO: 4-57389-2023
ÁREA SEGÚN CATASTRO: 256 m²

CONTENIDO:
FACHADAS
FACHADA PRINCIPAL (NORTE).
FACHADA POSTERIOR (SUR).
FACHADA LATERAL ESTE.
FACHADA LATERAL OESTE.
NOTAS.

ESCALAS: 1:50 / INDICADAS

CONTROL DE REVISIONES		
REV.	FECHA	DESCRIPCIÓN
0	06-10-2026	VERSIÓN DE TRABAJO PARA REVISIÓN
1	06-10-2026	CUBIERTA, VENTANAS POSTERIORES, SIN TAPIAS

ESTADO:
VERSIÓN DE TRABAJO
NO APTA PARA CONSTRUCCIÓN NI TRÁMITE

LUGAR	LÁMINA
COSTA RICA	A5
OCT 2026	TOTAL --