
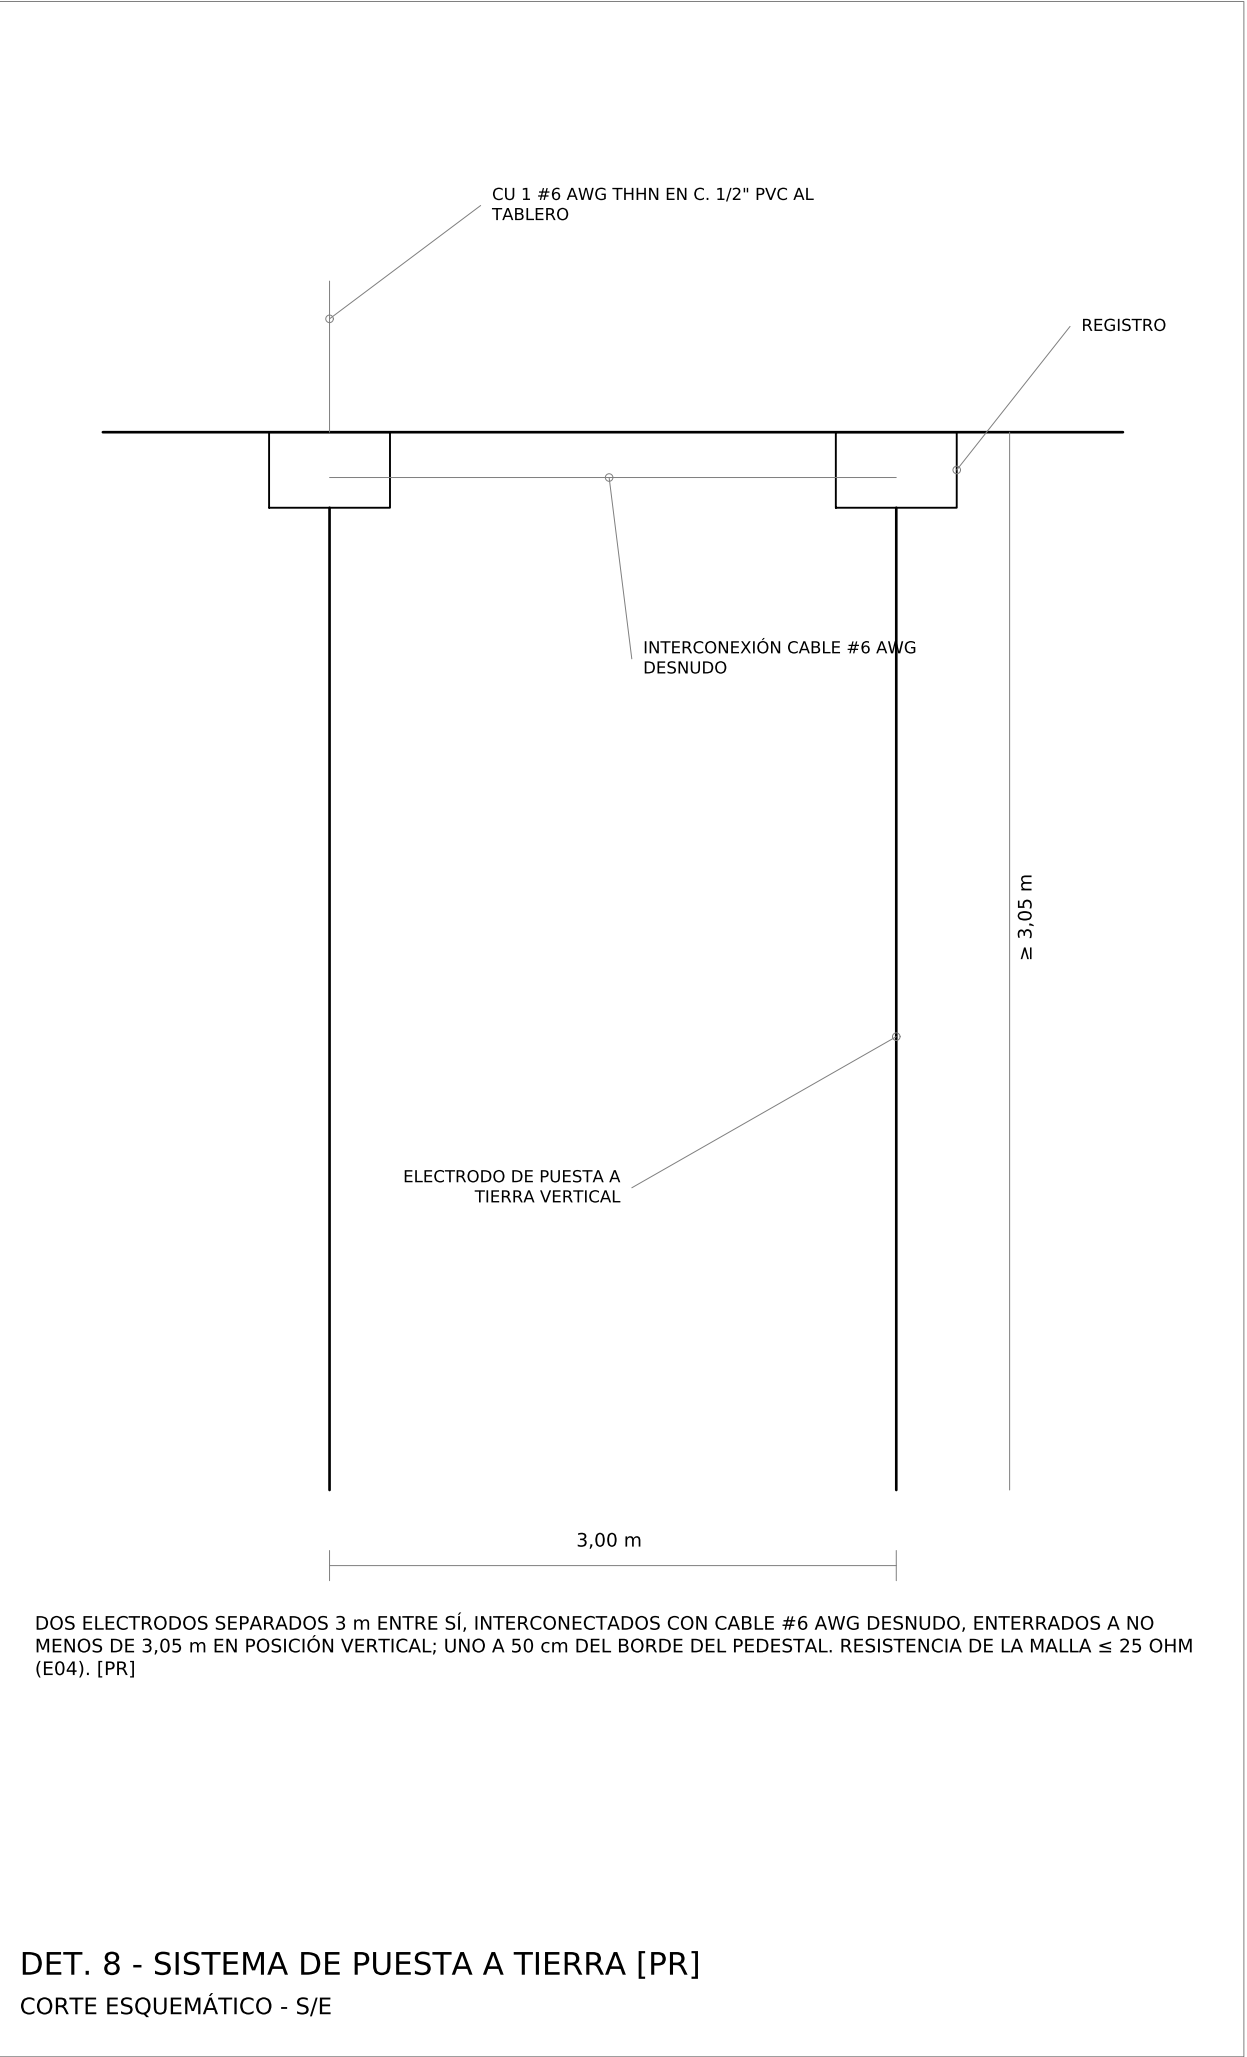
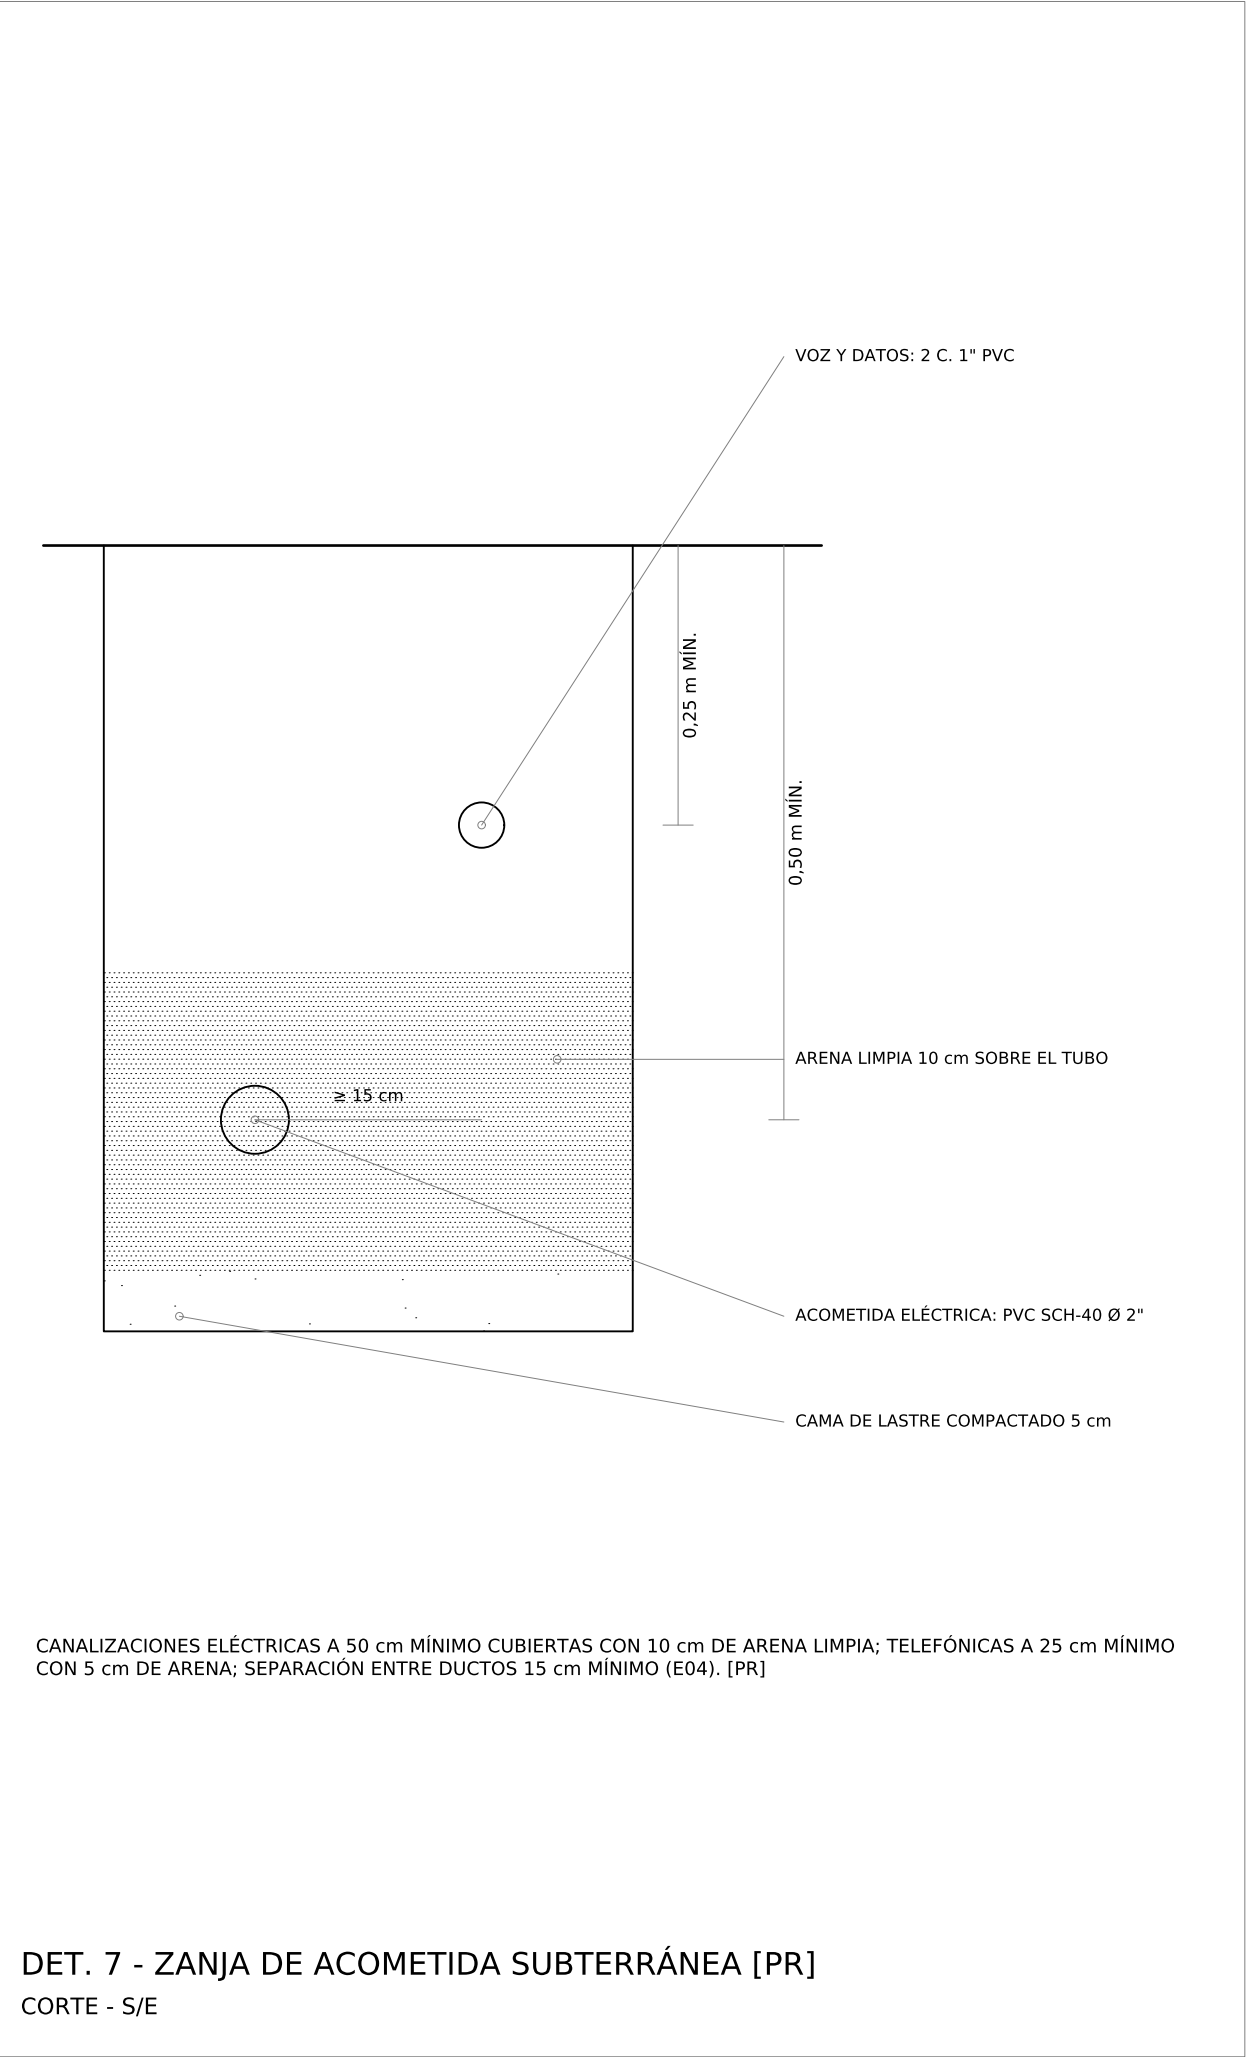
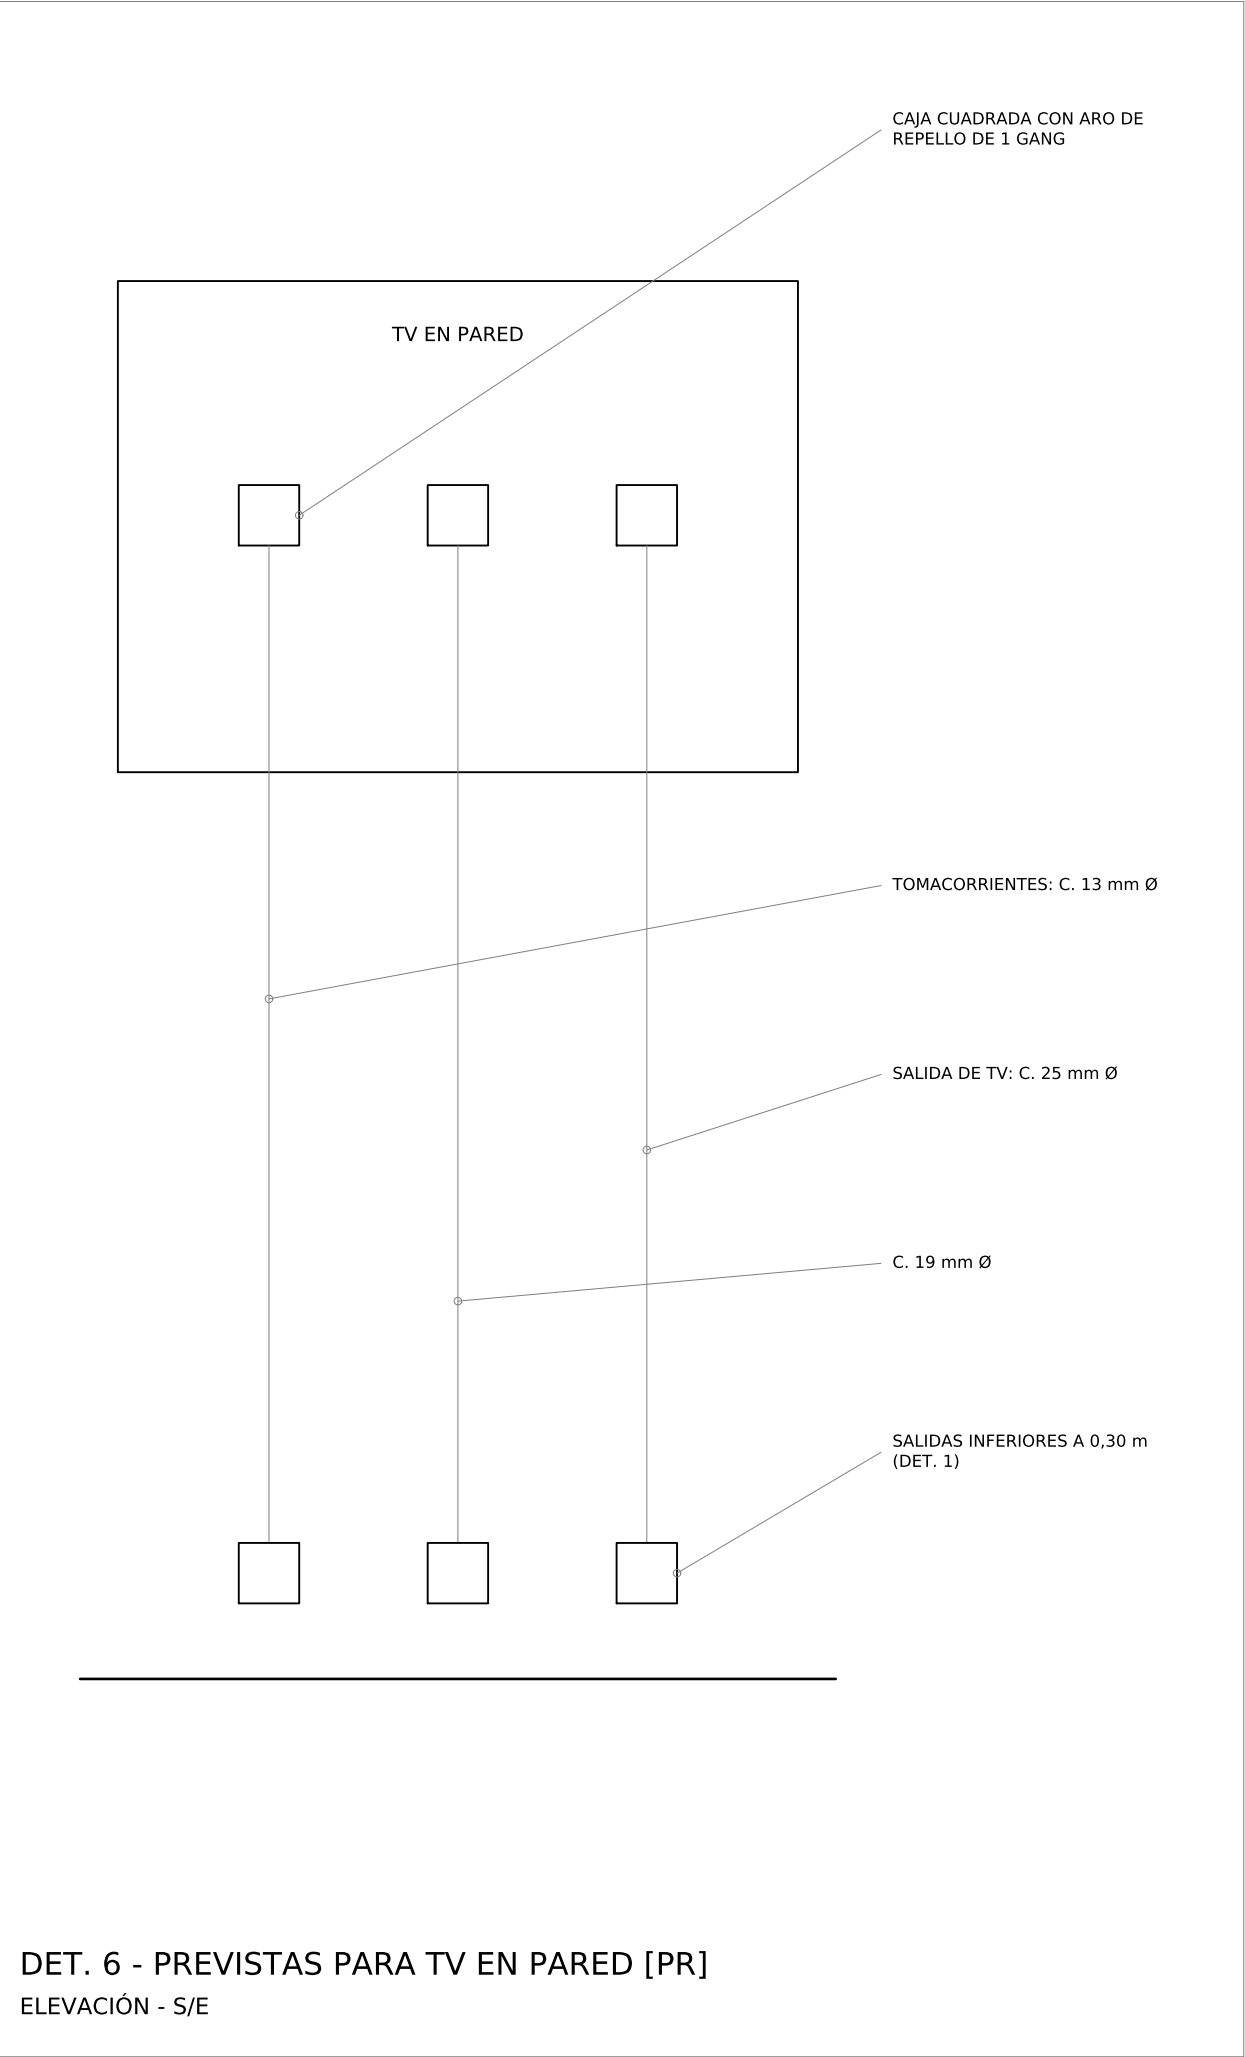
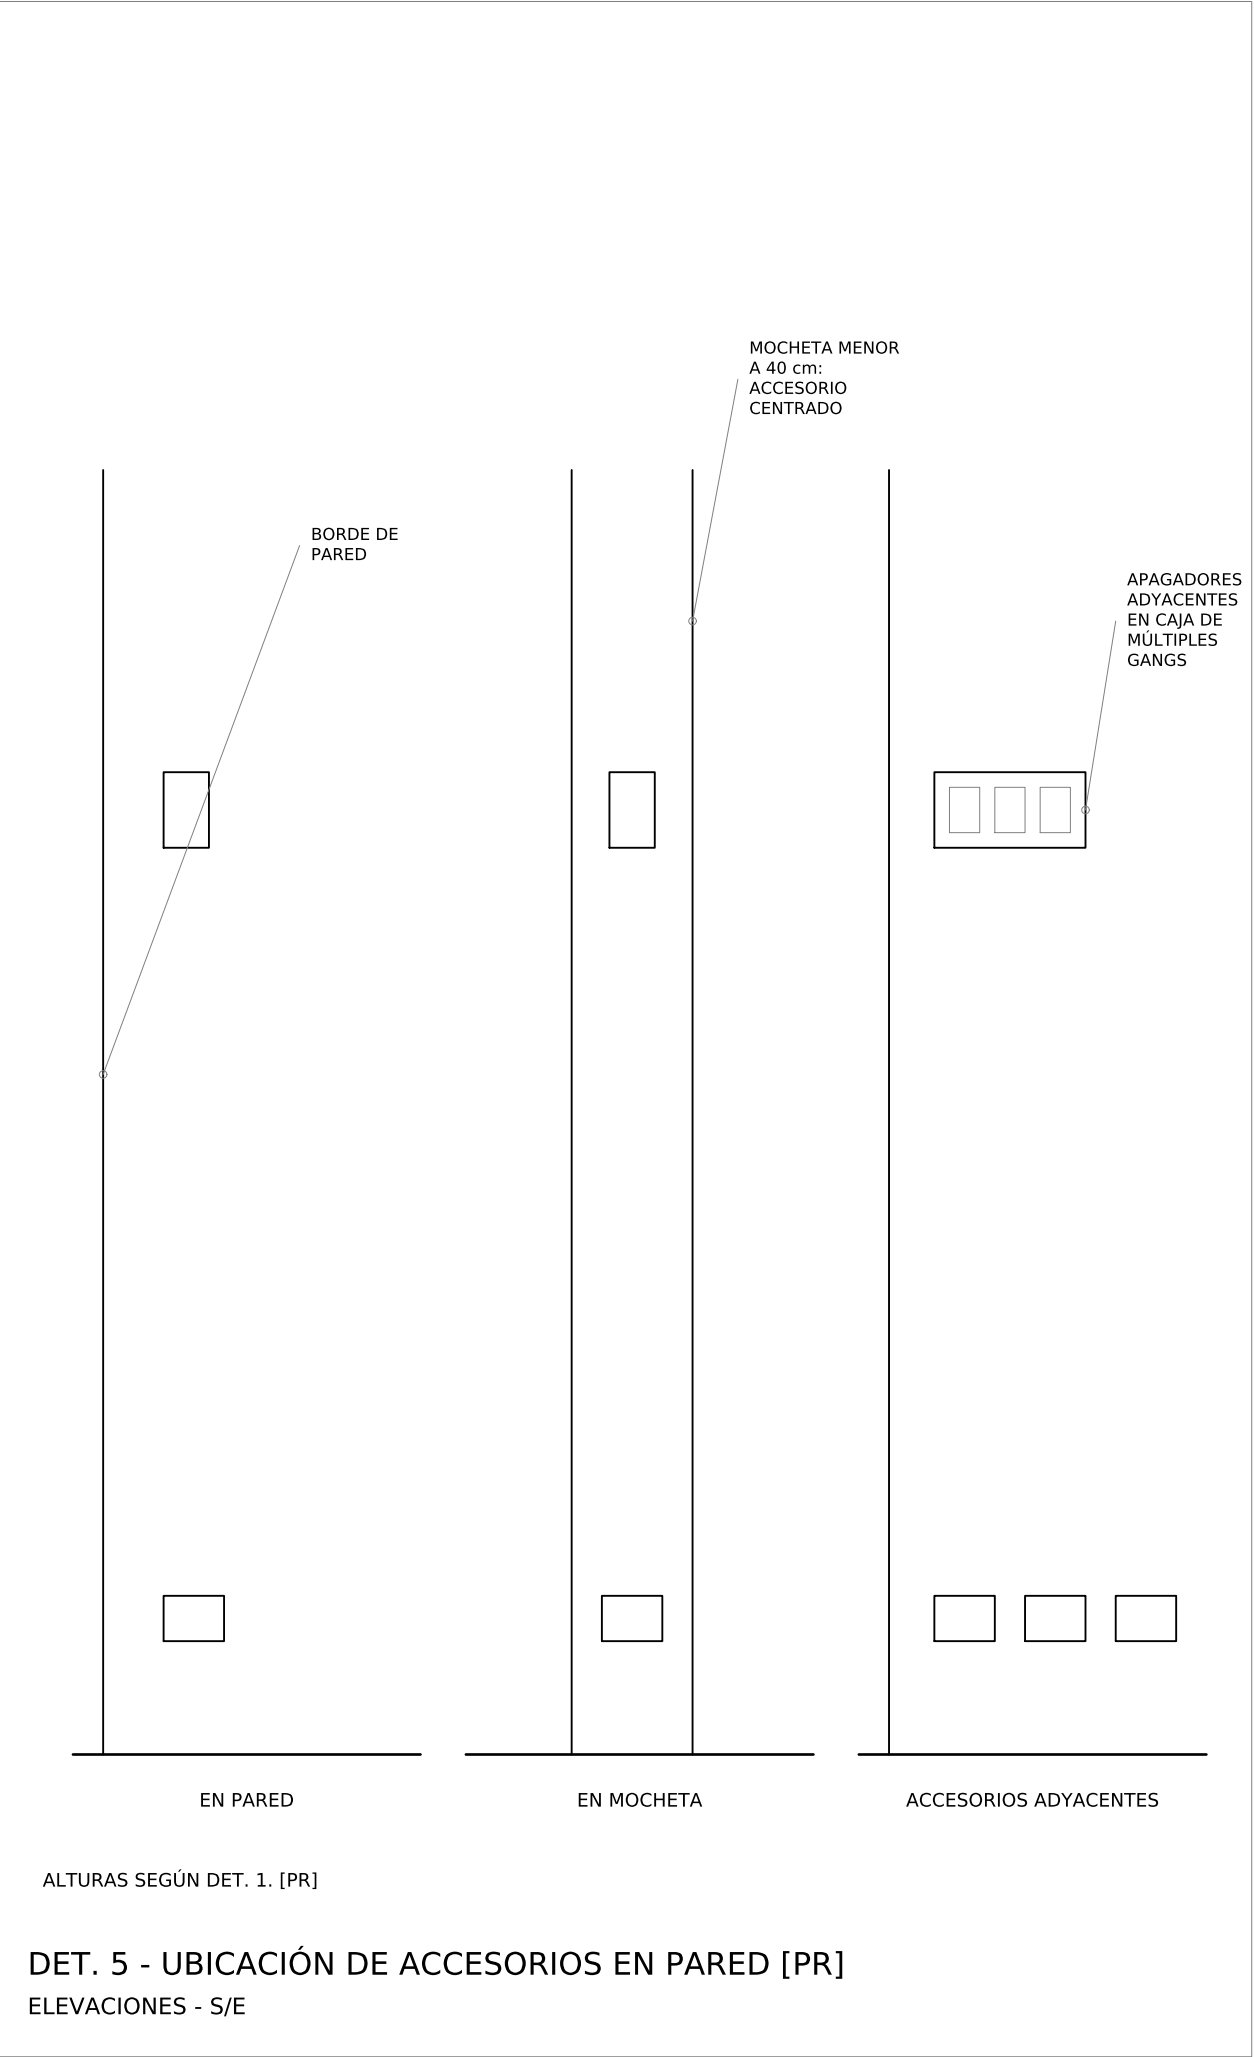
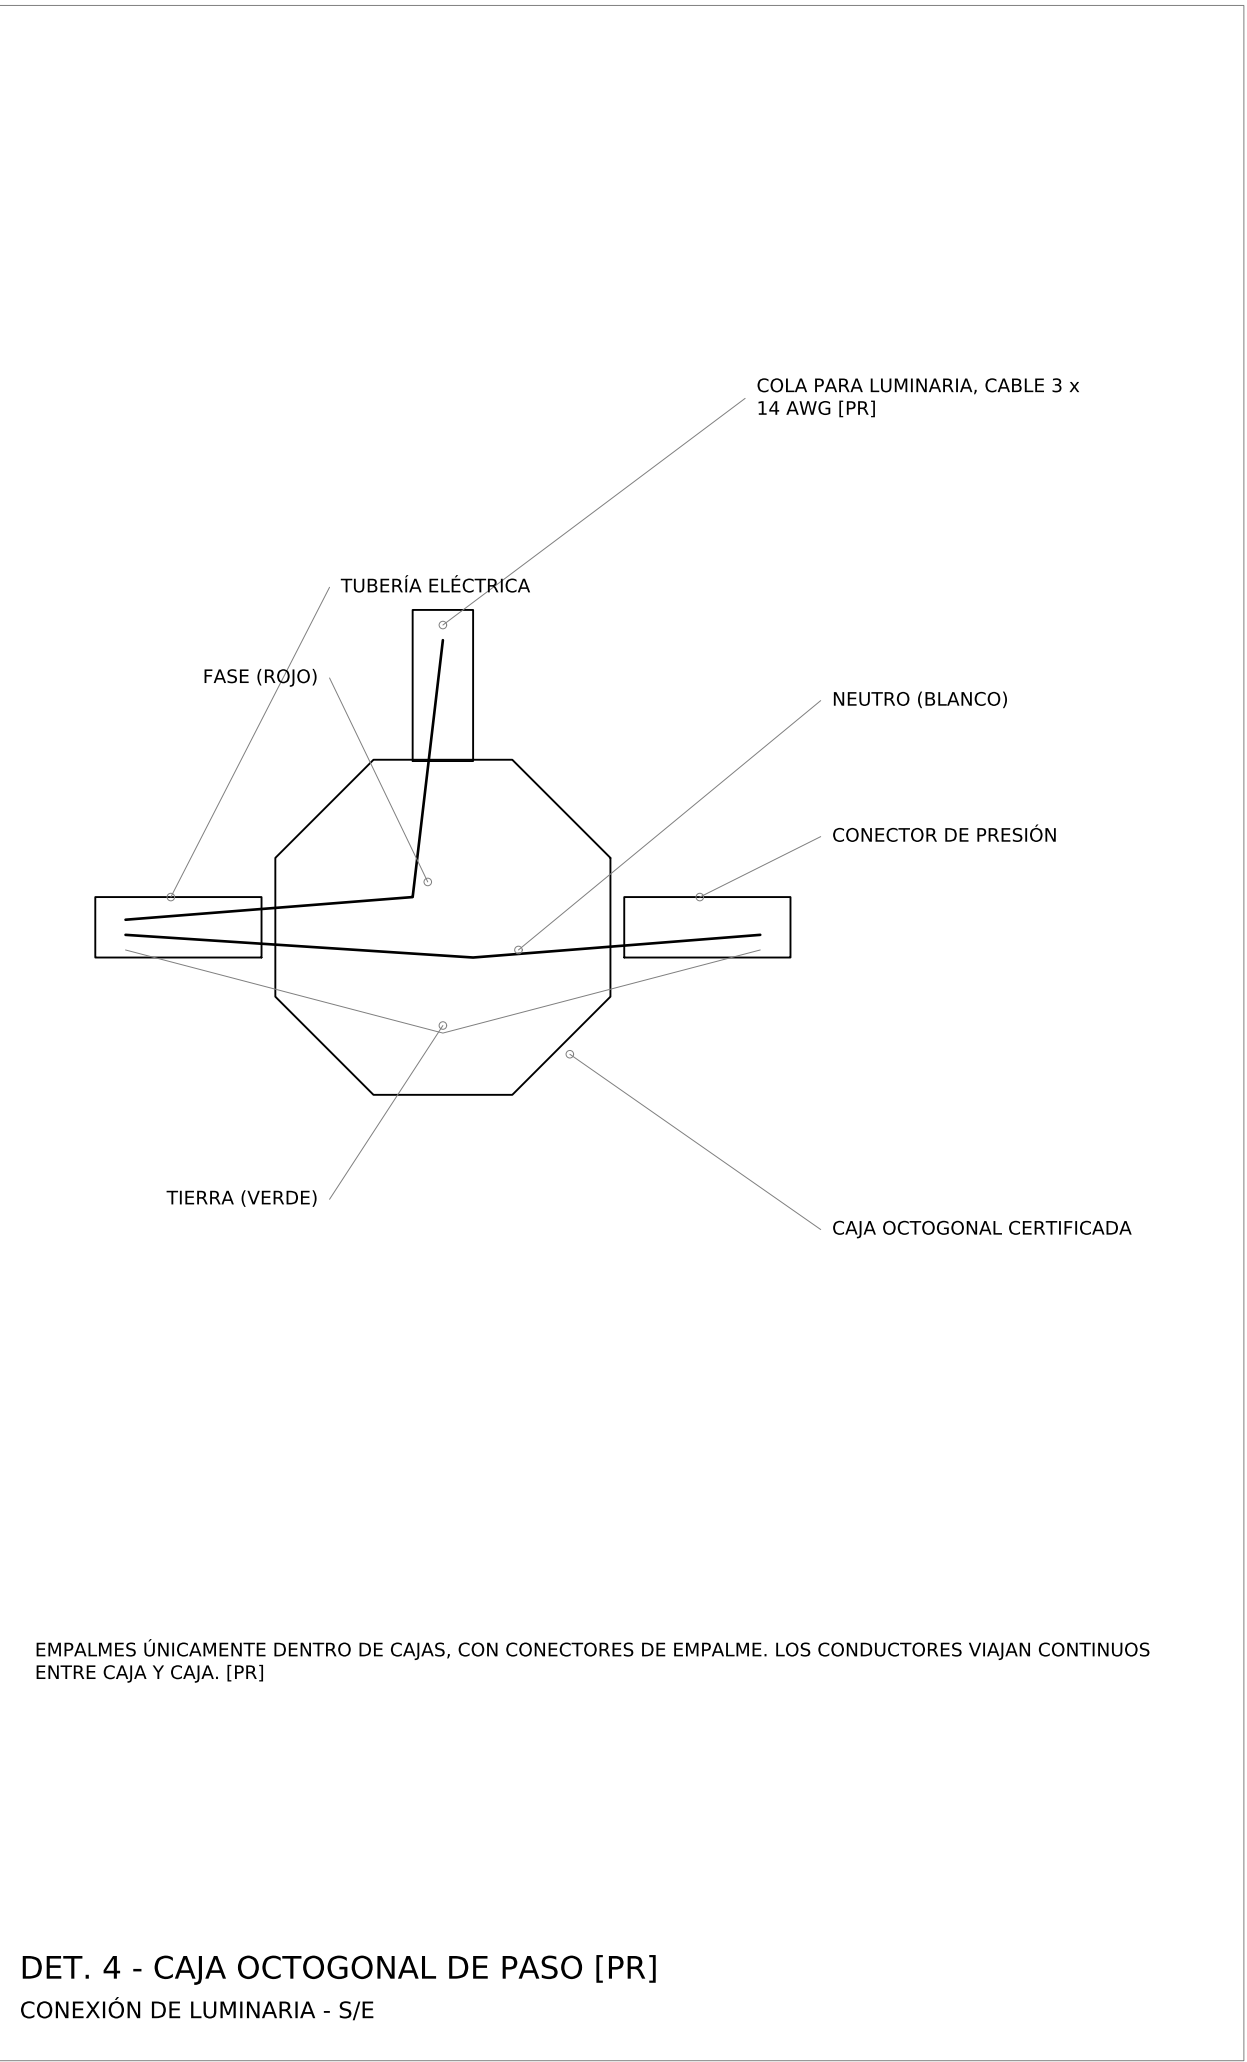
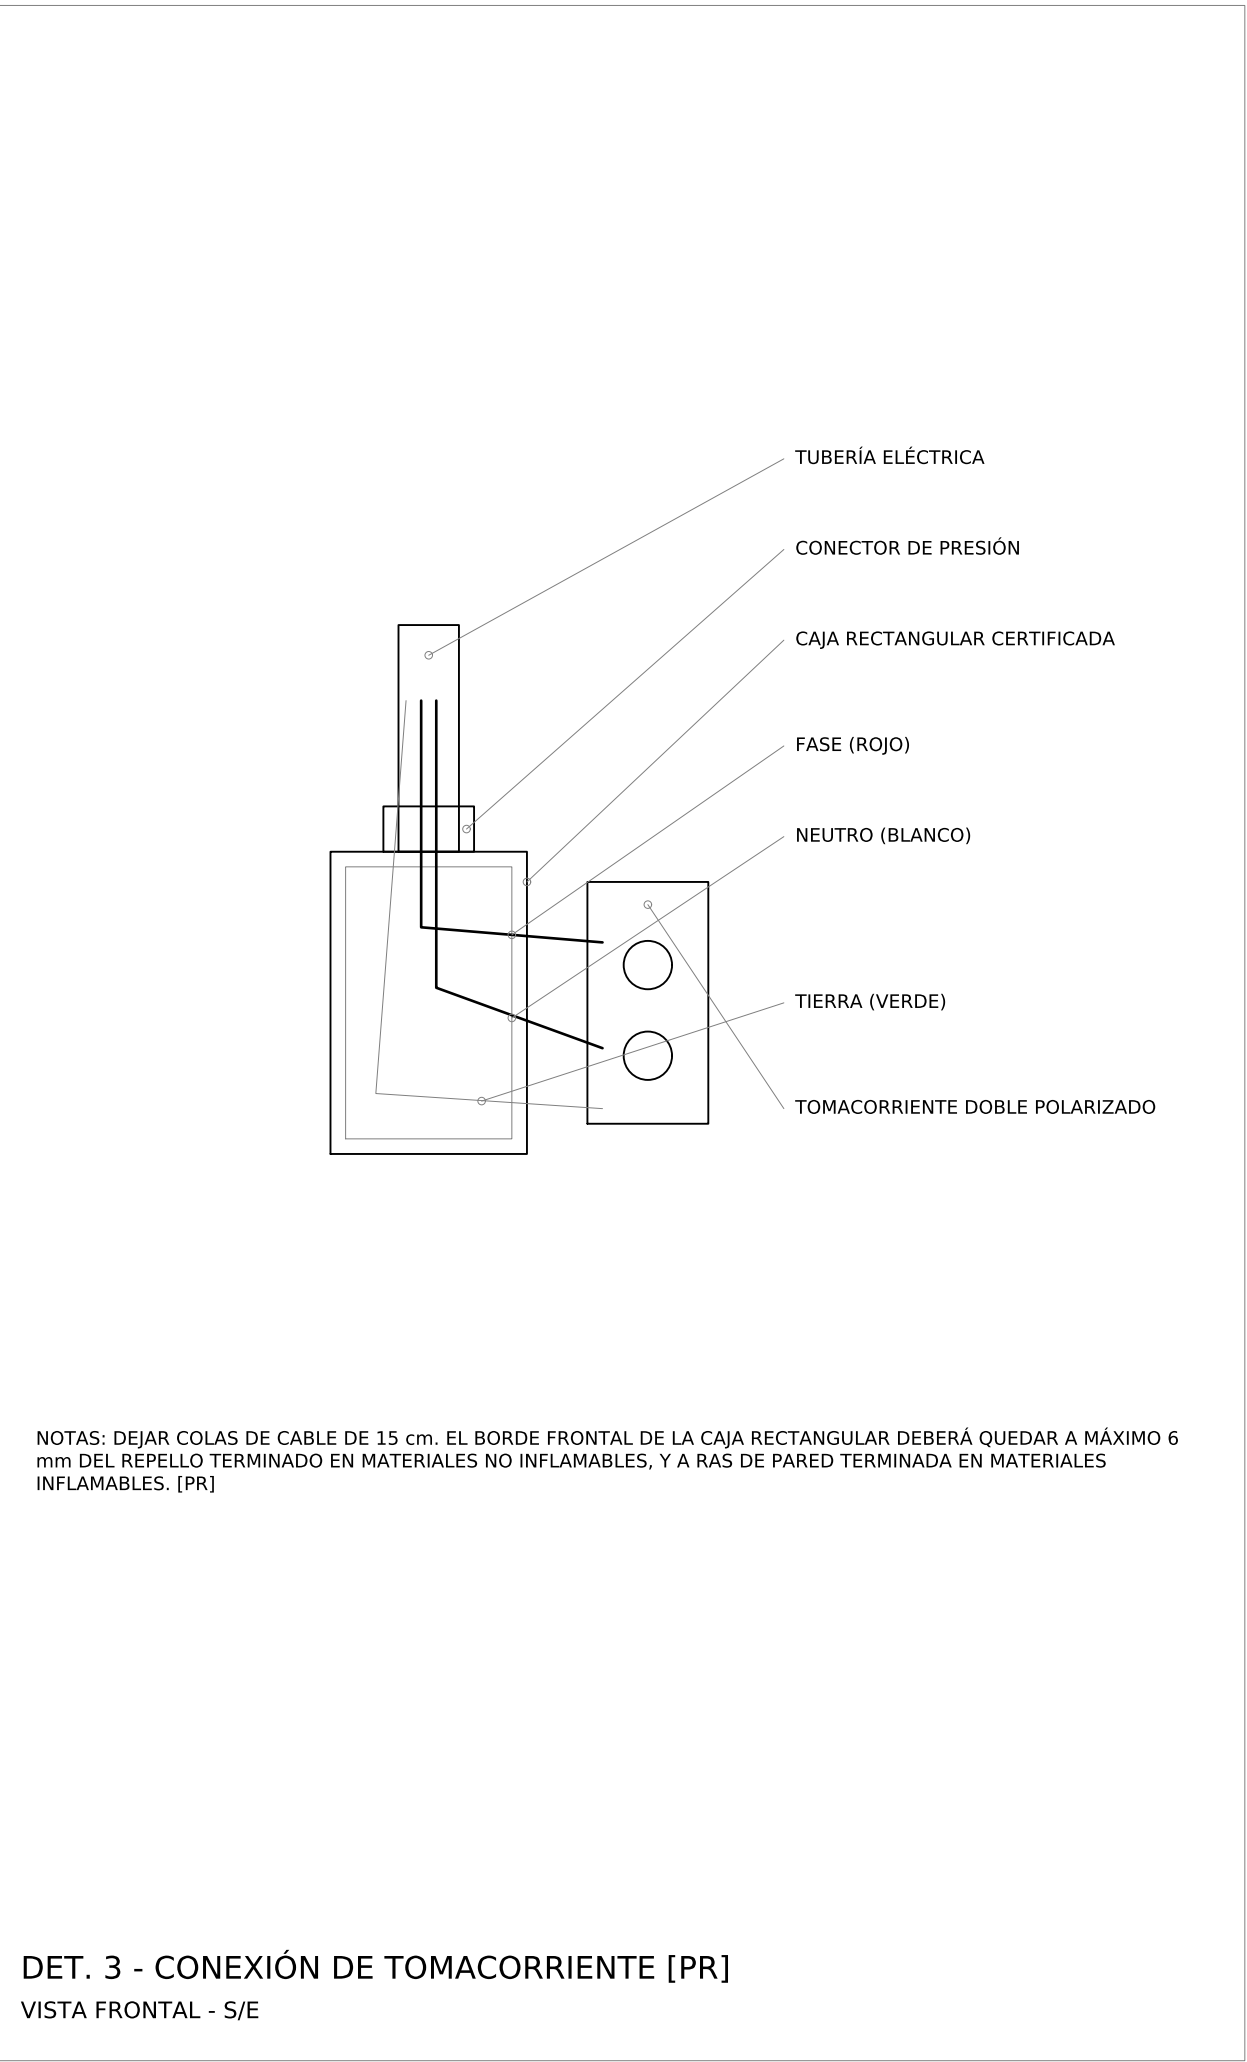
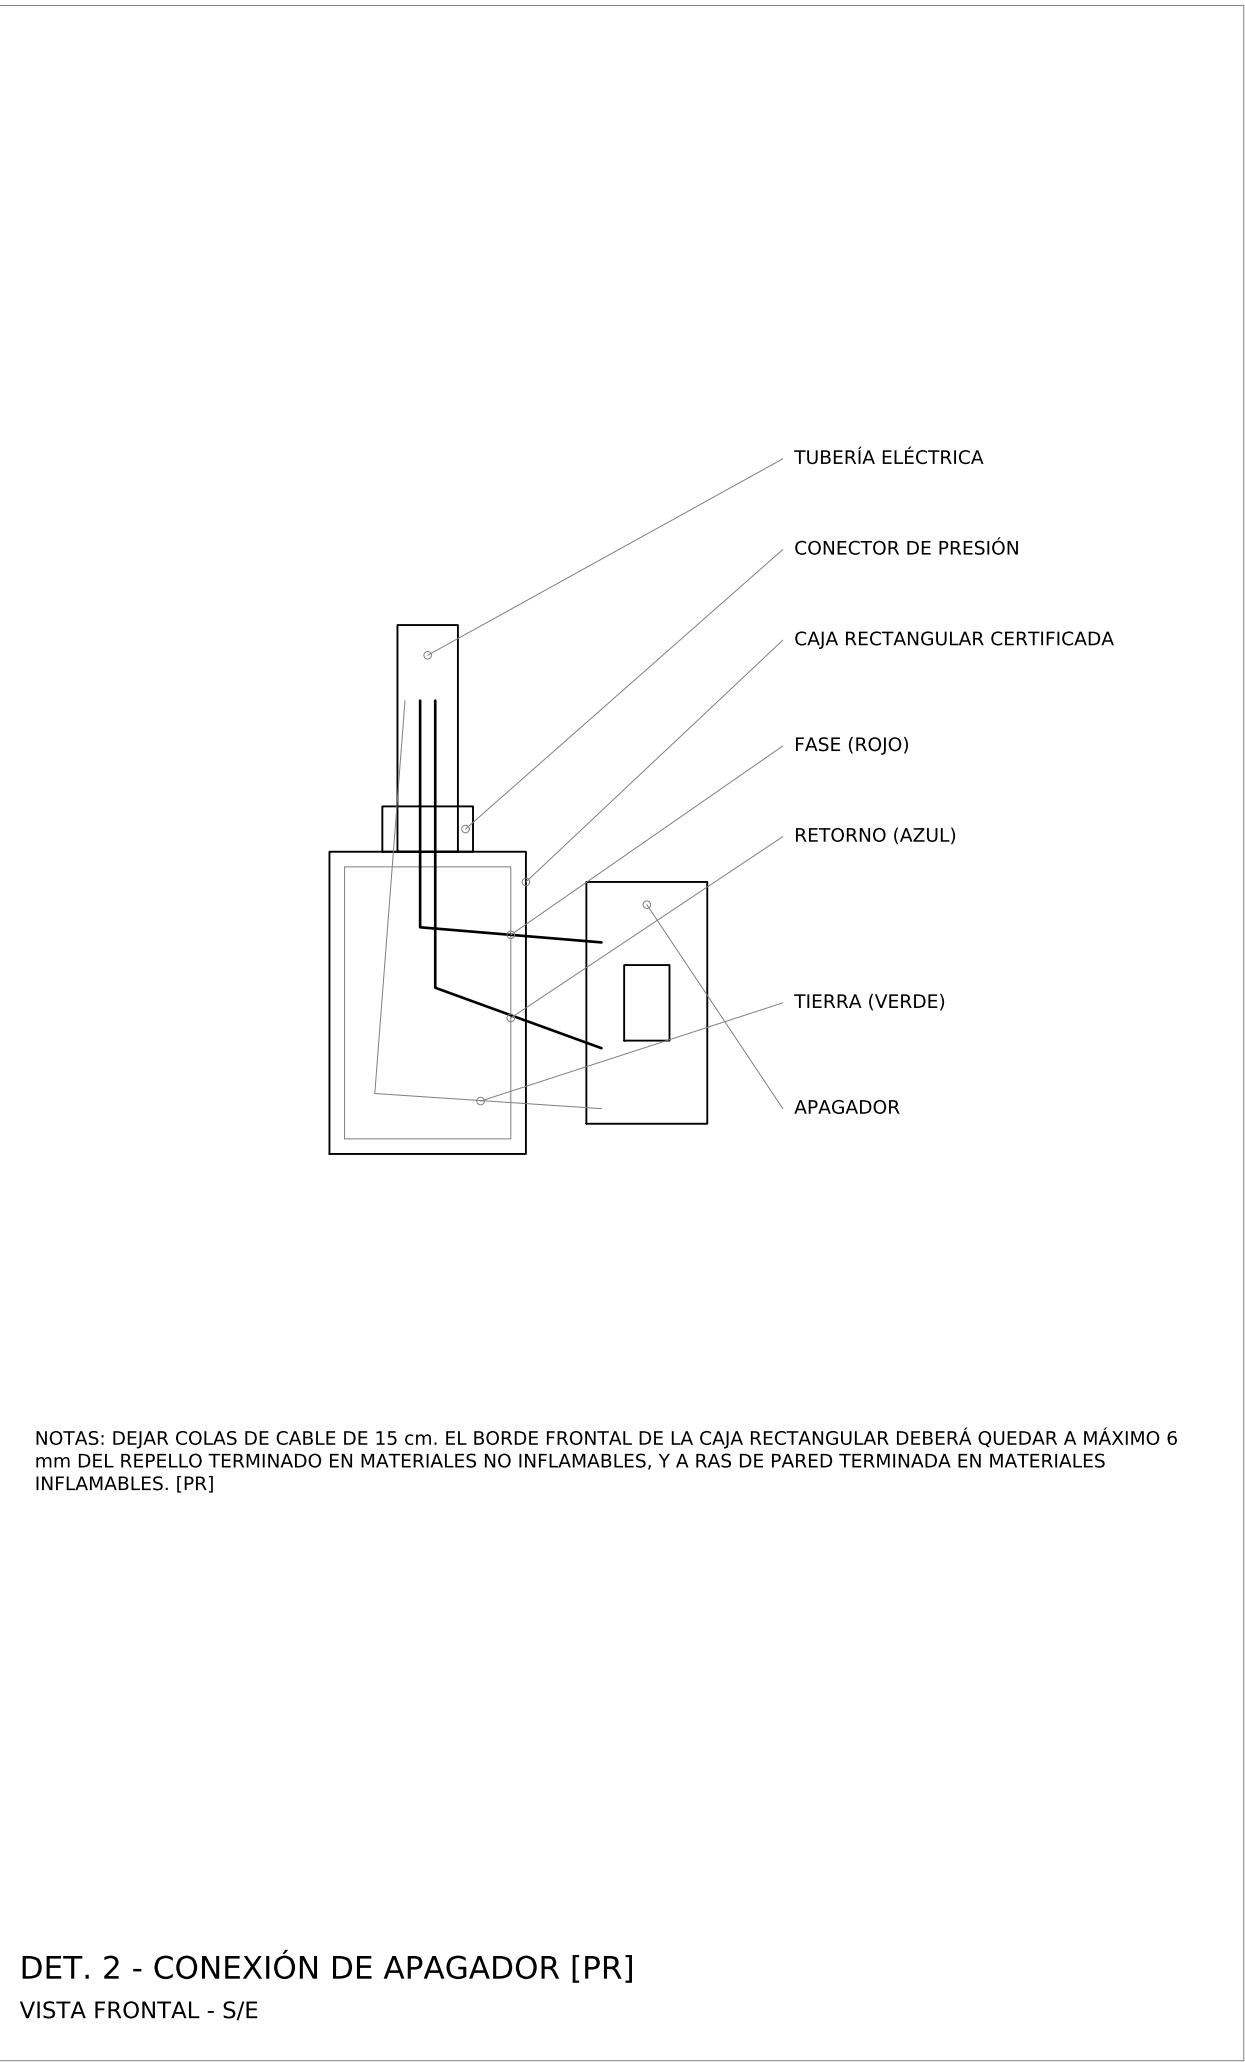


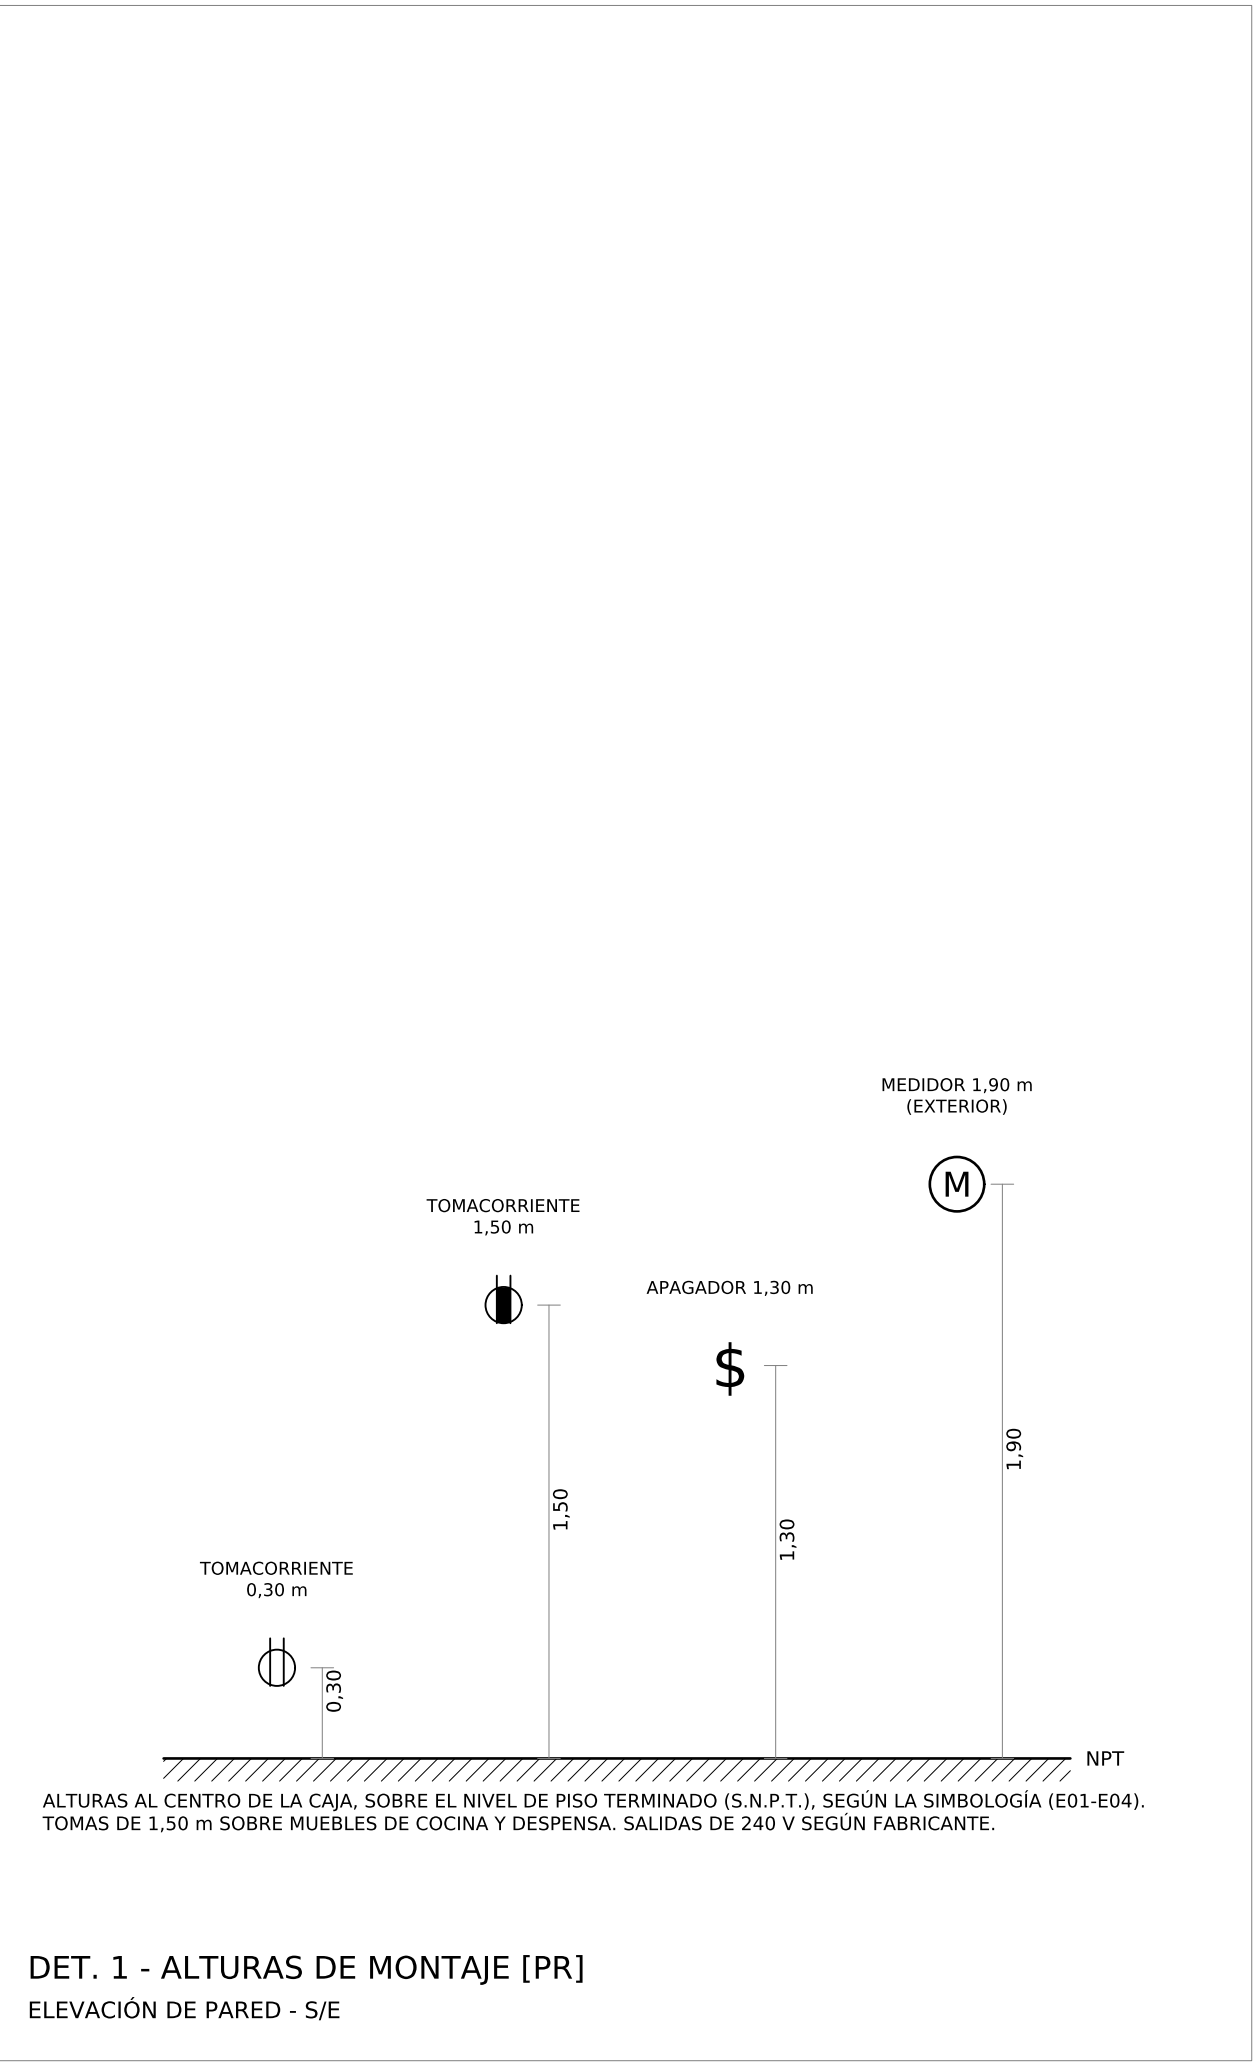

ESPACIO PARA SELLOS Y TIMBRES		
CivilCon Diseño y Construcción SRLTDA Céd. Jurídica: 3-102-762712		
PROFESIONAL RESPONSABLE: DIRECTOR TÉCNICO: Steven Viales (Civil) IC-40759 David Barrantes (Electricidad) IE-27499		
PROYECTO: VIVIENDA UNIFAMILIAR DISTRITO 03 SANTIAGO, CANTÓN 05 SAN RAFAEL, PROVINCIA 04 HEREDIA, COSTA RICA.		
INFORMACIÓN REGISTRO PÚBLICO: FOLIO REAL: 4-041200-000 PLANO CATASTRADO: 4-57389-2023 ÁREA SEGÚN CATASTRO: 256 m²		
CONTENIDO: ELECTRICIDAD DETALLES ELÉCTRICOS. CONEXIONES Y ACCESORIOS. ALTURAS DE MONTAJE. ZANJA DE ACOMETIDA. PUESTA A TIERRA.		
ESCALAS: S/E		
CONTROL DE REVISIONES		
REV.	FECHA	DESCRIPCIÓN
0	06-10-2026	VERSIÓN DE TRABAJO PARA REVISIÓN
ESTADO:		
VERSIÓN DE TRABAJO NO APTA PARA CONSTRUCCIÓN NI TRÁMITE		
LUGAR		LÁMINA
COSTA RICA		E05
OCT 2026		TOTAL --