


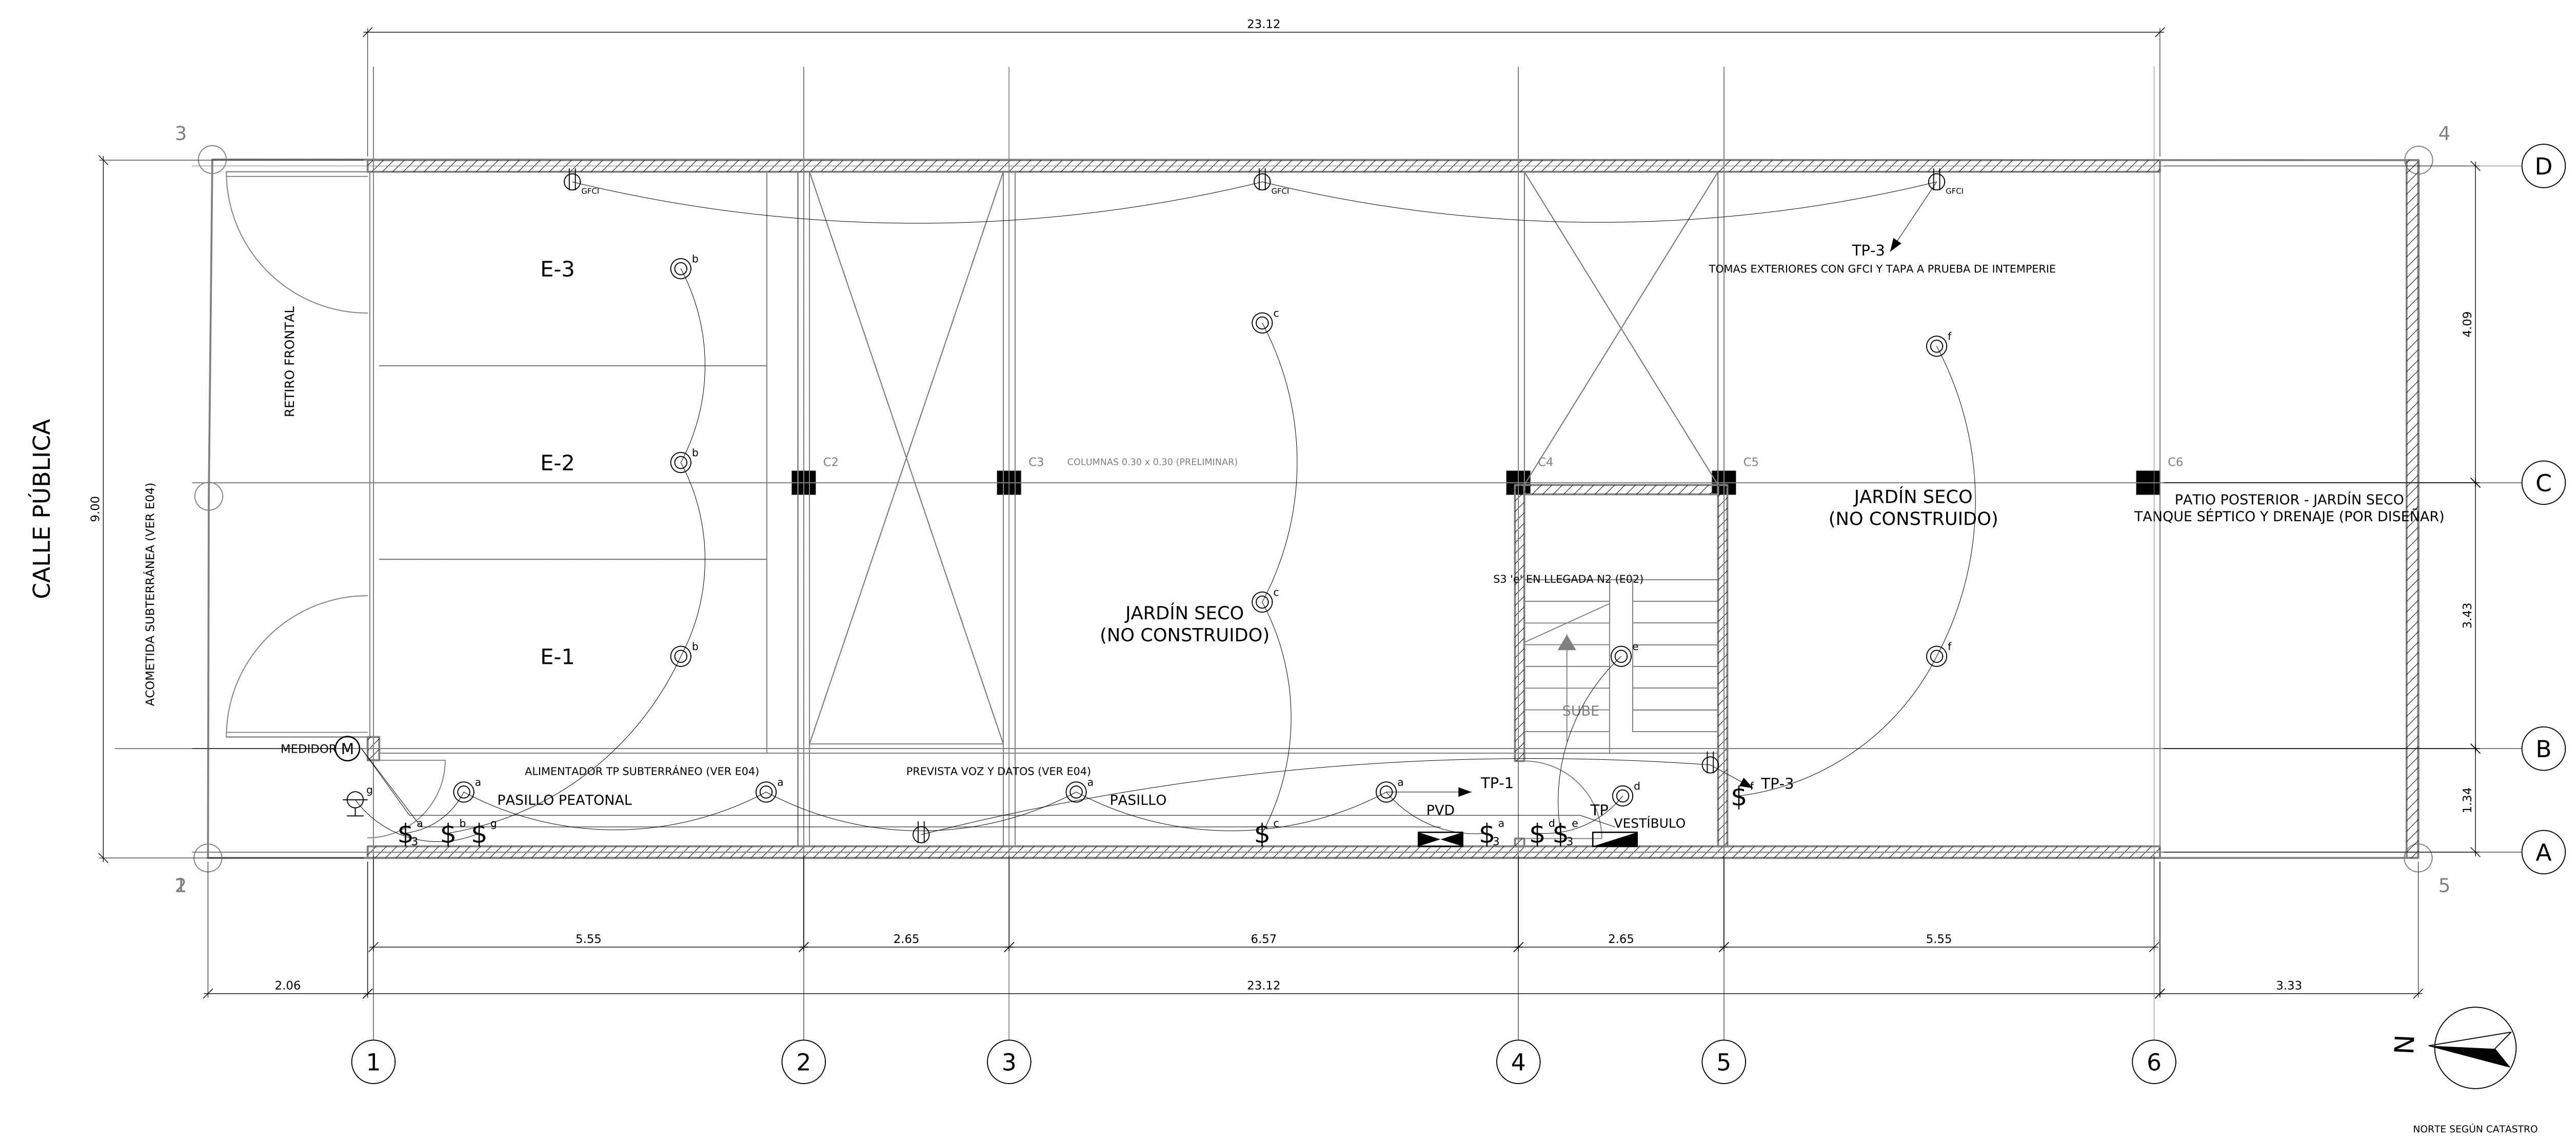

PLANTA ELÉCTRICA NIVEL 1
ILUMINACIÓN, TOMACORRIENTES Y VOZ/DATOS
Esc. 1:50



SIMBOLOGÍA ELÉCTRICA

	MEDIDOR ELÉCTRICO A 1,90 m S.N.P.T. [PR]
	TABLERO DE DISTRIBUCIÓN ELÉCTRICA
	TABLERO DE DISTRIBUCIÓN DE VOZ Y DATOS
	LUMINARIA EN SUPERFICIE DE CIELO
	LUMINARIA EMPOTRADA EN CIELO DE GYPSUM
	LUMINARIA EN PARED (APLIQUE)
	APAGADOR SENCILLO 15 A, 120 V, A 1,30 m S.N.P.T. [PR]
	APAGADOR DE TRES VÍAS 20 A, 120 V, A 1,30 m S.N.P.T. [PR]
	TOMACORRIENTE DOBLE POLARIZADO 120 V, 20 A, A 0,30 m S.N.P.T. [PR]
	TOMACORRIENTE DOBLE POLARIZADO 120 V, 20 A, A 1,50 m S.N.P.T. [PR]
	TOMACORRIENTE DOBLE 120 V, 20 A, CON PROTECCIÓN GFCI [PR]
	SALIDA ESPECIAL 240 V (VER CUADRO DE TABLEROS, E04)
	SALIDA DE TELEVISIÓN
	SALIDA DE VOZ Y DATOS

CIRCUITOS DEL NIVEL 1 (TABLERO TP)

CIRC.	DESCRIPCIÓN	DISYUNTOR	CONDUCTORES THHN [PR]
TP-1	ILUMINACIÓN NIVEL 1 (a-g)	1P-20 A	2 #12 + #12 T
TP-3	TOMACORRIENTES NIVEL 1 (GFCI EN EXTERIOR)	1P-20 A	2 #12 + #12 T

LETRAS a-g: AGRUPACIÓN DE LUMINARIAS POR APAGADOR. ALIMENTADORES DE TN2 Y TN3, SECADORA Y DEMÁS CIRCUITOS DEL TP: VER E04.

NOTAS:

- 1.- TODAS LAS MEDIDAS ESTÁN DADAS EN METROS. [PR]
 - 2.- LAS MEDIDAS DEBEN SER VERIFICADAS EN SITIO. [PR]
 - 3.- TODA LA INSTALACIÓN SE REALIZARÁ EN TUBERÍA SEGÚN SE INDICA EN EL TABLERO. EN EL NIVEL 1 (ESTRUCTURA EXPUESTA, SIN CIELO) LA TUBERÍA EXPUESTA A MENOS DE 2,5 m DE ALTURA SERÁ METÁLICA (EMT). [PR]
 - 4.- TODAS LAS SALIDAS, TANTO ELÉCTRICAS COMO DE TV Y DATOS, SERÁN POR MEDIO DE CAJAS DE CONEXIÓN RECTANGULARES U OCTOGONALES CON SUS RESPECTIVAS TAPAS. [PR]
 - 5.- SE IDENTIFICARÁN EN EL TABLERO LOS DIFERENTES CIRCUITOS Y SE DEJARÁN AL MENOS DOS TUBOS PREVISTOS COMO ADICIONALES. [PR]
 - 6.- TOMACORRIENTES EN ESTACIONAMIENTOS Y EXTERIORES CON PROTECCIÓN GFCI Y TAPA A PRUEBA DE INTEMPERIE.
 - 7.- UBICACIÓN EXACTA DEL MEDIDOR SEGÚN LA EMPRESA DISTRIBUIDORA (PD). DIAGRAMA UNIFILAR, CUADROS DE TABLEROS, NOTAS GENERALES Y DETALLES EN LA LÁMINA E04.
- [PR] = NOTA TOMADA DEL PROYECTO DE REFERENCIA, PENDIENTE DE REVISIÓN.

ESPACIO PARA SELLOS Y TIMBRES

CivilCon Diseño y Construcción SRLTDA
Céd. Jurídica: 3-102-762712

PROFESIONAL RESPONSABLE:
DIRECTOR TÉCNICO:
Steven Viales (Civil) IC-40759
David Barrantes (Electricidad) IE-27499

PROYECTO:
VIVIENDA UNIFAMILIAR
DISTRITO 03 SANTIAGO, CANTÓN 05 SAN RAFAEL,
PROVINCIA 04 HEREDIA, COSTA RICA.

INFORMACIÓN REGISTRO PÚBLICO:
FOLIO REAL: 4-041200-000
PLANO CATASTRADO: 4-57389-2023
ÁREA SEGÚN CATASTRO: 256 m²

CONTENIDO:
ELECTRICIDAD
PLANTA ELÉCTRICA NIVEL 1.
ILUMINACIÓN Y TOMACORRIENTES.
VOZ Y DATOS.
SIMBOLOGÍA.
NOTAS.

ESCALAS: 1:50

CONTROL DE REVISIONES

REV.	FECHA	DESCRIPCIÓN
0	06-10-2026	VERSIÓN DE TRABAJO PARA REVISIÓN

ESTADO:

VERSIÓN DE TRABAJO
NO APTA PARA CONSTRUCCIÓN NI TRÁMITE

LUGAR	LÁMINA
COSTA RICA	E01
OCT 2026	TOTAL --