




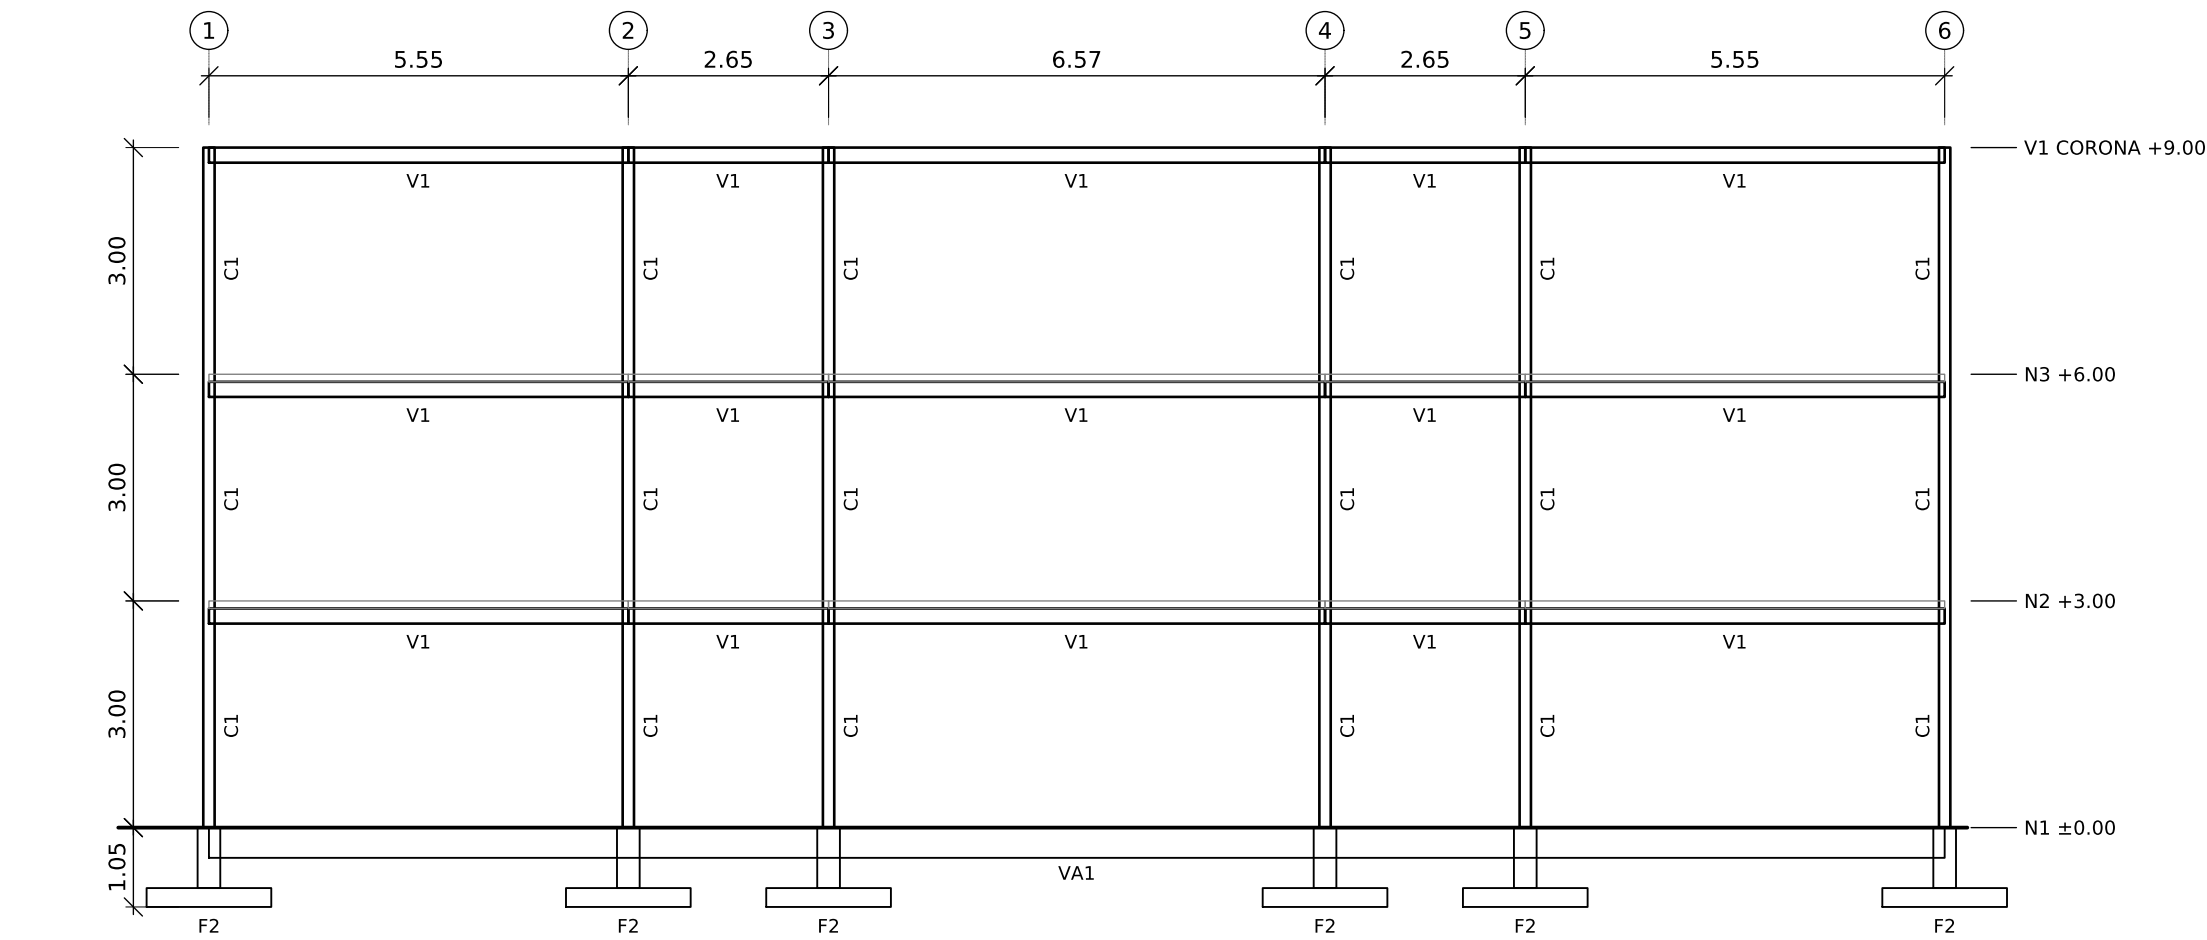


PÓRTICOS A Y D
EJES 1 A 6 (COLINDANCIAS) - Esc. 1:100

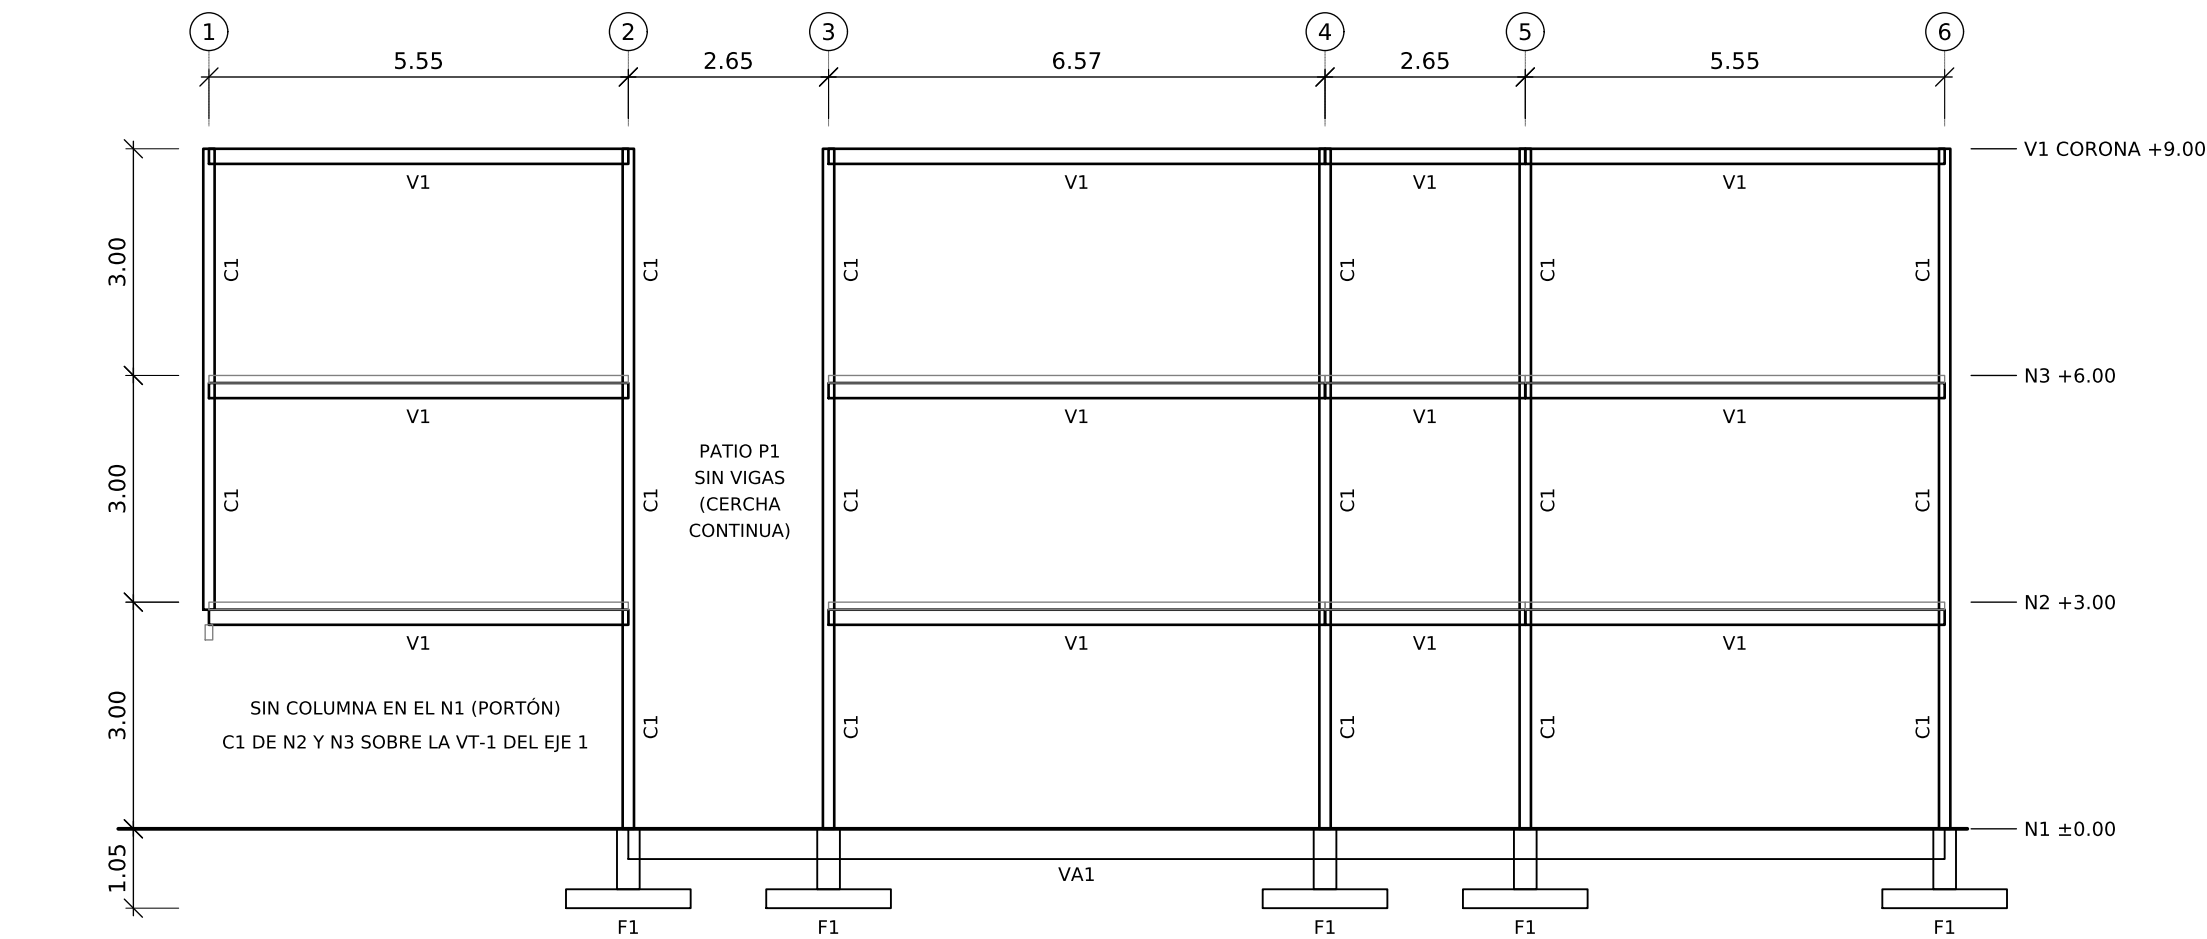

PÓRTICO C
EJES 1 A 6 (COLUMNAS FORRADAS A 0,30 x 0,30) - Esc. 1:100

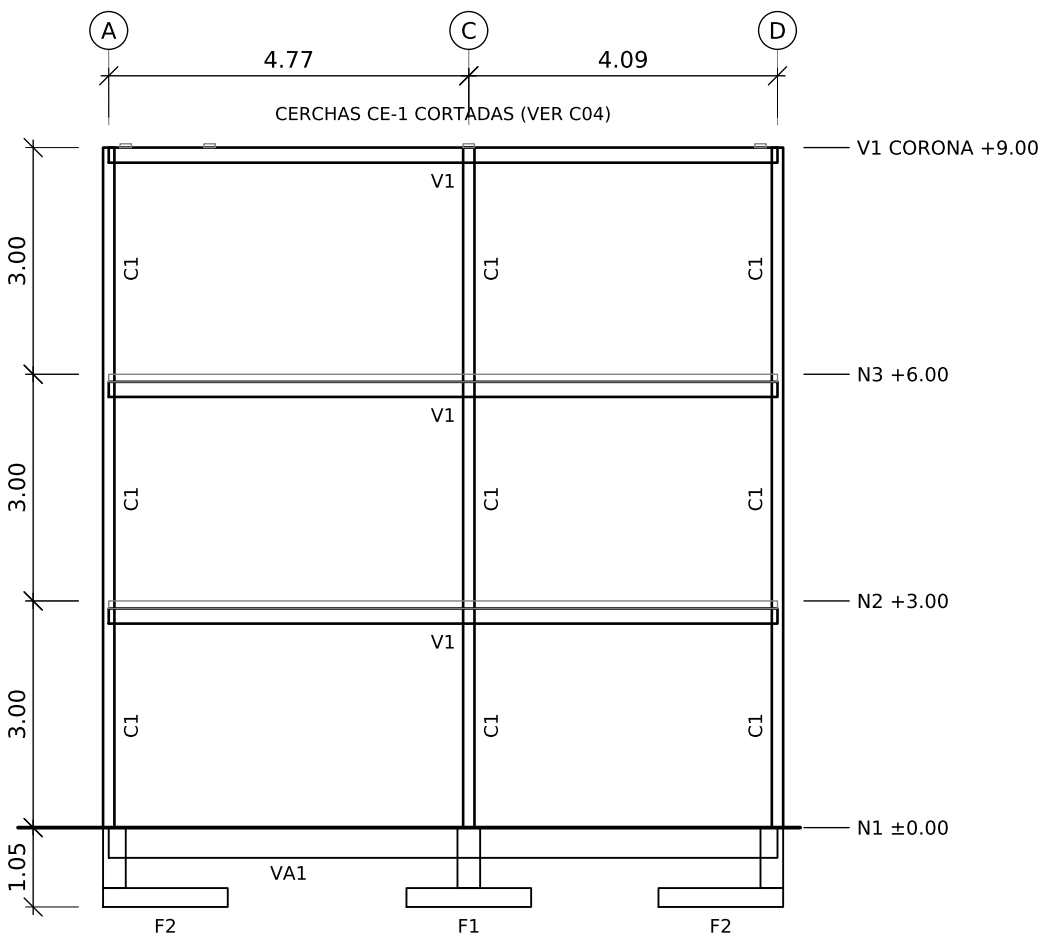

PÓRTICOS 2 A 6
EJES A, C Y D - Esc. 1:100

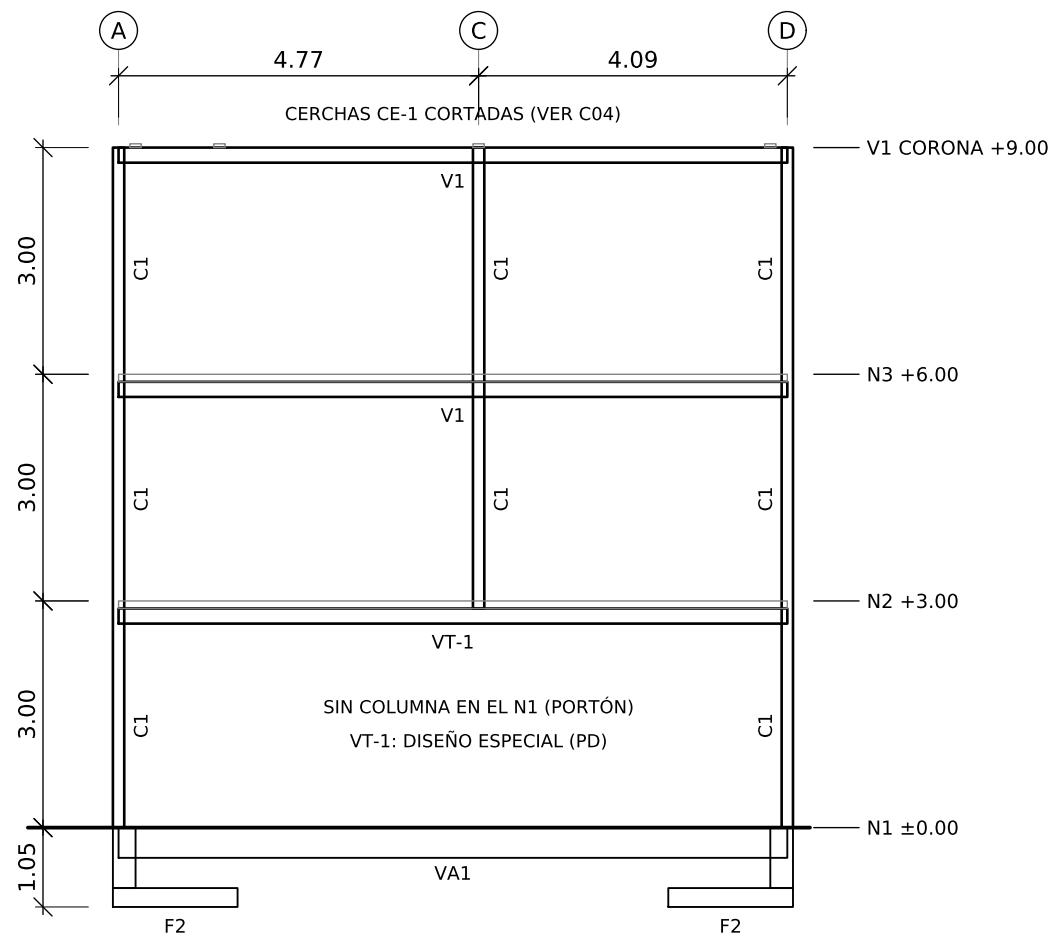

PÓRTICO 1
EJES A, C Y D (FACHADA FRONTAL) - Esc. 1:100

DETALLE DE PÓRTICOS

EJES LONGITUDINALES Y TRANSVERSALES
Esc. 1:100

SIMBOLOGÍA ELEMENTOS PORTANTES

C1	COLUMNA - TUBO DE ACERO 6x6" EN 3,17 mm [PR]
V1	VIGA - TUBO DE ACERO 4x8" EN 3,17 mm [PR]
VT-1	VIGA DE TRANSFERENCIA, EJE 1 EN N2 - DISEÑO ESPECIAL (PD)
VA1	VIGA RIOSTRA 0,20 x 0,40, 6 #4, AROS #3 @20 cm [PR]
F1 / F2	PLACA 1,65 x 1,65 x 0,25 CENTRADA / EXCÉNTRICA (C02) [PR]

NOTAS:

- TODAS LAS MEDIDAS ESTÁN DADAS EN METROS, SALVO INDICACIÓN CONTRARIA. [PR]
 - ELEVACIONES ESQUEMÁTICAS. UBICACIÓN DE COLUMNAS Y VIGAS SEGÚN C01, C03 Y C04; PLACAS, PEDESTALES Y VIGAS RIOSTRA SEGÚN C01 Y C02.
 - COLUMNAS C1 CONTINUAS DESDE LA PLACA HASTA LA VIGA DE CORONA (+9.00). LAS DEL EJE C VAN FORRADAS A 0,30 x 0,30 (A2-A4).
 - EJE C EN EL EJE 1: SIN COLUMNA EN EL NIVEL 1 (PORTÓN). LA C1 DE LOS NIVELES 2 Y 3 ARRANCA SOBRE LA VIGA DE TRANSFERENCIA VT-1 DEL EJE 1 (ENTREPISO DEL NIVEL 2), DE DISEÑO ESPECIAL SEGÚN LA MEMORIA DE CÁLCULO (PD).
 - VIGAS V1 DE ENTREPISO CON LA CARA SUPERIOR A 0,10 BAJO EL NPT (PAQUETE 0,30 = V1 0,20 + LOSA 0,10, VER C03); V1 DE CORONA CON LA CARA SUPERIOR A +9,00 (VER C04).
 - UNIONES VIGA-COLUMNA SOLDADAS Y VERIFICACIÓN DE PERFILES SEGÚN MEMORIA DE CÁLCULO (PD).
 - MATERIALES, PROTECCIÓN ANTICORROSIVA Y ESPECIFICACIONES SEGÚN LÁMINA C07.
 - LAS SECCIONES SON LAS DEL PROYECTO DE REFERENCIA, POR INDICACIÓN DEL INGENIERO RESPONSABLE; NO SUSTITUYEN LA MEMORIA DE CÁLCULO.
- [PR] = NOTA TOMADA DEL PROYECTO DE REFERENCIA, PENDIENTE DE REVISIÓN.

ESPACIO PARA SELLOS Y TIMBRES

CivilCon Diseño y Construcción SRLTDA
Céd. Jurídica: 3-102-762712

PROFESIONAL RESPONSABLE:
DIRECTOR TÉCNICO:
Steven Viales (Civil) IC-40759
David Barrantes (Electricidad) IE-27499

PROYECTO:
VIVIENDA UNIFAMILIAR
DISTRITO 03 SANTIAGO, CANTÓN 05 SAN RAFAEL,
PROVINCIA 04 HEREDIA, COSTA RICA.

INFORMACIÓN REGISTRO PÚBLICO:
FOLIO REAL: 4-041200-000
PLANO CATASTRADO: 4-57389-2023
ÁREA SEGÚN CATASTRO: 256 m²

CONTENIDO:
PÓRTICOS
PÓRTICOS A Y D.
PÓRTICO C.
PÓRTICOS 2 A 6.
PÓRTICO 1.
SIMBOLOGÍA Y NOTAS.

ESCALAS: 1:100

CONTROL DE REVISIONES		
REV.	FECHA	DESCRIPCIÓN
0	06-10-2026	VERSIÓN DE TRABAJO PARA REVISIÓN
1	06-10-2026	C05 Y C06 UNIFICADAS; C1 EJE C-1 EN N2-N3 SOBRE VT-1

ESTADO:
VERSIÓN DE TRABAJO
NO APTA PARA CONSTRUCCIÓN NI TRÁMITE

LUGAR	LÁMINA
COSTA RICA	C05
OCT 2026	TOTAL --