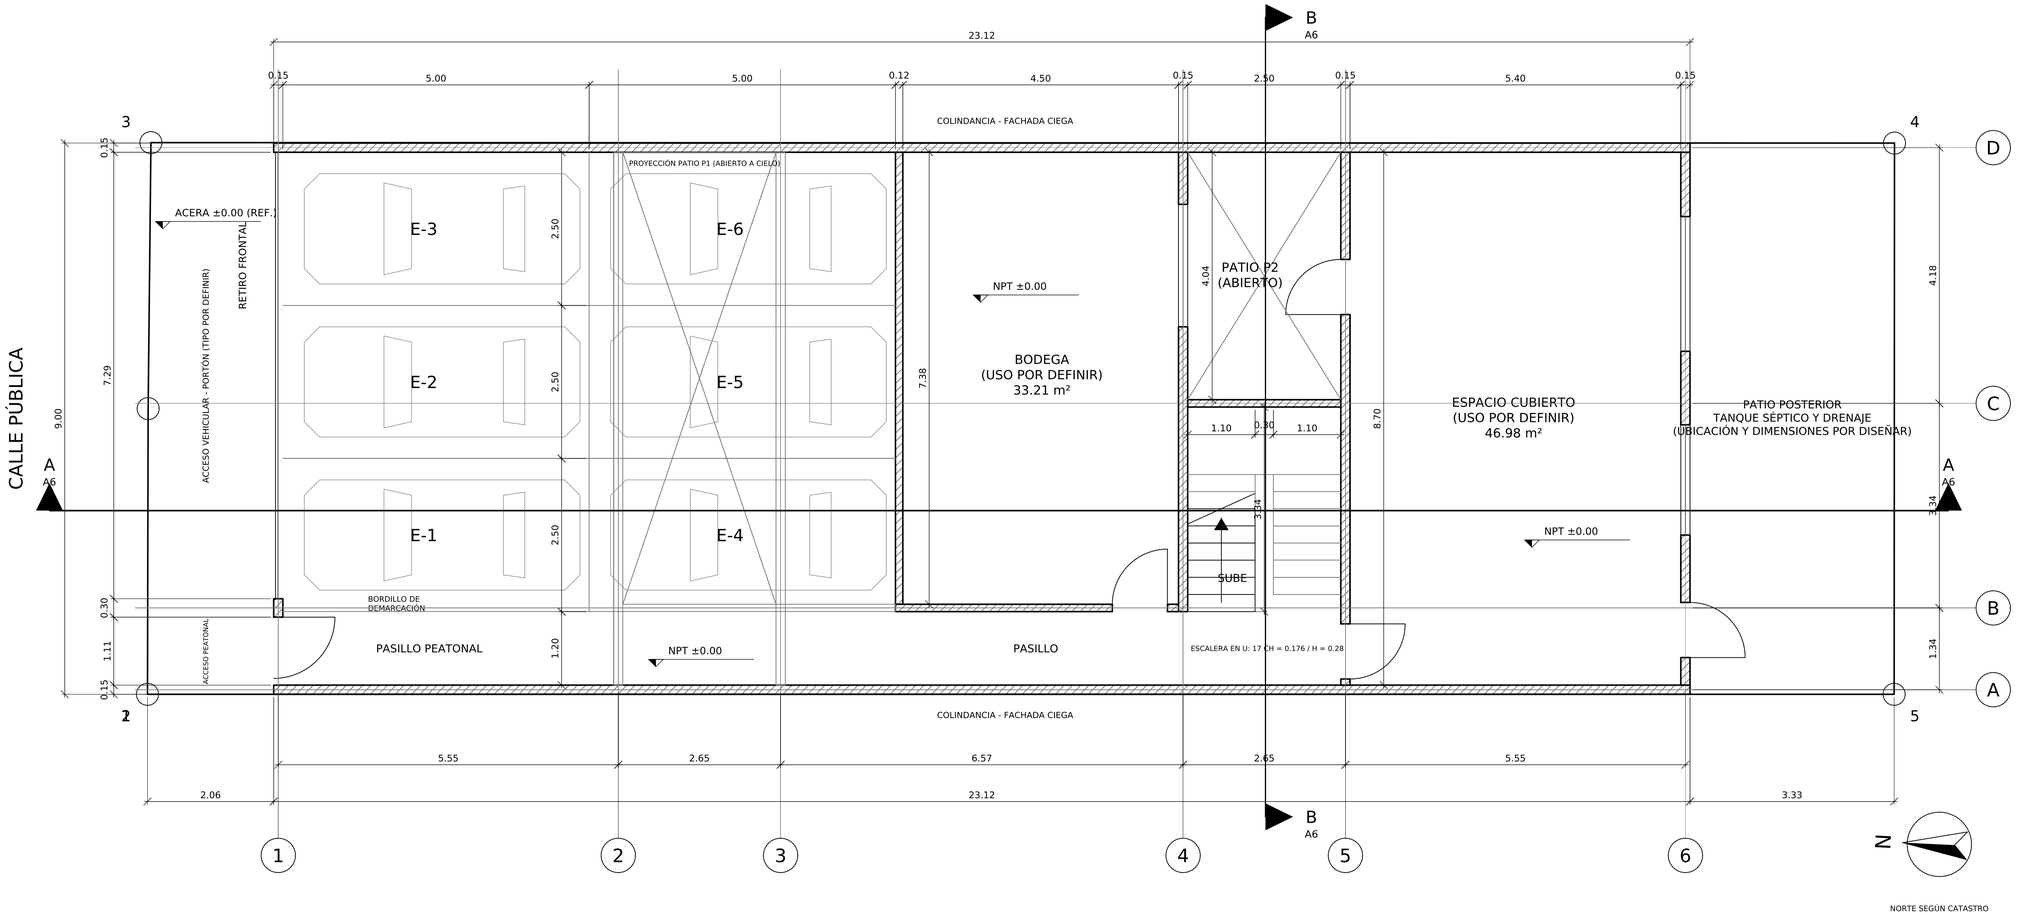


NORTE SEGÚN CATASTRO

PLANTA NIVEL 1

PARQUEOS, ACCESO Y CIRCULACIÓN VERTICAL

Esc. 1:50

0 1 2 3 4 5 m

D E R R O T E R O

LÍNEA	ACIMUT		DISTANCIA	
	°	'	m	cm
1 - 2	87	25	4	66
2 - 3	87	53	4	34
3 - 4	177	18	28	46
4 - 5	267	20	9	00
5 - 1	357	17	28	51
AMARRE	ACIMUT		DISTANCIA	
	°	'	m	cm
3 - P.I.	101	22	75	71

VER CUADRO DE COORDENADAS CRTM05 EN LÁMINA A1.

CUADRO DE ÁREAS

ESPACIO	ÁREA
ÁREA NIVEL 1	179,53 m²
ÁREA NIVEL 2 (PRELIMINAR, VER A3)	179,53 m²
ÁREA NIVEL 3 (PRELIMINAR, VER A4)	179,53 m²
ÁREA DE CONSTRUCCIÓN	538,59 m²

ÁREA POR NIVEL = ENVOLVENTE 9,00 x 23,12 (208,08 m²) - PATIOS ABIERTOS P1 Y P2 (28,55 m²). INCLUYE ESCALERA (8,35 m²) Y PASILLO.

DESGLOSE NIVEL 1 (ÁREAS LIBRES ENTRE MUROS)

ESTACIONAMIENTOS (6) 7,50 x 10,00 (1)	75,00 m²
PASILLO PEATONAL 1,20 x 17,27	20,72 m²
BODEGA 7,38 x 4,50	33,21 m²
ESCALERA 3,34 x 2,50	8,35 m²
ESPACIO CUBIERTO POSTERIOR 8,70 x 5,40	46,98 m²

(1) INCLUYE 18,45 m² BAJO EL PATIO P1, ABIERTO A CIELO.

PORCENTAJE DE COBERTURA

CONCEPTO	VALOR
ÁREA DE LOTE (SEGÚN CATASTRO)	256,00 m²
HUELLA CONSTRUCTIVA NIVEL 1	179,53 m²
% COBERTURA	70,13 %

CÁLCULO: (HUELLA / ÁREA DE LOTE) x 100 = (179,53 / 256,00) x 100 = 70,13 %

NOTAS:

1.- TODAS LAS MEDIDAS ESTÁN DADAS EN METROS, SALVO INDICACIÓN CONTRARIA. [PR]
2.- LA TAPIA COLINDANTE DE MAMPOSTERÍA DEBERÁ PROLONGARSE HASTA EL NIVEL DE LA VIGA CORONA DEL ÚLTIMO NIVEL, GARANTIZANDO EL APANTALLAMIENTO VISUAL PERMANENTE HACIA LA PROPIEDAD COLINDANTE.
3.- LOS DATOS DEL LOTE (VÉRTICES, DERROTERO Y ÁREA) SE TOMARON DEL PLANO CATASTRADO 4-57389-2023, SISTEMA CRTM05. NO SUSTITUYEN UN LEVANTAMIENTO TOPOGRÁFICO.
4.- RETIROS DE DISEÑO: FRONTAL 2.00 m MEDIDO DESDE EL VÉRTICE 3; POSTERIOR MÍNIMO 3.00 m; LATERALES 0.00 m. CONFIRMAR CON ALINEAMIENTO Y USO DE SUELO MUNICIPAL.
5.- LAS FACHADAS LATERALES SE UBICAN SOBRE COLINDANCIA Y SERÁN CIEGAS (SIN VENTANAS NI VANOS).
6.- LOS BAÑOS CONTARÁN CON EXTRACTOR MECÁNICO DE AIRE.
7.- LAS CANOAS TENDRÁN MALLA PROTECTORA PARA EVITAR EL ACCESO DE BASURA. [PR]
8.- EL AGUA POTABLE PROVIENE DEL SISTEMA PÚBLICO (ESPH), DIRECTAMENTE DE LA CONEXIÓN DE LA CALLE.
9.- LAS AGUAS PLUVIALES SE DIRIGEN HACIA LA CUNETA PÚBLICA.
10.- LAS AGUAS RESIDUALES SE TRATARÁN MEDIANTE TANQUE SÉPTICO Y DRENAJE EN EL PATIO POSTERIOR; DISEÑO Y UBICACIÓN EN LÁMINAS SANITARIAS.
11.- LA COBERTURA SE CALCULA SOBRE EL ÁREA SEGÚN CATASTRO (256 m²). LOS PATIOS P1 Y P2 SON ABIERTOS DESDE EL NIVEL 1 HASTA EL CIELO Y NO SE CONTABILIZAN EN LA HUELLA.
12.- PATIOS DE LUZ P1 Y P2 DE 2.50 m DE LADO MÍNIMO, DIMENSIÓN ACEPTADA POR LA MUNICIPALIDAD (ALTURA MEDIDA DESDE EL NIVEL 1).
13.- NIVEL 1: 6 ESTACIONAMIENTOS DE 2.50 x 5.00 m, E-1 A E-3 INDEPENDIENTES Y E-4 A E-6 EN TÁNDEM, CON ACCESO RECTO DESDE LA CALLE.
14.- PORTÓN VEHICULAR CON CLARO LIBRE DE 7.29 m Y ACCESO PEATONAL DE 1.00 m; TIPO DE PORTÓN POR DEFINIR.
15.- COLUMNAS, VIGAS Y PILASTRA DEL EJE B SEGÚN PLANOS ESTRUCTURALES (PENDIENTES DE DISEÑO). SOBRE LOS ESTACIONAMIENTOS NO SE PREVÉN COLUMNAS INTERMEDIAS.
16.- NPT ±0.00 = NIVEL DE ACERA (TERRENO PLANO). PENDIENTES DE PISO Y DESAGÜES SEGÚN LÁMINAS SANITARIAS.
17.- LOS USOS DE LA BODEGA Y DEL ESPACIO CUBIERTO POSTERIOR ESTÁN POR DEFINIR.
[PR] = NOTA TOMADA DEL PROYECTO DE REFERENCIA, PENDIENTE DE REVISIÓN.

ESPACIO PARA SELLOS Y TIMBRES

CivilCon Diseño y Construcción SRLTDA
Céd. Jurídica: 3-102-762712

PROFESIONAL RESPONSABLE:
DIRECTOR TÉCNICO:
Steven Viales (Civil) IC-40759
David Barrantes (Electricidad) IE-27499

PROYECTO:
VIVIENDA UNIFAMILIAR
DISTRITO 03 SANTIAGO, CANTÓN 05 SAN RAFAEL,
PROVINCIA 04 HEREDIA, COSTA RICA.

INFORMACIÓN REGISTRO PÚBLICO:
FOLIO REAL: 4-041200-000
PLANO CATASTRADO: 4-57389-2023
ÁREA SEGÚN CATASTRO: 256 m²

CONTENIDO:
PLANTA NIVEL 1
PARQUEOS Y ACCESO.
DERROTERO.
CUADRO DE ÁREAS.
PORCENTAJE DE COBERTURA.
NOTAS.

ESCALAS: 1:50 / INDICADAS

CONTROL DE REVISIONES

REV.	FECHA	DESCRIPCIÓN
0	06-10-2026	VERSIÓN DE TRABAJO PARA REVISIÓN

ESTADO:
VERSIÓN DE TRABAJO
NO APTA PARA CONSTRUCCIÓN NI TRÁMITE

LUGAR	LÁMINA
COSTA RICA	A2
OCT 2026	TOTAL --

FORMATO A1 841 mm x 594 mm