


CALLE PÚBLICA

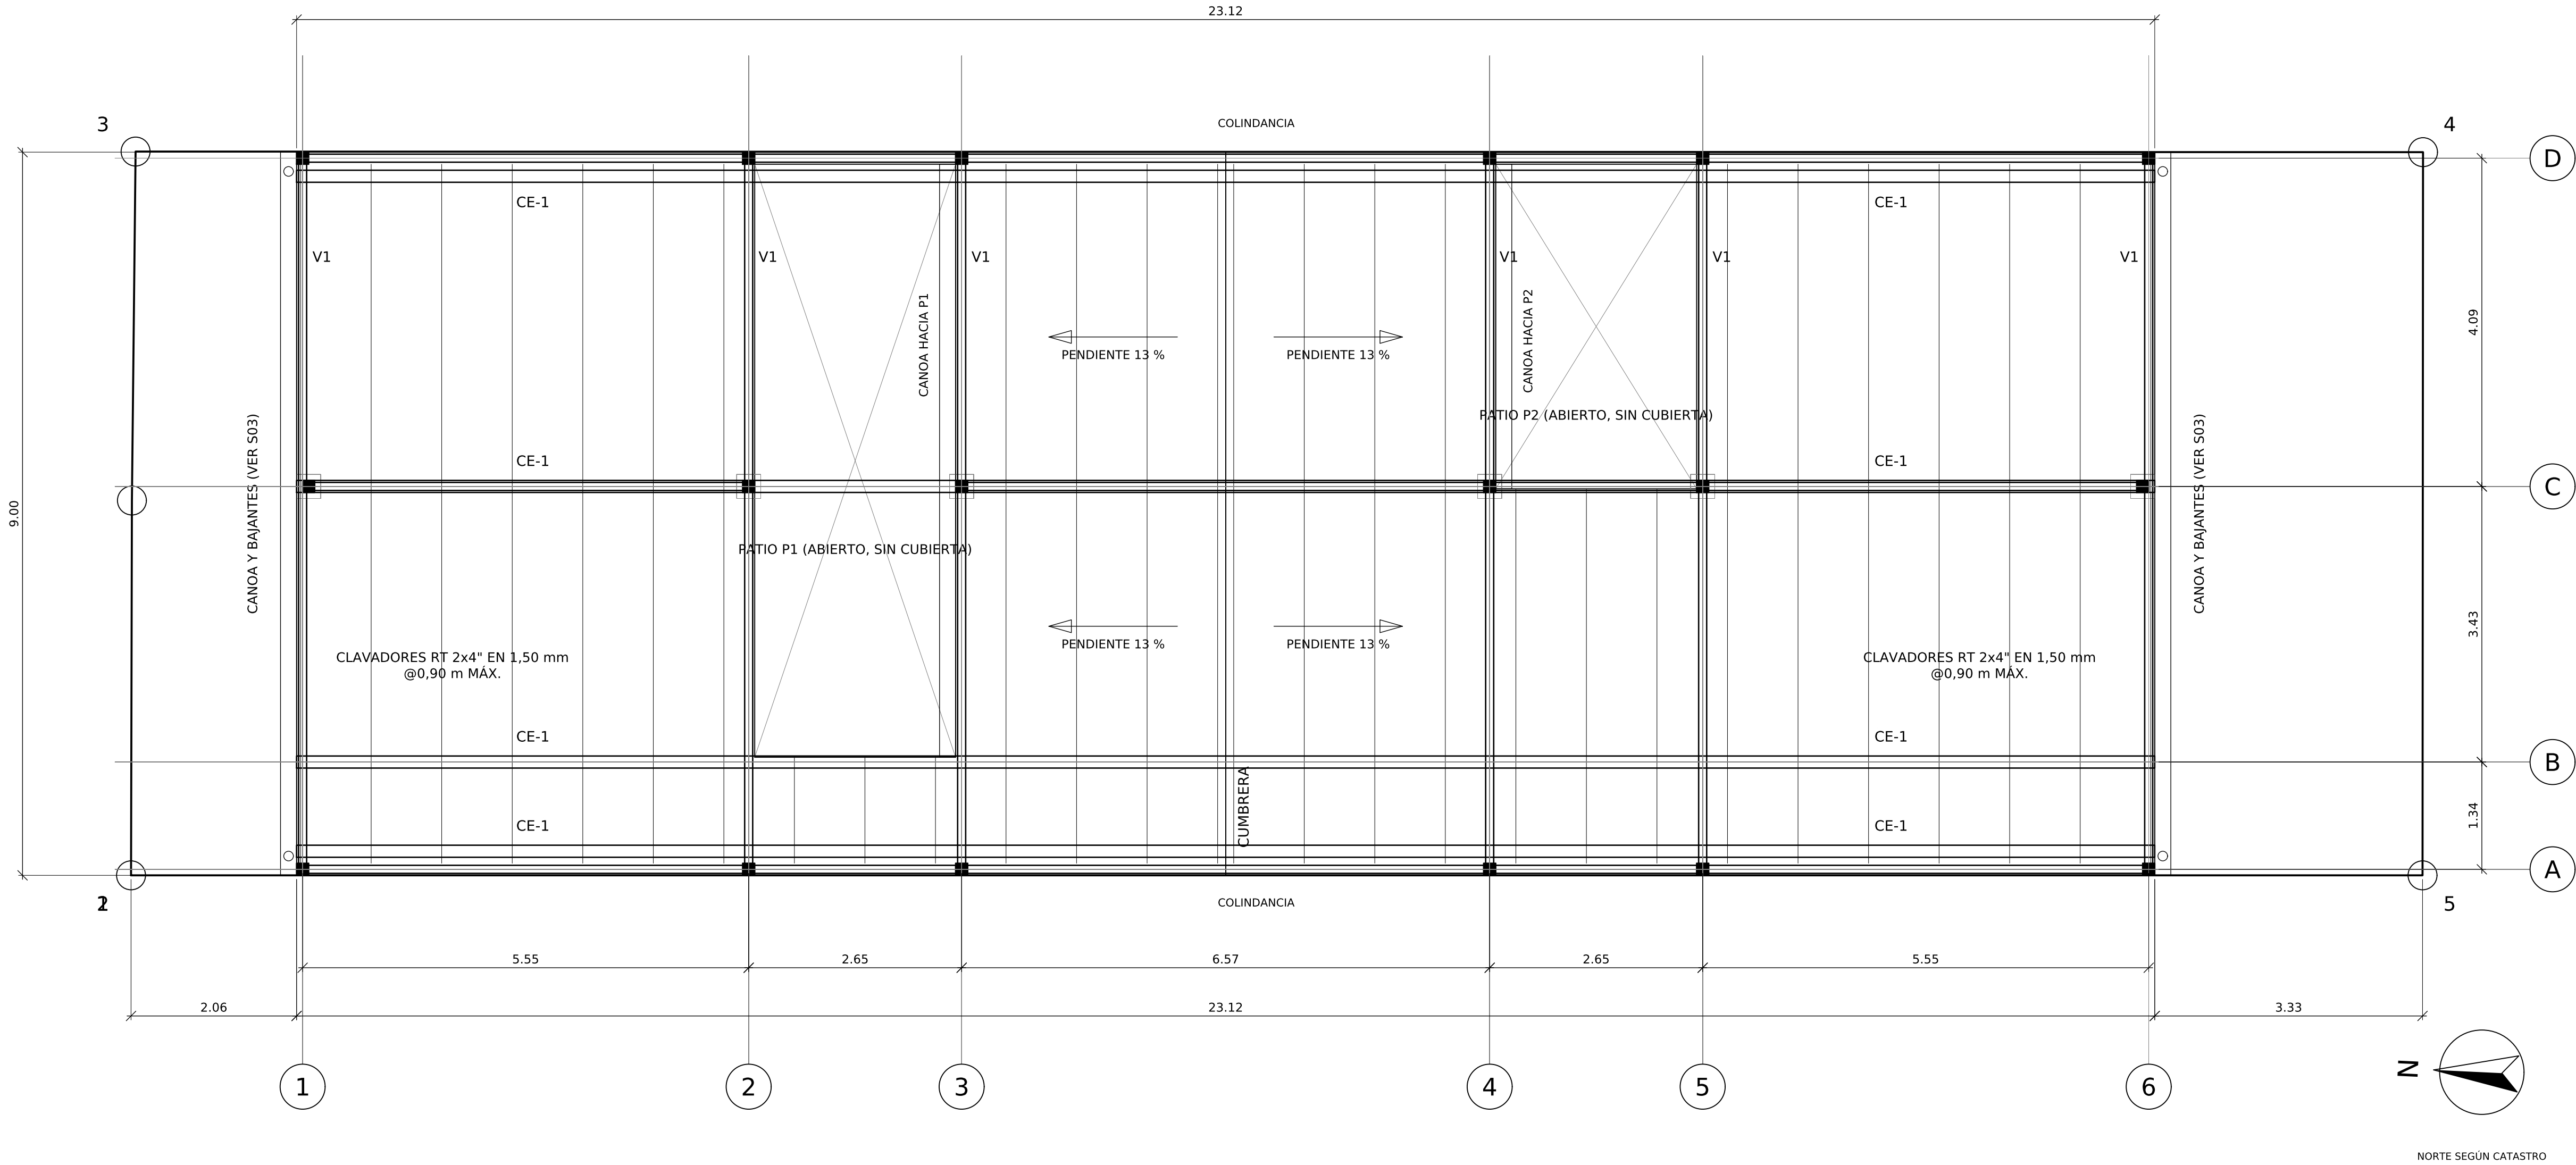

PLANTA DE TECHO


ESTRUCTURA DE CUBIERTA

Esc. 1:50




SIMBOLOGÍA ELEMENTOS PORTANTES

C1	COLUMNA - TUBO DE ACERO 6x6" EN 3,17 mm [PR]
V1	VIGA DE CORONA - TUBO 4x8" EN 3,17 mm, +9,00 [PR]
CE-1	CERCHA - CORDONES 2x6" EN 2,38 mm
	DIAGONALES Y MONTANTES 2x2" EN 1,50 mm
CL	CLAVADOR - TUBO RT 2x4" EN 1,50 mm @0,90 m MÁX.
	PATIO ABIERTO (SIN CUBIERTA)

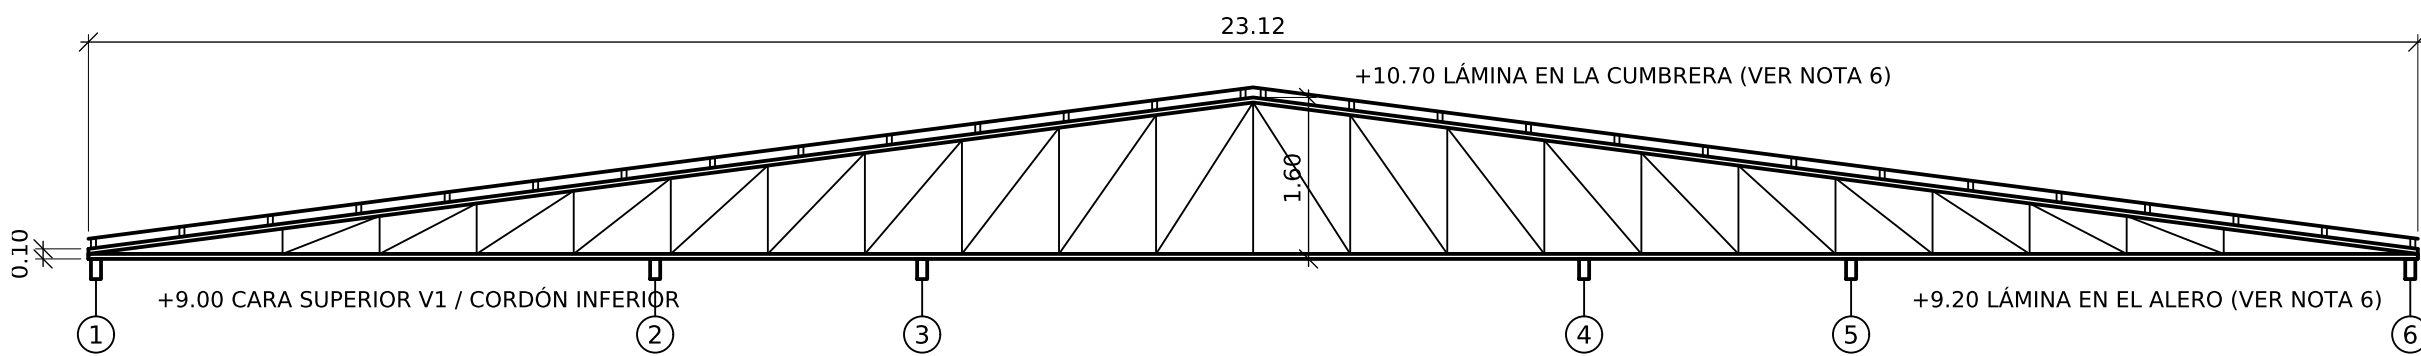

CERCHA TÍPICA CE-1 (ELEVACIÓN)

EN x 0,30 / EJE B / EJE C / x 8,70 - Esc. 1:75

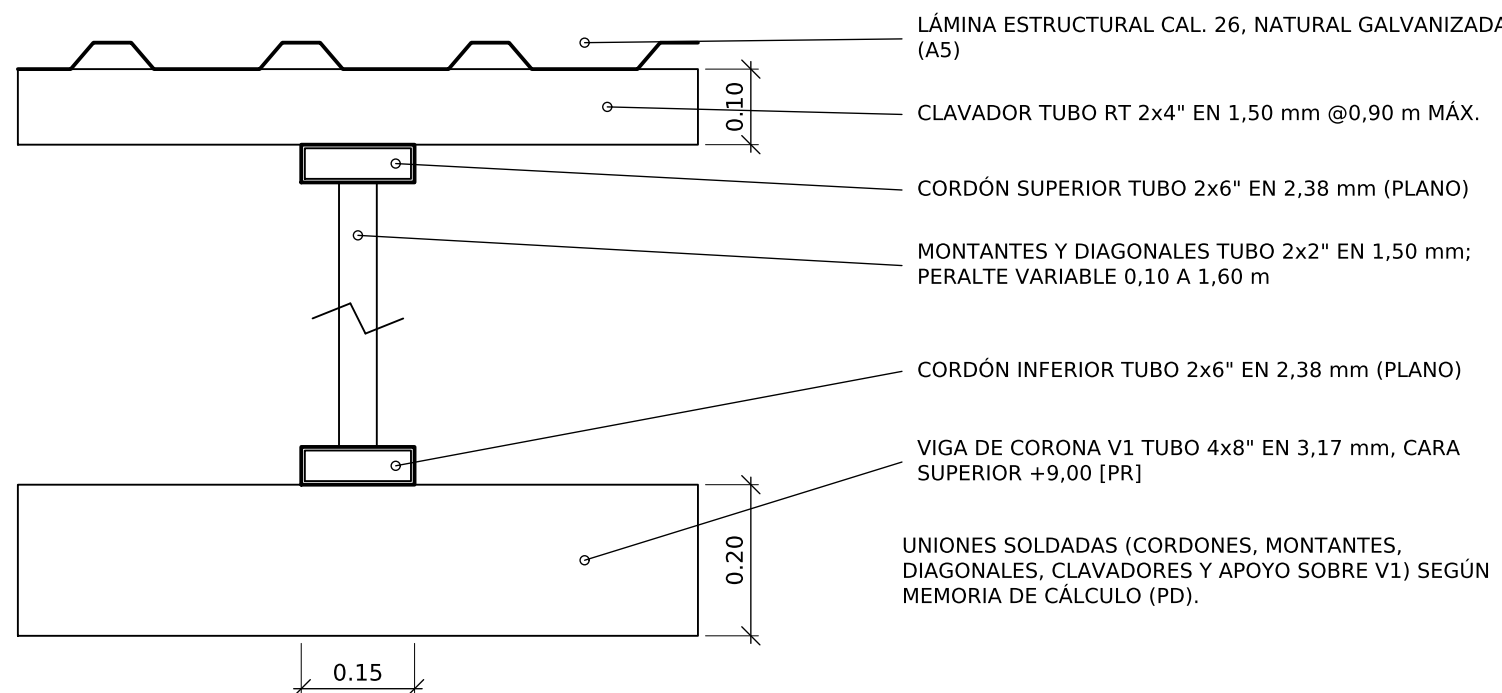

SECCIÓN TÍPICA DE CUBIERTA

PERPENDICULAR A LA CERCHA - Esc. 1:10

NOTAS:

- TODAS LAS MEDIDAS ESTÁN DADAS EN METROS, SALVO INDICACIÓN CONTRARIA. [PR]
- CUBIERTA DE LÁMINA ESTRUCTURAL CAL. 26 A DOS AGÜAS (FRENTE Y FONDO), PENDIENTE 13 %, SOBRE CLAVADORES Y CERCÍAS METÁLICAS EN LA DIRECCIÓN DE LA PENDIENTE (A5, A6).
- CERCÍAS CE-1 EN x 0,30, EJE B, EJE C Y x 8,70, APOYADAS EN LAS VIGAS DE CORONA V1 DE LOS EJES 1 A 6. LA CERCHA DEL EJE C ES CONTINUA SOBRE EL PATIO P1.
- VIGAS DE CORONA V1 A +9,00 EN LOS EJES 1 A 6 Y EN A, C Y D, SOBRE LAS COLUMNAS C1, IGUAL QUE EN LOS ENTREPISOS (C03). [PR]
- PATIOS P1 Y P2 ABIERTOS, SIN CUBIERTA, CANOAS AL FRENTE, AL FONDO Y HACIA LOS PATIOS; BAJANTES Y DETALLE DE CANOA EN S03.
- NIVELES DE LÁMINA RESULTANTES DE LA CERCHA: +9,20 EN EL ALERO Y +10,70 EN LA CUMBRERA (IGUAL QUE EN A5 Y A6).
- UNIONES SOLDADAS Y VERIFICACIÓN DE PERFILES SEGÚN MEMORIA DE CÁLCULO (PD).
- MATERIALES, PROTECCIÓN ANTICORROSIVA Y ESPECIFICACIONES SEGÚN LÁMINA C06. [PR] = NOTA TOMADA DEL PROYECTO DE REFERENCIA, PENDIENTE DE REVISIÓN.

ESPACIO PARA SELLOS Y TIMBRES

CivilCon Diseño y Construcción SRLTDA
Céd. Jurídica: 3-102-762712

PROFESIONAL RESPONSABLE:

DIRECTOR TÉCNICO:
Steven Viales (Civil) IC-40759
David Barrantes (Electricidad) IE-27499

PROYECTO:

VIVIENDA UNIFAMILIAR
DISTRITO 03 SANTIAGO, CANTÓN 05 SAN RAFAEL,
PROVINCIA 04 HEREDIA, COSTA RICA.

INFORMACIÓN REGISTRO PÚBLICO:

FOLIO REAL: 4-041200-000
PLANO CATASTRADO: 4-57389-2023
ÁREA SEGÚN CATASTRO: 256 m²

CONTENIDO:

TECHO
PLANTA DE TECHO.
CERCHA TÍPICA CE-1.
SECCIÓN TÍPICA DE CUBIERTA.
SIMBOLOGÍA.
NOTAS.

ESCALAS: 1:50 / INDICADAS

CONTROL DE REVISIONES

REV.	FECHA	DESCRIPCIÓN
0	06-10-2026	VERSIÓN DE TRABAJO PARA REVISIÓN
1	06-10-2026	C1 EJE C-1 HASTA CORONA; REFERENCIA A C06
2	07-10-2026	REFERENCIAS A S03; NIVELES CONFIRMADOS

ESTADO:

VERSIÓN DE TRABAJO
NO APTA PARA CONSTRUCCIÓN NI TRÁMITE

LUGAR	LÁMINA
COSTA RICA	C04
OCT 2026	TOTAL --