



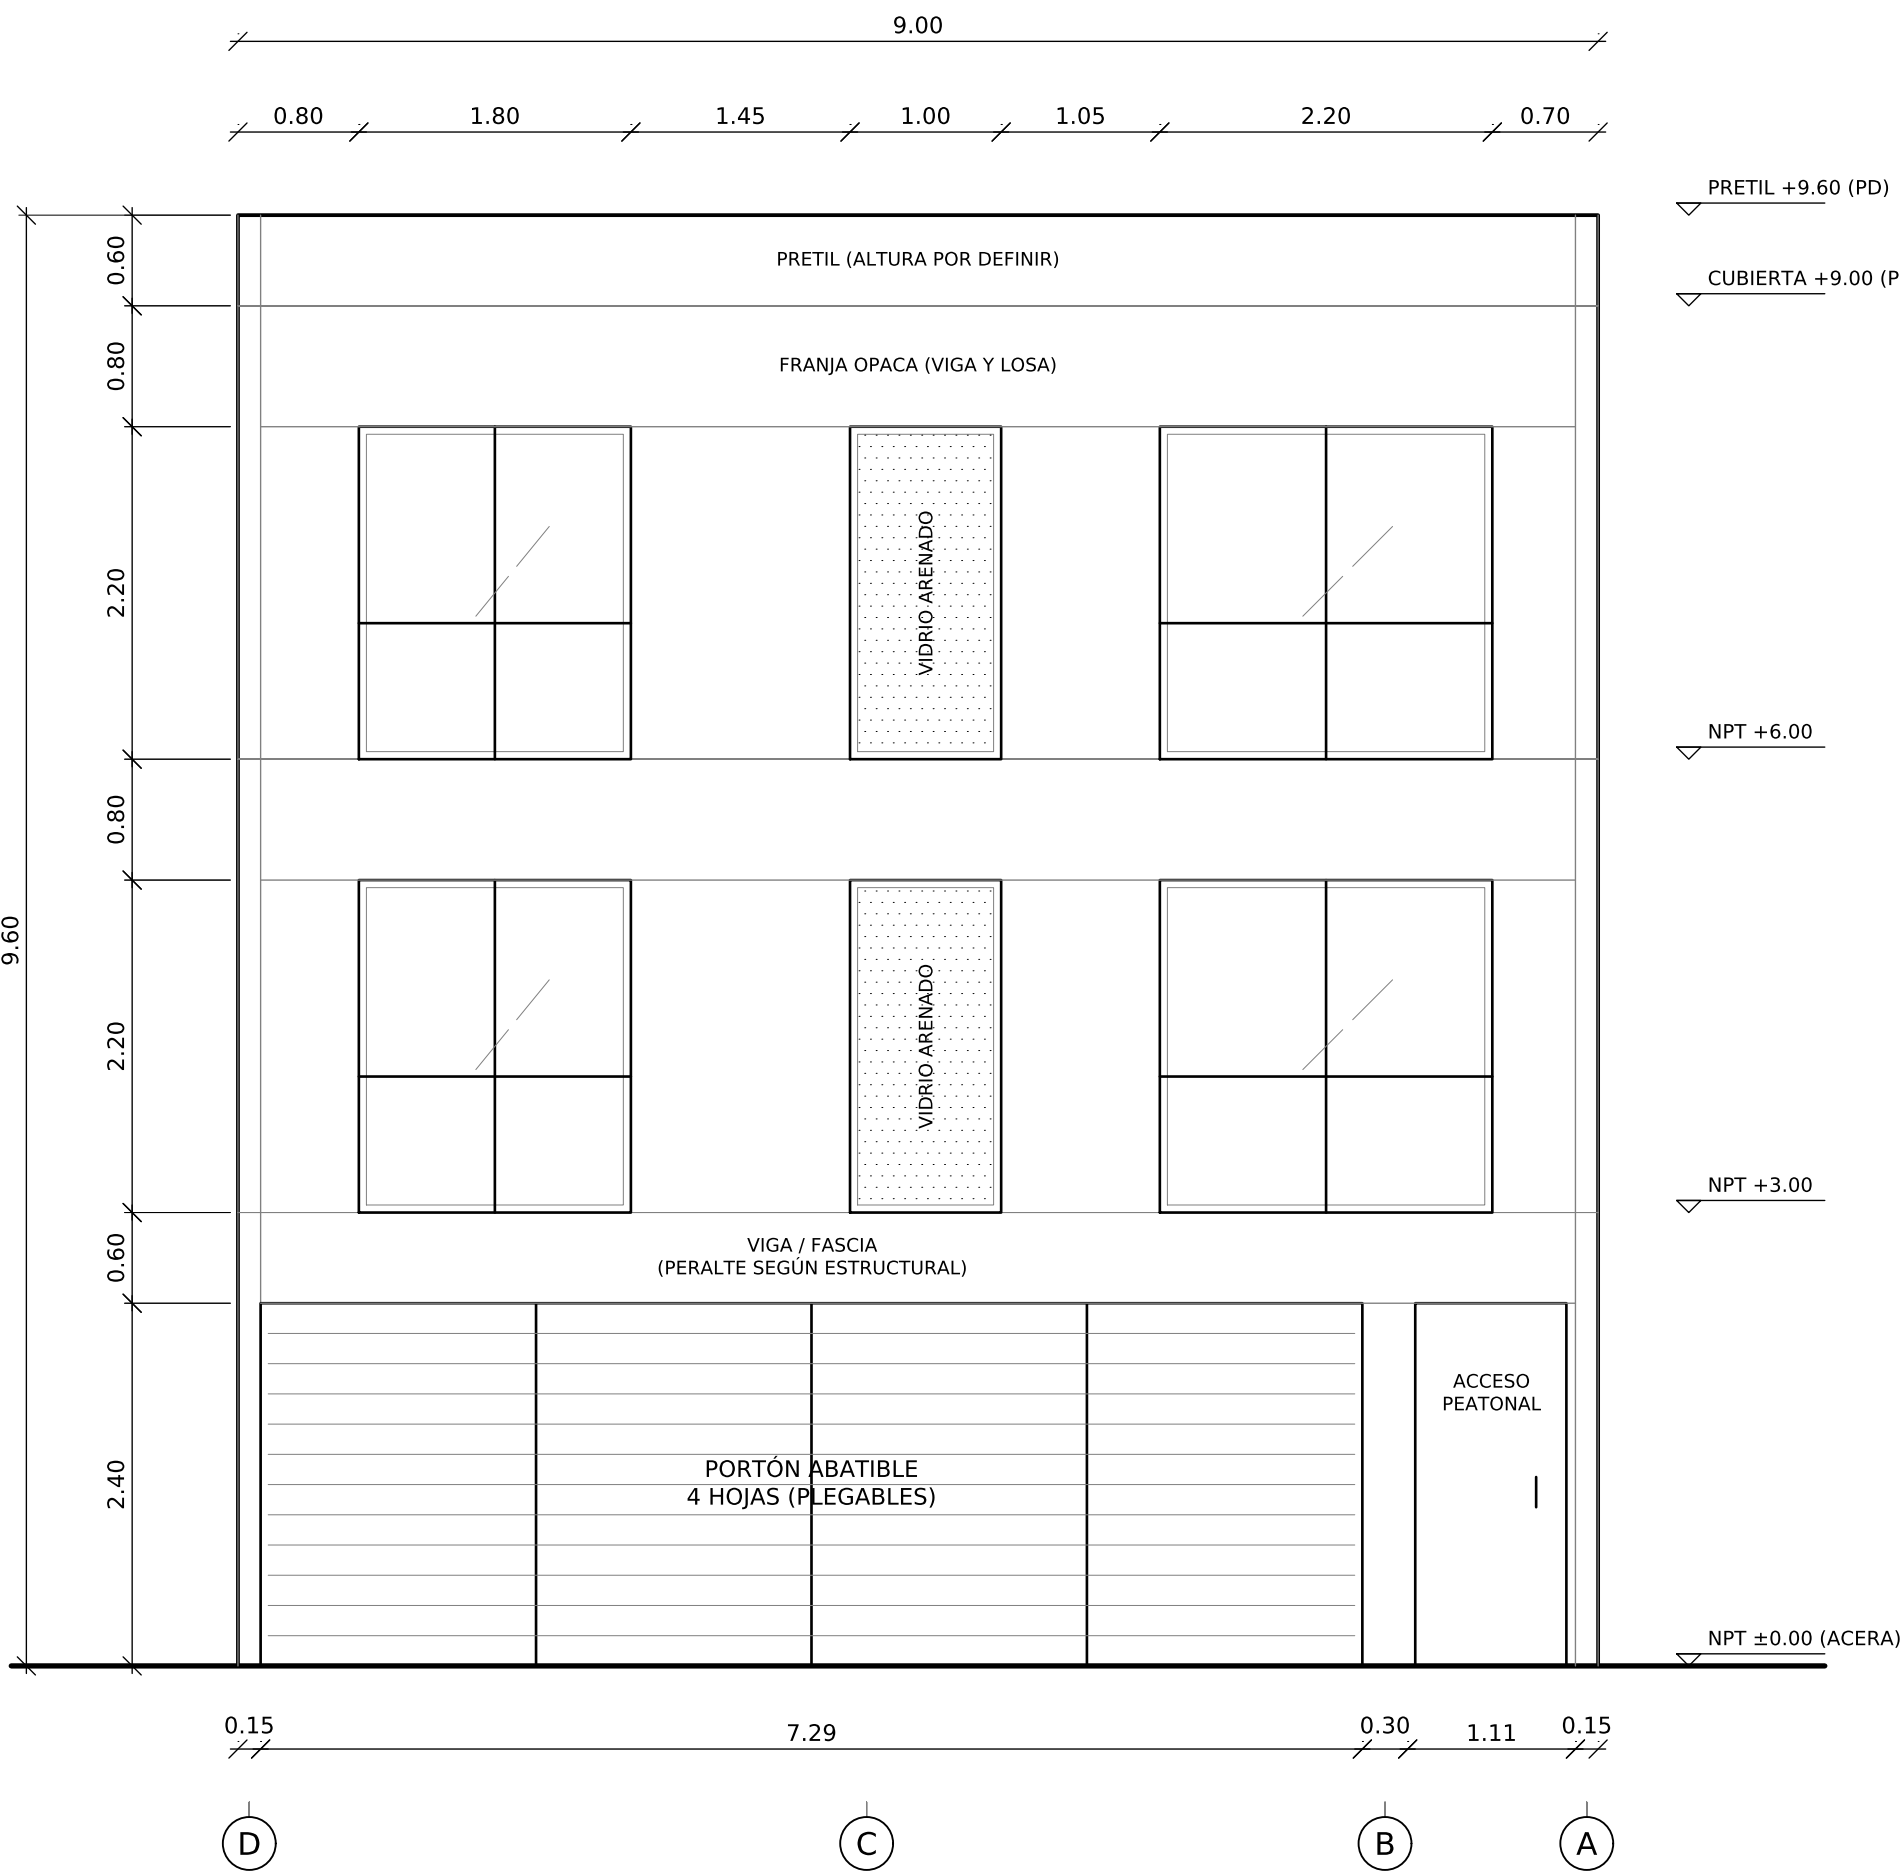


FACHADA PRINCIPAL (NORTE)
VISTA DESDE LA CALLE
Esc. 1:50



FACHADA LATERAL ESTE
MURO DE COLINDANCIA
Esc. 1:100

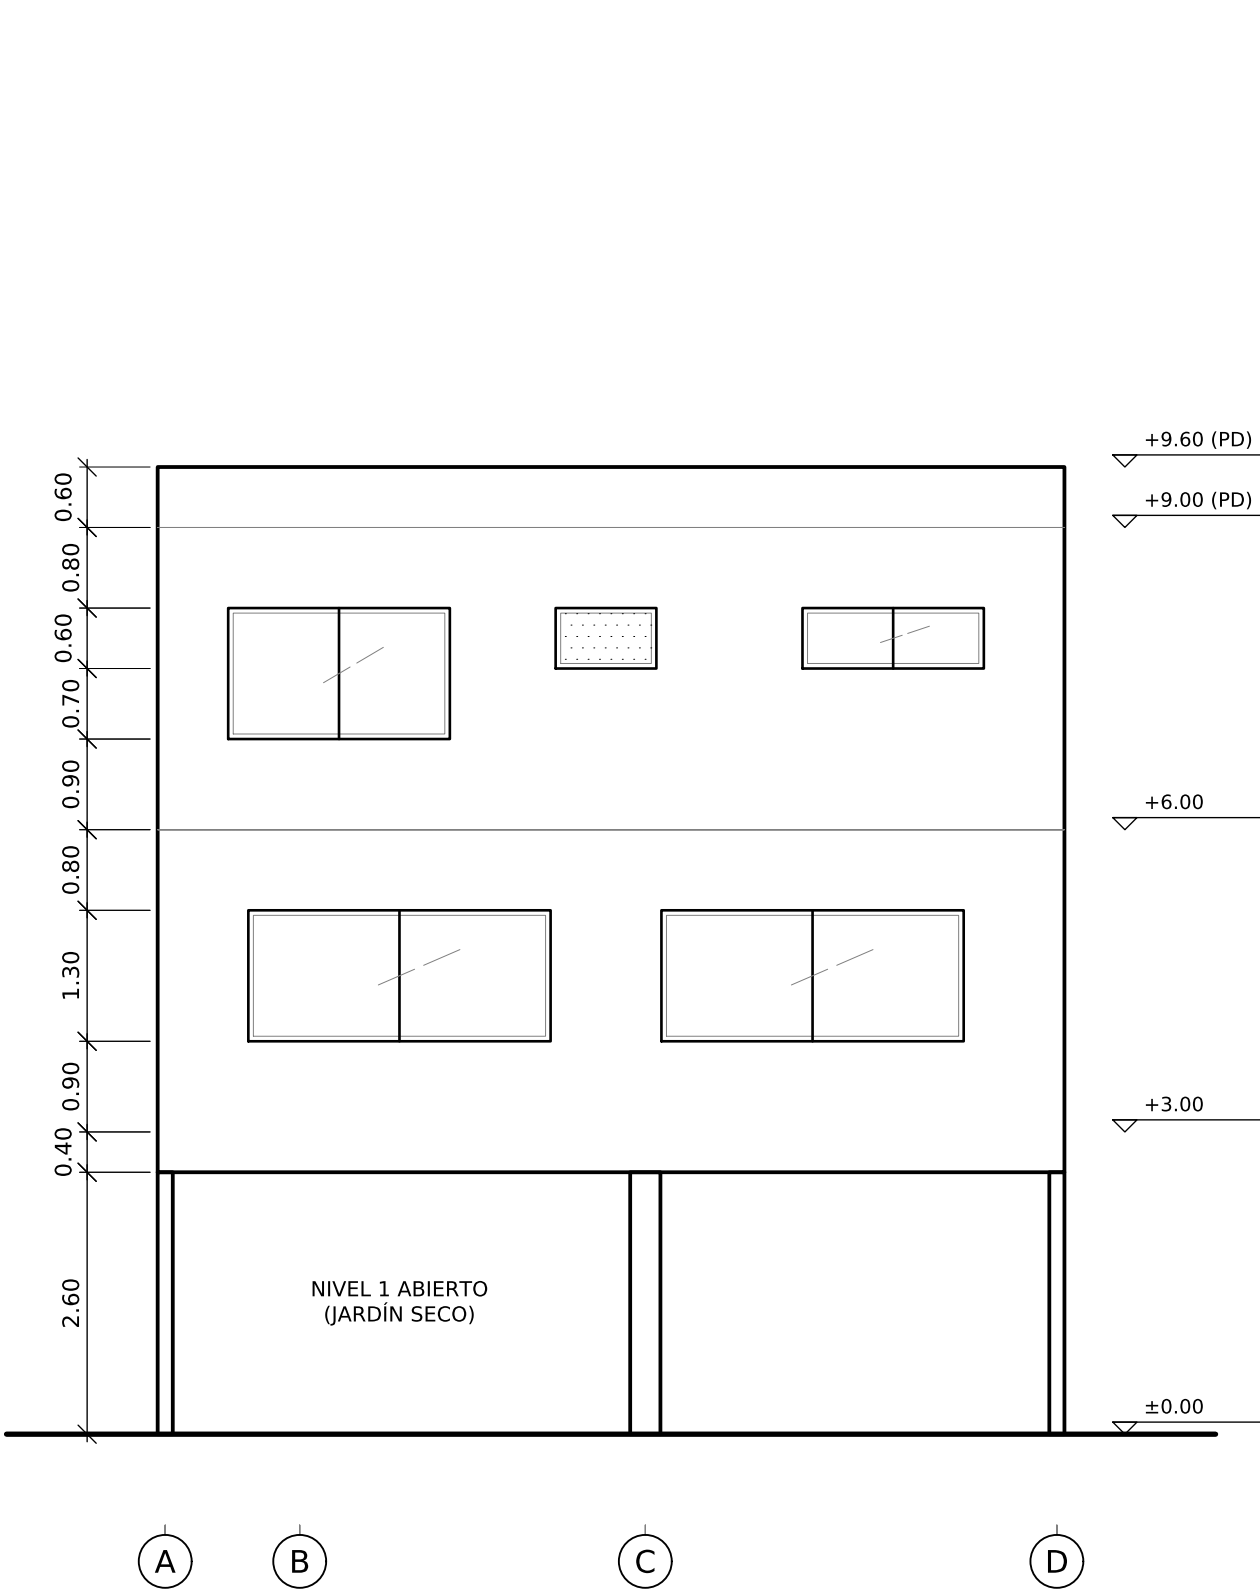

FACHADA POSTERIOR (SUR)
VISTA DESDE EL PATIO POSTERIOR
Esc. 1:75

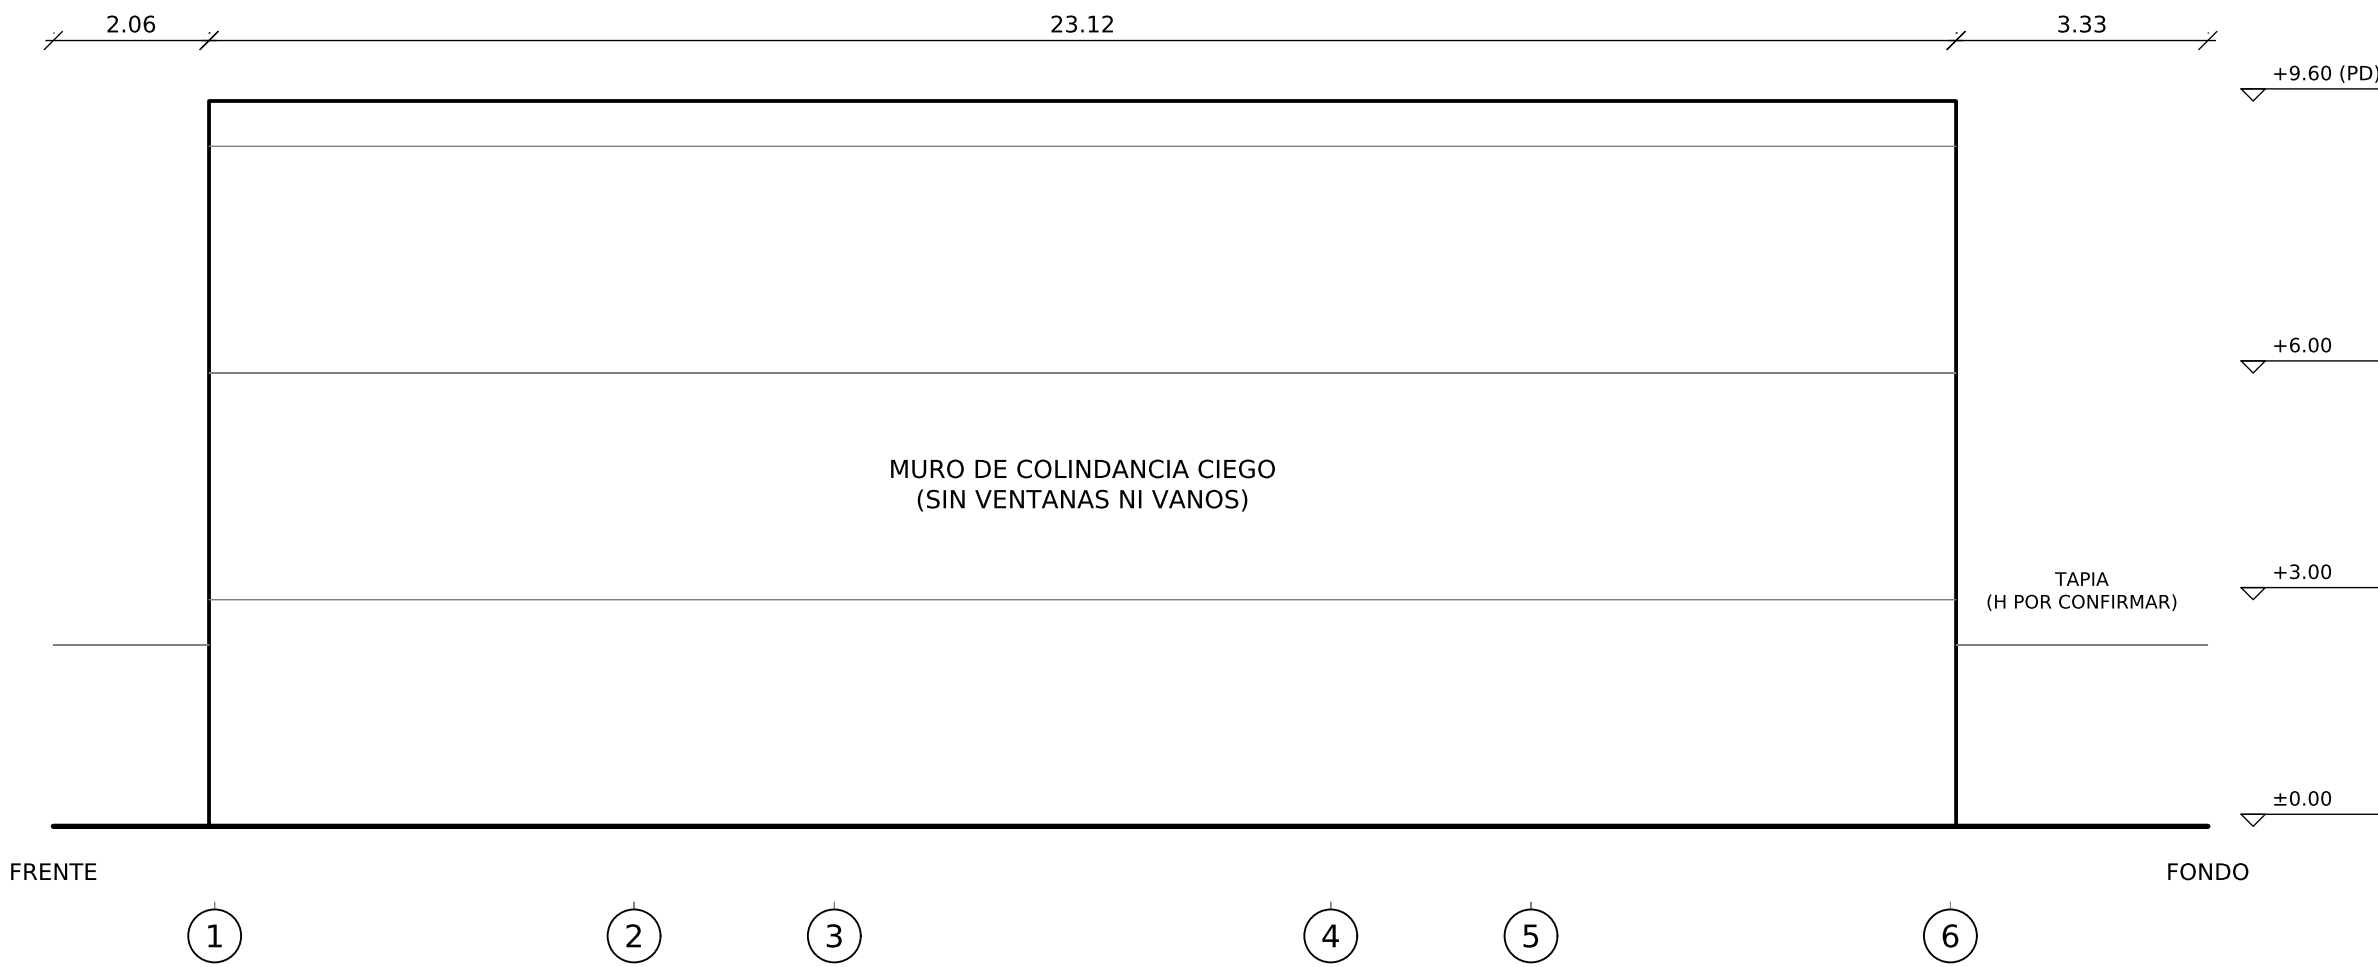

FACHADA LATERAL OESTE
MURO DE COLINDANCIA
Esc. 1:100

- NOTAS:
- TODAS LAS MEDIDAS ESTÁN DADAS EN METROS, SALVO INDICACIÓN CONTRARIA. [PR]
 - LA TAPIA COLINDANTE DE MAMPOSTERÍA DEBERÁ PROLONGARSE HASTA EL NIVEL DE LA VIGA CORONA DEL ÚLTIMO NIVEL, GARANTIZANDO EL APANTALLAMIENTO VISUAL PERMANENTE HACIA LA PROPIEDAD COLINDANTE.
 - LOS BAÑOS CONTARÁN CON EXTRACTOR MECÁNICO DE AIRE.
 - NIVELES: NPT ±0.00 (ACERA), N2 +3.00, N3 +6.00. CUBIERTA +9.00 Y PRETIL +9.60 SON PRELIMINARES (PD = POR DEFINIR CON EL DISEÑO DE TECHOS Y LA ALTURA MÁXIMA MUNICIPAL).
 - FACHADA PRINCIPAL: VENTANAS DE PISO A 2.20 m SOBRE NPT, ALINEADAS ENTRE NIVELES, CON FRANJA OPACA HASTA LA LOSA SUPERIOR (VIGAS). COMPOSICIÓN BASE PARA EL DISEÑO MODERNO.
 - VENTANAS DESDE EL PISO EN NIVELES 2 Y 3: VIDRIO DE SEGURIDAD (TEMPLADO O LAMINADO) Y PROTECCIÓN CONTRA CAÍDAS EN LA PARTE INFERIOR (PAÑO FIJO LAMINADO HASTA 0.90 m O BARANDA INTERIOR). VERIFICAR CON LA NORMATIVA VIGENTE.
 - BAÑOS: VIDRIO ARENADO (SANDBLAST) TEMPLADO. EN LA ZONA DE DUCHA EL VIDRIO DEBE QUEDAR SELLADO Y CON ANTEPECHO IMPERMEABLE O PANEL OPACO INTERIOR (POR DEFINIR).
 - FACHADA POSTERIOR: ANTEPECHO 0.90 m EN SALA Y DORMITORIO; 1.60 m EN BAÑO Y WALK-IN.
 - FACHADAS LATERALES SOBRE COLINDANCIA: MUROS CIEGOS.
 - PORTÓN Y PUERTA PEATONAL CON ALTURA PRELIMINAR DE 2.40 m. TIPOS DE VENTANAS Y PUERTAS EN LÁMINAS A7 A A9; ACABADOS DE FACHADA EN LÁMINA A10.
 - [PR] = NOTA TOMADA DEL PROYECTO DE REFERENCIA, PENDIENTE DE REVISIÓN.

- SIMBOLOGÍA:
- VIDRIO CLARO
 - VIDRIO ARENADO (SANDBLAST)
 - LÍNEA OCULTA (LOSA / NIVEL)

ESPACIO PARA SELLOS Y TIMBRES

CivilCon Diseño y Construcción SRLTDA
Céd. Jurídica: 3-102-762712

PROFESIONAL RESPONSABLE:
DIRECTOR TÉCNICO:
Steven Viales (Civil) IC-40759
David Barrantes (Electricidad) IE-27499

PROYECTO:
VIVIENDA UNIFAMILIAR
DISTRITO 03 SANTIAGO, CANTÓN 05 SAN RAFAEL,
PROVINCIA 04 HEREDIA, COSTA RICA.

INFORMACIÓN REGISTRO PÚBLICO:
FOLIO REAL: 4-041200-000
PLANO CATASTRADO: 4-57389-2023
ÁREA SEGÚN CATASTRO: 256 m²

CONTENIDO:
FACHADAS
FACHADA PRINCIPAL (NORTE).
FACHADA POSTERIOR (SUR).
FACHADA LATERAL ESTE.
FACHADA LATERAL OESTE.
NOTAS.

ESCALAS: 1:50 / INDICADAS

CONTROL DE REVISIONES		
REV.	FECHA	DESCRIPCIÓN
0	06-10-2026	VERSIÓN DE TRABAJO PARA REVISIÓN

ESTADO:
VERSIÓN DE TRABAJO
NO APTA PARA CONSTRUCCIÓN NI TRÁMITE

LUGAR	LÁMINA
COSTA RICA	A5
OCT 2026	TOTAL --