




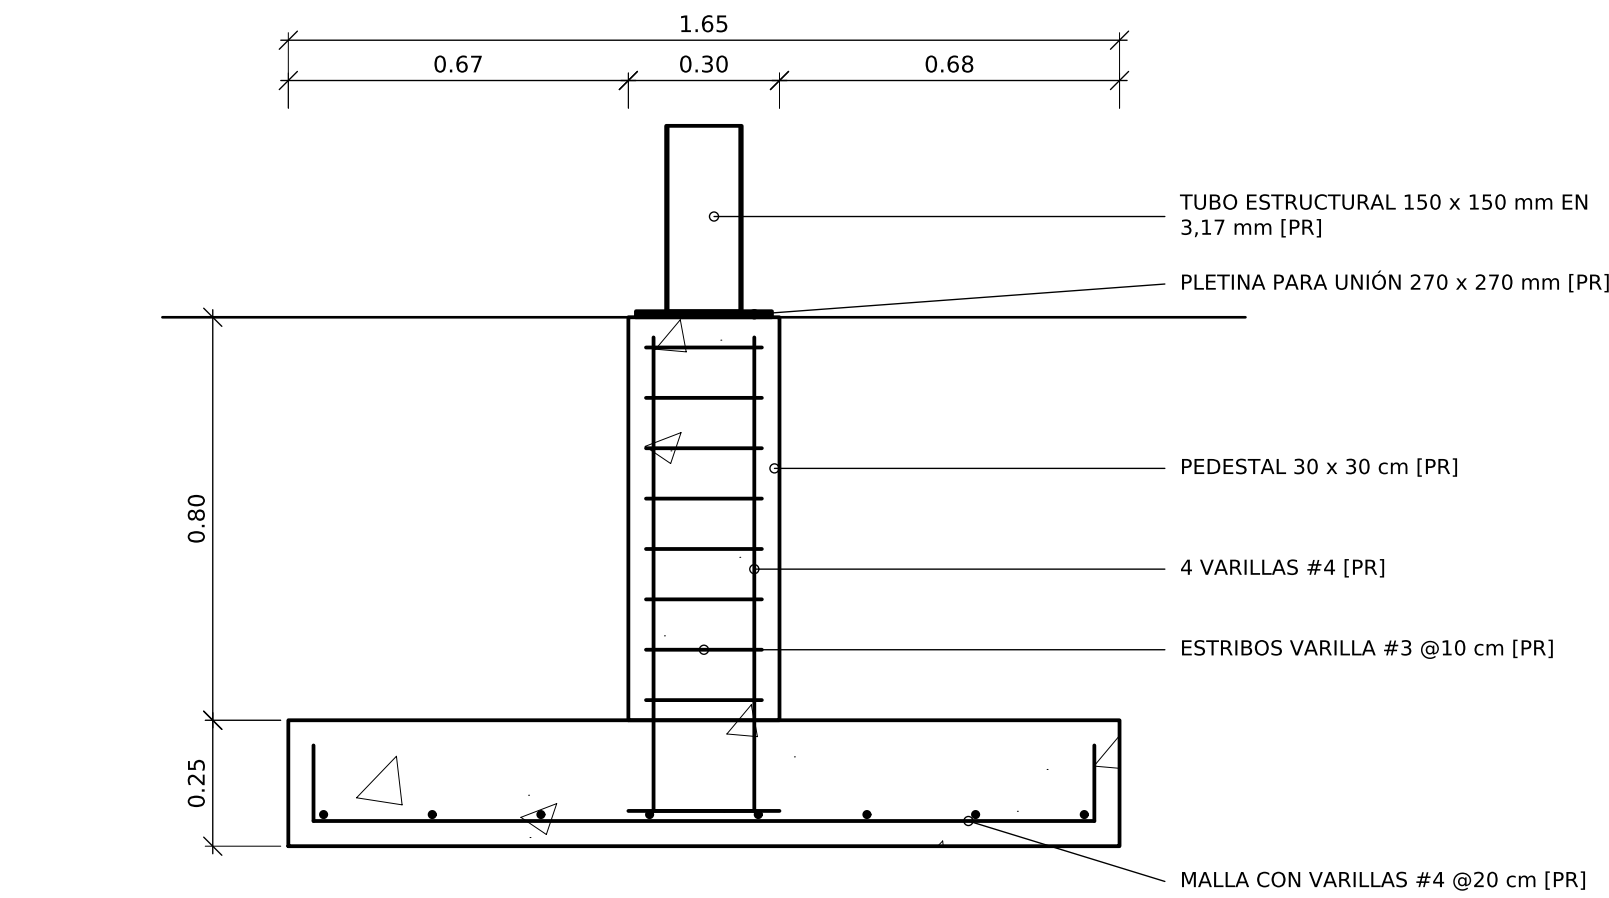


CORTE FUNDACIÓN F1 (CENTRADA)
Esc. 1:15

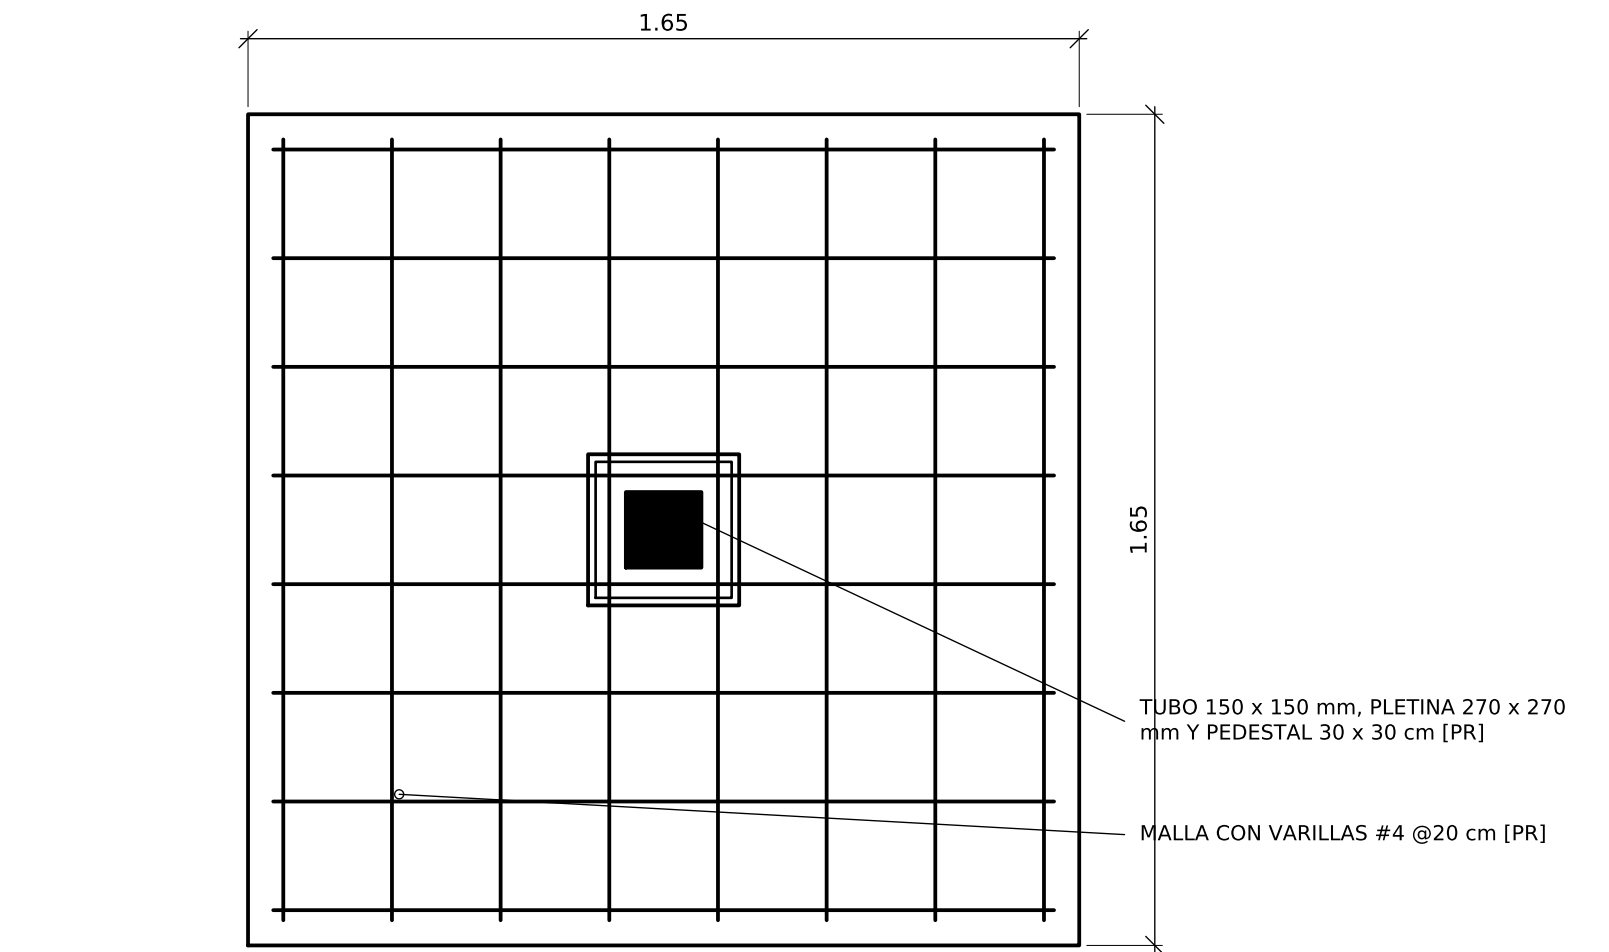


PLANTA FUNDACIÓN F1
Esc. 1:15

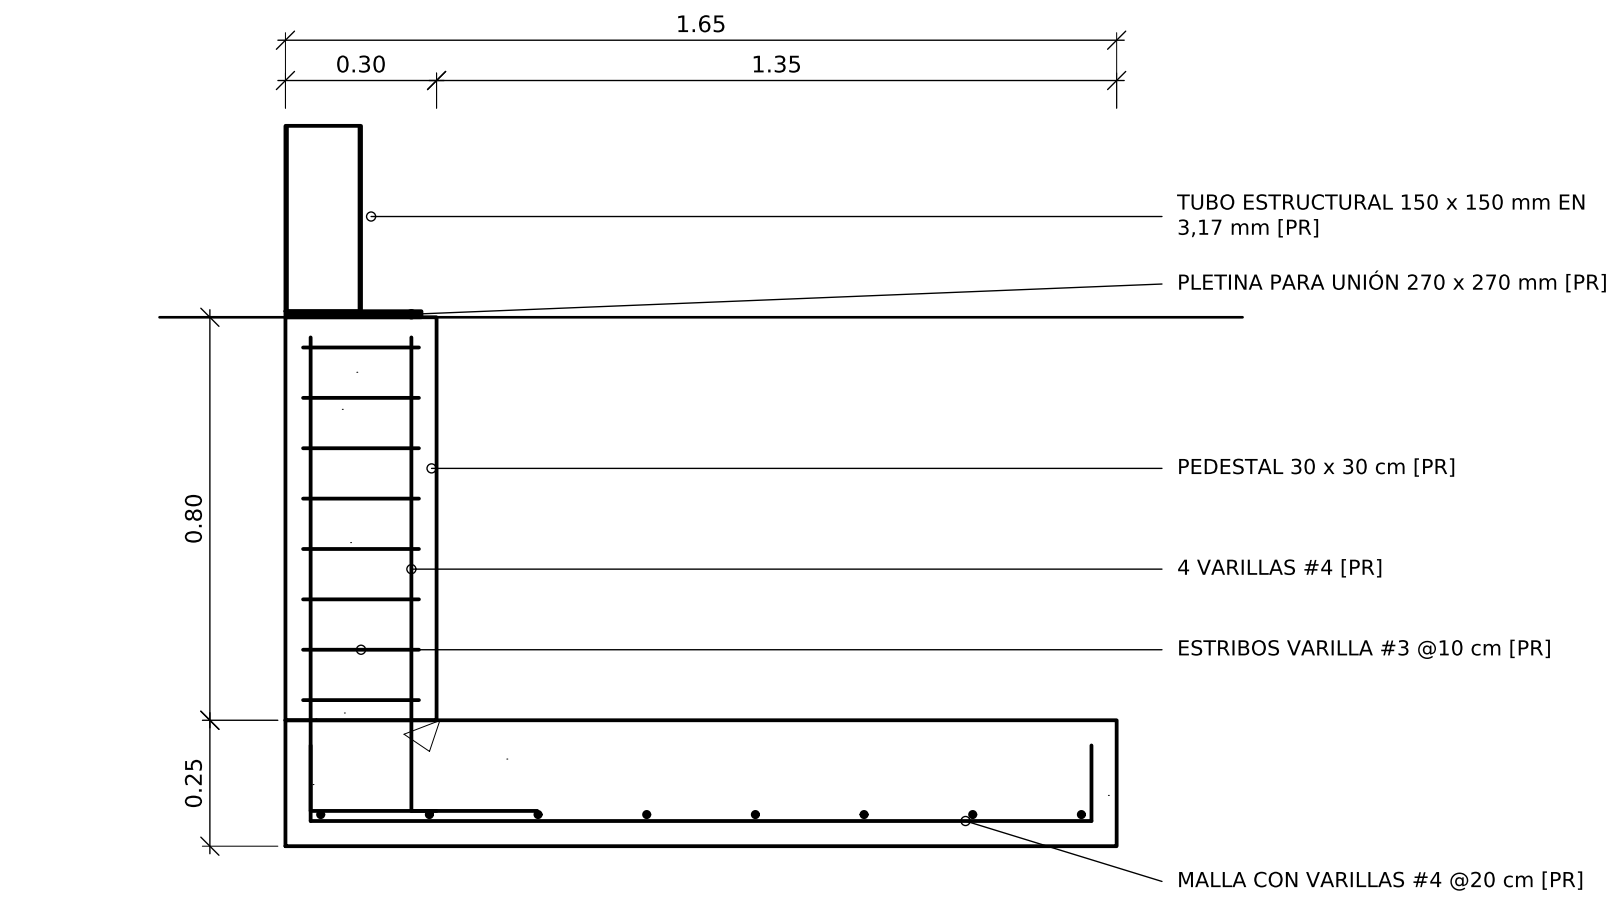

CORTE FUNDACIÓN F2 (EXCÉNTRICA, LINDERO)
Esc. 1:15

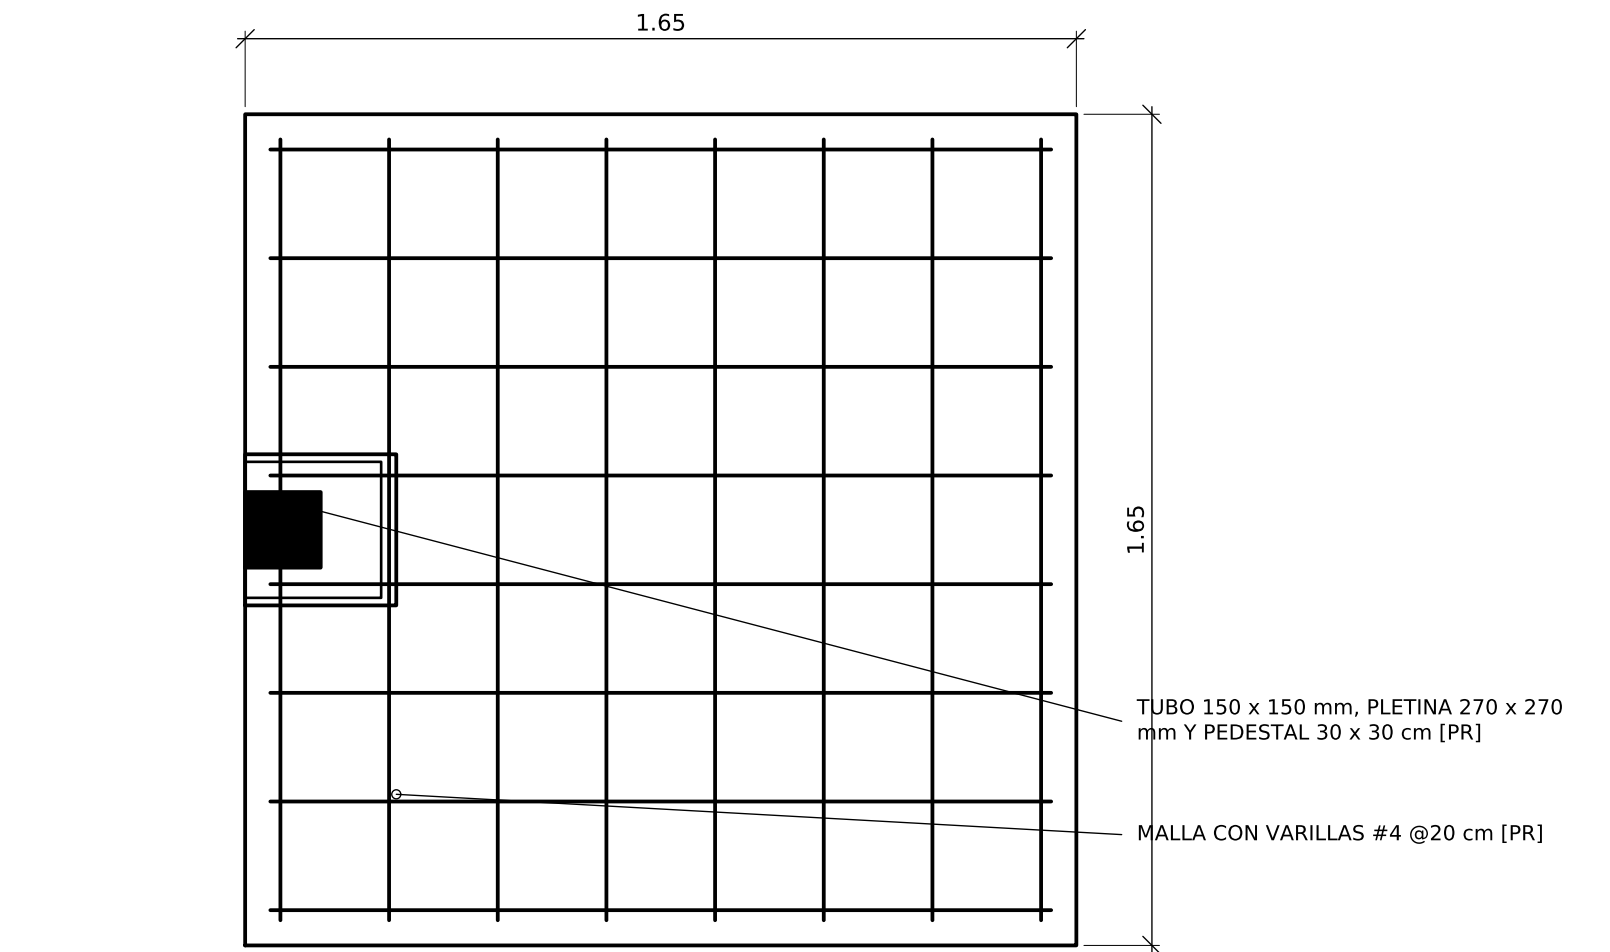

PLANTA FUNDACIÓN F2
Esc. 1:15

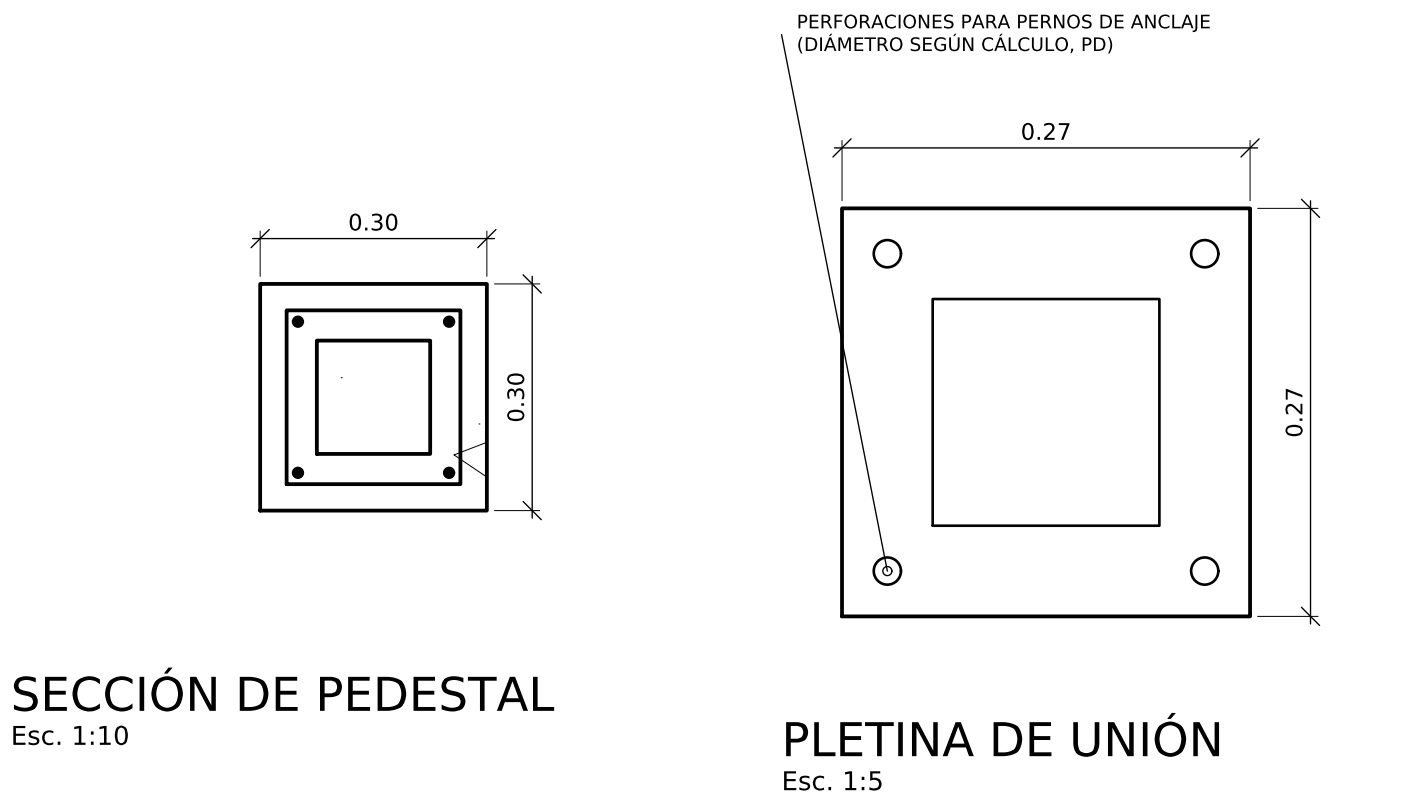

NOTAS:

- 1.- TODAS LAS MEDIDAS ESTÁN DADAS EN METROS, SALVO INDICACIÓN CONTRARIA. [PR]
- 2.- UBICACIÓN DE LAS FUNDACIONES F1 Y F2 SEGÚN LÁMINA C01.
- 3.- F1: PLACA CENTRADA BAJO LAS COLUMNAS DEL EJE C. F2: PLACA EXCÉNTRICA EN LOS LINDEROS (EJES A Y D), CON PEDESTAL Y TUBO A PAÑO DEL LINDERO; NO INVADE EL PREDIO VECINO.
- 4.- PLACAS DE 1,65 x 1,65 m CON MALLA DE VARILLAS #4 @20 cm EN AMBAS DIRECCIONES Y GANCHOS EN LOS EXTREMOS. RECUBRIMIENTO DE 5 cm EN ELEMENTOS COLADOS CONTRA EL TERRENO. [PR]
- 5.- PEDESTAL DE 30 x 30 cm Y 0,80 m DE ALTO, 4 VARILLAS #4 CON PATA DE 25 cm Y ESTRIBOS #3 @10 cm. [PR]
- 6.- COLUMNA: TUBO ESTRUCTURAL DE 150 x 150 mm EN 3,17 mm SOLDADO A PLETINA DE 270 x 270 mm ANCLADA AL PEDESTAL. PERNOS Y SOLDADURA SEGÚN CÁLCULO (PD). [PR]
- 7.- CAPACIDAD SOPORTANTE CONSIDERADA $q_{adm} = 12 \text{ t/m}^2$ [PR]. VERIFICAR CON ESTUDIO DE SUELOS.
- 8.- MATERIALES Y ESPECIFICACIONES SEGÚN LÁMINA C08. LAS SECCIONES SON LAS DEL PROYECTO DE REFERENCIA, POR INDICACIÓN DEL INGENIERO RESPONSABLE; NO SUSTITUYEN LA MEMORIA DE CÁLCULO.

[PR] = NOTA TOMADA DEL PROYECTO DE REFERENCIA, PENDIENTE DE REVISIÓN.

ESPACIO PARA SELLOS Y TIMBRES

CivilCon Diseño y Construcción SRLTDA Céd. Jurídica: 3-102-762712		
PROFESIONAL RESPONSABLE: DIRECTOR TÉCNICO: Steven Viales (Civil) IC-40759 David Barrantes (Electricidad) IE-27499		
PROYECTO: VIVIENDA UNIFAMILIAR DISTRITO 03 SANTIAGO, CANTÓN 05 SAN RAFAEL, PROVINCIA 04 HEREDIA, COSTA RICA.		
INFORMACIÓN REGISTRO PÚBLICO: FOLIO REAL: 4-041200-000 PLANO CATASTRADO: 4-57389-2023 ÁREA SEGÚN CATASTRO: 256 m²		
CONTENIDO: FUNDACIONES DETALLES. CORTE Y PLANTA F1 Y F2. SECCIÓN DE PEDESTAL. PLETINA DE UNIÓN. NOTAS.		
ESCALAS: INDICADAS		
CONTROL DE REVISIONES		
REV.	FECHA	DESCRIPCIÓN
0	06-10-2026	VERSIÓN DE TRABAJO PARA REVISIÓN
ESTADO:		
VERSIÓN DE TRABAJO NO APTA PARA CONSTRUCCIÓN NI TRÁMITE		
LUGAR		LÁMINA
COSTA RICA		C02
OCT 2026		TOTAL --