



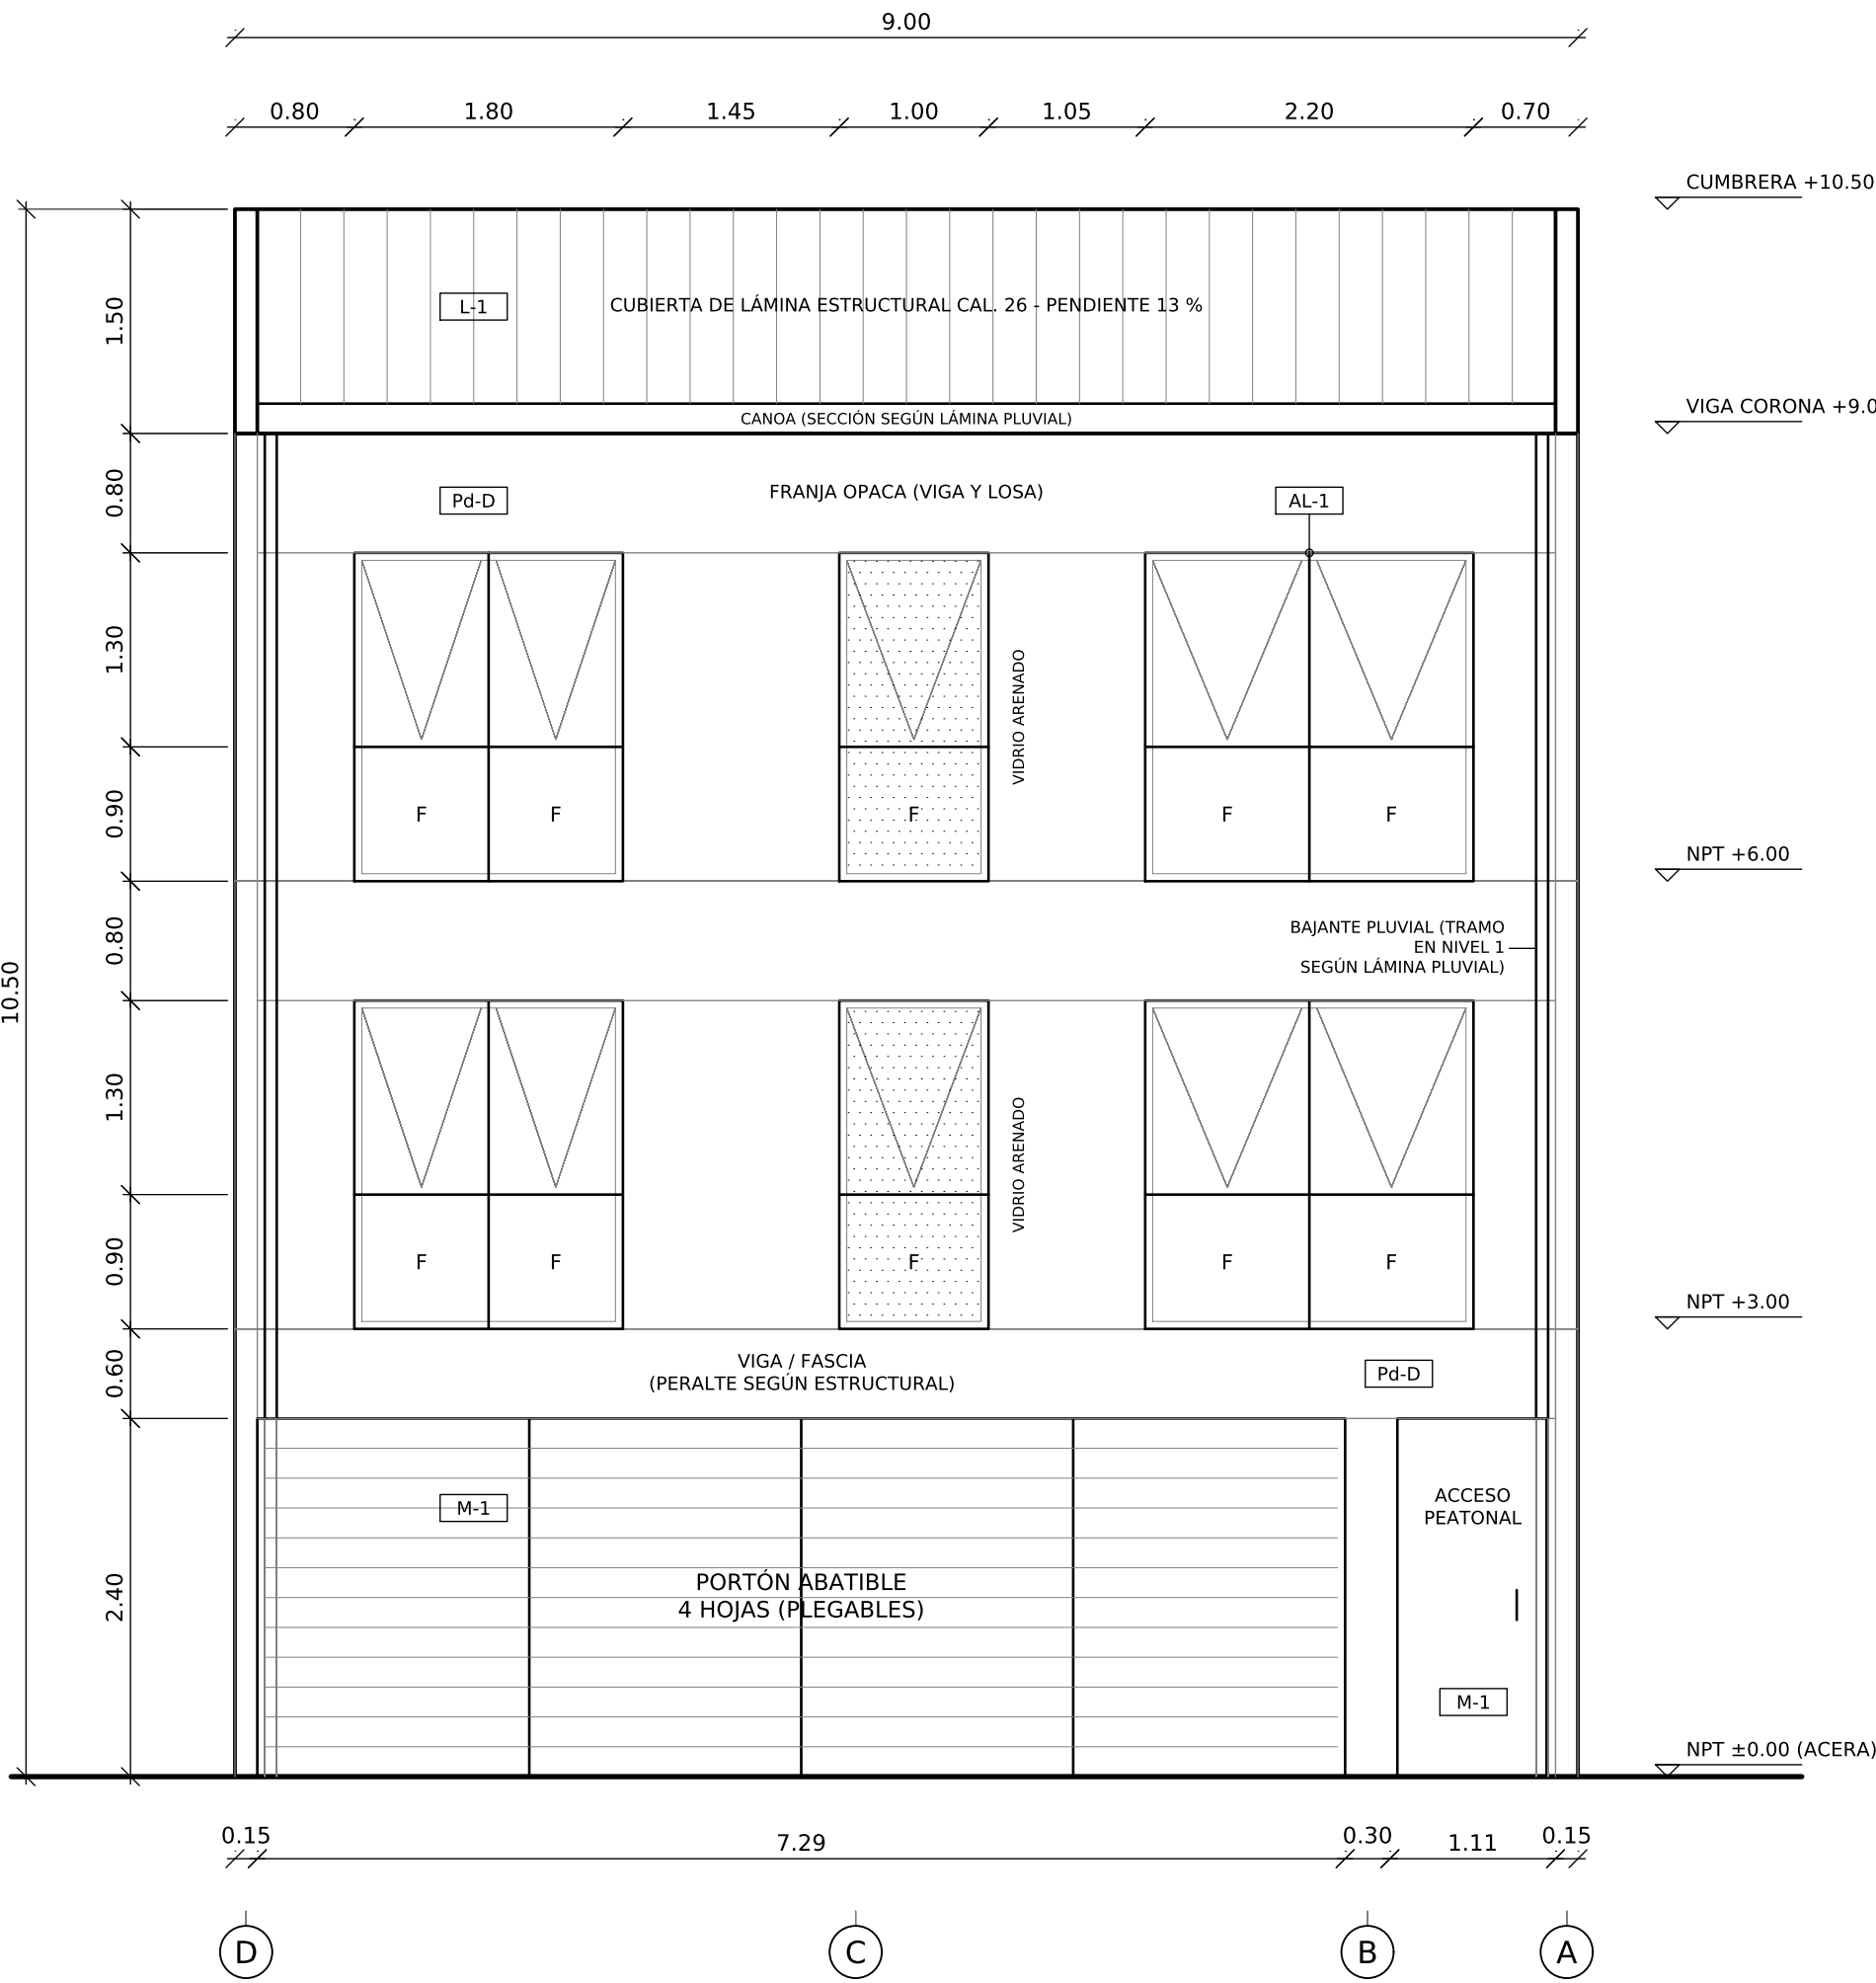


FACHADA PRINCIPAL (NORTE)
VISTA DESDE LA CALLE
Esc. 1:50

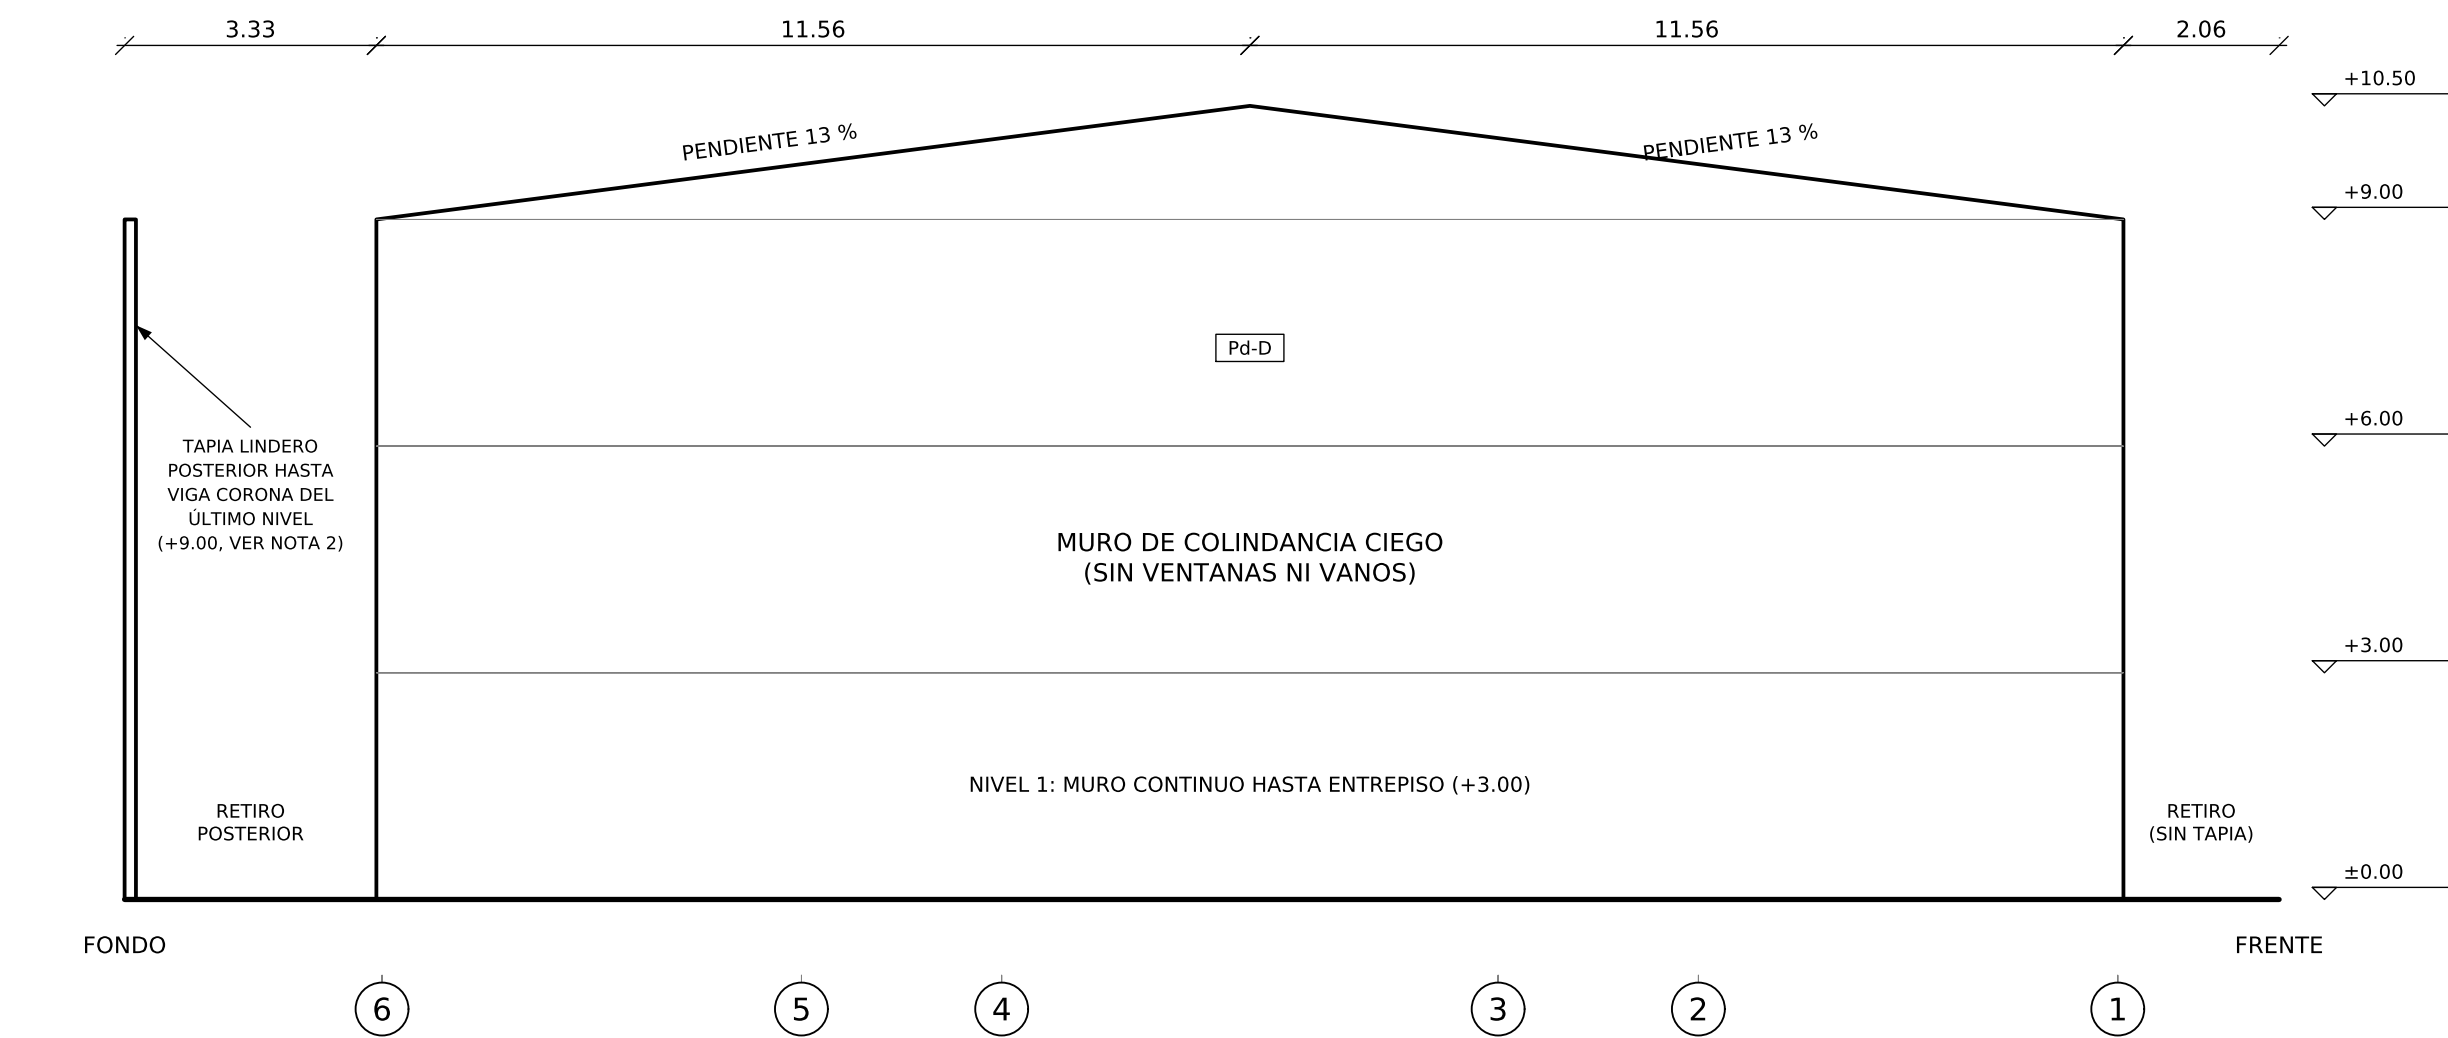

FACHADA LATERAL ESTE
MURO DE COLINDANCIA
Esc. 1:100



FACHADA POSTERIOR (SUR)
VISTA DESDE EL PATIO POSTERIOR
Esc. 1:75

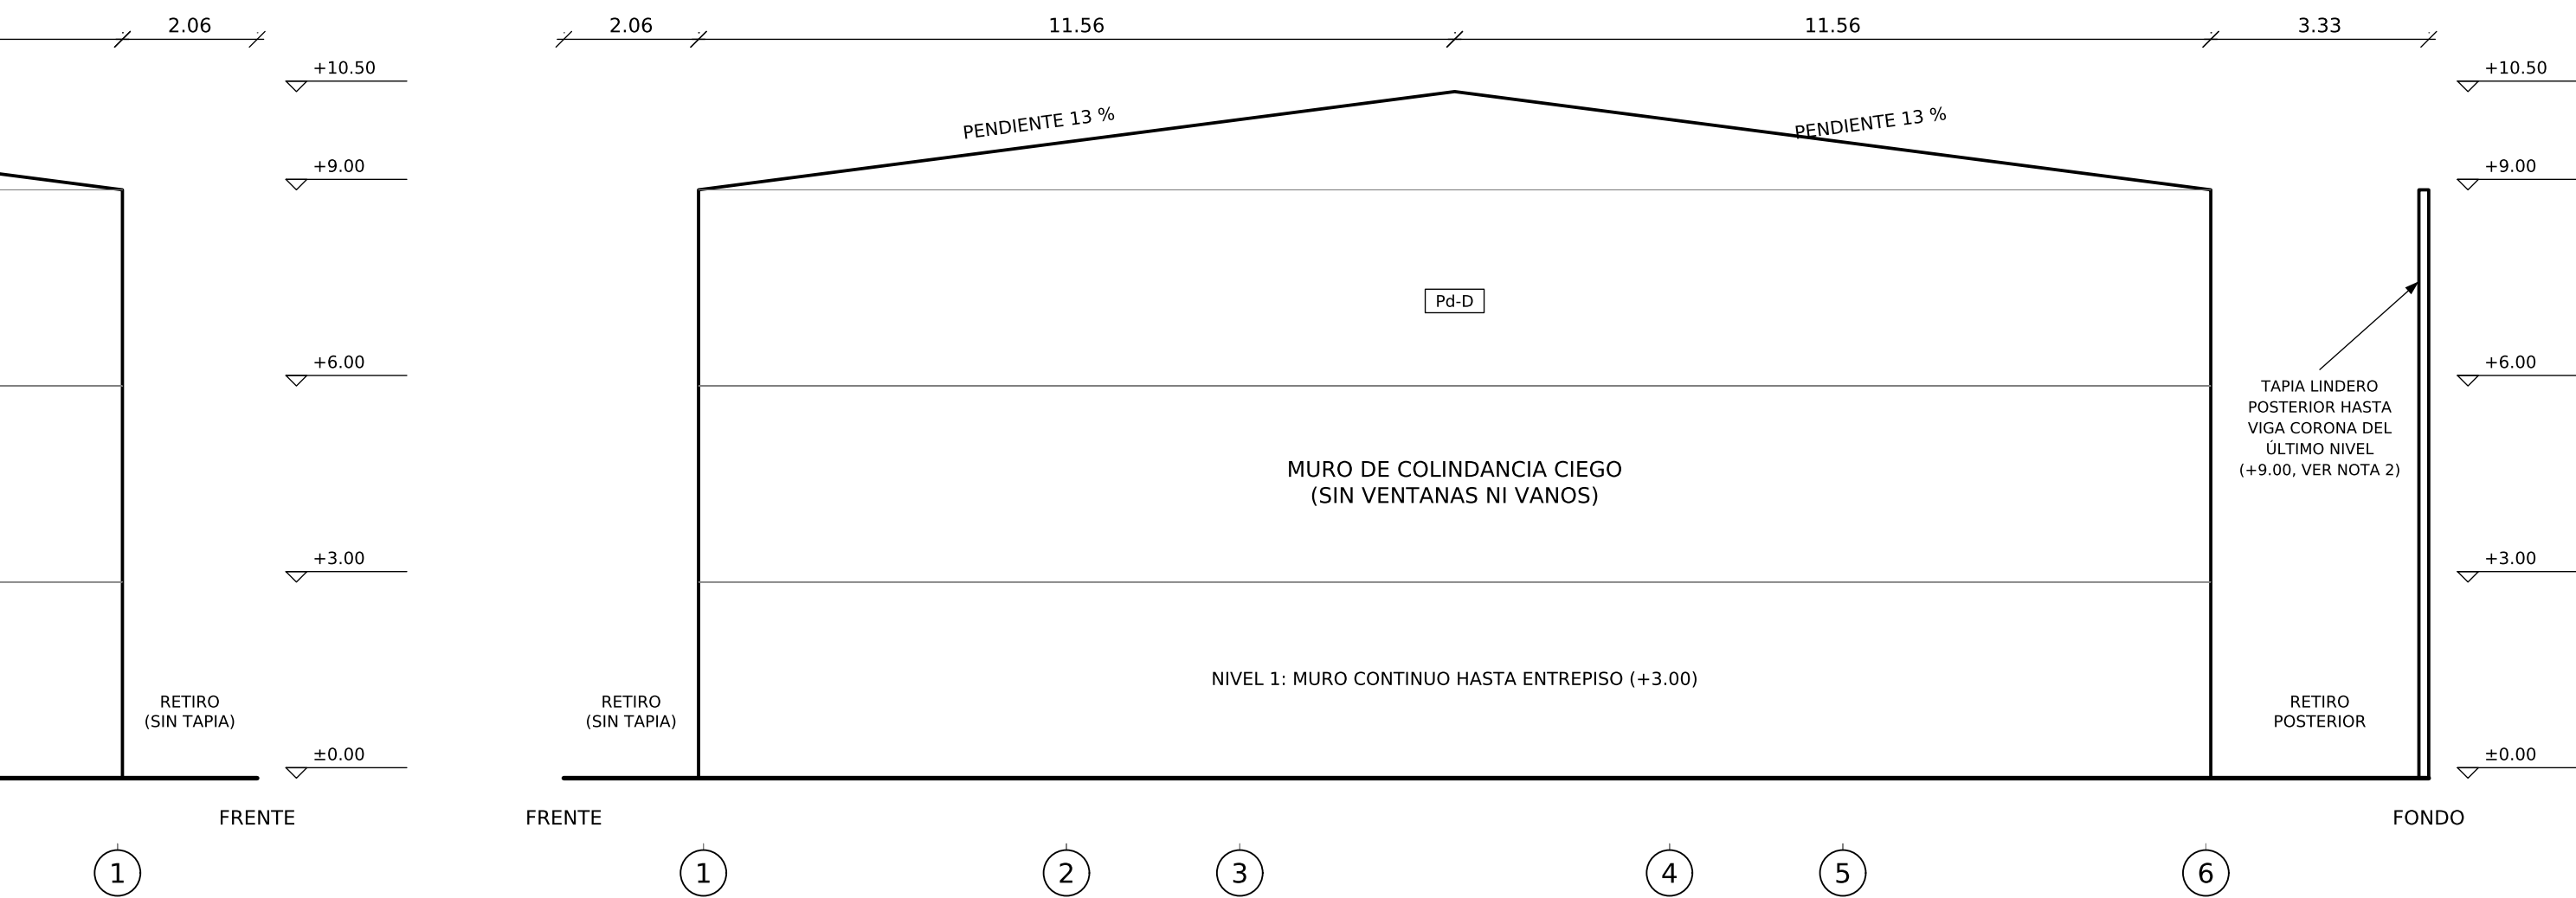

FACHADA LATERAL OESTE
MURO DE COLINDANCIA
Esc. 1:100

NOTAS:

- 1.- TODAS LAS MEDIDAS ESTÁN DADAS EN METROS, SALVO INDICACIÓN CONTRARIA. [PR]
 - 2.- LA TAPIA COLINDANTE DE MAMPOSTERÍA DEBERÁ PROLONGARSE HASTA EL NIVEL DE LA VIGA CORONA DEL ÚLTIMO NIVEL, GARANTIZANDO EL APANTALLAMIENTO VISUAL PERMANENTE HACIA LA PROPIEDAD COLINDANTE.
 - 3.- LOS BAÑOS CONTARÁN CON EXTRACTOR MECÁNICO DE AIRE.
 - 4.- NIVELES: NPT N1 ±0.00 (ACERA), N2 +3.00, N3 +6.00; VIGA CORONA Y ARRANQUE DE CUBIERTA +9.00.
 - 5.- CUBIERTA DE LÁMINA ESTRUCTURAL CALIBRE 26 A DOS AGUAS (HACIA EL FRENTE Y HACIA EL FONDO), PENDIENTE 13 %, CUMBRERA AL CENTRO DE LA VIVIENDA A +10.50 (REFERENCIAL). ESTRUCTURA DE TECHO SEGÚN PLANOS ESTRUCTURALES.
 - 6.- AGUAS PLUVIALES: CANOA FRONTAL Y CANOA POSTERIOR, CADA UNA CON 2 BAJANTES (UNO EN CADA EXTREMO), CONDUCIDOS HACIA LA CUNETETA DEL FRENTE. DIÁMETROS, UBICACIÓN DEFINITIVA Y TRAZADO SEGÚN LÁMINA PLUVIAL. CANOAS TAMBIÉN EN LOS BORDES DE CUBIERTA HACIA LOS PATIOS P1 Y P2 DONDE SE REQUIERA.
 - 7.- FACHADA PRINCIPAL: VENTANAS DE PISO A 2.20 m SOBRE NPT, ALINEADAS ENTRE NIVELES, CON PAÑO FIJO INFERIOR DE SEGURIDAD HASTA 0.90 m (F) Y FRANJA OPACA HASTA LA LOSA SUPERIOR (VIGAS). SOBRE EL PAÑO FIJO, VENTILAS ABATIBLES HACIA AFUERA.
 - 8.- TODAS LAS VENTANAS SON DE VENTILACIÓN: VENTILA ABATIBLE HACIA AFUERA (BISAGRA SUPERIOR), QUE ABIERTA FUNCIONA COMO ALERO ANTE LA LLUVIA. DONDE LA APERTURA HACIA AFUERA INTERFERIA CON UN PASILLO SE USARÁ VENTANA CORREDIZA DE DOS PAÑOS MÓVIL-MÓVIL. SOLO SON FIJOS LOS PAÑOS INFERIORES DE SEGURIDAD DE LA FACHADA PRINCIPAL.
 - 9.- BAÑOS Y VENTANA V-05 DE LA SALA: VIDRIO ARENADO (SANDBLAST). EN LA ZONA DE DUCHA EL VIDRIO DEBE QUEDAR SELLADO Y CON ANTEPECHO IMPERMEABLE O PANEL OPACO INTERIOR (POR DEFINIR).
 - 10.- FACHADA POSTERIOR: ANTEPECHO COMÚN DE 0.90 m Y DINTEL A 2.20 m SOBRE NPT, VENTANAS ALINEADAS ENTRE LOS NIVELES 2 Y 3, OPERABLES EN TODA SU ÁREA (EL ANTEPECHO DA LA PROTECCIÓN). LA VENTANA ANGOSTA (3.85 A 4.60) LIBRA LA COLUMNA C6.
 - 11.- FACHADAS LATERALES: MUROS DE COLINDANCIA CIEGOS, CONTINUOS DESDE EL NIVEL 1 (EN EL NIVEL 1 HASTA EL ENTREPISO +3.00), CON REMATE SUPERIOR SEGÚN LA PENDIENTE DE LA CUBIERTA. NO HAY TAPIAS LATERALES EN LOS RETIROS. LA TAPIA DEL LINDERO POSTERIOR LLEGA HASTA LA VIGA CORONA DEL ÚLTIMO NIVEL (+9.00), SEGÚN NOTA 2.
 - 12.- PORTÓN VEHICULAR Y PUERTA PEATONAL DE 2.40 m DE ALTURA. TIPOS DE VENTANAS Y PUERTAS EN LÁMINA A7. ACABADOS DE FACHADA SEGÚN CUADRO DE ESTA LÁMINA (ÍTEGRA LA A10).
- [PR] = NOTA TOMADA DEL PROYECTO DE REFERENCIA, PENDIENTE DE REVISIÓN.

SIMBOLOGÍA:

- VENTILA ABATIBLE HACIA AFUERA (BISAGRA SUPERIOR)
- F = PAÑO FIJO DE SEGURIDAD
- VIDRIO ARENADO (SANDBLAST)
- LÍNEA OCULTA (LOSA / NIVEL)

ACABADOS DE FACHADA:

CÓDIGO	ELEMENTO	ACABADO	COLOR
Pd-D	PARÉDES EXTERNAS Y MUROS DE COLINDANCIA	REPELLO GRUESO, ACABADO ESTUCO PULIDO	GRIS CONCRETO
AL-1	VENTANAS (MARCOS)	ALUMINIO Y VIDRIO (ARENADO EN BAÑOS Y V-05)	NEGRO
M-1	PORTÓN, PUERTA PEATONAL, CANOAS Y BAJANTES	METAL (ACERO)	NEGRO
L-1	CUBIERTA	LÁMINA ESTRUCTURAL CAL. 26	NATURAL GALVANIZADA

ESPACIO PARA SELLOS Y TIMBRES

CivilCon Diseño y Construcción SRLTDA
Céd. Jurídica: 3-102-762712

PROFESIONAL RESPONSABLE:
DIRECTOR TÉCNICO:
Steven Viales (Civil) IC-40759
David Barrantes (Electricidad) IE-27499

PROYECTO:
VIVIENDA UNIFAMILIAR
DISTRITO 03 SANTIAGO, CANTÓN 05 SAN RAFAEL,
PROVINCIA 04 HEREDIA, COSTA RICA.

INFORMACIÓN REGISTRO PÚBLICO:
FOLIO REAL: 4-041200-000
PLANO CATASTRADO: 4-57389-2023
ÁREA SEGÚN CATASTRO: 256 m²

CONTENIDO:
FACHADAS
FACHADA PRINCIPAL (NORTE).
FACHADA POSTERIOR (SUR).
FACHADA LATERAL ESTE.
FACHADA LATERAL OESTE.
NOTAS.
ACABADOS DE FACHADA.

ESCALAS: 1:50 / INDICADAS

CONTROL DE REVISIONES		
REV.	FECHA	DESCRIPCIÓN
3	06-10-2026	SÍMBOLO DE VENTILA INVERTIDO
4	06-10-2026	V-05 SALA ARENADO; REFERENCIA A7
5	06-10-2026	ACABADOS DE FACHADA (ÍTEGRA A10)

ESTADO:
VERSIÓN DE TRABAJO
NO APTA PARA CONSTRUCCIÓN NI TRÁMITE

LUGAR	LÁMINA
COSTA RICA	A5
OCT 2026	TOTAL --