




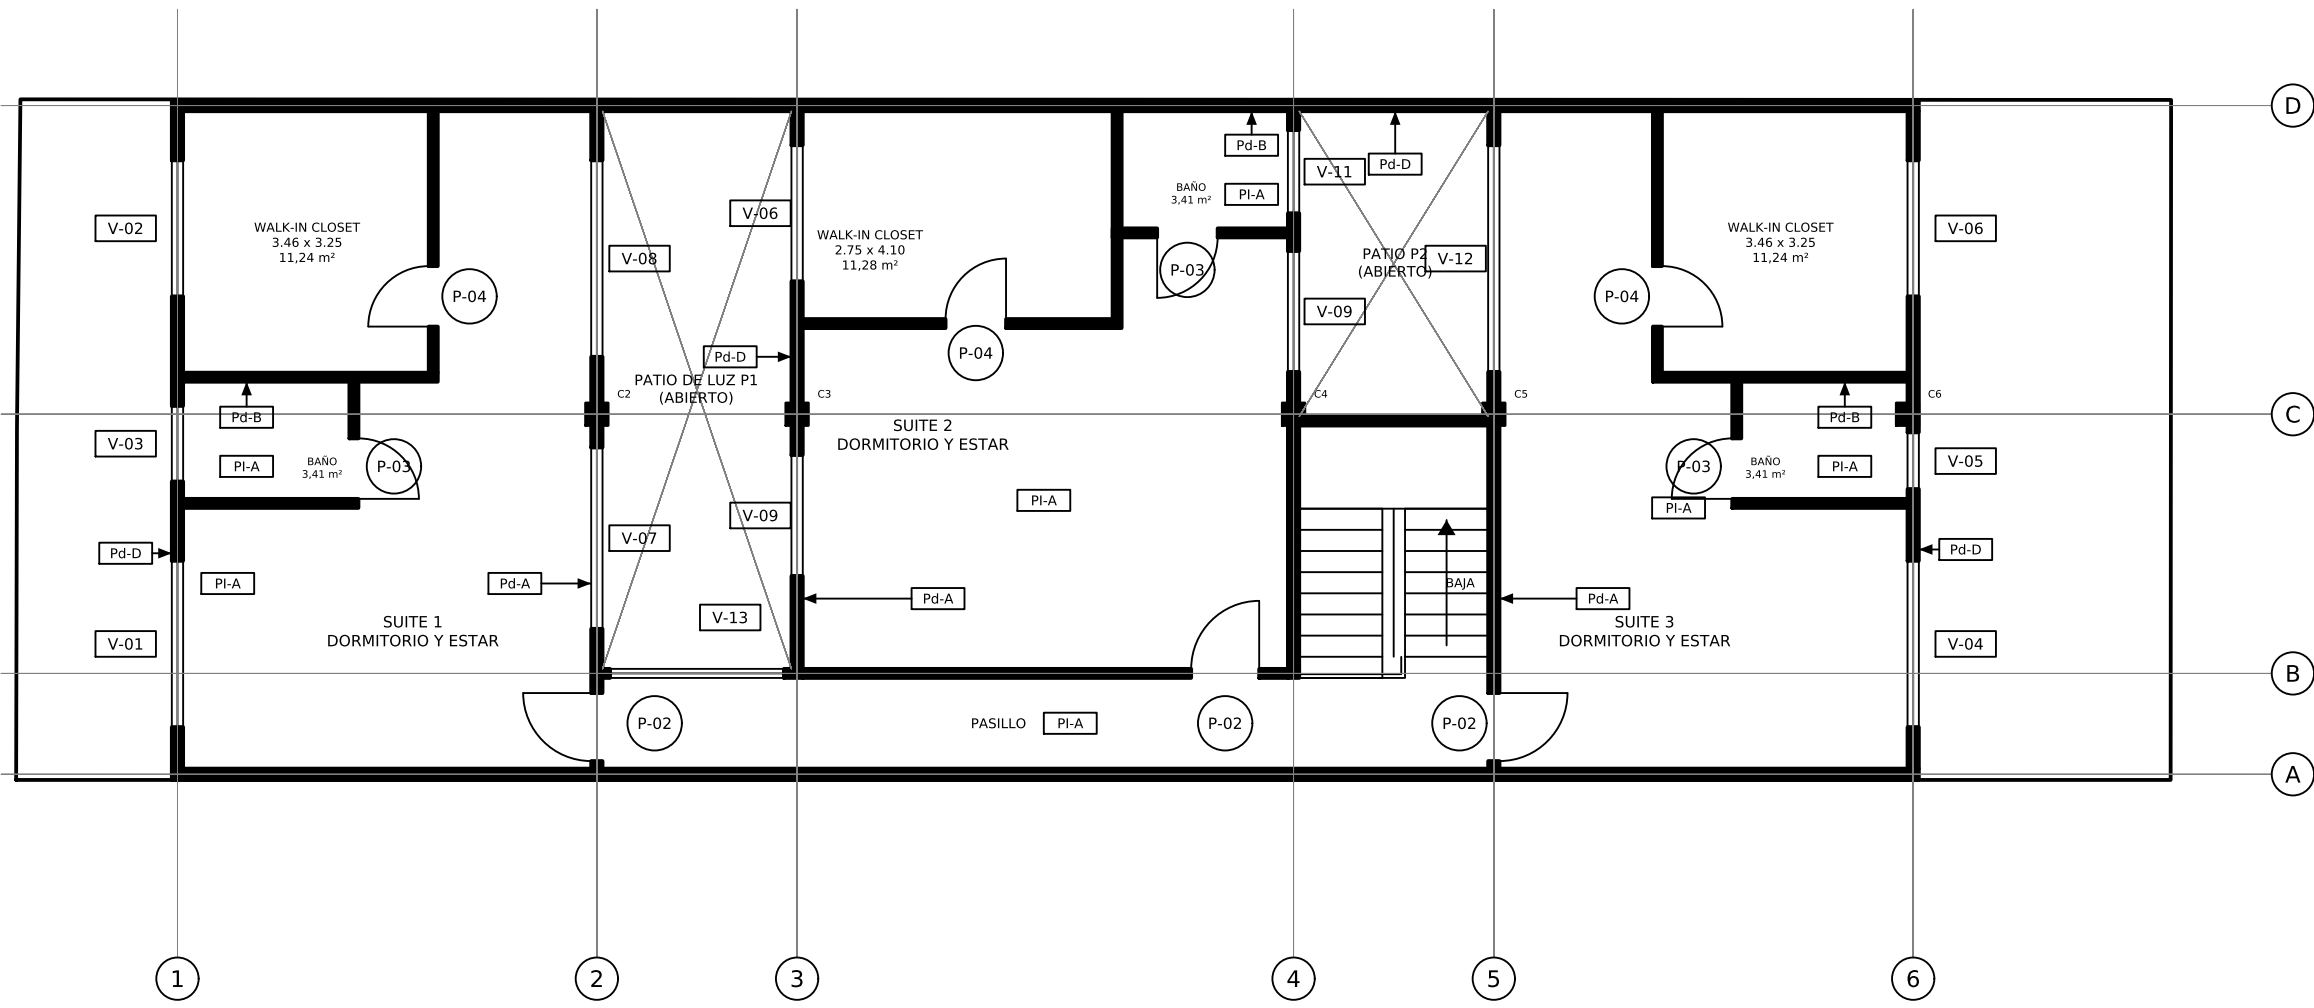

PLANTA NIVEL 3
PUERTAS, VENTANAS Y ACABADOS - Esc. 1:100

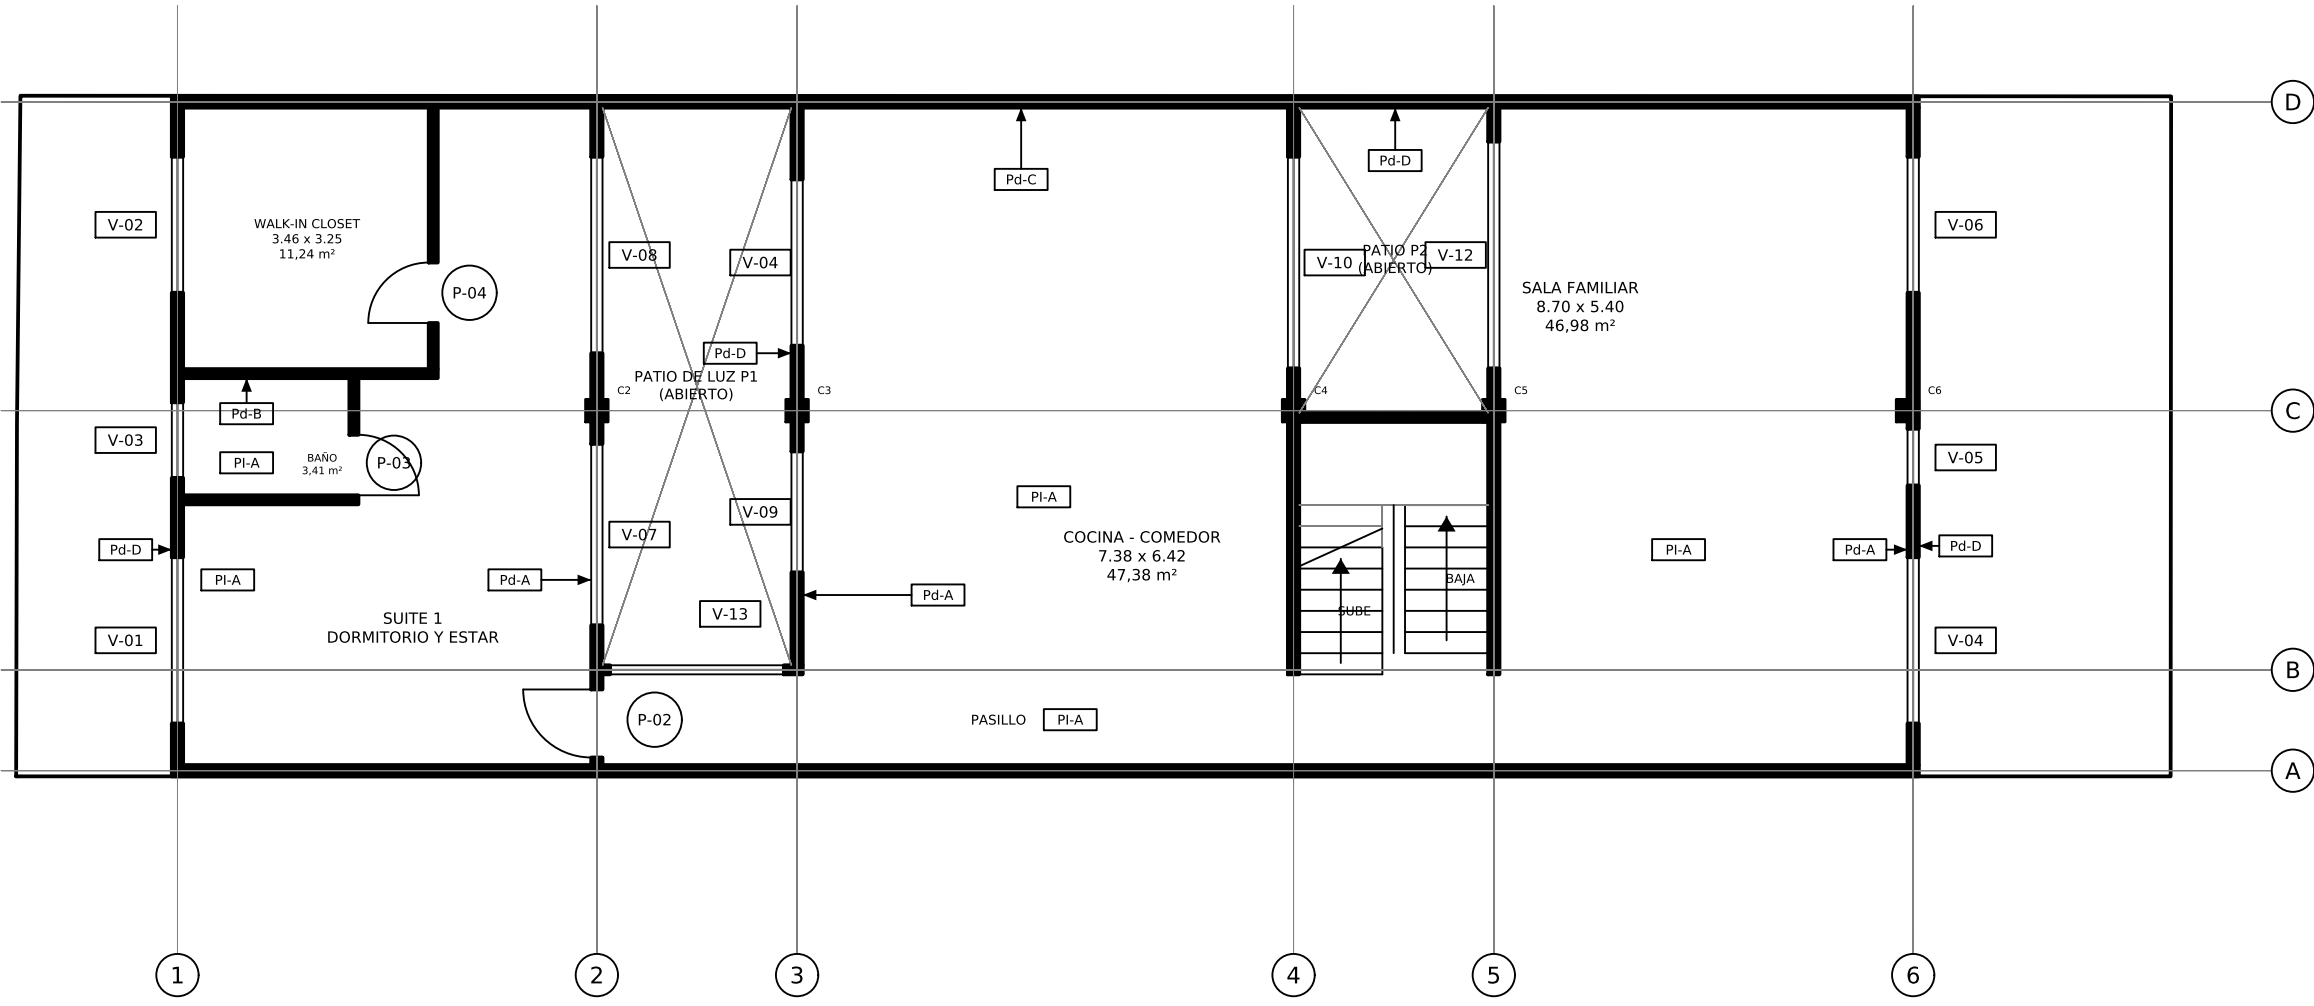


PLANTA NIVEL 2
PUERTAS, VENTANAS Y ACABADOS - Esc. 1:100

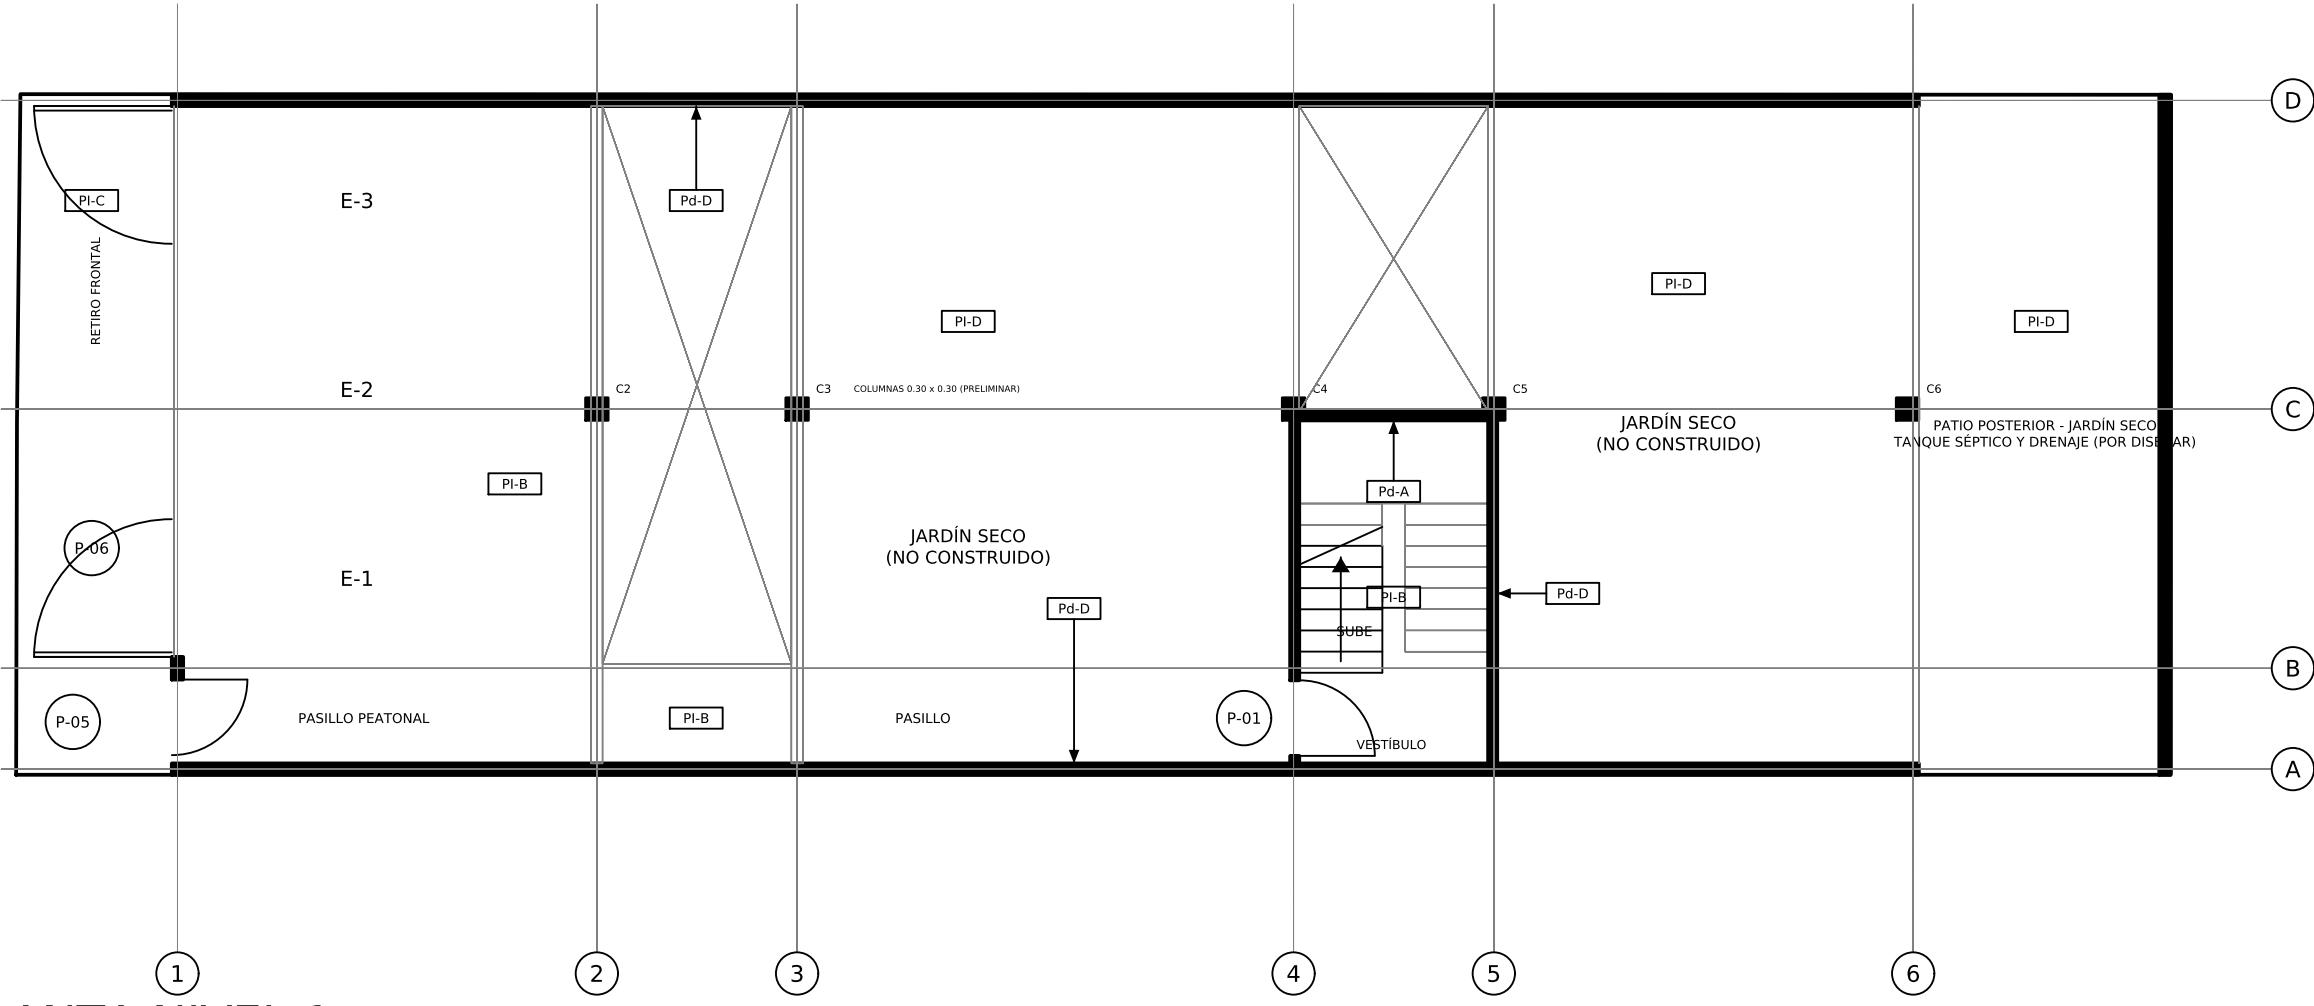

PLANTA NIVEL 1
PUERTAS, VENTANAS Y ACABADOS - Esc. 1:100

DETALLE VENTANAS
Esc. 1:75 - VISTA EXTERIOR

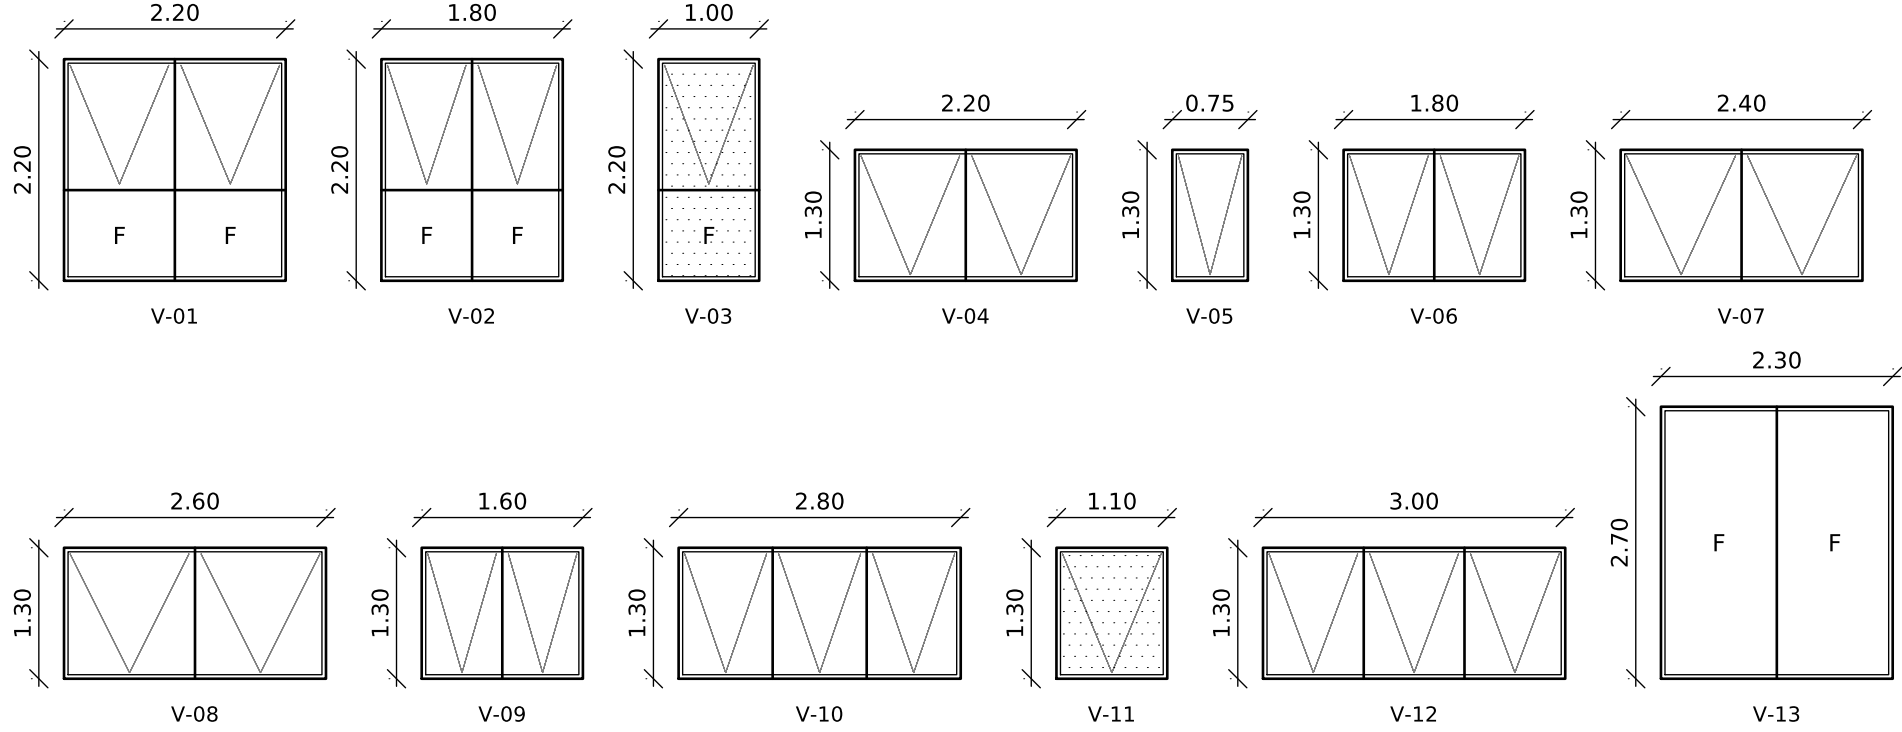


CUADRO DE PUERTAS (UNIDADES EN METROS)					
PUERTA	ANCHO	ALTO	TIPO	CANT	UBICACIÓN
P-01	1,00	2,10	BATIENTE	1	ACCESO PPAL. (VESTIBULO NIVEL 1)
P-02	0,90	2,10	BATIENTE	4	HABITACIONES (SUITES 1, 2 Y 3)
P-03	0,80	2,10	BATIENTE	4	BAÑOS
P-04	0,80	2,10	BATIENTE	4	WALK-IN CLOSET
P-05	1,00	2,40	BATIENTE	1	PUERTA PEATONAL (FRENTE NIVEL 1)
P-06	7,29	2,40	ABATIBLE 4 HOJAS	1	PORTÓN VEHICULAR (FRENTE NIVEL 1)

CUADRO DE VENTANAS (UNIDADES EN METROS)					
VENTANA	ANCHO	ALTO	TIPO	CANT	UBICACIÓN
V-01	2,20	2,20	FIJA INF. + VENTILA ABATIBLE	2	DORMITORIO SUITE 1, FACHADA PRINCIPAL (N2 Y N3)
V-02	1,80	2,20	FIJA INF. + VENTILA ABATIBLE	2	WALK-IN SUITE 1, FACHADA PRINCIPAL (N2 Y N3)
V-03	1,00	2,20	FIJA INF. + VENTILA ABATIBLE	2	BAÑO SUITE 1, FACHADA PRINCIPAL (VIDRIO ARENADO)
V-04	2,20	1,30	VENTILA ABATIBLE	3	SALA Y SUITE 3, FACHADA POSTERIOR; COCINA A P1 (N2)
V-05	0,75	1,30	VENTILA ABATIBLE	2	FACHADA POSTERIOR: SALA (N2) Y BAÑO SUITE 3 (ARENADO)
V-06	1,80	1,30	VENTILA ABATIBLE	3	FACHADA POSTERIOR (N2 Y N3); WALK-IN SUITE 2 A P1
V-07	2,40	1,30	VENTILA ABATIBLE	2	SUITE 1 HACIA PATIO P1 (N2 Y N3)
V-08	2,60	1,30	VENTILA ABATIBLE	2	WALK-IN SUITE 1 HACIA PATIO P1 (N2 Y N3)
V-09	1,60	1,30	VENTILA ABATIBLE	3	COCINA (N2) Y SUITE 2 (N3) A P1; SUITE 2 A P2
V-10	2,80	1,30	VENTILA ABATIBLE	1	COCINA HACIA PATIO P2 (N2)
V-11	1,10	1,30	VENTILA ABATIBLE	1	BAÑO SUITE 2 HACIA PATIO P2 (N3, VIDRIO ARENADO)
V-12	3,00	1,30	VENTILA ABATIBLE	2	SALA (N2) Y SUITE 3 (N3) HACIA PATIO P2
V-13	2,30	2,70	FIJA	2	GALERÍA DEL PASILLO HACIA PATIO P1 (N2 Y N3)

ITEM	TIPO DE ACABADO	COLOR
Pd - A	PAREDES INTERNAS: REPELLO GRUESO, ACABADO LISO, CON DOS MANOS DE PINTURA CLASE A, CON BASE SATINADO.	REFERENCIA: PANTONE, ALMOND MILK
Pd - B	BAÑOS: REPELLO GRUESO, ACABADO CON CERÁMICA O PORCELANATO. 1,80 m EN DUCHAS.	BLANCO
Pd - C	COCINA: REPELLO GRUESO, ACABADO CON CERÁMICA O PORCELANATO EN SALPICADERO.	BLANCO
Pd - D	PAREDES EXTERNAS: REPELLO GRUESO, ACABADO ESTUCO PULIDO.	GRIS CONCRETO

ITEM	TIPO DE ACABADO	COLOR
PI - A	PISO PARA INTERIORES Y BAÑOS, PORCELANATO 60x60CM BLANCO O COLOR CLARO CON RODAPIE DE PORCELANATO.	BLANCO
PI - B	CONTRAPISO DE CONCRETO DE 0,10 m (ESTACIONAMIENTOS, PASILLO, VESTIBULO Y GRADAS DEL NIVEL 1).	GRIS CONCRETO
PI - C	ZACATE BLOCK (PERMEABLE) EN RETIRO FRONTAL.	NATURAL
PI - D	GRAVA (JARDIN SECO).	NATURAL

ITEM	TIPO DE ACABADO	COLOR
CIELO RASO TIPO GYPSUM (REGULAR PLANO, SUSPENDIDO A 2,70 m), NIVELES 2 Y 3.		BLANCO
NIVEL 1: ESTRUCTURA DE ACERO EXPUESTA (SIN CIELO RASO).		SEGÚN ESTRUCTURAL

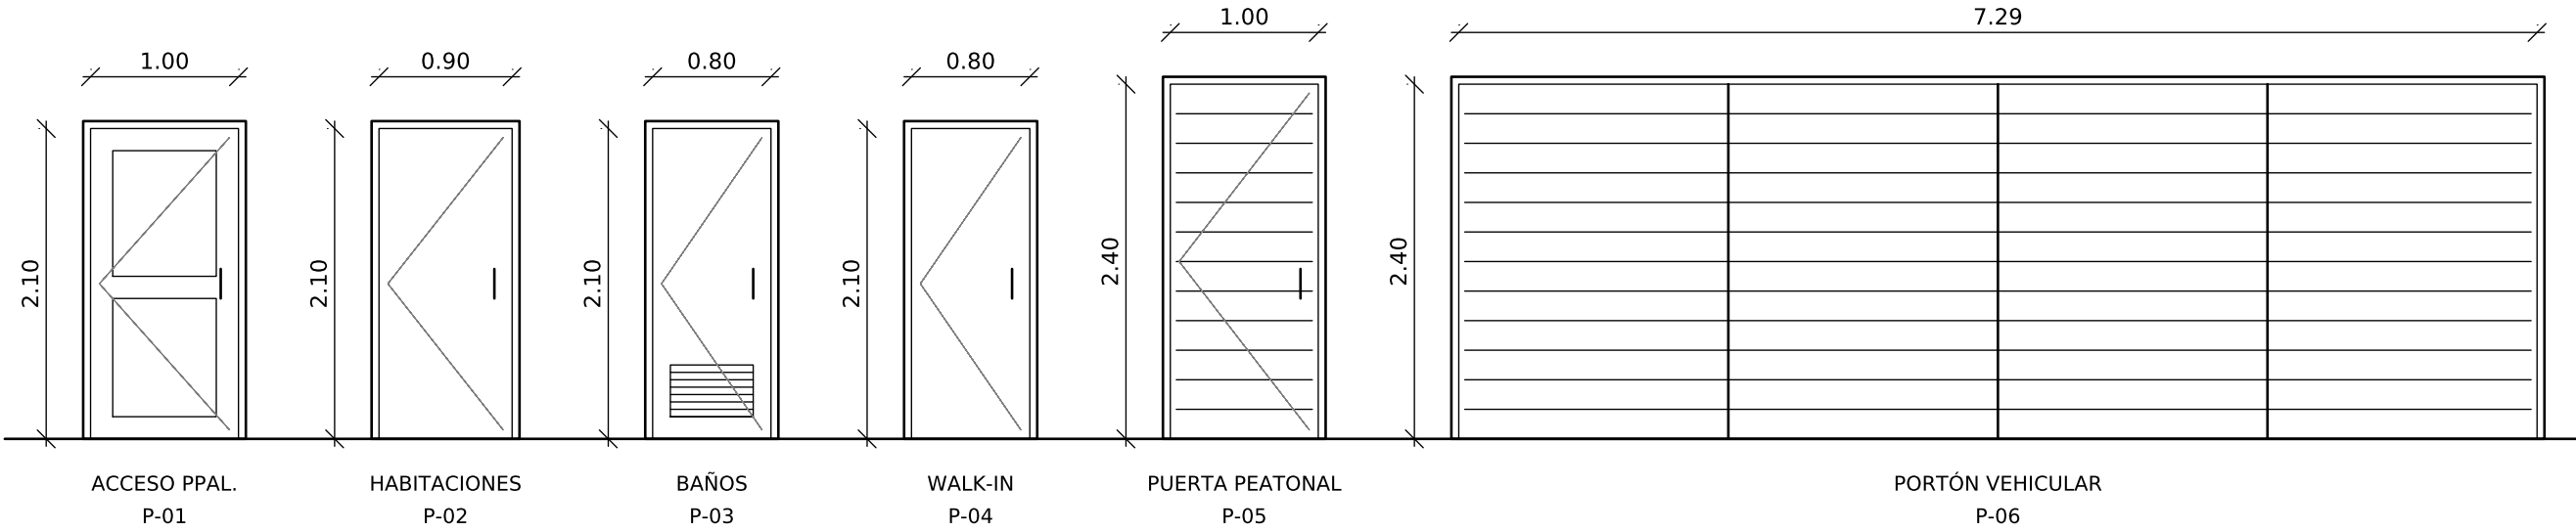

DETALLE PUERTAS
Esc. 1:50 - VISTA DESDE EL LADO DE APERTURA

NOTAS:
1.- TODAS LAS MEDIDAS ESTÁN DADAS EN METROS. [PR]
2.- EL NIVEL ±0.00 ES EL NIVEL DE ACERA (NPT DEL NIVEL 1); N2 +3.00 Y N3 +6.00.
3.- LAS MEDIDAS DEBEN SER VERIFICADAS EN SITIO. [PR]
4.- LOS MARCOS DE LAS VENTANAS SERÁN DE ALUMINIO COLOR NEGRO. [PR]
5.- VENTANAS: VENTILA ABATIBLE HACIA AFUERA (BISAGRA SUPERIOR, TRIÁNGULO INVERTIDO); F = PAÑO FIJO. FACHADA PRINCIPAL DE 0.00 A 2.20 m CON PAÑO FIJO INFERIOR DE SEGURIDAD HASTA 0.90 m; LAS DEMÁS CON ANTEPECHO DE 0.90 m Y DINTEL A 2.20 m. VIDRIO ARENADO EN BAÑOS.
6.- PUERTAS DE 2.10 m DE ALTO. P-05 Y P-06 (2.40 m) METÁLICAS SEGÚN FACHADA AS.
7.- PLANTAS SIN MOBILIARIO NI COTAS; DISTRIBUCIÓN Y MEDIDAS SEGÚN LÁMINAS A2, A3 Y A4.
[PR] = NOTA TOMADA DEL PROYECTO DE REFERENCIA, PENDIENTE DE REVISIÓN.

ESPACIO PARA SELLOS Y TIMBRES

CivilCon Diseño y Construcción SRLTDA Céd. Jurídica: 3-102-762712	
PROFESIONAL RESPONSABLE: DIRECTOR TÉCNICO: Steven Viales (Civil) IC-40759 David Barrantes (Electricidad) IE-27499	
PROYECTO: VIVIENDA UNIFAMILIAR DISTRITO 03 SANTIAGO, CANTÓN 05 SAN RAFAEL, PROVINCIA 04 HEREDIA, COSTA RICA.	
INFORMACIÓN REGISTRO PÚBLICO: FOLIO REAL: 4-041200-000 PLANO CATASTRADO: 4-57389-2023 ÁREA SEGÚN CATASTRO: 256 m²	
CONTENIDO: PUERTAS Y VENTANAS PLANTAS NIVELES 1, 2 Y 3. CUADROS DE PUERTAS Y VENTANAS. ACABADOS EN PAREDES, PISOS Y CIELOS. DETALLE DE PUERTAS Y VENTANAS. NOTAS.	
ESCALAS: 1:100 / INDICADAS	
CONTROL DE REVISIONES	
REV.	FECHA
0	06-10-2026
DESCRIPCIÓN	
VERSIÓN DE TRABAJO PARA REVISIÓN	
ESTADO:	
VERSIÓN DE TRABAJO NO APTA PARA CONSTRUCCIÓN NI TRÁMITE	
LUGAR	LÁMINA
COSTA RICA	A7
OCT 2026	TOTAL --