



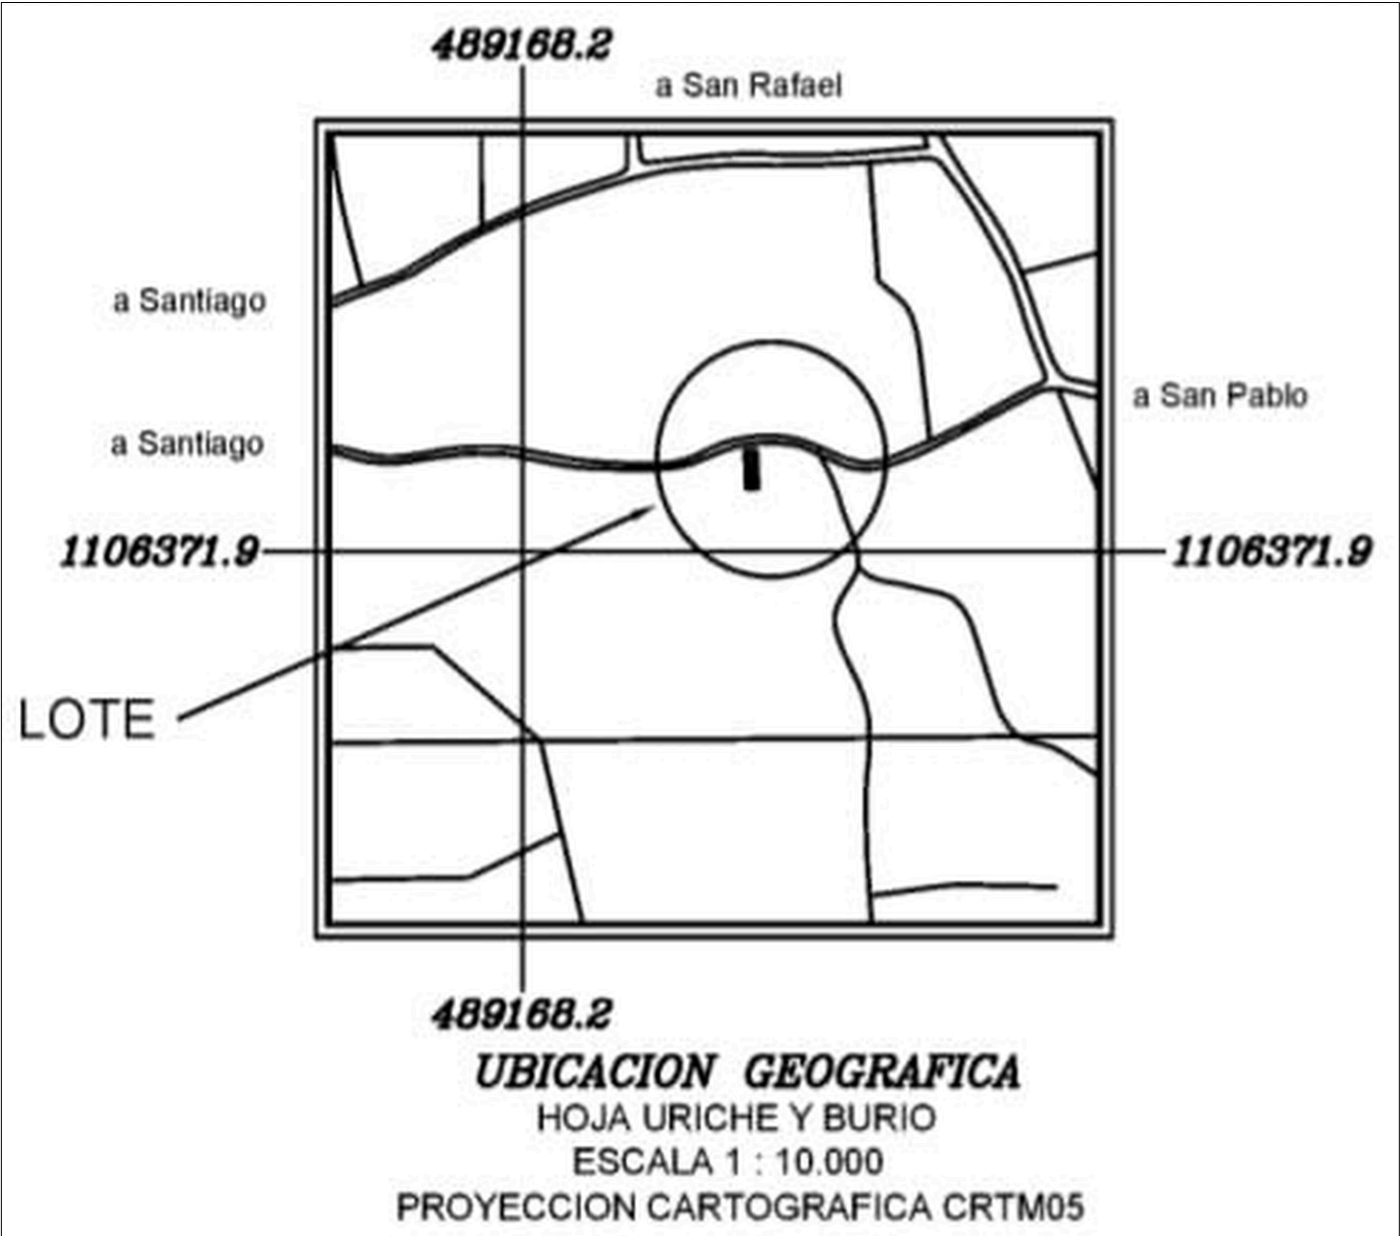



UBICACIÓN GEOGRÁFICA

LOTE DE TERRENO
Esc. S/E (imagen tomada del plano catastrado 4-57389-2023)

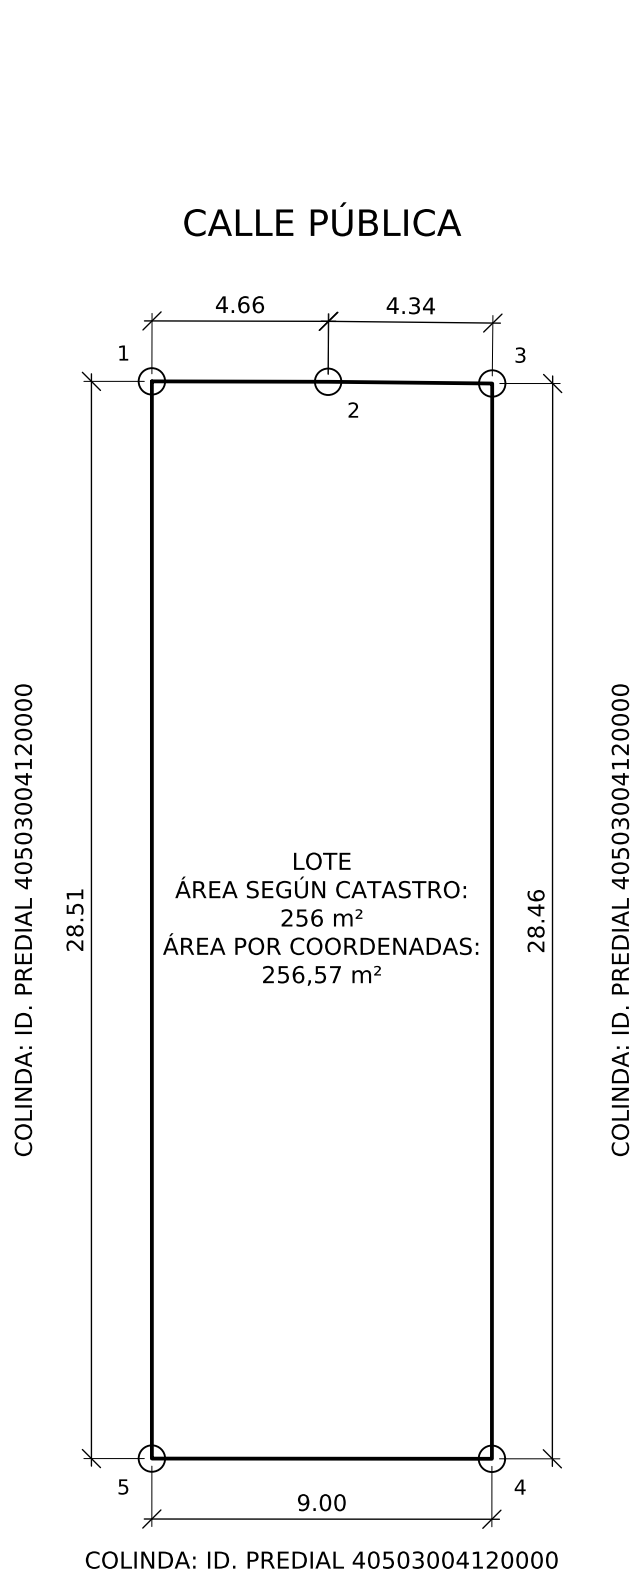



POLIGONAL TERRENO

LOTE DE TERRENO
Esc. 1:200

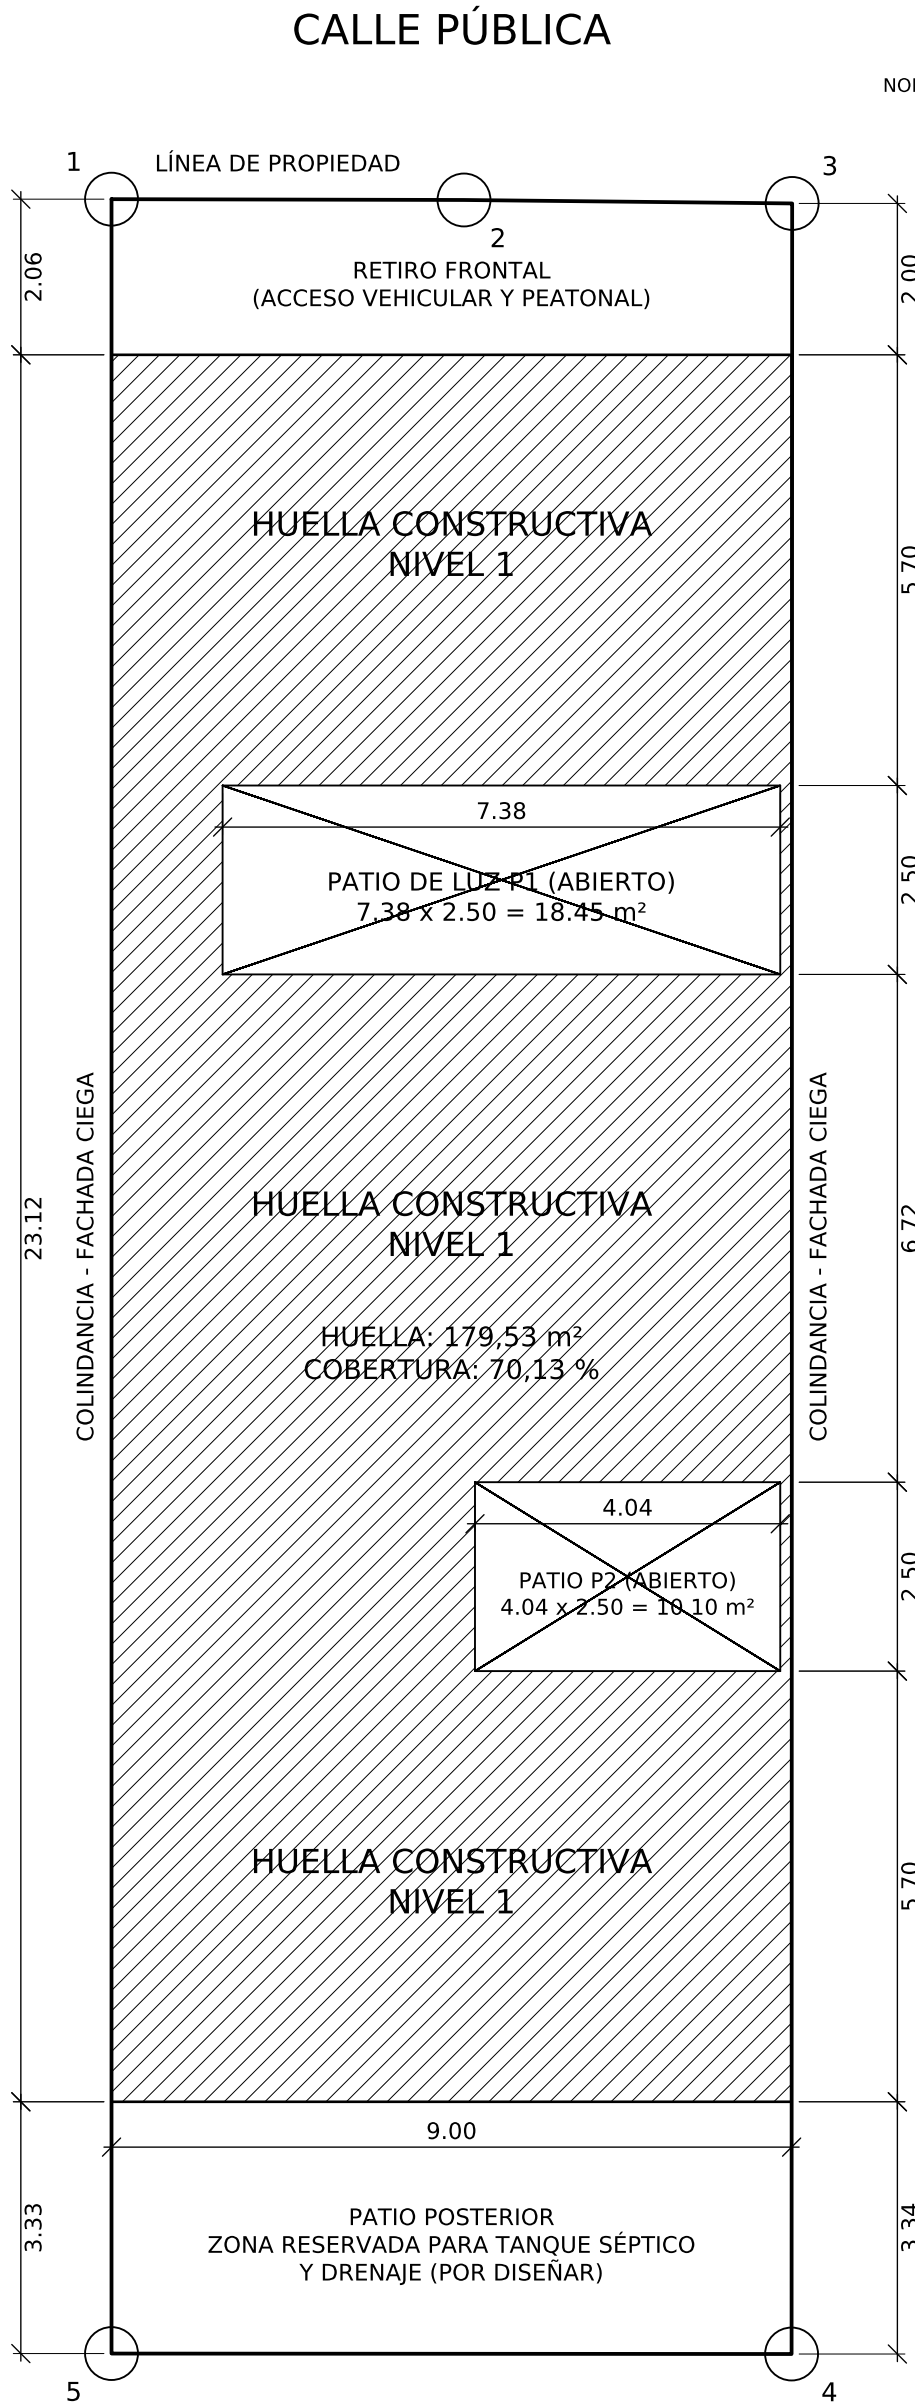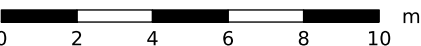

RETIROS Y HUELLA

LOTE DE TERRENO - NIVEL 1
Esc. 1:100

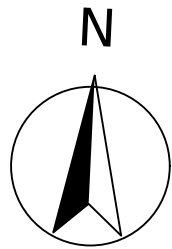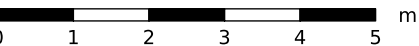

NORTE SEGÚN PLANO CATASTRADO (CRTM05)

DERROTERO

LÍNEA	ACIMUT		DISTANCIA	
	°	'	m	cm
1 - 2	87	25	4	66
2 - 3	87	53	4	34
3 - 4	177	18	28	46
4 - 5	267	20	9	00
5 - 1	357	17	28	51
AMARRE	ACIMUT		DISTANCIA	
	°	'	m	cm
3 - P.I.	101	22	75	71

Acimutes y distancias calculados con las coordenadas CRTM05 del plano catastrado 4-57389-2023 (redondeo al minuto y al centímetro). Amarre al punto de intersección (P.I.) según el mismo plano.

CUADRO DE COORDENADAS CRTM05

VÉRTICE	ESTE (m)	NORTE (m)
1	489,351.38	1,106,442.25
2	489,356.04	1,106,442.46
3	489,360.38	1,106,442.62
4	489,361.72	1,106,414.19
5	489,352.73	1,106,413.77

CUADRO DE ÁREAS Y COBERTURA

CONCEPTO	VALOR
ÁREA DEL LOTE SEGÚN CATASTRO	256,00 m²
ÁREA DEL LOTE SEGÚN COORDENADAS	256,57 m²
ENVOLVENTE DE CONSTRUCCIÓN (9,00 x 23,12)	208,08 m²
PATIOS ABIERTOS P1 + P2	28,55 m²
HUELLA CONSTRUCTIVA NIVEL 1	179,53 m²
ÁREA LIBRE DEL LOTE (CATASTRO - HUELLA)	76,47 m²
COBERTURA	70,13 %

CÁLCULO: HUELLA / ÁREA SEGÚN CATASTRO x 100 = (179,53 / 256,00) x 100 = 70,13 %

NOTAS:

- TODAS LAS MEDIDAS ESTÁN DADAS EN METROS, SALVO INDICACIÓN CONTRARIA. [PR]
- LA TAPIA COLINDANTE DE MAMPOSTERÍA DEBERÁ PROLONGARSE HASTA EL NIVEL DE LA VIGA CORONA DEL ÚLTIMO NIVEL, GARANTIZANDO EL APANTALLAMIENTO VISUAL PERMANENTE HACIA LA PROPIEDAD COLINDANTE.
- LOS DATOS DEL LOTE (VÉRTICES, DERROTERO Y ÁREA) SE TOMARON DEL PLANO CATASTRADO 4-57389-2023, SISTEMA CRTM05. NO SUSTITUYEN UN LEVANTAMIENTO TOPOGRÁFICO.
- RETIROS DE DISEÑO: FRONTAL 2.00 m MEDIDO DESDE EL VÉRTICE 3; POSTERIOR MÍNIMO 3.00 m; LATERALES 0.00 m. CONFIRMAR CON ALINEAMIENTO Y USO DE SUELO MUNICIPAL.
- LAS FACHADAS LATERALES SE UBICAN SOBRE COLINDANCIA Y SERÁN CIEGAS (SIN VENTANAS NI VANOS).
- LOS BAÑOS CONTARÁN CON EXTRACTOR MECÁNICO DE AIRE.
- LAS CANOAS TENDRÁN MALLA PROTECTORA PARA EVITAR EL ACCESO DE BASURA. [PR]
- EL AGUA POTABLE PROVIENE DEL SISTEMA PÚBLICO (ESPH), DIRECTAMENTE DE LA CONEXIÓN DE LA CALLE.
- LAS AGUAS PLUVIALES SE DIRIGEN HACIA LA CUNETÁ PÚBLICA.
- LAS AGUAS RESIDUALES SE TRATARÁN MEDIANTE TANQUE SÉPTICO Y DRENAJE EN EL PATIO POSTERIOR; DISEÑO Y UBICACIÓN EN LÁMINAS SANITARIAS.
- LA COBERTURA SE CALCULA SOBRE EL ÁREA SEGÚN CATASTRO (256 m²). LOS PATIOS P1 Y P2 SON ABIERTOS DESDE EL NIVEL 1 HASTA EL CIELO Y NO SE CONTABILIZAN EN LA HUELLA.
- PATIOS DE LUZ P1 Y P2 DE 2.50 m DE LADO MÍNIMO, DIMENSIÓN ACEPTADA POR LA MUNICIPALIDAD (ALTURA MEDIDA DESDE EL NIVEL 1).
- [PR] = NOTA TOMADA DEL PROYECTO DE REFERENCIA, PENDIENTE DE REVISIÓN.

SIMBOLOGÍA:

- LÍNEA DE PROPIEDAD (LINDERO)
- 1 VÉRTICE DEL PLANO CATASTRADO
- ▨ HUELLA CONSTRUCTIVA (NIVEL 1)
- ▧ PATIO ABIERTO A CIELO
- ↔ 5.70 COTA (m)

ESPACIO PARA SELLOS Y TIMBRES

CivilCon Diseño y Construcción SRLTDA
Céd. Jurídica: 3-102-762712

PROFESIONAL RESPONSABLE:
DIRECTOR TÉCNICO:
Steven Viales (Civil) IC-40759
David Barrantes (Electricidad) IE-27499

PROYECTO:
VIVIENDA UNIFAMILIAR
DISTRITO 03 SANTIAGO, CANTÓN 05 SAN RAFAEL,
PROVINCIA 04 HEREDIA, COSTA RICA.

INFORMACIÓN REGISTRO PÚBLICO:
FOLIO REAL: 4-041200-000
PLANO CATASTRADO: 4-57389-2023
ÁREA SEGÚN CATASTRO: 256 m²

CONTENIDO:
LOTE DE TERRENO
UBICACIÓN GEOGRÁFICA.
POLIGONAL.
RETIROS Y HUELLA.
DERROTERO Y CUADRO DE COORDENADAS.
CUADRO DE ÁREAS Y COBERTURA.
NOTAS.

ESCALAS: INDICADAS

CONTROL DE REVISIONES		
REV.	FECHA	DESCRIPCIÓN
0	06-10-2026	VERSIÓN DE TRABAJO PARA REVISIÓN
1	06-10-2026	NOTA 2 TAPIA; PATIOS ACEPTADOS (NOTA 12)

ESTADO:
VERSIÓN DE TRABAJO
NO APTA PARA CONSTRUCCIÓN NI TRÁMITE

LUGAR	LÁMINA
COSTA RICA	A1
OCT 2026	TOTAL --