



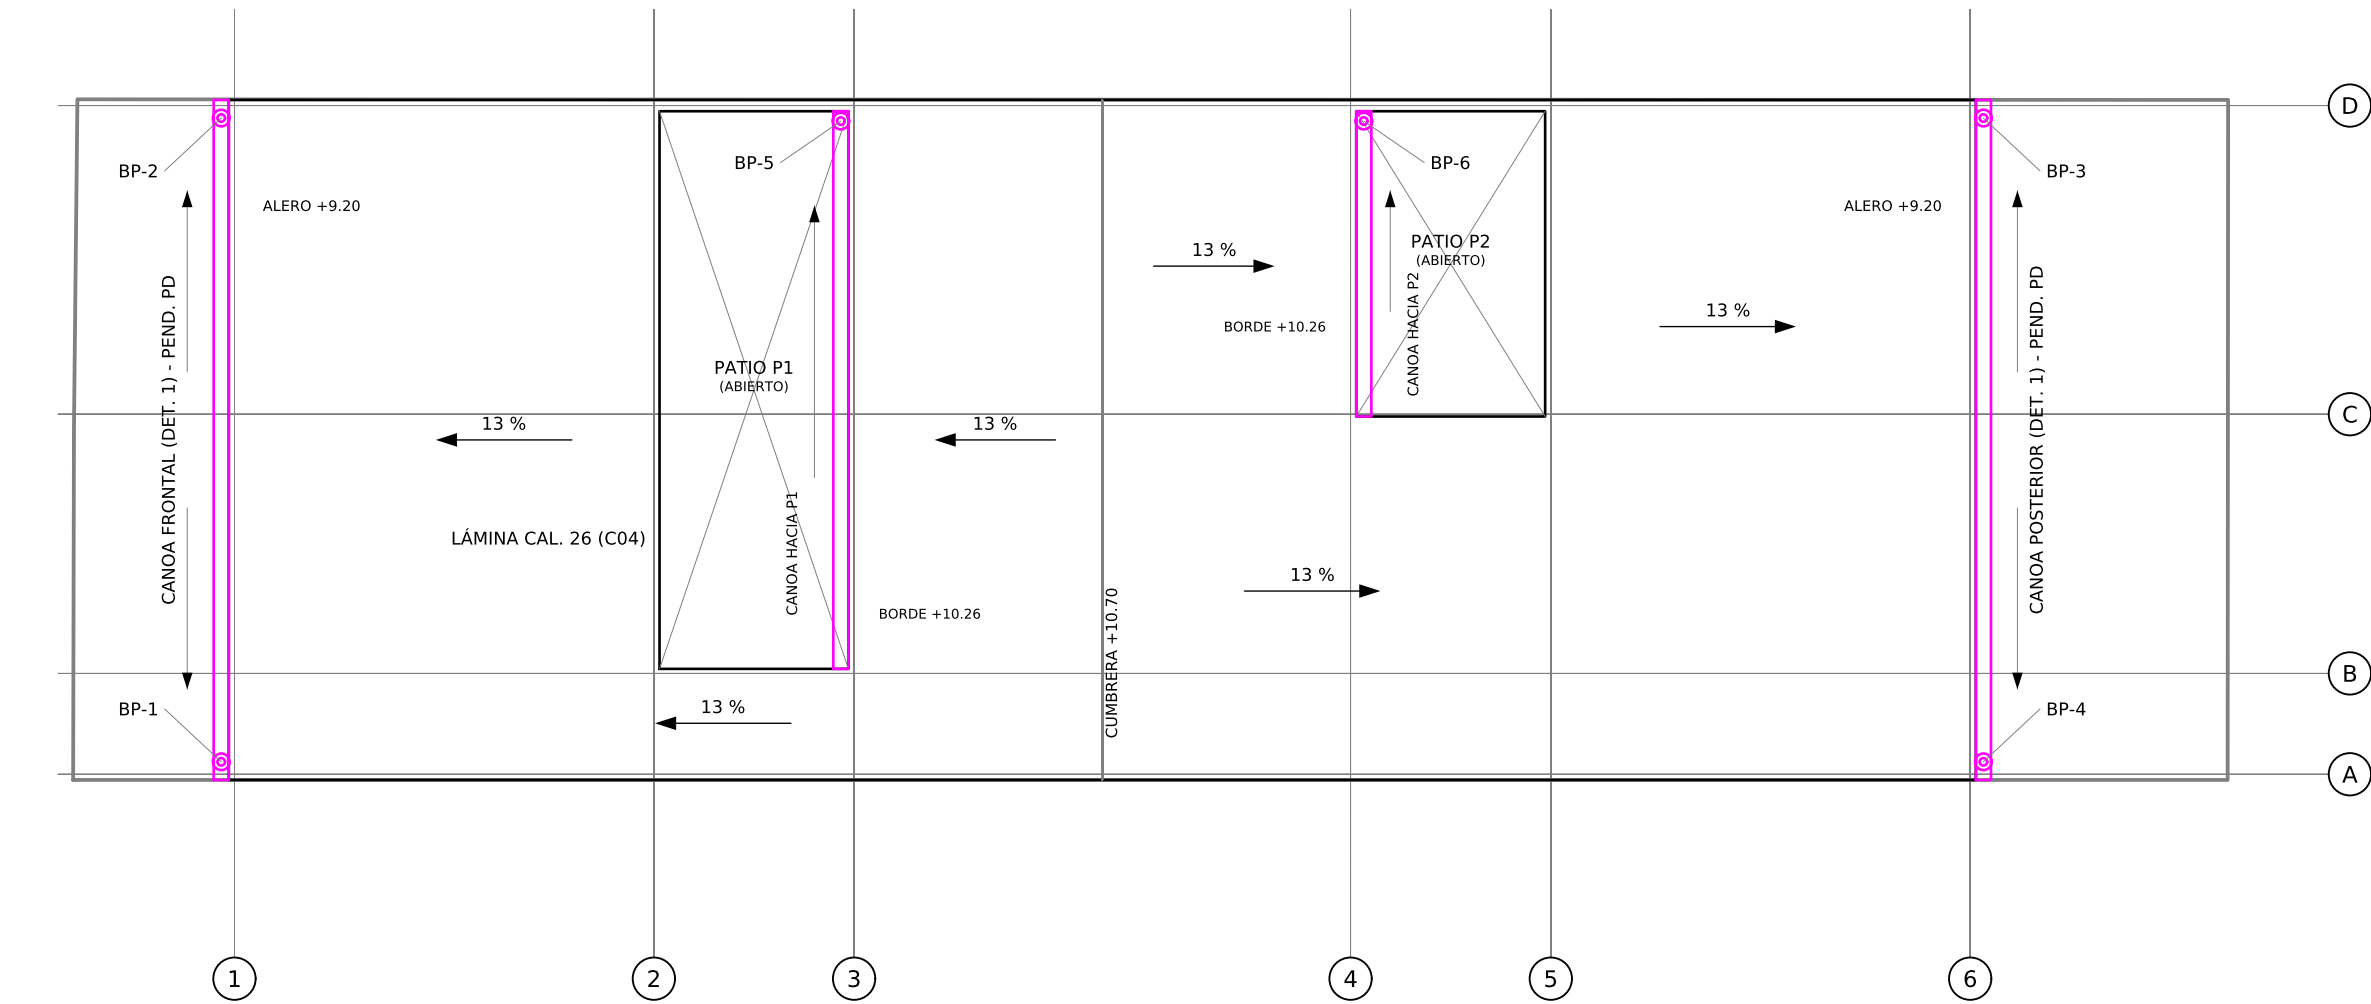


AGUAS PLUVIALES - PLANTA DE TECHO
Esc. 1:100

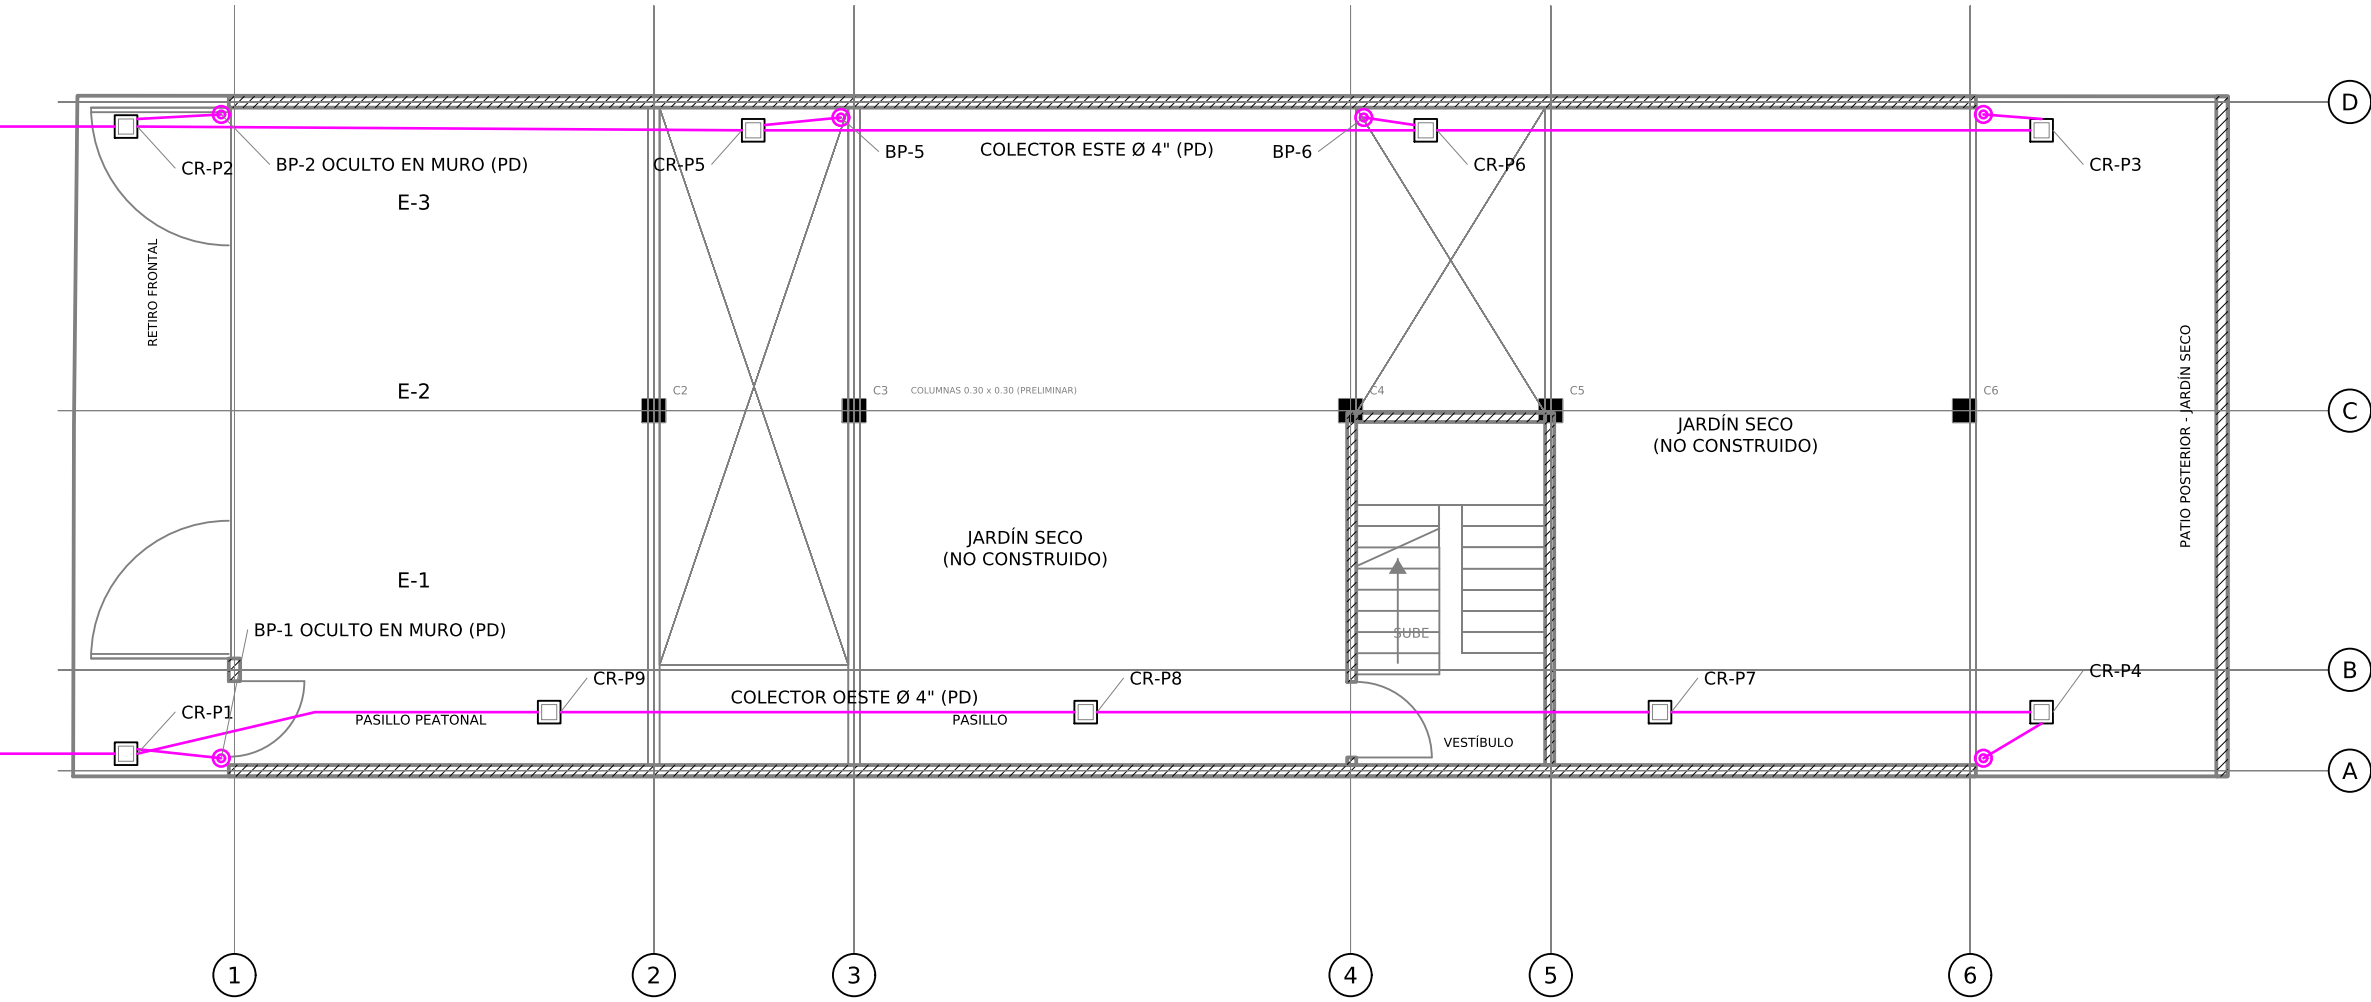

AGUAS PLUVIALES - NIVEL 1
Esc. 1:100

DETALLE 1 - CANOA (SECCIÓN TÍPICA)
Esc. 1:10 - FRONTAL, POSTERIOR Y HACIA PATIOS

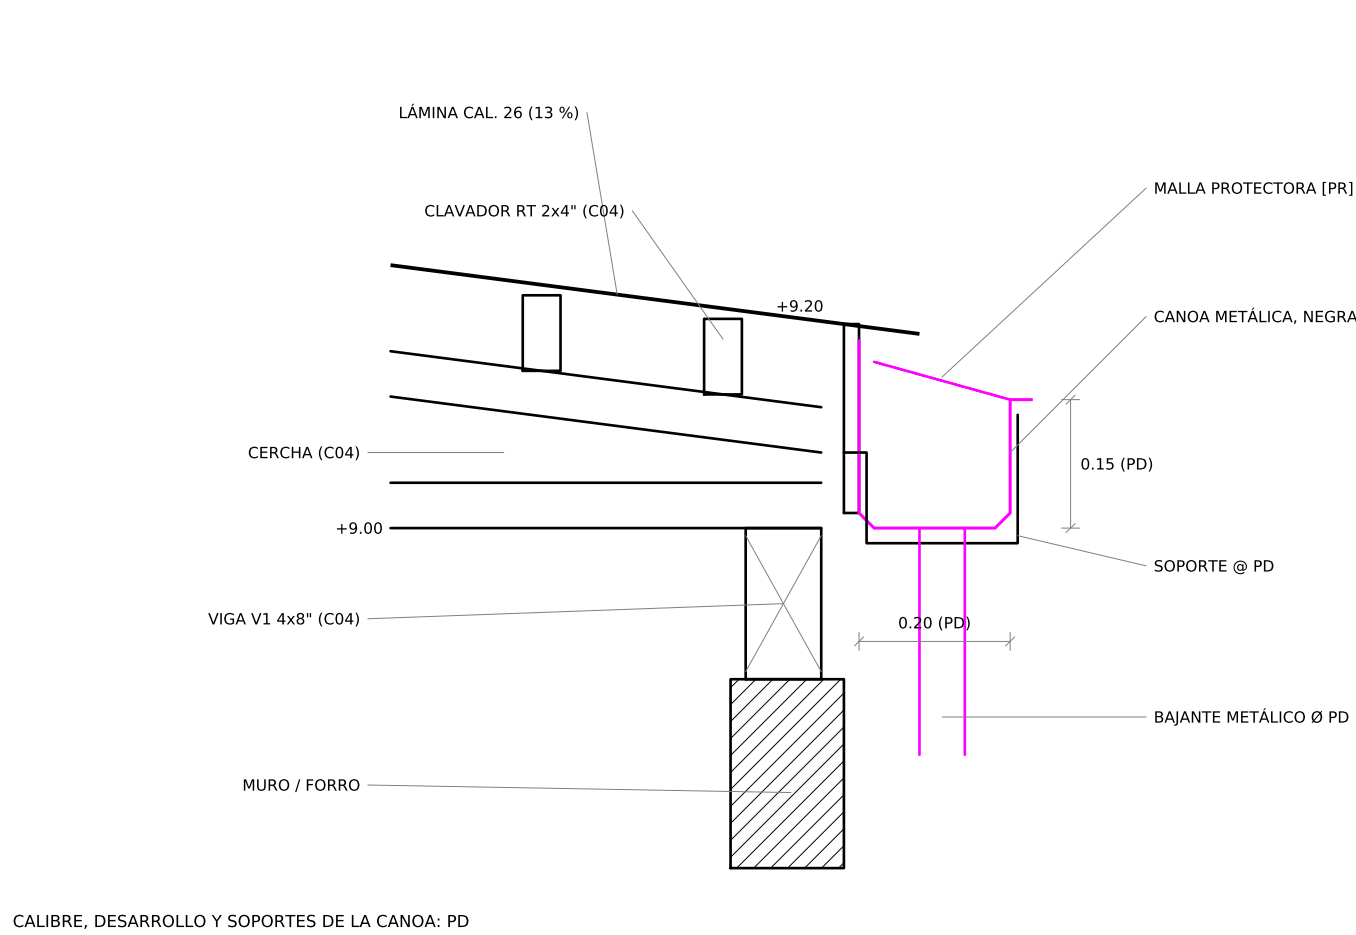

CALIBRE, DESARROLLO Y SOPORTES DE LA CANOA: PD

ÁREAS TRIBUTARIAS DE CUBIERTA (PROYECCIÓN HORIZONTAL)

CANOA	ÁREA (m²)	BAJANTES	m² POR BAJANTE
FRONTAL	60.79	BP-1, BP-2	30.40
HACIA P1	24.80	BP-5	24.80
HACIA P2	13.57	BP-6	13.57
POSTERIOR	80.37	BP-3, BP-4	40.18
TOTAL CUBIERTA	179.53	6	


ÁREAS CALCULADAS CON LA GEOMETRÍA DE LA C04 (CUMBRERA EN y = 13.62). LOS PATIOS P1 (18.45 m²) Y P2 (10.10 m²) SON ABIERTOS: LA LLUVIA DIRECTA CAE SOBRE LA GRAVA DEL NIVEL 1.

NOTAS:

- 1.- TODAS LAS MEDIDAS ESTÁN DADAS EN METROS, SALVO INDICACIÓN CONTRARIA. [PR]
 - 2.- LAS AGUAS PLUVIALES SE DIRIGEN HACIA LA CUNETA PÚBLICA DEL FRENTE. [PR] NO SE CONECTAN AL TANQUE SÉPTICO NI AL DRENAJE (S02).
 - 3.- CUBIERTA SEGÚN LA C04: LÁMINA CAL. 26 A DOS AGUAS, PENDIENTE 13 %, ALERO +9.20 Y CUMBRERA +10.70.
 - 4.- CANOAS FRONTAL Y POSTERIOR CON DOS BAJANTES CADA UNA, UNO EN CADA EXTREMO; CANOAS HACIA LOS PATIOS P1 Y P2 CON UN BAJANTE CADA UNA, EN EL EXTREMO ESTE.
 - 5.- CANOAS Y BAJANTES VISIBLES METÁLICOS, ACABADO NEGRO (A5). BAJANTES FRONTALES BP-1 Y BP-2 OCULTOS EN EL MURO FRONTAL DEL NIVEL 1 (PD).
 - 6.- LAS CANOAS TENDRÁN MALLA PROTECTORA PARA EVITAR EL ACCESO DE BASURA. [PR]
 - 7.- DIRIGIR LAS PENDIENTES HACIA BAJANTES O CANOAS; EVITAR DEPRESIONES QUE PROVOQUEN EMPOZAMIENTOS. [PR]
 - 8.- DIÁMETROS DE BAJANTES Y COLECTORES, PENDIENTES DE CANOAS Y COLECTORES, CALIBRE Y DESARROLLO DE LAS CANOAS: PD, SEGÚN CÁLCULO HIDRAULICO.
 - 9.- COLECTORES ENTERRADOS DE PVC CON CAJAS PLUVIALES DE 0.30 x 0.30 (DETALLE 2) AL PIE DE CADA BAJANTE Y EN LOS CAMBIOS DE DIRECCIÓN. [PR]
 - 10.- COLECTOR OESTE POR EL PASILLO PEATONAL, ENTRE LOS ALIMENTADORES ELÉCTRICOS (E01) Y LA TUBERÍA DE AGUA POTABLE (S01); CRUZA BAJO LOS DUCTOS ELÉCTRICOS FRENTE A CR-P9 (PD).
 - 11.- COLECTOR ESTE JUNTO AL MURO D; CRUZA LOS RAMALES SANITARIOS DE LA SUITE 2 (S02) ENTRE CR-P6 Y CR-P5 (PROFUNDIDADES RELATIVAS PD).
 - 12.- LAS TUBERÍAS PASAN SOBRE LAS PLACAS DE CIMENTACIÓN SIN ATRAVESAR PEDESTALES; CRUCES CON VIGAS RIOSTRA CON CAMISA (PD). LAS CAJAS SE UBICAN FUERA DE LAS PLACAS (C01).
 - 13.- DESCARGA A LA CUNETA (DETALLE 3): UBICACIÓN, FORMA DE CONEXIÓN Y PERMISO SEGÚN LA MUNICIPALIDAD (PD).
 - 14.- LIMPIAR CANOAS, MALLAS Y CAJAS PLUVIALES PERIÓDICAMENTE.
- [PR] = NOTA TOMADA DEL PROYECTO DE REFERENCIA, PENDIENTE DE REVISIÓN.


DETALLE 2 - CAJA PLUVIAL [PR]

S/E - INTERIOR 0.30 x 0.30 [PR]

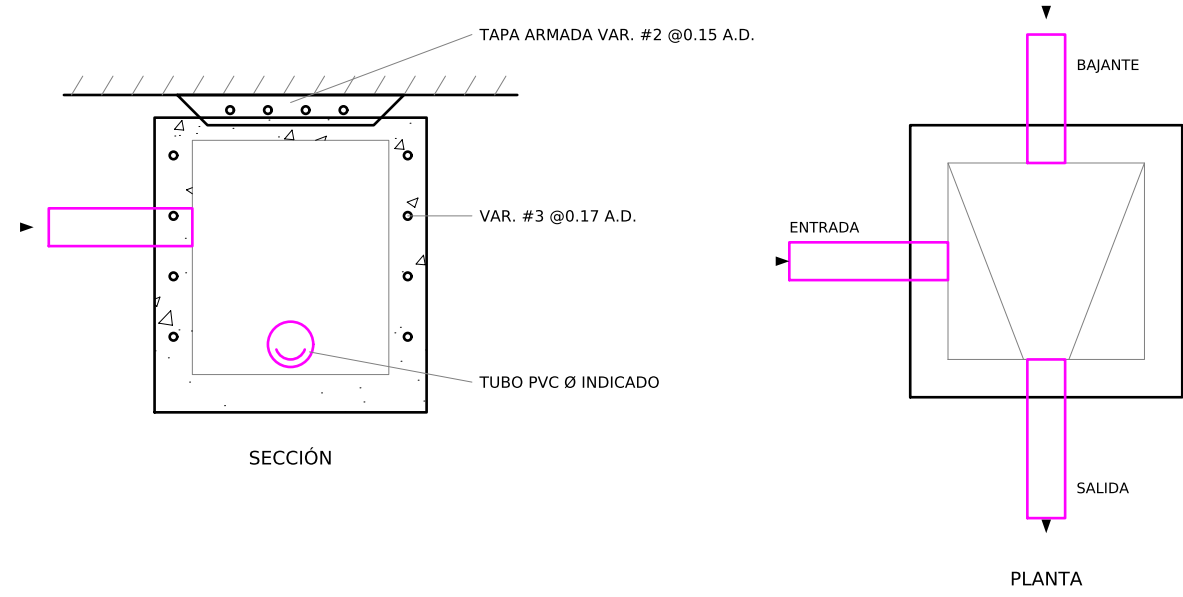

DETALLE 3 - DESCARGA A CUNETA (ESQUEMÁTICO)

S/E

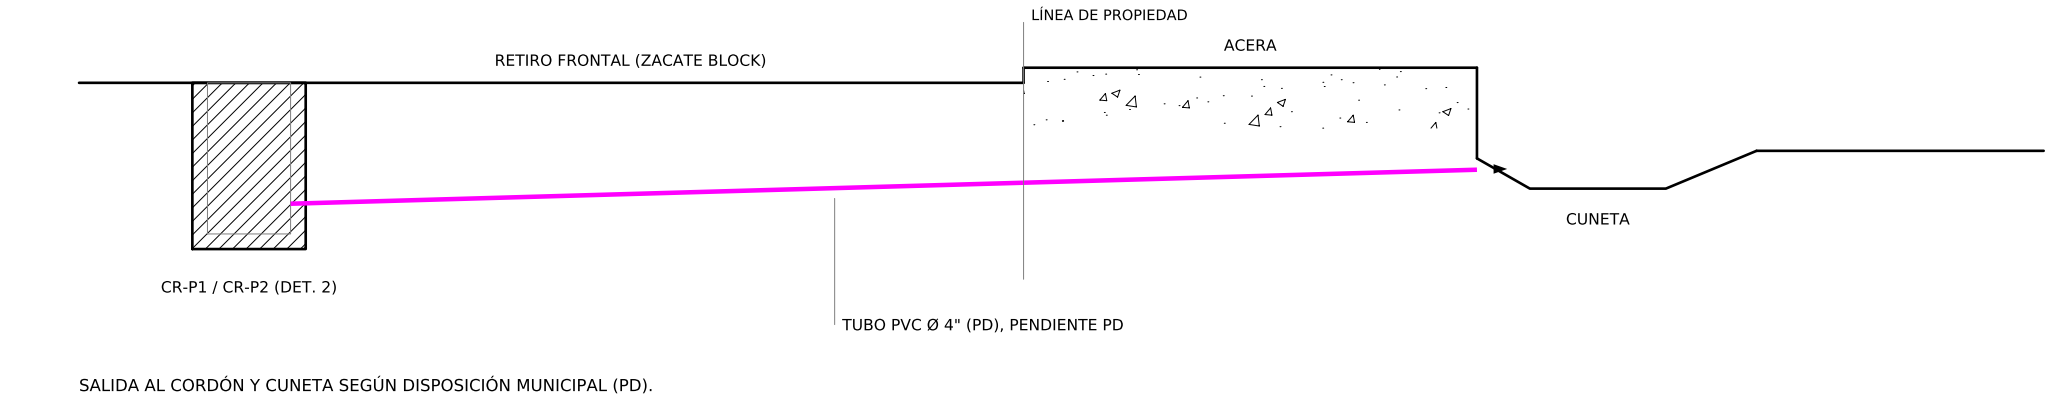

SIMBOLOGÍA

	CANOA METÁLICA (DET. 1)
	BAJANTE PLUVIAL (BP-n)
	COLECTOR PLUVIAL ENTERRADO (PVC)
	CAJA PLUVIAL 0.30 x 0.30 (DET. 2) [PR]
	PENDIENTE DE CUBIERTA / CANOA

ESPACIO PARA SELLOS Y TIMBRES

CivilCon Diseño y Construcción SRLTDA
Céd. Jurídica: 3-102-762712

PROFESIONAL RESPONSABLE:
DIRECTOR TÉCNICO:
Steven Viales (Civil) IC-40759
David Barrantes (Electricidad) IE-27499

PROYECTO:
VIVIENDA UNIFAMILIAR
DISTRITO 03 SANTIAGO, CANTÓN 05 SAN RAFAEL,
PROVINCIA 04 HEREDIA, COSTA RICA.

INFORMACIÓN REGISTRO PÚBLICO:
FOLIO REAL: 4-041200-000
PLANO CATASTRADO: 4-57389-2023
ÁREA SEGÚN CATASTRO: 256 m²

CONTENIDO:
AGUAS PLUVIALES
PLANTA DE TECHO.
PLANTA DEL NIVEL 1.
DETALLE DE CANOA.
CAJA PLUVIAL Y DESCARGA
A CUNETA. ÁREAS TRIBUTARIAS.
SIMBOLOGÍA Y NOTAS.

ESCALAS: 1:100 / INDICADAS

CONTROL DE REVISIONES		
REV.	FECHA	DESCRIPCIÓN
0	07-10-2026	VERSIÓN DE TRABAJO PARA REVISIÓN

ESTADO:
VERSIÓN DE TRABAJO
NO APTA PARA CONSTRUCCIÓN NI TRÁMITE

LUGAR	LÁMINA
COSTA RICA	S03
OCT 2026	TOTAL --