




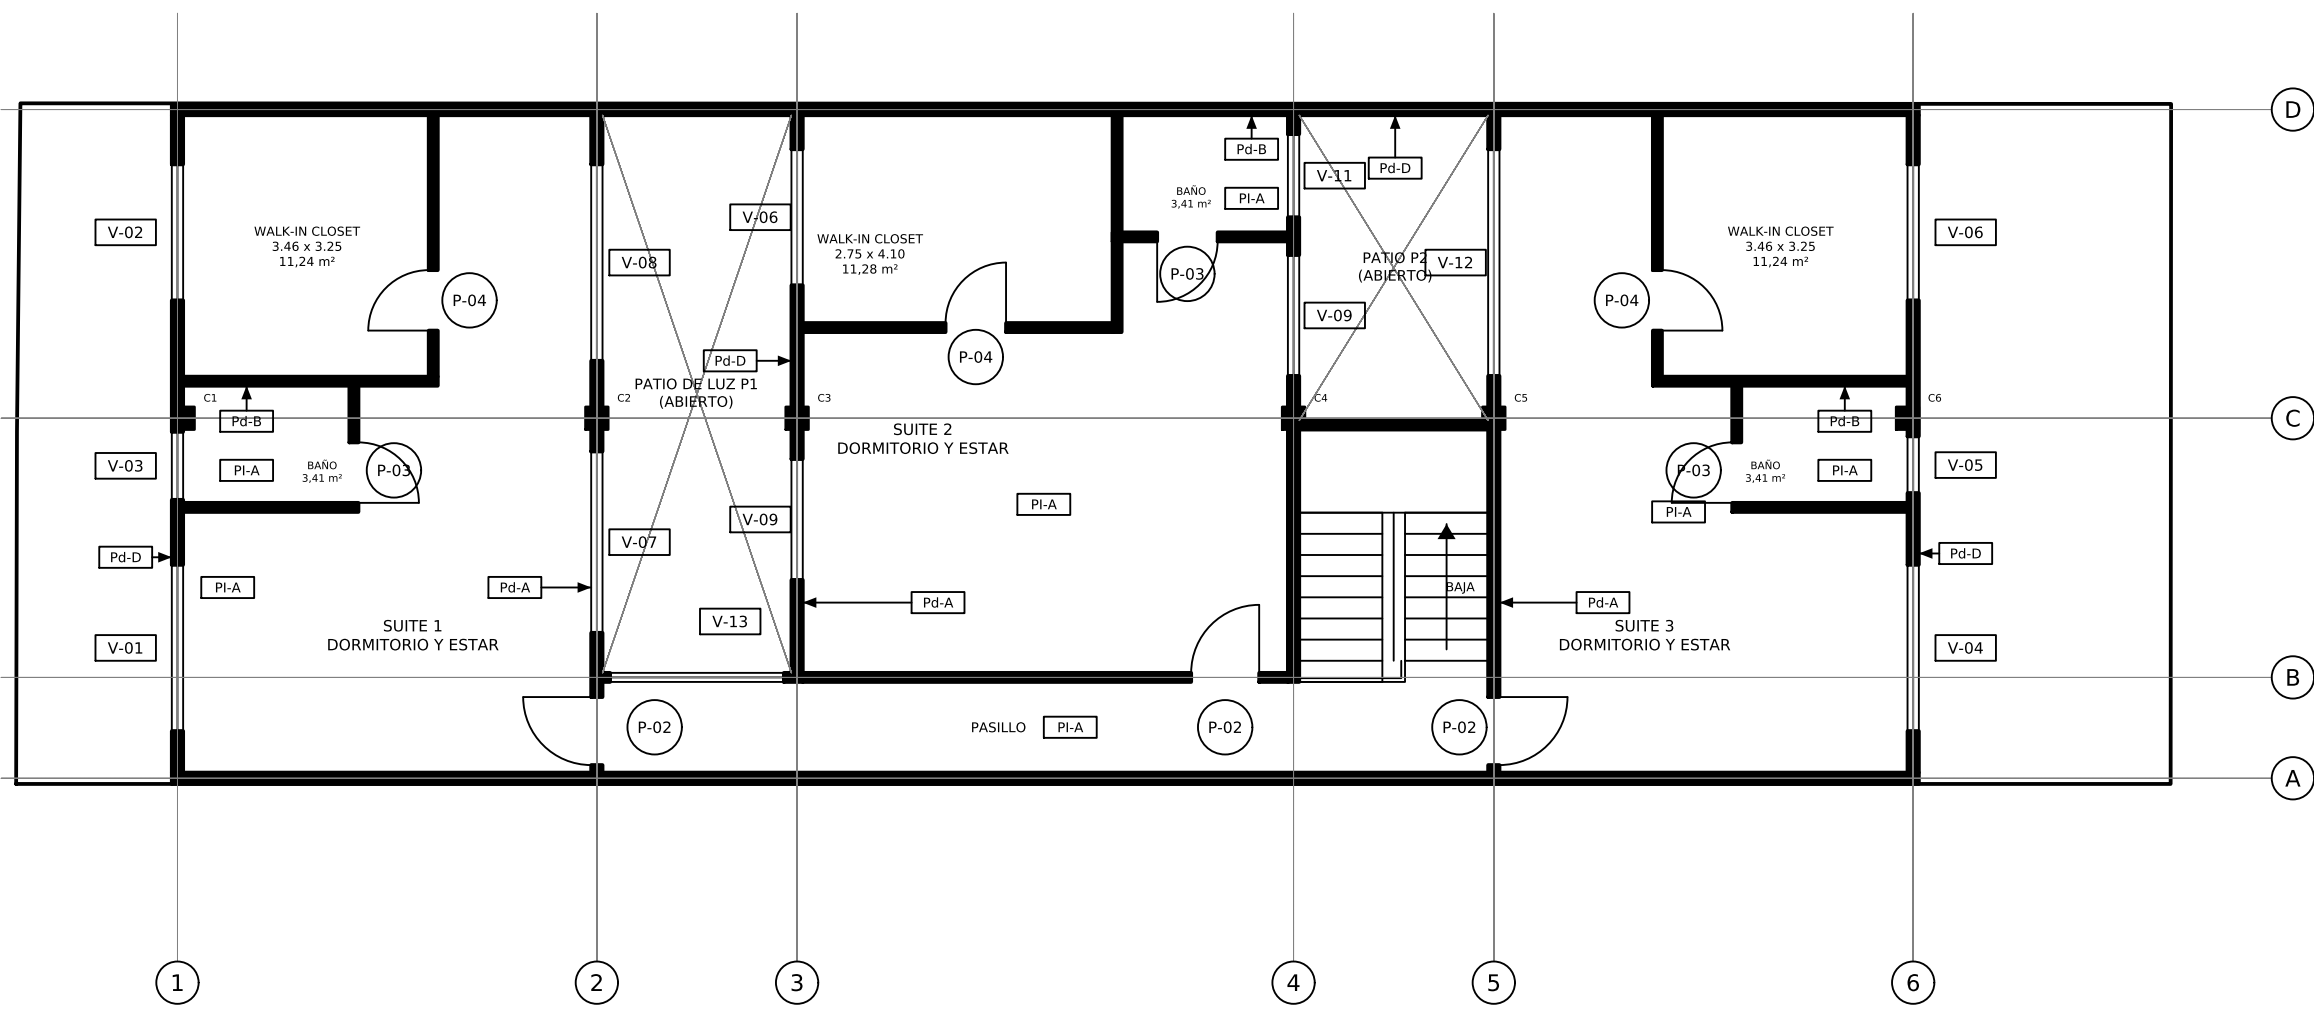

PLANTA NIVEL 3  
PUERTAS, VENTANAS Y ACABADOS - Esc. 1:100

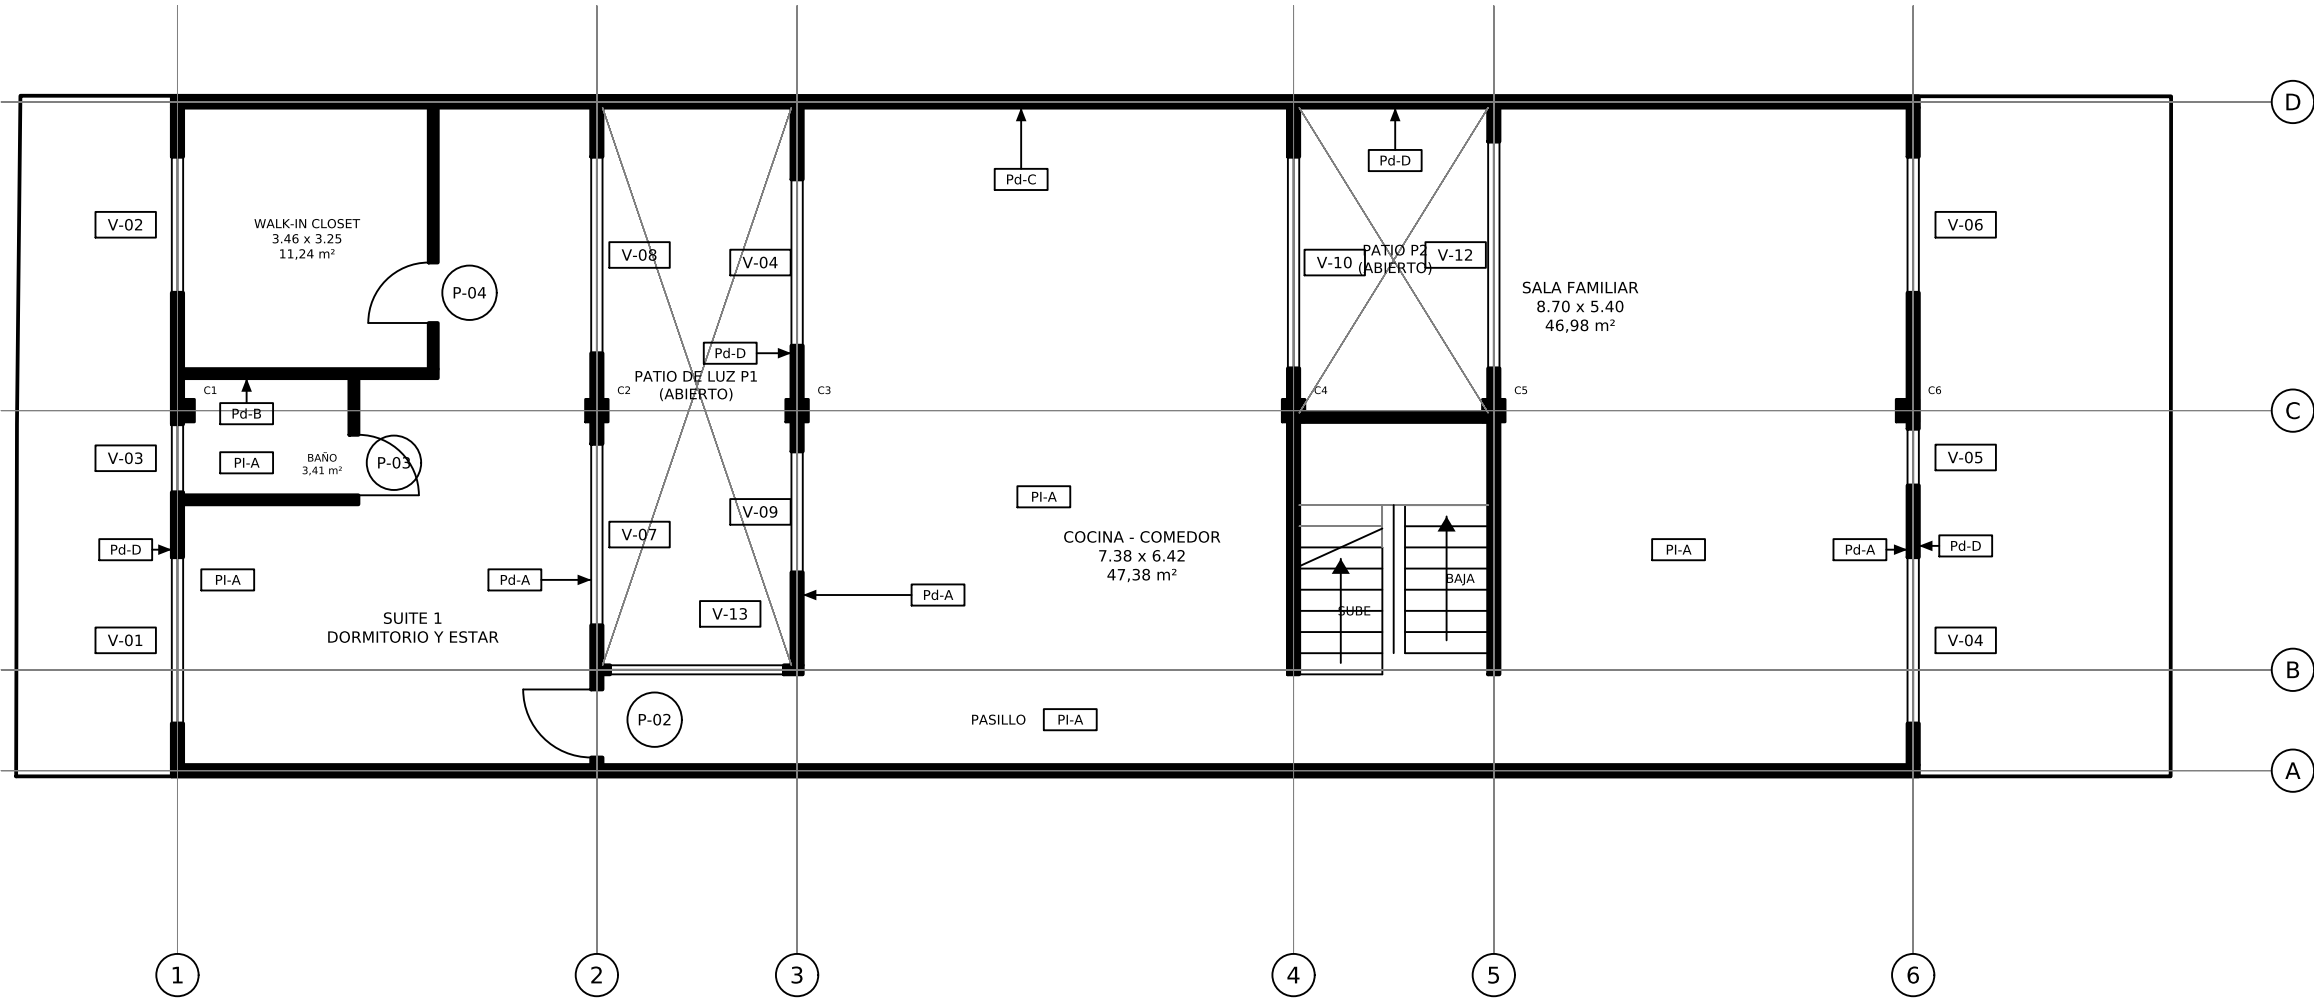


PLANTA NIVEL 2  
PUERTAS, VENTANAS Y ACABADOS - Esc. 1:100

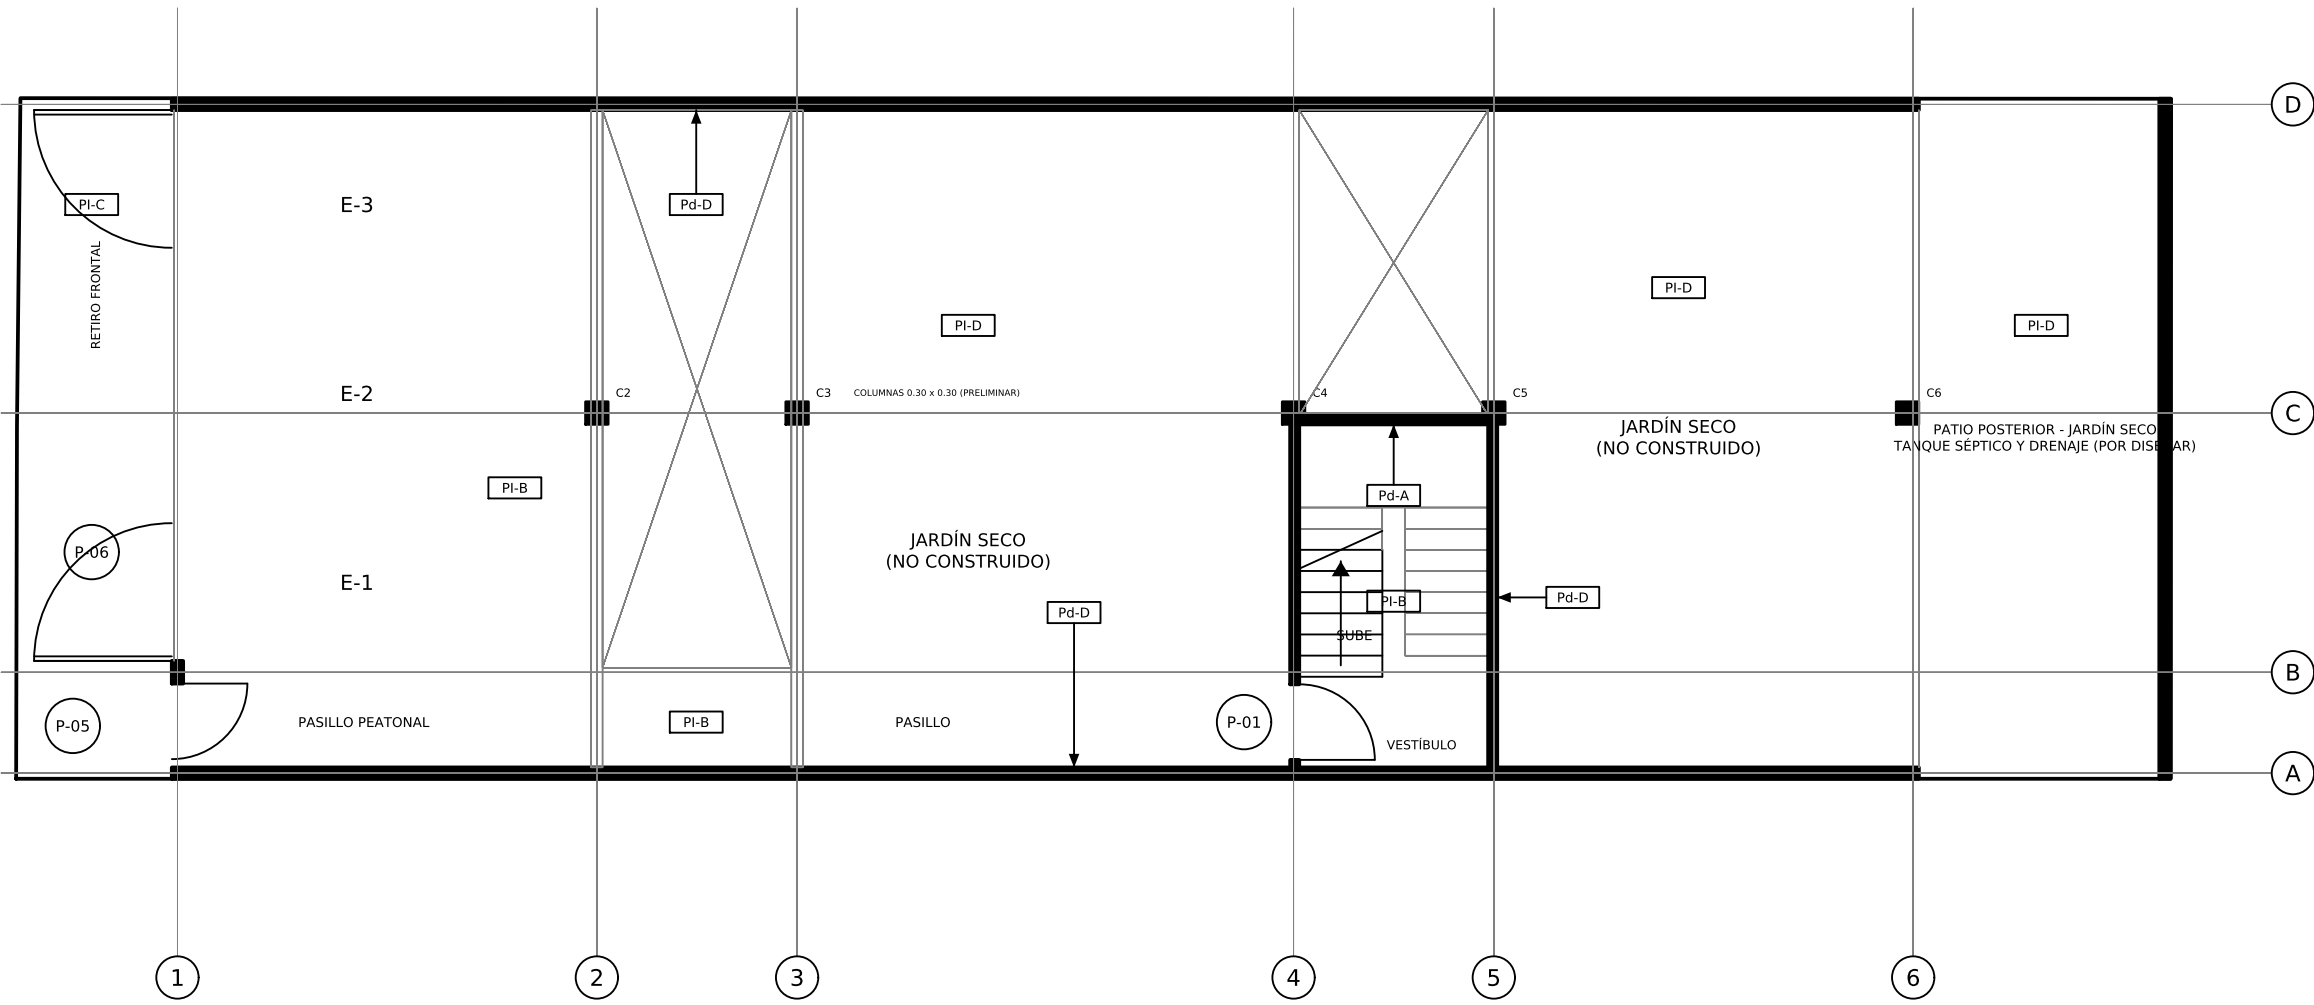

PLANTA NIVEL 1  
PUERTAS, VENTANAS Y ACABADOS - Esc. 1:100

DETALLE VENTANAS  
Esc. 1:75 - VISTA EXTERIOR

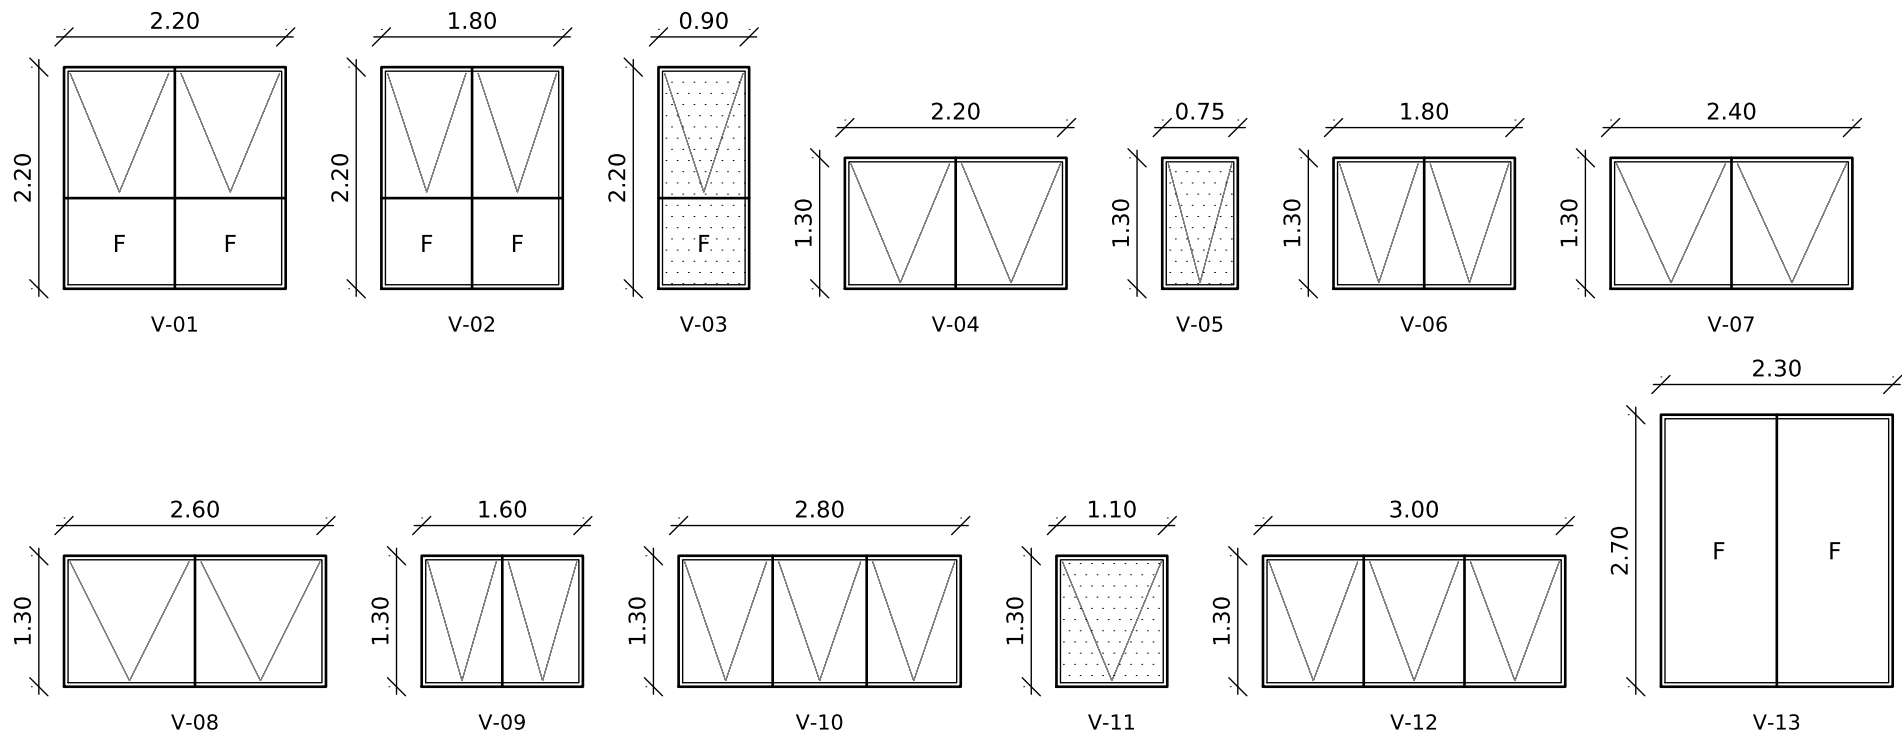


| CUADRO DE PUERTAS<br>(UNIDADES EN METROS) |       |      |                  |      |                                   |                               |
|-------------------------------------------|-------|------|------------------|------|-----------------------------------|-------------------------------|
| PUERTA                                    | ANCHO | ALTO | TIPO             | CANT | UBICACIÓN                         | MATERIAL                      |
| P-01                                      | 1,00  | 2,10 | BATIENTE         | 1    | ACCESO PPAL. (VESTIBULO NIVEL 1)  | MADERA                        |
| P-02                                      | 0,90  | 2,10 | BATIENTE         | 4    | HABITACIONES (SUITES 1, 2 Y 3)    | MADERA                        |
| P-03                                      | 0,80  | 2,10 | BATIENTE         | 4    | BAÑOS                             | MADERA CON ROMANILLA INFERIOR |
| P-04                                      | 0,80  | 2,10 | BATIENTE         | 4    | WALK-IN CLOSET                    | MADERA                        |
| P-05                                      | 1,00  | 2,40 | BATIENTE         | 1    | PUERTA PEATONAL (FRENTE NIVEL 1)  | METAL (ACERO)                 |
| P-06                                      | 7,29  | 2,40 | ABATIBLE 4 HOJAS | 1    | PORTÓN VEHICULAR (FRENTE NIVEL 1) | METAL (ACERO)                 |

| CUADRO DE VENTANAS<br>(UNIDADES EN METROS) |       |      |                              |      |                                                              |                   |
|--------------------------------------------|-------|------|------------------------------|------|--------------------------------------------------------------|-------------------|
| VENTANA                                    | ANCHO | ALTO | TIPO                         | CANT | UBICACIÓN                                                    | MATERIAL          |
| V-01                                       | 2,20  | 2,20 | FIJA INF. + VENTILA ABATIBLE | 2    | DORMITORIO SUITE 1, FACHADA PRINCIPAL (N2 Y N3)              | ALUMINIO Y VIDRIO |
| V-02                                       | 1,80  | 2,20 | FIJA INF. + VENTILA ABATIBLE | 2    | WALK-IN SUITE 1, FACHADA PRINCIPAL (N2 Y N3)                 | ALUMINIO Y VIDRIO |
| V-03                                       | 0,90  | 2,20 | FIJA INF. + VENTILA ABATIBLE | 2    | BAÑO SUITE 1, FACHADA PRINCIPAL (VIDRIO ARENADO)             | ALUMINIO Y VIDRIO |
| V-04                                       | 2,20  | 1,30 | VENTILA ABATIBLE             | 3    | SALA Y SUITE 3, FACHADA POSTERIOR; COCINA A P1 (N2)          | ALUMINIO Y VIDRIO |
| V-05                                       | 0,75  | 1,30 | VENTILA ABATIBLE             | 2    | FACHADA POSTERIOR: SALA (N2) Y BAÑO SUITE 3 (VIDRIO ARENADO) | ALUMINIO Y VIDRIO |
| V-06                                       | 1,80  | 1,30 | VENTILA ABATIBLE             | 3    | FACHADA POSTERIOR (N2 Y N3); WALK-IN SUITE 2 A P1            | ALUMINIO Y VIDRIO |
| V-07                                       | 2,40  | 1,30 | VENTILA ABATIBLE             | 2    | SUITE 1 HACIA PATIO P1 (N2 Y N3)                             | ALUMINIO Y VIDRIO |
| V-08                                       | 2,60  | 1,30 | VENTILA ABATIBLE             | 2    | WALK-IN SUITE 1 HACIA PATIO P1 (N2 Y N3)                     | ALUMINIO Y VIDRIO |
| V-09                                       | 1,60  | 1,30 | VENTILA ABATIBLE             | 3    | COCINA (N2) Y SUITE 2 (N3) A P1; SUITE 2 A P2                | ALUMINIO Y VIDRIO |
| V-10                                       | 2,80  | 1,30 | VENTILA ABATIBLE             | 1    | COCINA HACIA PATIO P2 (N2)                                   | ALUMINIO Y VIDRIO |
| V-11                                       | 1,10  | 1,30 | VENTILA ABATIBLE             | 1    | BAÑO SUITE 2 HACIA PATIO P2 (N3, VIDRIO ARENADO)             | ALUMINIO Y VIDRIO |
| V-12                                       | 3,00  | 1,30 | VENTILA ABATIBLE             | 2    | SALA (N2) Y SUITE 3 (N3) HACIA PATIO P2                      | ALUMINIO Y VIDRIO |
| V-13                                       | 2,30  | 2,70 | FIJA                         | 2    | GALERÍA DEL PASILLO HACIA PATIO P1 (N2 Y N3)                 | ALUMINIO Y VIDRIO |

| ACABADO EN PAREDES |   |                                  |
|--------------------|---|----------------------------------|
| ITEM               | TIPO DE ACABADO                                                                                     | COLOR                            |
| Pd - A             | PAREDES INTERNAS: REPELLO GRUESO, ACABADO LISO, CON DOS MANOS DE PINTURA CLASE A, CON BASE SATINADO | REFERENCIA: PANTONE, ALMOND MILK |
| Pd - B             | BAÑOS: REPELLO GRUESO, ACABADO CON CERÁMICA O PORCELANATO. 1,80 m EN DUCHAS.                        | BLANCO                           |
| Pd - C             | COCINA: REPELLO GRUESO, ACABADO CON CERÁMICA O PORCELANATO EN SALPICADERO.                          | BLANCO                           |
| Pd - D             | PAREDES EXTERNAS: REPELLO GRUESO, ACABADO ESTUCO PULIDO.                                            | GRIS CONCRETO                    |

| ACABADO EN PISOS |   |               |
|------------------|---|---------------|
| ITEM             | TIPO DE ACABADO                                                                                    | COLOR         |
| PI - A           | PISO PARA INTERIORES Y BAÑOS, PORCELANATO 60x60CM BLANCO O COLOR CLARO CON RODAPIE DE PORCELANATO. | BLANCO        |
| PI - B           | CONTRAPISO DE CONCRETO DE 0,10 m (ESTACIONAMIENTOS, PASILLO, VESTIBULO Y GRADAS DEL NIVEL 1).      | GRIS CONCRETO |
| PI - C           | ZACATE BLOCK (PERMEABLE) EN RETIRO FRONTAL.                                                        | NATURAL       |
| PI - D           | GRAVA (JARDIN SECO).                                                                               | NATURAL       |

| ACABADO EN CIELOS                                                           |                   |
|-----------------------------------------------------------------------------|-------------------|
| ITEM                                                                        | TIPO DE ACABADO   |
| CIELO RASO TIPO GYPSUM (REGULAR PLANO, SUSPENDIDO A 2,70 m), NIVELES 2 Y 3. | COLOR BLANCO      |
| NIVEL 1: ESTRUCTURA DE ACERO EXPUESTA (SIN CIELO RASO).                     | SEGÚN ESTRUCTURAL |

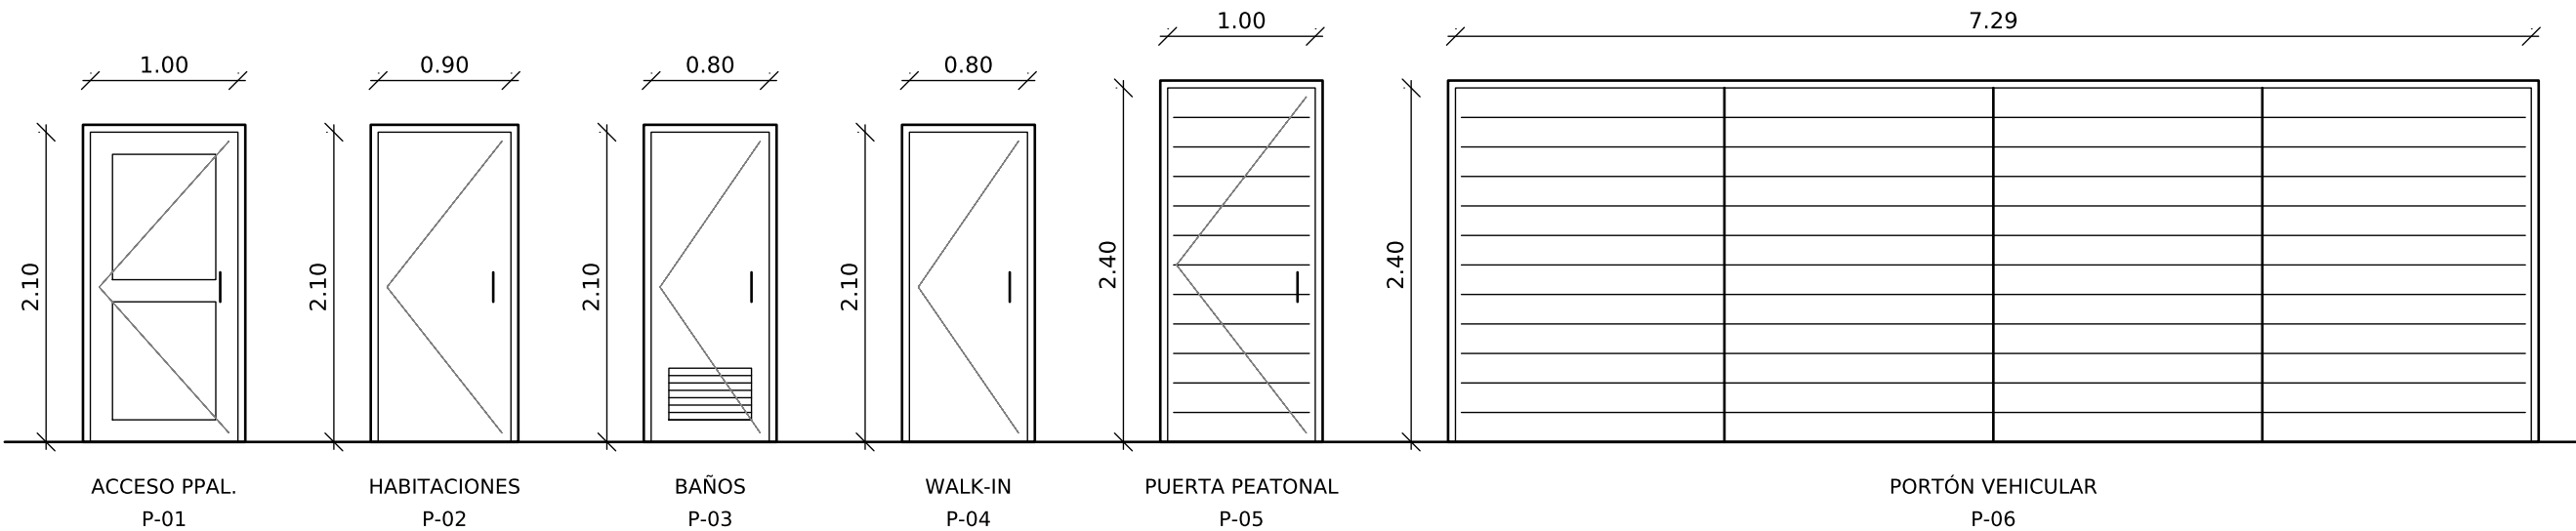

DETALLE PUERTAS  
Esc. 1:50 - VISTA DESDE EL LADO DE APERTURA

- NOTAS:
- TODAS LAS MEDIDAS ESTÁN DADAS EN METROS. [PR]
  - EL NIVEL ±0.00 ES EL NIVEL DE ACERA (NPT DEL NIVEL 1); N2 +3.00 Y N3 +6.00.
  - LAS MEDIDAS DEBEN SER VERIFICADAS EN SITIO. [PR]
  - LOS MARCOS DE LAS VENTANAS SERÁN DE ALUMINIO COLOR NEGRO. [PR]
  - VENTANAS: VENTILA ABATIBLE HACIA AFUERA (BISAGRA SUPERIOR, TRIANGULO INVERTIDO); F = PAÑO FIJO. FACHADA PRINCIPAL DE 0.00 A 2.20 m CON PAÑO FIJO INFERIOR DE SEGURIDAD HASTA 0.90 m; LAS DEMÁS CON ANTEPECHO DE 0.90 m Y DINTEL A 2.20 m. VIDRIO ARENADO EN BAÑOS.
  - PUERTAS DE 2.10 m DE ALTO. P-05 Y P-06 (2.40 m) METÁLICAS SEGÚN FACHADA AS.
  - PLANTAS SIN MOBILIARIO NI COTAS; DISTRIBUCIÓN Y MEDIDAS SEGÚN LÁMINAS A2, A3 Y A4.
- [PR] = NOTA TOMADA DEL PROYECTO DE REFERENCIA, PENDIENTE DE REVISIÓN.

ESPACIO PARA SELLOS Y TIMBRES

|   |                                             |
|---|---------------------------------------------|
| CivilCon Diseño y Construcción SRLTDA<br>Céd. Jurídica: 3-102-762712   |                                             |
| PROFESIONAL RESPONSABLE:<br>DIRECTOR TÉCNICO:<br>Steven Viales (Civil) IC-40759<br>David Barrantes (Electricidad) IE-27499                                                          |                                             |
| PROYECTO:<br>VIVIENDA UNIFAMILIAR<br>DISTRITO 03 SANTIAGO, CANTÓN 05 SAN RAFAEL,<br>PROVINCIA 04 HEREDIA, COSTA RICA.                                                               |                                             |
| INFORMACION REGISTRO PÚBLICO:<br>FOLIO REAL: 4-041200-000<br>PLANO CATASTRADO: 4-57389-2023<br>ÁREA SEGÚN CATASTRO: 256 m²                                                          |                                             |
| CONTENIDO:<br>PUERTAS Y VENTANAS<br>PLANTAS NIVELES 1, 2 Y 3.<br>CUADROS DE PUERTAS Y VENTANAS.<br>ACABADOS EN PAREDES, PISOS Y CIELOS.<br>DETALLE DE PUERTAS Y VENTANAS.<br>NOTAS. |                                             |
| ESCALAS: 1:100 / INDICADAS   |                                             |
| CONTROL DE REVISIONES   |                                             |
| REV.   | FECHA DESCRIPCIÓN                           |
| 0   | 06-10-2026 VERSIÓN DE TRABAJO PARA REVISION |
| 1   | 06-10-2026 V-05 CON VIDRIO ARENADO          |
| 2   | 06-10-2026 V-03 DE 0,90 (COLUMNA EJE C-1)   |
| ESTADO: VERSIÓN DE TRABAJO<br>NO APTA PARA CONSTRUCCIÓN NI TRÁMITE   |                                             |
| LUGAR   | LÁMINA                                      |
| COSTA RICA   | A7                                          |
| OCT 2026   | TOTAL --                                    |