


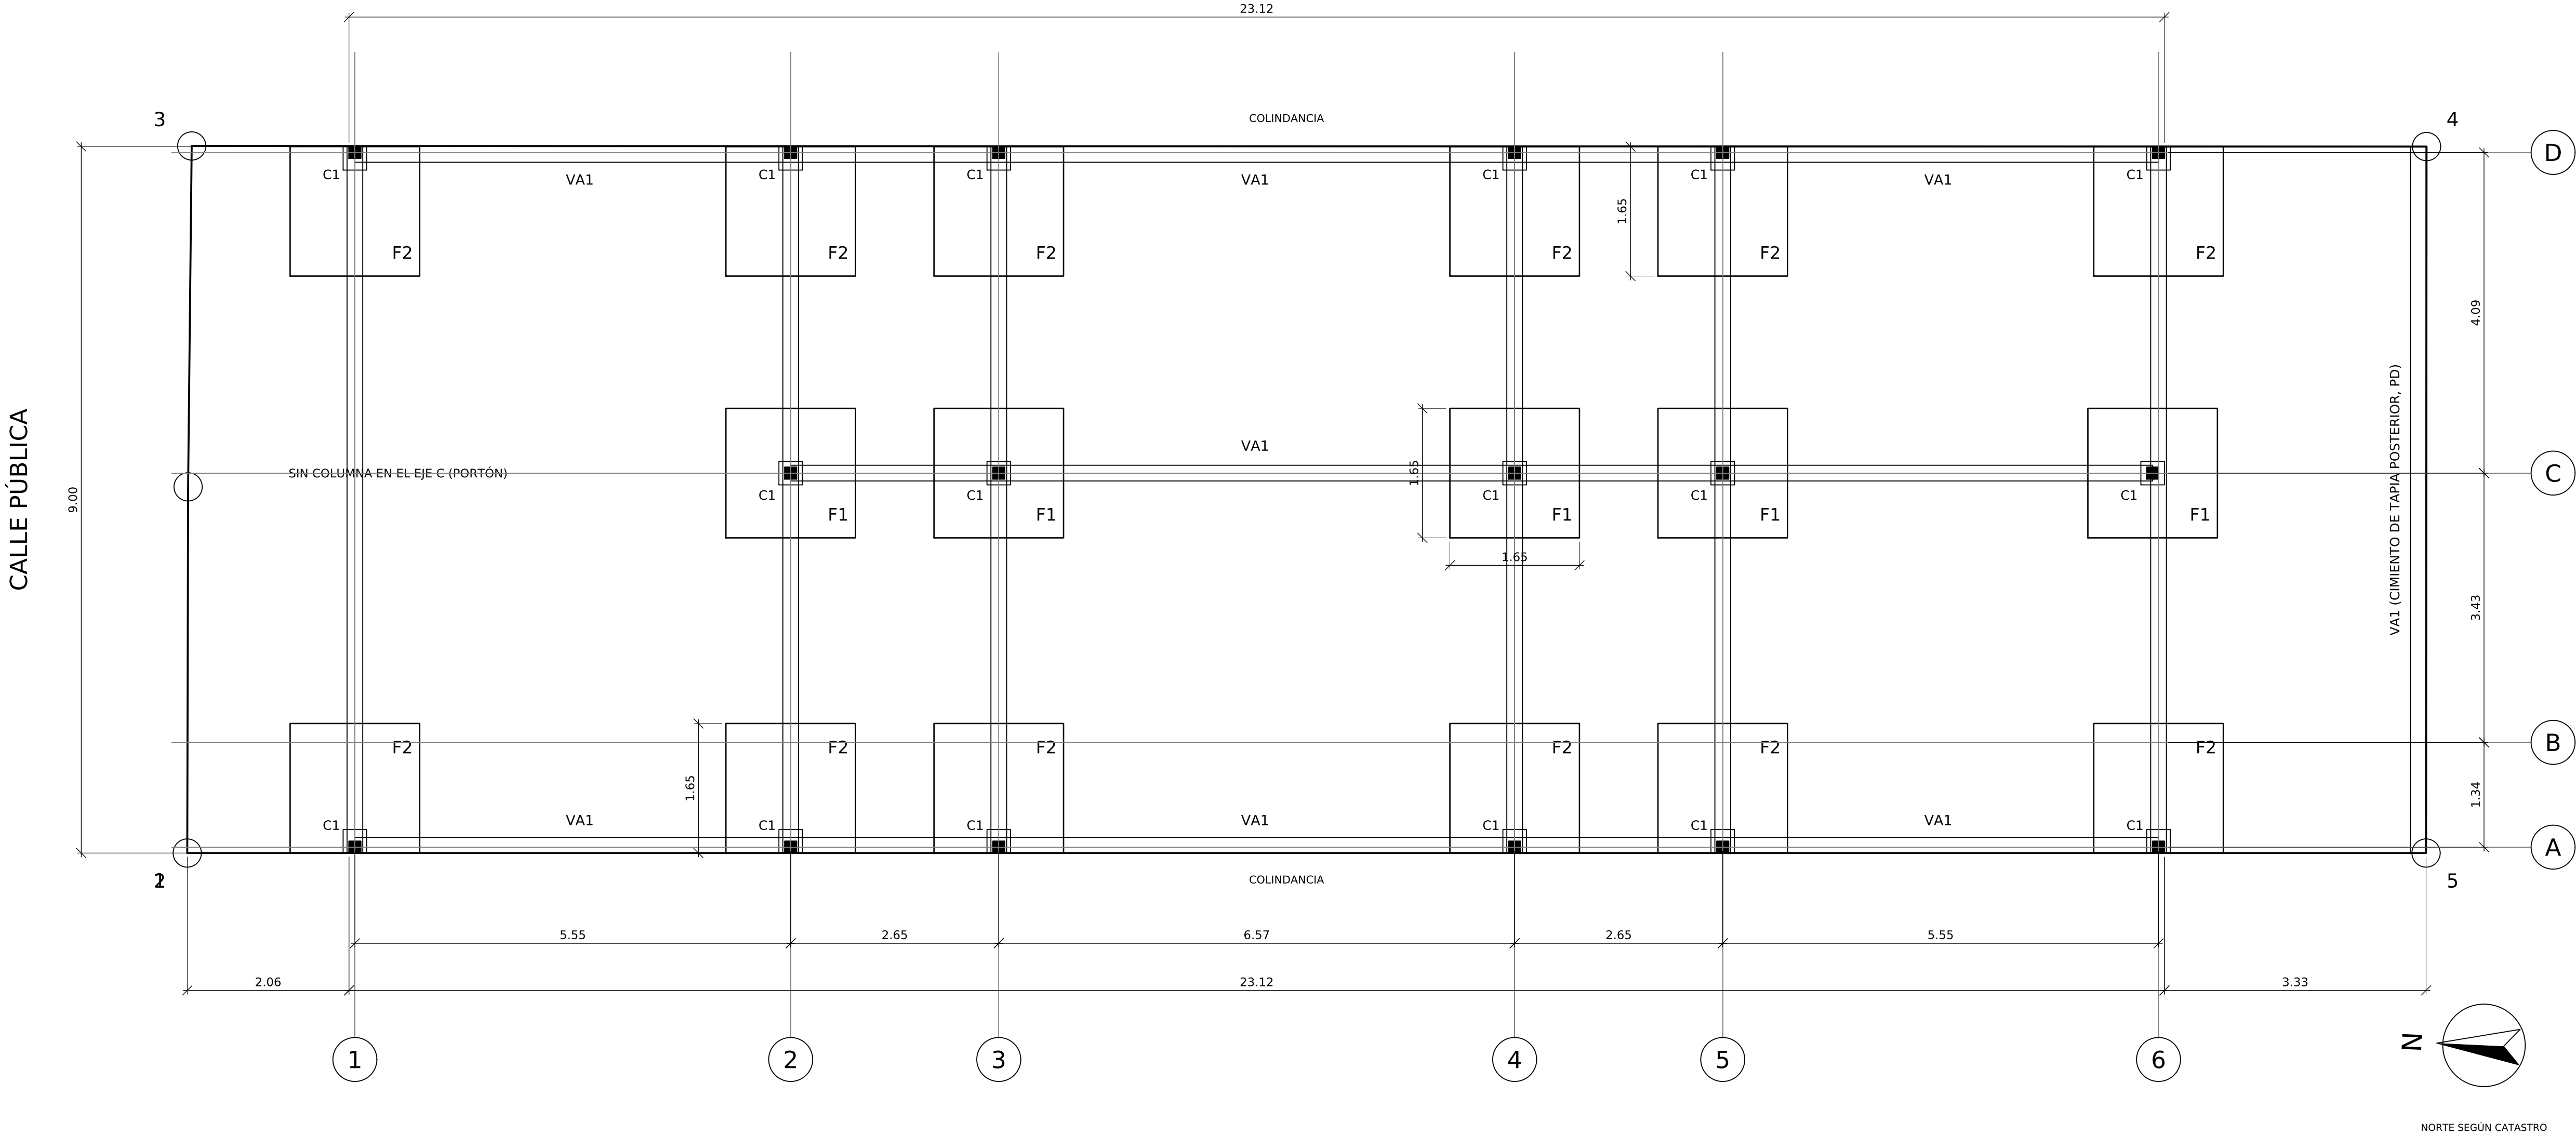

PLANTA DE CIMENTACIONES

PLACAS, PEDESTALES Y VIGAS RIOSTRA
Esc. 1:50



CUADRO DE CIMENTACIONES

TIPO	PLACA (m)	ESPESOR	REFUERZO	PEDESTAL	CANT.
F1	1,65 x 1,65 CENTRADA	0,25	MALLA #4 @20cm	0,30x0,30x0,80	5
F2	1,65 x 1,65 EXCÉNTRICA	0,25	MALLA #4 @20cm	0,30x0,30x0,80	12


PEDESTAL: 4 VARILLAS #4, ESTRIBOS #3 @10cm; PLETINA DE UNIÓN 270 x 270 mm. DETALLES EN LÁMINA C02. [PR]

SIMBOLOGÍA ELEMENTOS PORTANTES

C1	COLUMNA - TUBO DE ACERO 6x6" EN 3,17mm (EJE C FORRADA A 0,30 x 0,30) [PR]
VA1	VIGA RIOSTRA DE CONCRETO 0,20 x 0,40, 6 #4, AROS #3 @20cm [PR]
F1 / F2	PLACA AISLADA CENTRADA / EXCÉNTRICA (VER C02) [PR]

NOTAS:

- 1.- TODAS LAS MEDIDAS ESTÁN DADAS EN METROS, SALVO INDICACIÓN CONTRARIA. [PR]
2.- CAPACIDAD SOPORTANTE ADMISIBLE DEL SUELO CONSIDERADA: qadm = 12 t/m² [PR]. DEBE VERIFICARSE CON ESTUDIO DE SUELOS ANTES DE CONSTRUIR.
3.- LAS PLACAS DEBEN APOYARSE SOBRE SUELO NATURAL PREPARADO ADECUADAMENTE. NIVEL DE DESPLANTE SEGÚN DETALLE C02 (PEDESTAL 0,80 m + PLACA 0,25 m). [PR]
4.- COLUMNAS C1 EN LOS EJES A Y D (EJES 1 A 6) Y EN EL EJE C (EJES 2 A 6). SIN COLUMNA EN EL EJE C DEL EJE 1 PARA NO OBSTRUIR EL PORTÓN (LA C1 DE LOS NIVELES 2 Y 3 EN ESE PUNTO APOYA EN LA VIGA DE TRANSFERENCIA VT-1, VER C05). LAS PLACAS DE LINDERO (F2) SON EXCÉNTRICAS Y NO INVADEN EL PREDIO VECINO.
5.- VIGAS RIOSTRA VA1 EN LOS EJES A, C Y D Y EN LOS EJES 1 A 6. LOS MUROS DE LINDERO Y EL FRENTE DEL NIVEL 1 (MAMPOSTERÍA) APOYAN SOBRE LAS VA1. CIMIENTO DE LA TAPIA POSTERIOR: VA1 (PD).
6.- CONTRAPISO DE 0,10 m EN ESTACIONAMIENTOS, PASILLO, VESTÍBULO Y GRADAS (VER A2 Y A6).
7.- MATERIALES, RECUBRIMIENTOS Y ESPECIFICACIONES SEGÚN LÁMINA C06. [PR]
8.- LAS SECCIONES DE ESTA LÁMINA SON LAS DEL PROYECTO DE REFERENCIA, POR INDICACIÓN DEL INGENIERO RESPONSABLE; NO SUSTITUYEN LA MEMORIA DE CÁLCULO.
[PR] = NOTA TOMADA DEL PROYECTO DE REFERENCIA, PENDIENTE DE REVISIÓN.

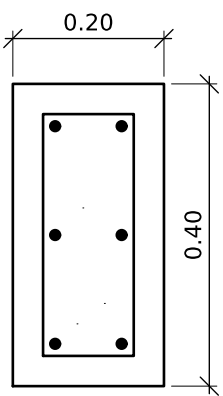

VIGA VA1: 0,20 x 0,40
6 VARILLAS #4
AROS VARILLA #3 @20cm
RECUBRIMIENTO 4cm [PR]

DETALLE DE VIGA RIOSTRA VA1

Esc. 1:10

ESPACIO PARA SELLOS Y TIMBRES

CivilCon Diseño y Construcción SRLTDA
Céd. Jurídica: 3-102-762712

PROFESIONAL RESPONSABLE:
DIRECTOR TÉCNICO:
Steven Viales (Civil) IC-40759
David Barrantes (Electricidad) IE-27499

PROYECTO:
VIVIENDA UNIFAMILIAR
DISTRITO 03 SANTIAGO, CANTÓN 05 SAN RAFAEL,
PROVINCIA 04 HEREDIA, COSTA RICA.

INFORMACIÓN REGISTRO PÚBLICO:
FOLIO REAL: 4-041200-000
PLANO CATASTRADO: 4-57389-2023
ÁREA SEGÚN CATASTRO: 256 m²

CONTENIDO:
FUNDACIONES
PLANTA DE CIMENTACIONES.
DETALLE DE VIGA RIOSTRA.
CUADRO DE CIMENTACIONES.
SIMBOLOGÍA.
NOTAS.

ESCALAS: 1:50 / INDICADAS

CONTROL DE REVISIONES		
REV.	FECHA	DESCRIPCIÓN
0	06-10-2026	VERSIÓN DE TRABAJO PARA REVISIÓN
1	06-10-2026	REFERENCIA A C06; NOTA C1 EJE C-1 SOBRE VT-1

ESTADO:
VERSIÓN DE TRABAJO
NO APTA PARA CONSTRUCCIÓN NI TRÁMITE

LUGAR	LÁMINA
COSTA RICA	C01
OCT 2026	TOTAL --