


CALLE PÚBLICA

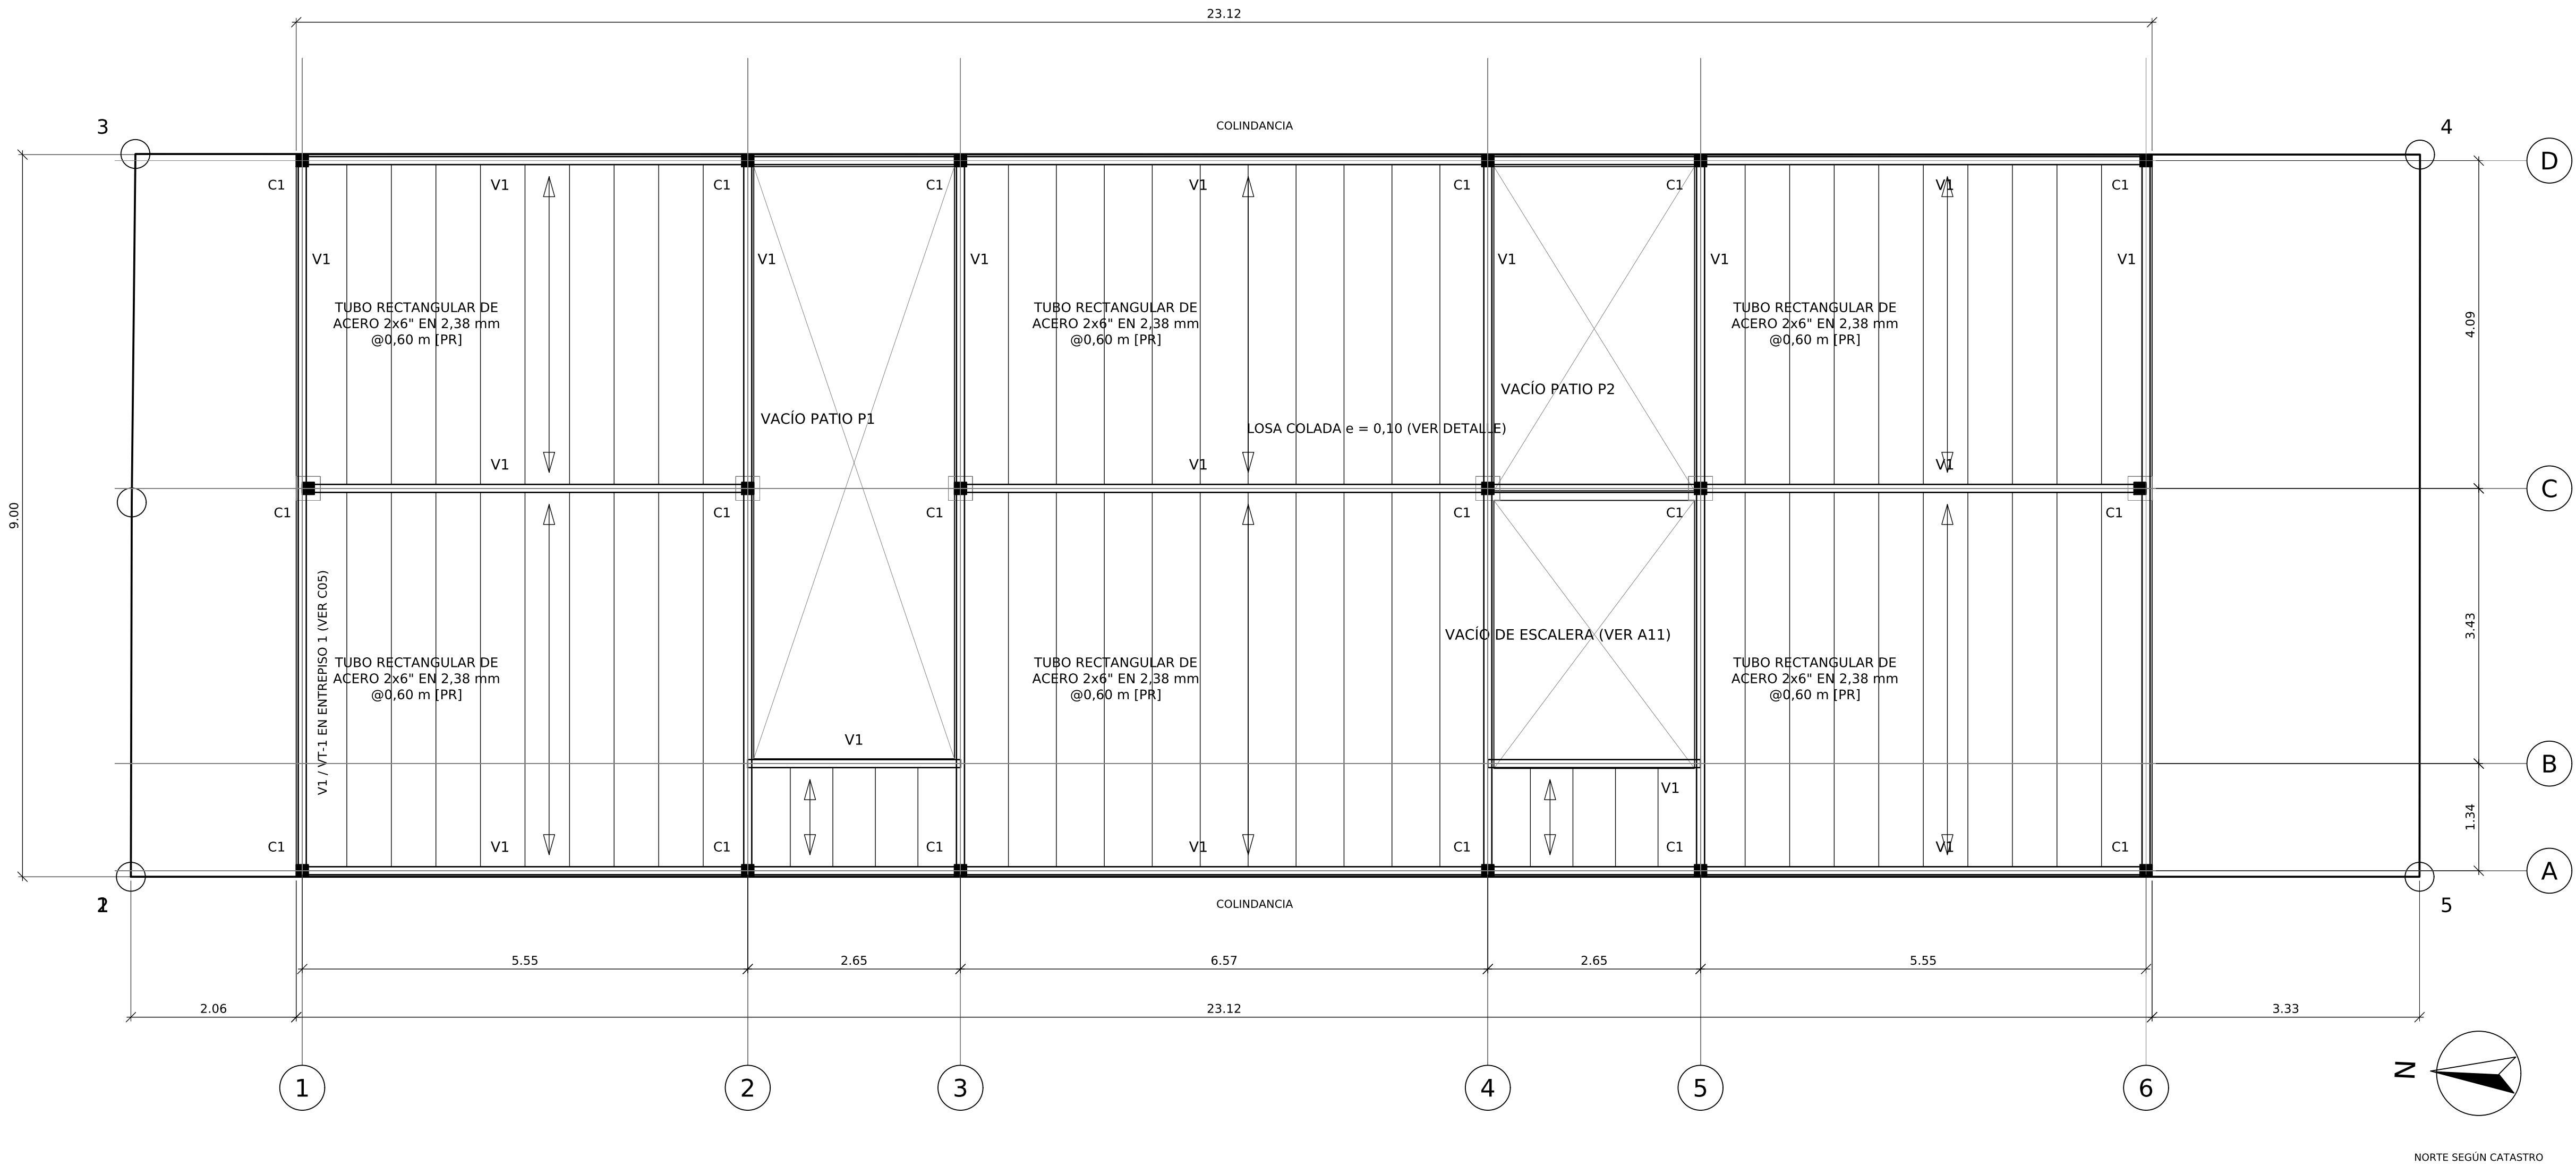


PLANTA DE ENTREPISO 1 Y 2

ENTREPISO 1: NIVEL 2 (NPT +3.00) / ENTREPISO 2: NIVEL 3 (NPT +6.00)
Esc. 1:50




SIMBOLOGÍA ELEMENTOS PORTANTES

C1	COLUMNA - TUBO DE ACERO 6x6" EN 3,17 mm [PR]
	(EJE C FORRADA A 0,30 x 0,30)
V1	VIGA - TUBO DE ACERO 4x8" EN 3,17 mm [PR]
VT-1	VIGA DE TRANSFERENCIA EJE 1, ENTREPISO 1 (PD)
VG	VIGUETA - TUBO 2x6" EN 2,38 mm @0,60 m [PR]
	VACÍO (PATIO O ESCALERA)

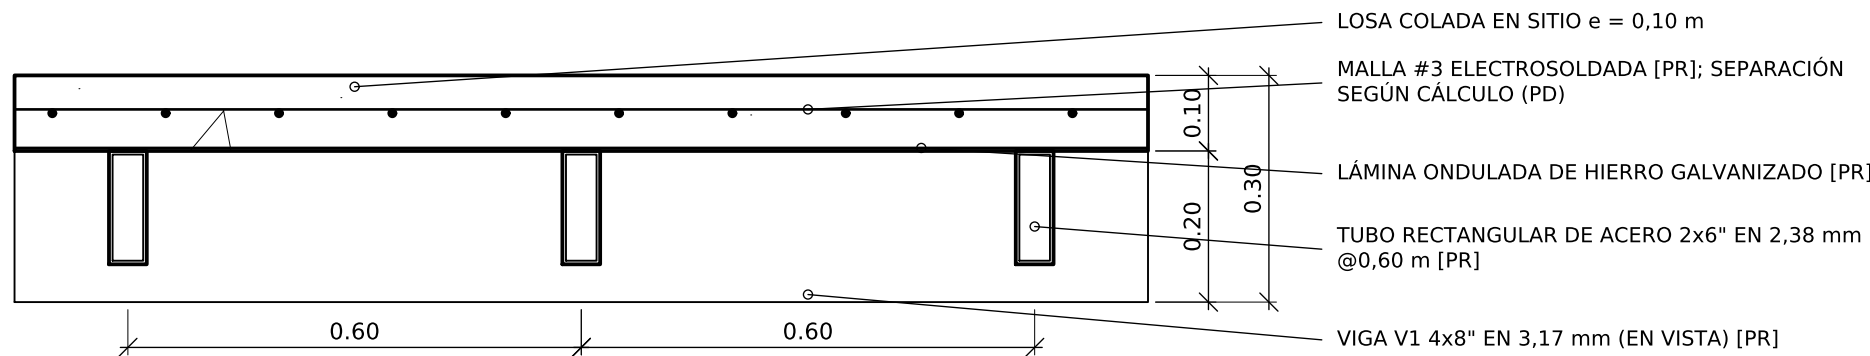

DETALLE DE ENTREPISO

CORTE PERPENDICULAR A LAS VIGUETAS - Esc. 1:10

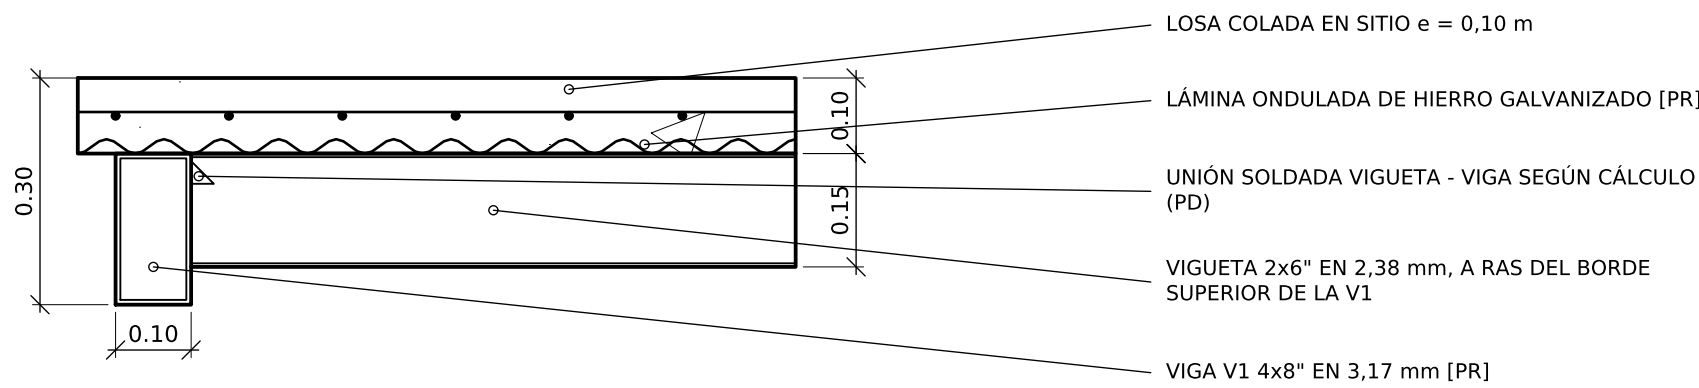

SECCIÓN A-A

A LO LARGO DE LA VIGUETA - Esc. 1:10

NOTAS:

- TODAS LAS MEDIDAS ESTÁN DADAS EN METROS, SALVO INDICACIÓN CONTRARIA. [PR]
- ENTREPISO: LOSA COLADA EN SITIO DE 0,10 m CON MALLA #3 ELECTROSOLDADA SOBRE LÁMINA ONDULADA DE HIERRO GALVANIZADO, APOYADA EN VIGUETAS DE TUBO 2x6" EN 2,38 mm. [PR]
- VIGUETAS EN SENTIDO TRANSVERSAL (ENTRE LAS VIGAS DE LOS EJES A, C Y D, Y A Y B EN LA FRANJA DEL PASILLO), SEPARACIÓN MÁXIMA 0,60 m REPARTIDA EN CADA PAÑO.
- VIGAS V1 4x8" EN 3,17 mm EN LOS EJES 1 A 6 (MARCOS A-C-D) Y EN LOS EJES A, C Y D; EN EL EJE B COMO BORDE DE LOS VACÍOS DEL PATIO P1 Y DE LA ESCALERA. [PR]
- PAQUETE DE ENTREPISO 0,30 m = VIGA 0,20 + LOSA 0,10 (VER A6). LAS VIGUETAS QUEDAN A RAS DEL BORDE SUPERIOR DE LAS VIGAS.
- COLUMNAS C1 CONTINUAS DEL NIVEL 1 AL NIVEL 3 (VER C01 Y C05). EN EL EJE C DEL EJE 1 LA C1 ARRANCA EN EL NIVEL 2 SOBRE LA VIGA DE TRANSFERENCIA VT-1 DEL ENTREPISO 1 (DISEÑO ESPECIAL, PD); SIN COLUMNA EN EL NIVEL 1 (PORTÓN).
- UNIONES SOLDADAS, PERFILES DEFINITIVOS Y SEPARACIÓN DE LA MALLA SEGÚN MEMORIA DE CÁLCULO (PD).
- MATERIALES, PROTECCIÓN ANTICORROSIVA Y ESPECIFICACIONES SEGÚN LÁMINA C06. [PR]
- LAS SECCIONES DE ESTA LÁMINA SON LAS DEL PROYECTO DE REFERENCIA, POR INDICACIÓN DEL INGENIERO RESPONSABLE; NO SUSTITUYEN LA MEMORIA DE CÁLCULO.
- [PR] = NOTA TOMADA DEL PROYECTO DE REFERENCIA, PENDIENTE DE REVISIÓN.

ESPACIO PARA SELLOS Y TIMBRES

CivilCon Diseño y Construcción SRLTDA
Céd. Jurídica: 3-102-762712

PROFESIONAL RESPONSABLE:
DIRECTOR TÉCNICO:
Steven Viales (Civil) IC-40759
David Barrantes (Electricidad) IE-27499

PROYECTO:
VIVIENDA UNIFAMILIAR
DISTRITO 03 SANTIAGO, CANTÓN 05 SAN RAFAEL,
PROVINCIA 04 HEREDIA, COSTA RICA.

INFORMACIÓN REGISTRO PÚBLICO:
FOLIO REAL: 4-041200-000
PLANO CATASTRADO: 4-57389-2023
ÁREA SEGÚN CATASTRO: 256 m²

CONTENIDO:
ENTREPISO
PLANTA DE ENTREPISO 1 Y 2.
DETALLE DE ENTREPISO.
SECCIÓN A-A.
SIMBOLOGÍA.
NOTAS.

ESCALAS: 1:50 / INDICADAS

CONTROL DE REVISIONES		
REV.	FECHA	DESCRIPCIÓN
0	06-10-2026	VERSIÓN DE TRABAJO PARA REVISIÓN
1	06-10-2026	ENTREPISOS 1 Y 2 EN UNA SOLA LÁMINA
2	06-10-2026	C1 EJE C-1 SOBRE VT-1; REFERENCIA A C06

ESTADO:
VERSIÓN DE TRABAJO
NO APTA PARA CONSTRUCCIÓN NI TRÁMITE

LUGAR	LÁMINA
COSTA RICA	C03
OCT 2026	TOTAL --