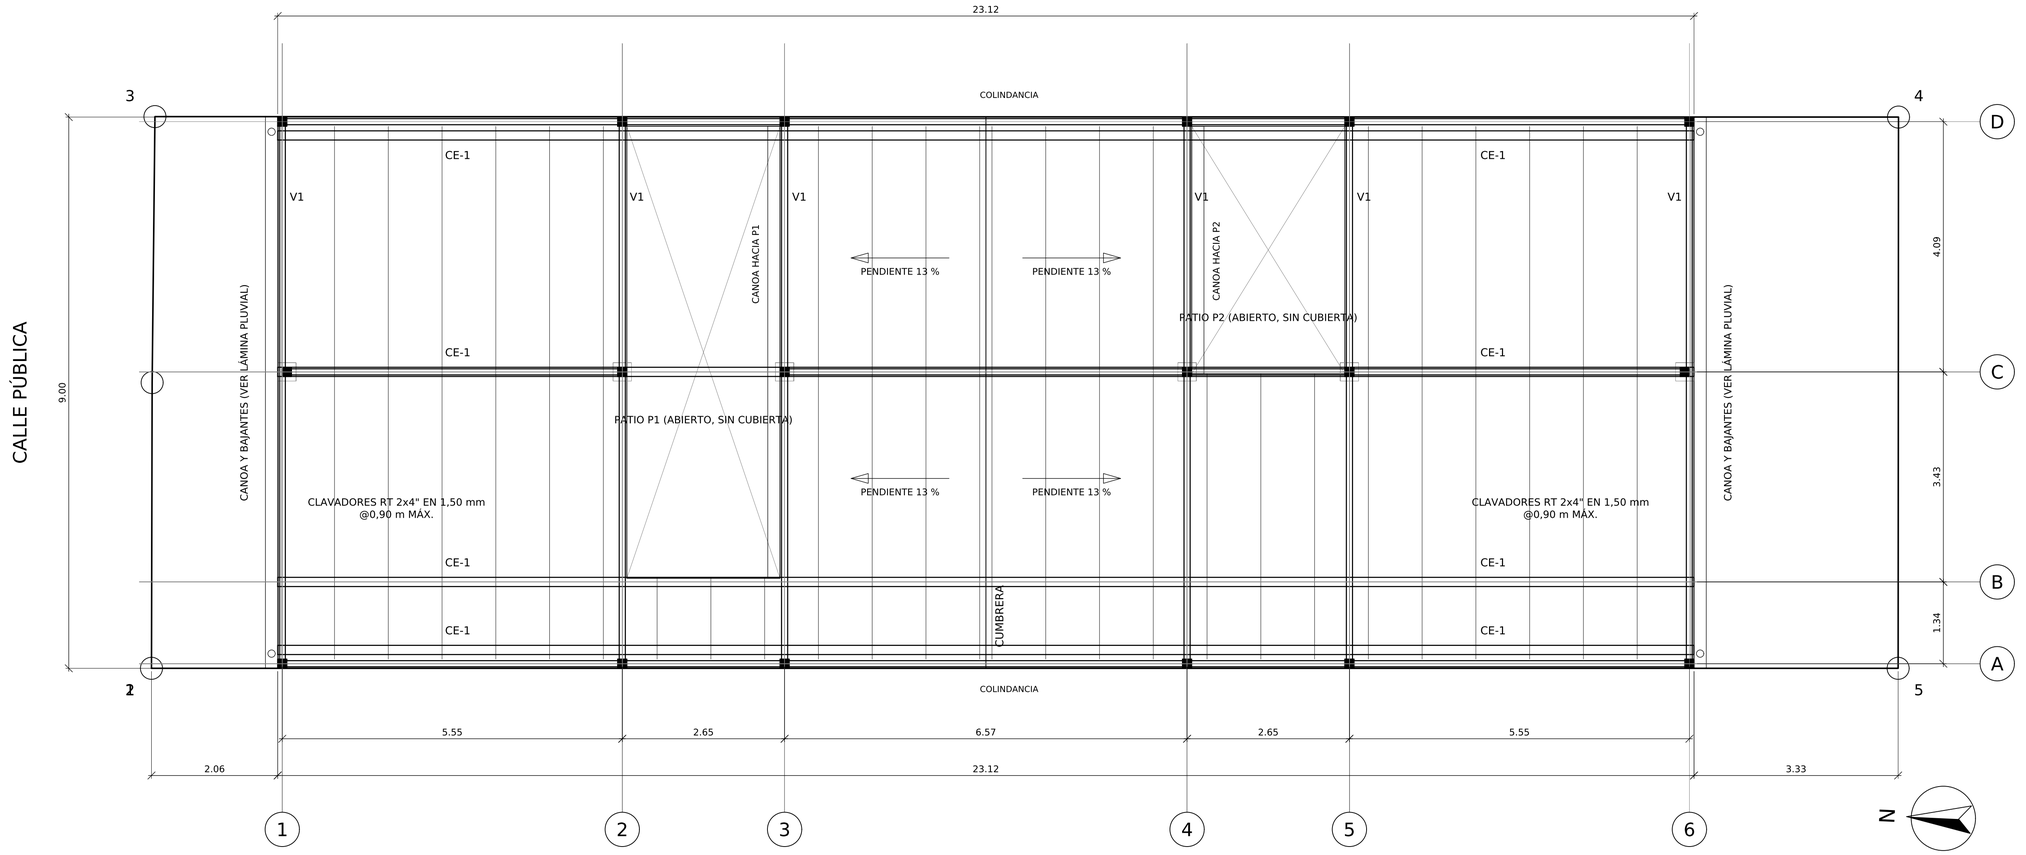




# PLANTA DE TECHO

ESTRUCTURA DE CUBIERTA
Esc. 1:50

0 1 2 3 4 5 m


## SIMBOLOGÍA ELEMENTOS PORTANTES

| | |
|---|---|
| C1 | COLUMNA - TUBO DE ACERO 6x6" EN 3,17 mm [PR] |
| V1 | VIGA DE CORONA - TUBO 4x8" EN 3,17 mm, +9,00 [PR] |
| CE-1 | CERCHA - CORDONES 2x6" EN 2,38 mm |
| | DIAGONALES Y MONTANTES 2x2" EN 1,50 mm |
| CL | CLAVADOR - TUBO RT 2x4" EN 1,50 mm @0,90 m MÁX. |
| ⊠ | PATIO ABIERTO (SIN CUBIERTA) |

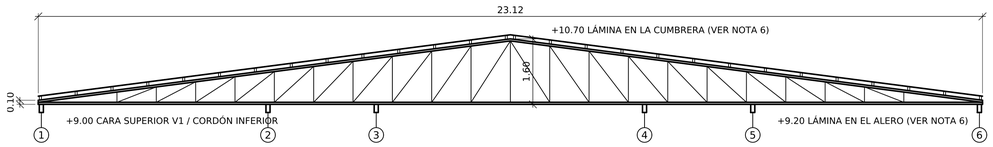


## CERCHA TÍPICA CE-1 (ELEVACIÓN)

EN x 0,30 / EJE B / EJE C / x 8,70 - Esc. 1:75

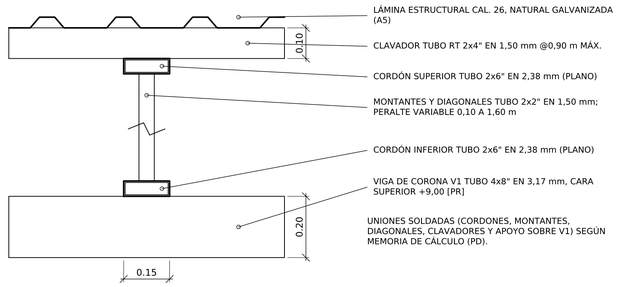


## SECCIÓN TÍPICA DE CUBIERTA

PERPENDICULAR A LA CERCHA - Esc. 1:10

## NOTAS:

1.- TODAS LAS MEDIDAS ESTÁN DADAS EN METROS, SALVO INDICACIÓN CONTRARIA. [PR]
2.- CUBIERTA DE LÁMINA ESTRUCTURAL CAL. 26 A DOS AGUAS (FRENTE Y FONDO), PENDIENTE 13 %, SOBRE CLAVADORES Y CERCHAS METÁLICAS EN LA DIRECCIÓN DE LA PENDIENTE (A5, A6).
3.- CERCHAS CE-1 EN x 0,30, EJE B, EJE C Y x 8,70, APOYADAS EN LAS VIGAS DE CORONA V1 DE LOS EJES 1 A 6. LA CERCHA DEL EJE C ES CONTINUA SOBRE EL PATIO P1.
4.- VIGAS DE CORONA V1 A +9,00 EN LOS EJES 1 A 6 Y EN A, C Y D, SOBRE LAS COLUMNAS C1, IGUAL QUE EN LOS ENTREPISOS (C03). [PR]
5.- PATIOS P1 Y P2 ABIERTOS, SIN CUBIERTA. CANOAS AL FRENTE, AL FONDO Y HACIA LOS PATIOS; BAJANTES Y DETALLE DE CANOA SEGÚN LÁMINA PLUVIAL.
6.- NIVELES DE LÁMINA RESULTANTES DE LA CERCHA: +9,20 EN EL ALERO Y +10,70 EN LA CUMBRERA (A5 Y A6 INDICAN +9,00 Y +10,50). PENDIENTE DE CONFIRMAR (PD).
7.- UNIONES SOLDADAS Y VERIFICACIÓN DE PERFILES SEGÚN MEMORIA DE CÁLCULO (PD).
8.- MATERIALES, PROTECCIÓN ANTICORROSIVA Y ESPECIFICACIONES SEGÚN LÁMINA C06.
[PR] = NOTA TOMADA DEL PROYECTO DE REFERENCIA, PENDIENTE DE REVISIÓN.

ESPACIO PARA SELLOS Y TIMBRES


CivilCon Diseño y Construcción SRLTDA
Céd. Jurídica: 3-102-762712

PROFESIONAL RESPONSABLE:
DIRECTOR TÉCNICO:
Steven Viales (Civil) IC-40759
David Barrantes (Electricidad) IE-27499


PROYECTO:
VIVIENDA UNIFAMILIAR
DISTRITO 03 SANTIAGO, CANTÓN 05 SAN RAFAEL, PROVINCIA 04 HEREDIA, COSTA RICA.

INFORMACIÓN REGISTRO PÚBLICO:
FOLIO REAL: 4-041200-000
PLANO CATASTRADO: 4-57389-2023
ÁREA SEGÚN CATASTRO: 256 m²

CONTENIDO:
TECHO
PLANTA DE TECHO.
CERCHA TÍPICA CE-1.
SECCIÓN TÍPICA DE CUBIERTA.
SIMBOLOGÍA.
NOTAS.

ESCALAS: 1:50 / INDICADAS

CONTROL DE REVISIONES

| REV. | FECHA | DESCRIPCIÓN |
|---|---|---|
| 0 | 06-10-2026 | VERSIÓN DE TRABAJO PARA REVISIÓN |
| 1 | 06-10-2026 | C1 EJE C-1 HASTA CORONA; REFERENCIA A C06 |
| | | |

ESTADO:
VERSIÓN DE TRABAJO
NO APTA PARA CONSTRUCCIÓN NI TRÁMITE

| LUGAR | LÁMINA |
|---|---|
| COSTA RICA | C04 |
| OCT 2026 | TOTAL -- |

FORMATO A1 841 mm x 594 mm