



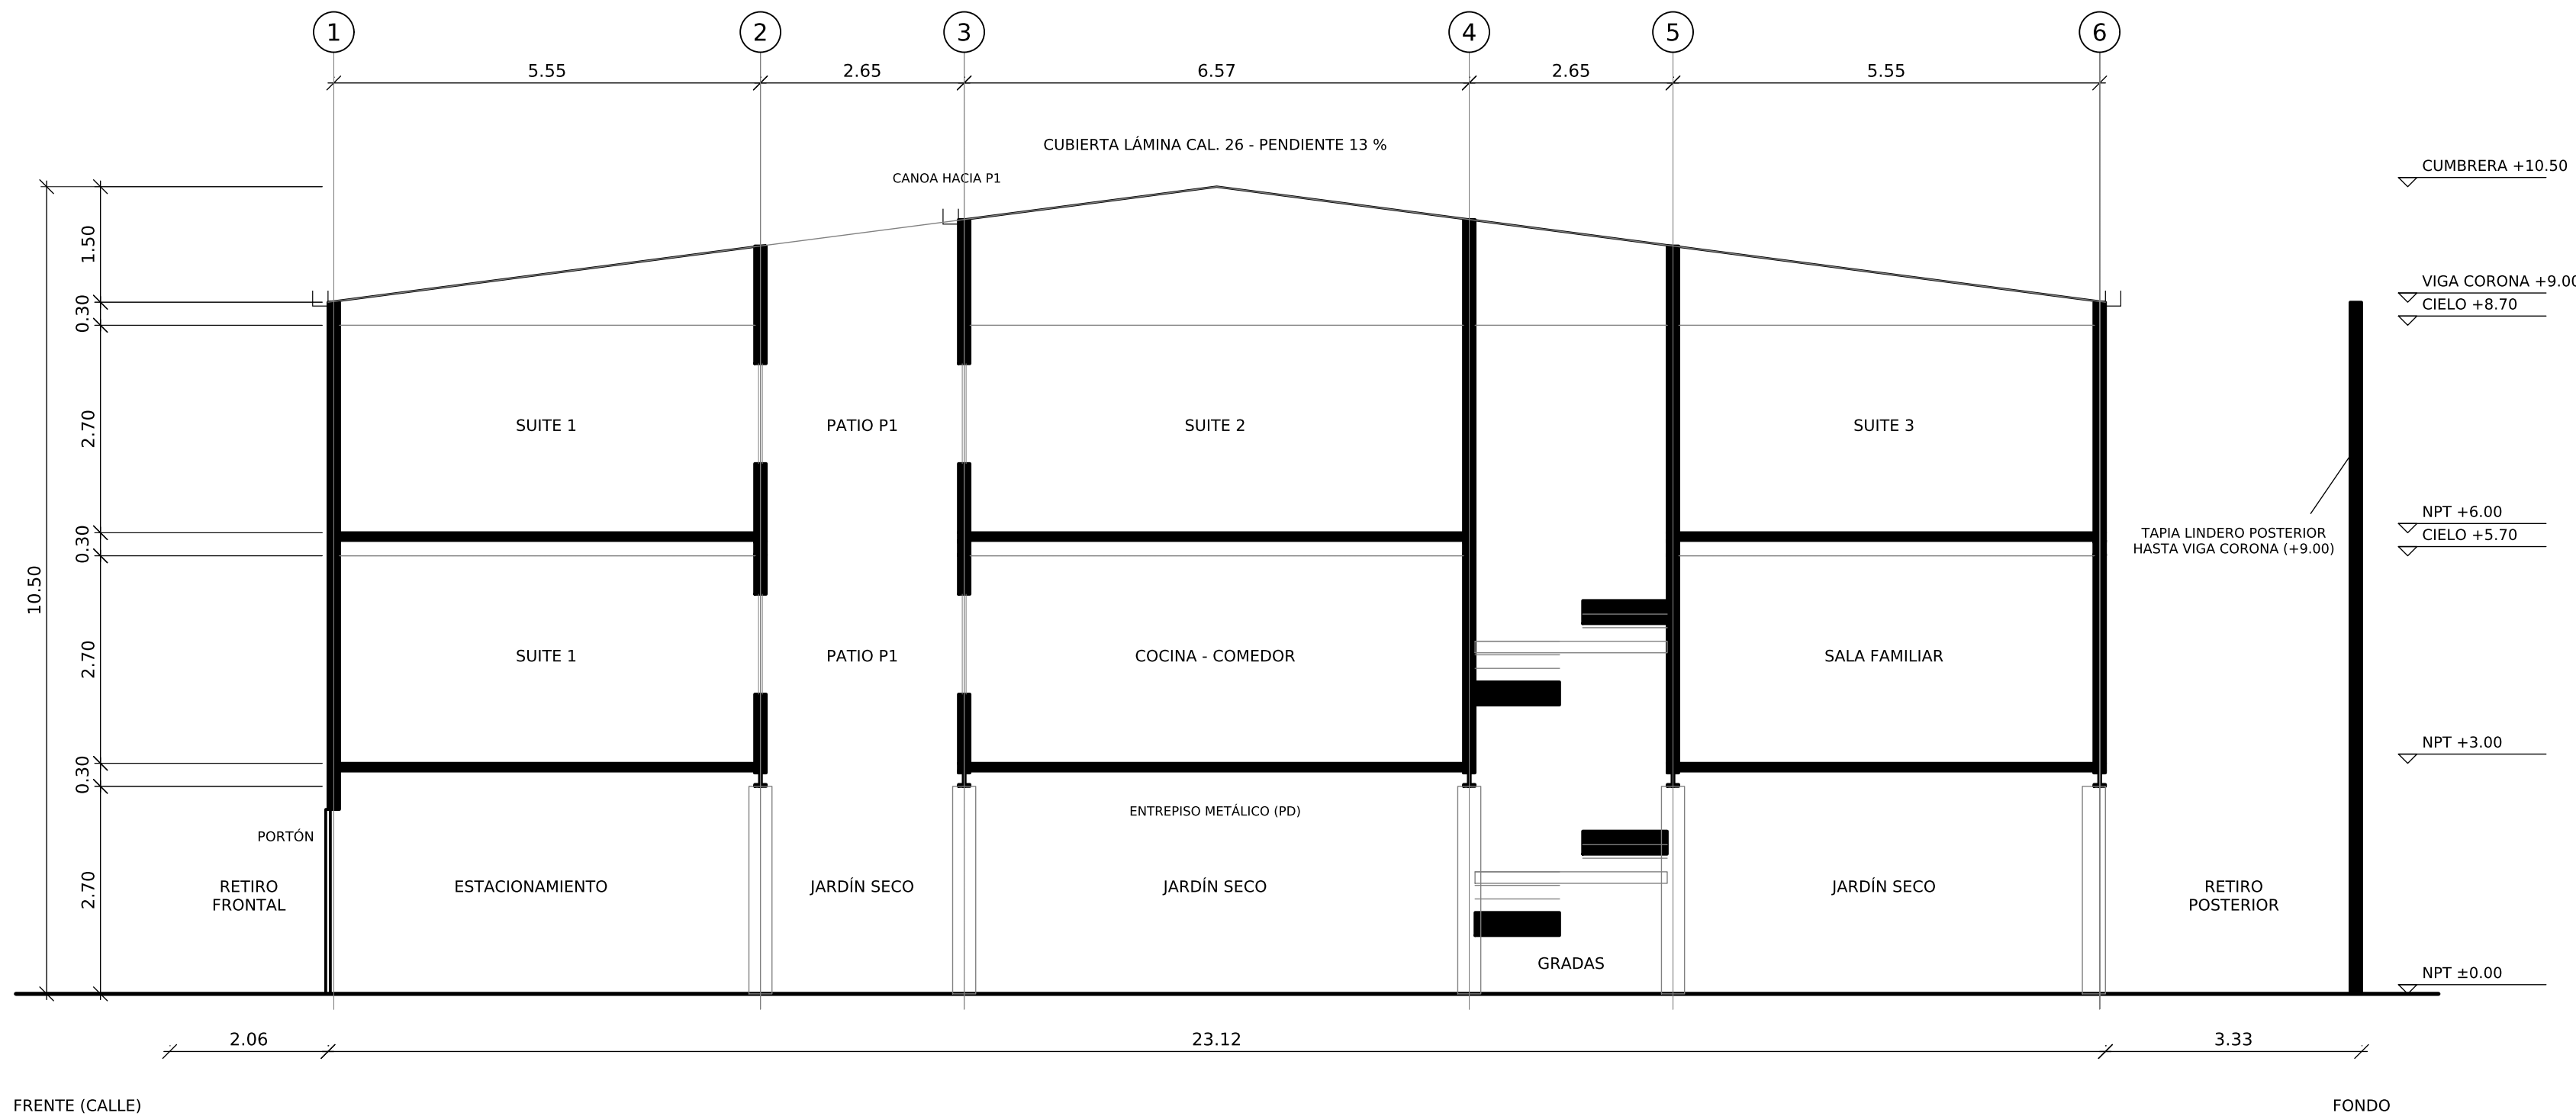

CORTE A-A

CORTE LONGITUDINAL EN x = 3.00 (VISTA HACIA EL ESTE)
Esc. 1:75

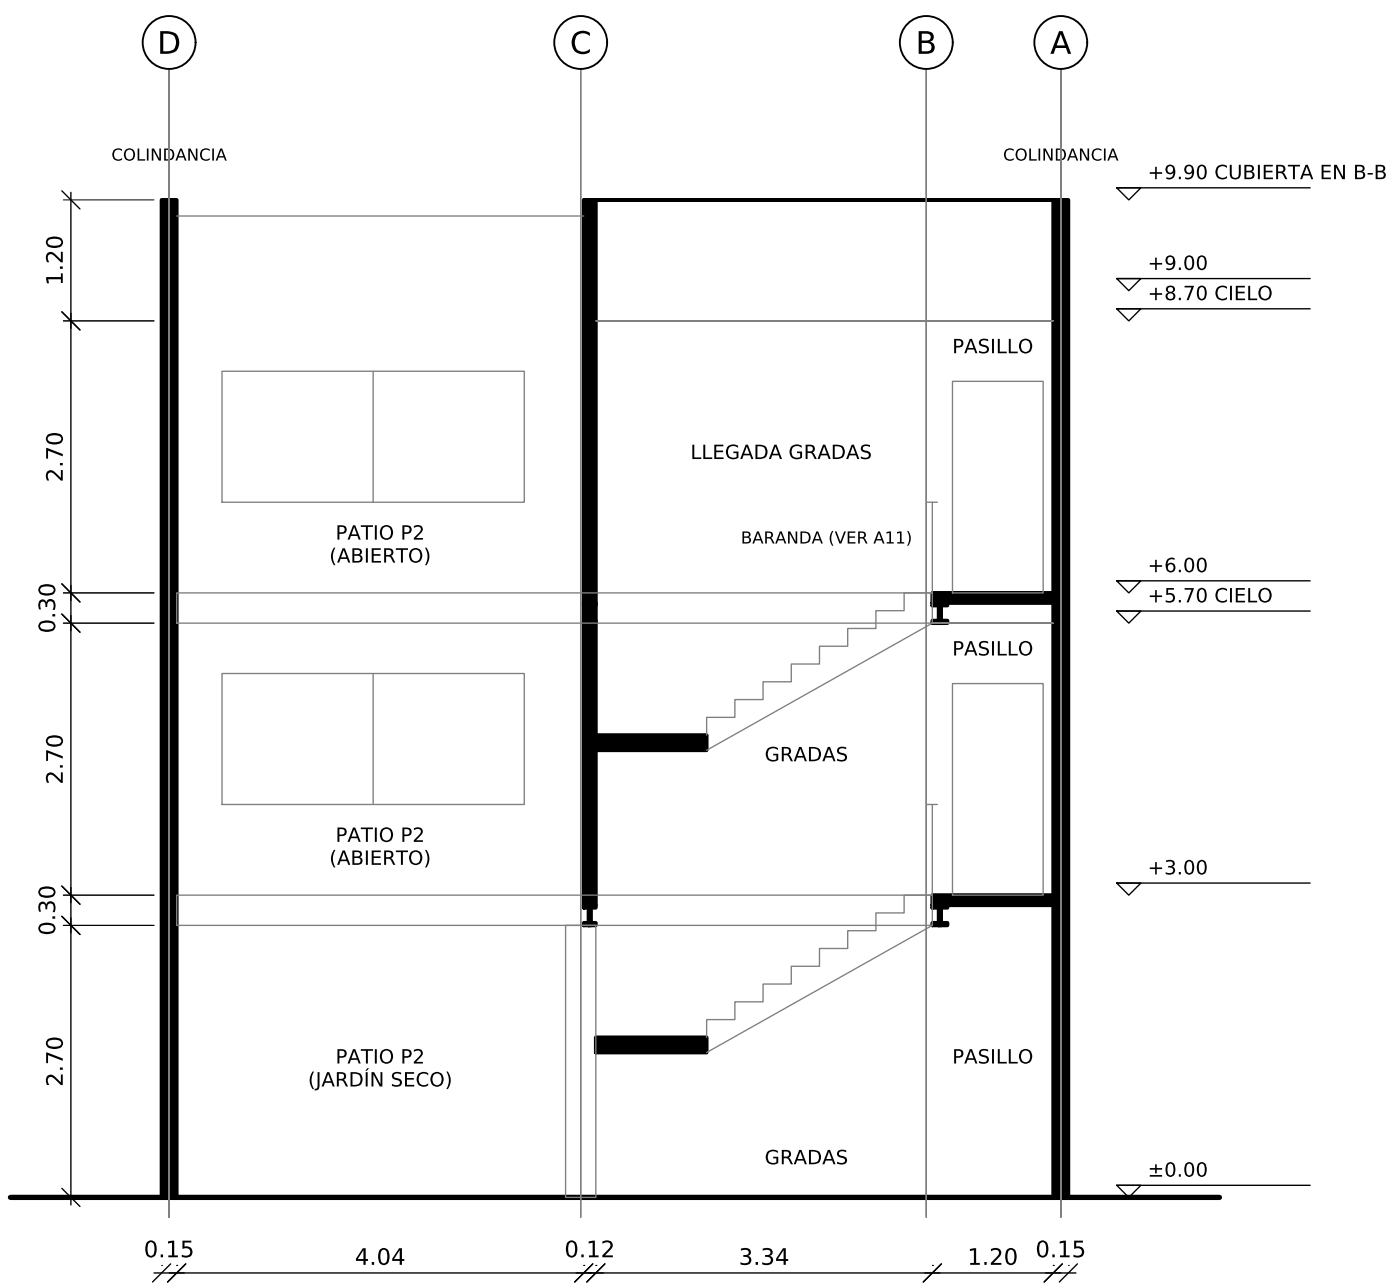

CORTE B-B

CORTE TRANSVERSAL EN y = 18.25 (VISTA HACIA EL FONDO)
Esc. 1:75



NOTAS:

- TODAS LAS MEDIDAS ESTÁN DADAS EN METROS, SALVO INDICACIÓN CONTRARIA. [PR]
- LA TAPIA COLINDANTE DE MAMPOSTERÍA DEBERÁ PROLONGARSE HASTA EL NIVEL DE LA VIGA CORONA DEL ÚLTIMO NIVEL, GARANTIZANDO EL APANTALLAMIENTO VISUAL PERMANENTE HACIA LA PROPIEDAD COLINDANTE.
- LOS BAÑOS CONTARÁN CON EXTRACTOR MECÁNICO DE AIRE.
- NIVELES: NPT N1 ±0.00 (ACERA), N2 +3.00, N3 +6.00; ALTURA DE PISO A PISO 3.00 m. CIELO RASO A 2.70 m SOBRE NPT EN LOS NIVELES 2 Y 3. NIVEL 1 SIN CIELO RASO.
- ENTREPIOS DE ESTRUCTURA METÁLICA: VIGAS DE ACERO Y LÁMINA COLABORANTE CON SOBRELOSA. ESPESORES DIBUJADOS (SOBRELOSA 0.10 m, VIGA 0.20 m) PRELIMINARES (PD); PERFILES, SECCIONES Y REFUERZO SEGÚN PLANOS ESTRUCTURALES.
- CUBIERTA DE LÁMINA ESTRUCTURAL CALIBRE 26 A DOS AGUAS, PENDIENTE 13 %, VIGA CORONA +9.00 Y CUMBRERA +10.50 AL CENTRO. CANOAS EN FRENTE, FONDO Y BORDES HACIA LOS PATIOS DONDE SE REQUIERA. ESTRUCTURA DE TECHO SEGÚN PLANOS ESTRUCTURALES.
- ESCALERA EN U: 17 CONTRAHUELLAS DE 0.176 m Y HUELLA DE 0.28 m POR NIVEL; DESCANSOS A +1.59 Y +4.59. BARANDAS Y PASAMANOS EN LÁMINA A11.
- ALTURAS PRELIMINARES (PD): PUERTAS 2.10 m; VENTANAS HACIA LOS PATIOS CON ANTEPECHO 0.90 m Y DINTEL 2.20 m. TIPOS EN LÁMINAS A7 A A9.
- LA TAPIA DEL LINDERO POSTERIOR LLEGA HASTA LA VIGA CORONA DEL ÚLTIMO NIVEL (+9.00).
- CIMENTACIÓN Y CONTRAPISO DEL NIVEL 1 SEGÚN PLANOS ESTRUCTURALES.
- TRAZO DE LOS CORTES SEGÚN LÁMINAS A2 A A4.
- [PR] = NOTA TOMADA DEL PROYECTO DE REFERENCIA, PENDIENTE DE REVISIÓN.

ESPACIO PARA SELLOS Y TIMBRES

CivilCon Diseño y Construcción SRLTDA
Céd. Jurídica: 3-102-762712

PROFESIONAL RESPONSABLE:
DIRECTOR TÉCNICO:
Steven Viales (Civil) IC-40759
David Barrantes (Electricidad) IE-27499

PROYECTO:
VIVIENDA UNIFAMILIAR
DISTRITO 03 SANTIAGO, CANTÓN 05 SAN RAFAEL,
PROVINCIA 04 HEREDIA, COSTA RICA.

INFORMACIÓN REGISTRO PÚBLICO:
FOLIO REAL: 4-041200-000
PLANO CATASTRADO: 4-57389-2023
ÁREA SEGÚN CATASTRO: 256 m²

CONTENIDO:
CORTES
CORTE A-A,
CORTE B-B,
NOTAS.

ESCALAS: 1:75

CONTROL DE REVISIONES

REV.	FECHA	DESCRIPCIÓN
0	06-10-2026	VERSIÓN DE TRABAJO PARA REVISIÓN

ESTADO:

VERSIÓN DE TRABAJO
NO APTA PARA CONSTRUCCIÓN NI TRÁMITE

LUGAR	LÁMINA
COSTA RICA	A6
OCT 2026	TOTAL --