


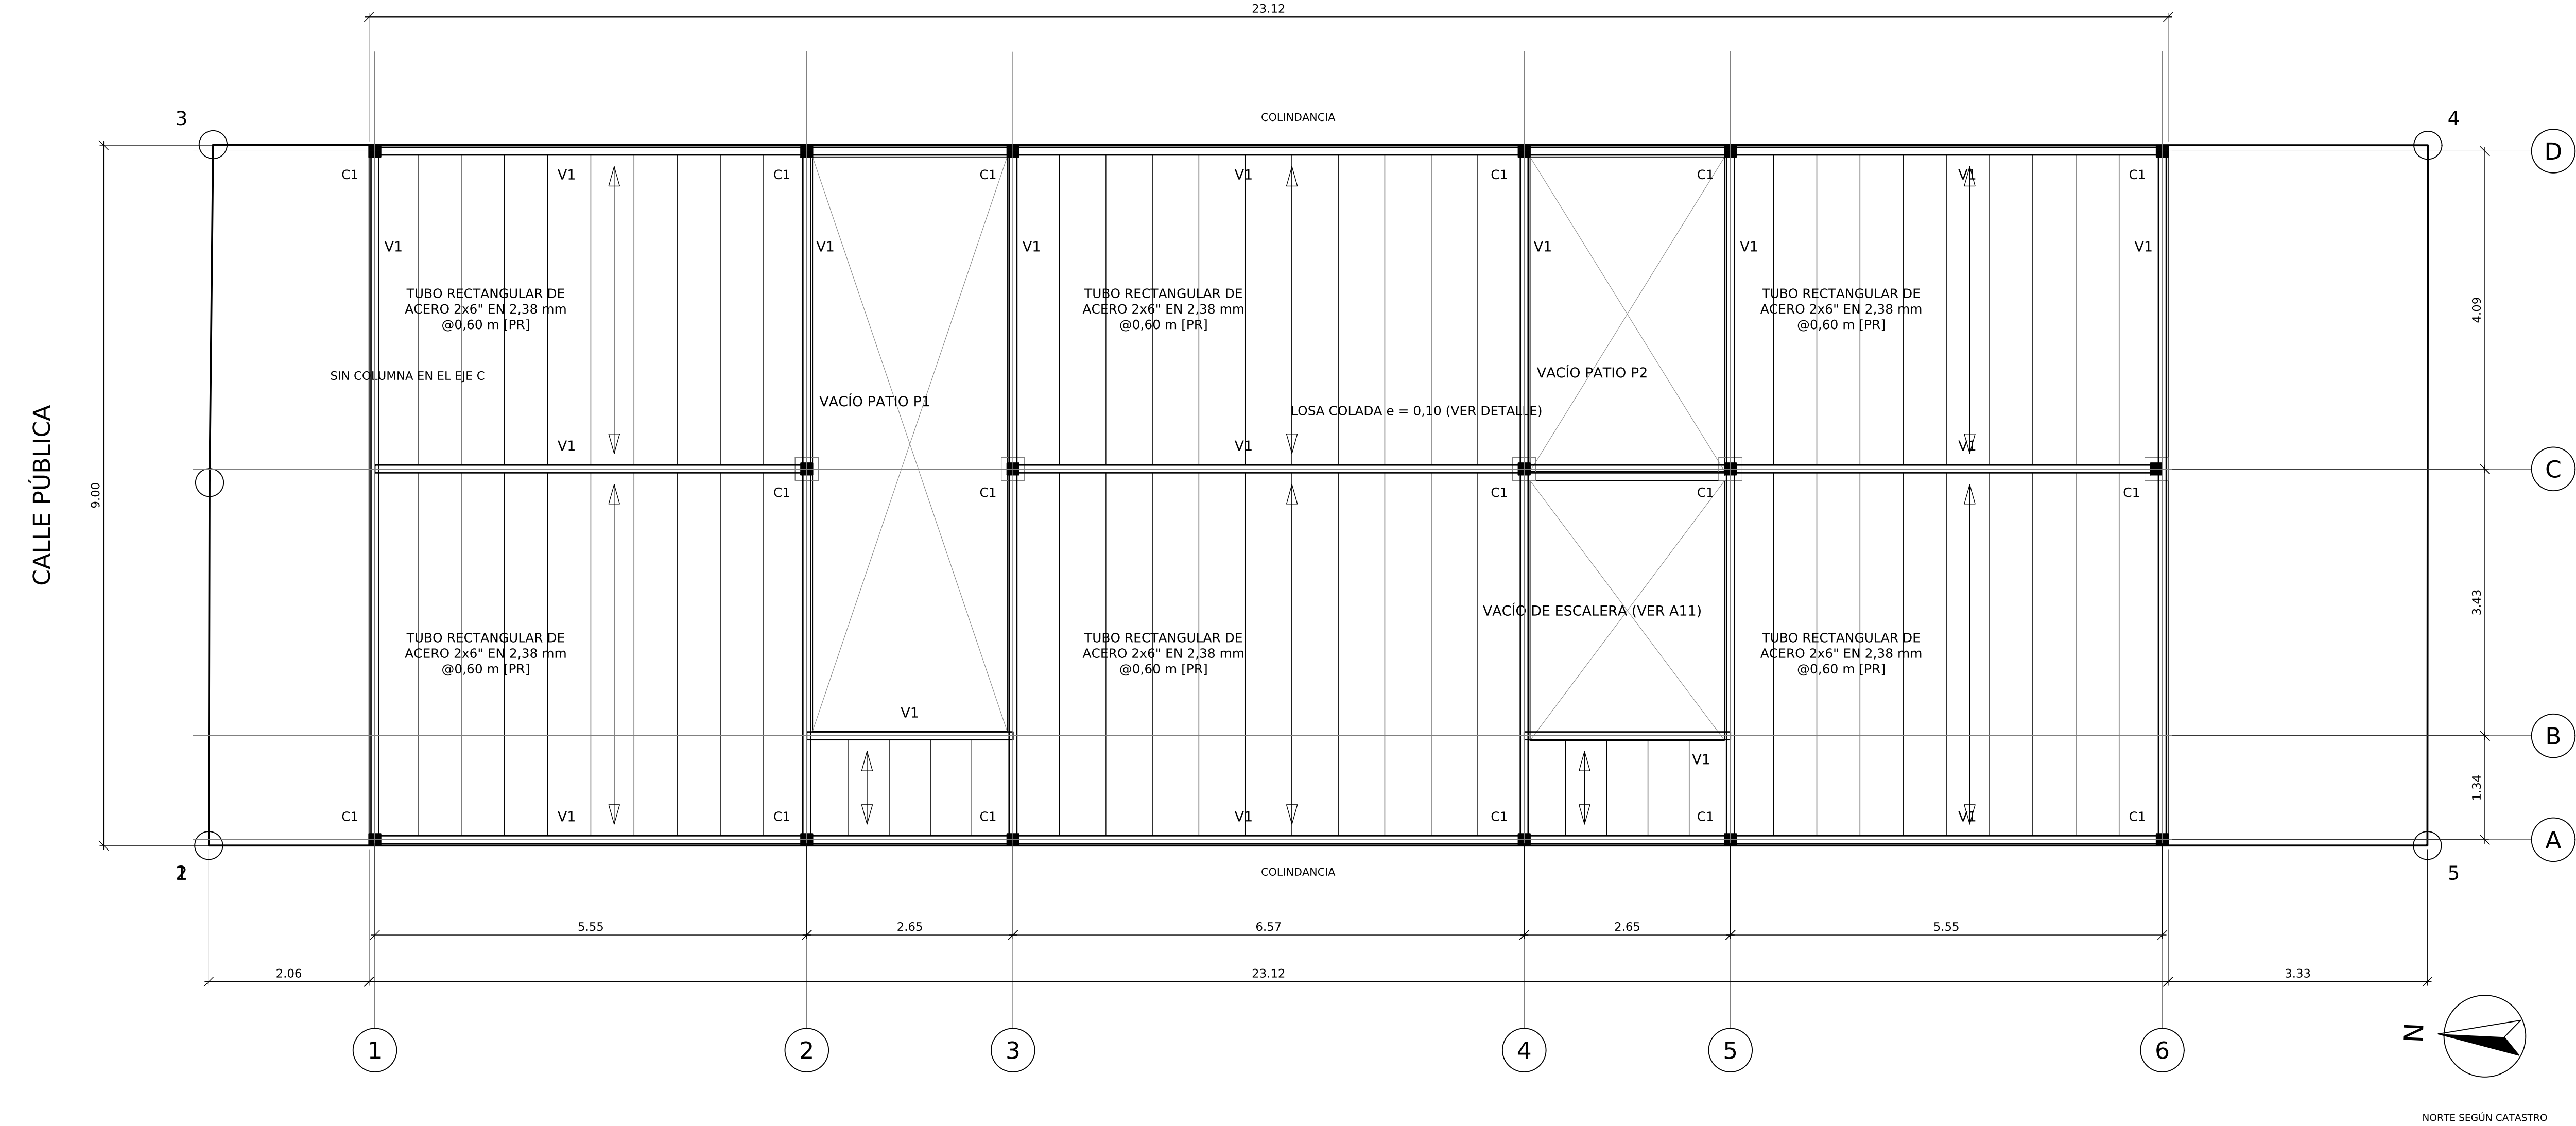


PLANTA DE ENTREPISO 1 Y 2

ENTREPISO 1: NIVEL 2 (NPT +3.00) / ENTREPISO 2: NIVEL 3 (NPT +6.00)

Esc. 1:50




SIMBOLOGÍA ELEMENTOS PORTANTES	
C1	COLUMNA - TUBO DE ACERO 6x6" EN 3,17 mm [PR]
	(EJE C FORRADA A 0,30 x 0,30)
V1	VIGA - TUBO DE ACERO 4x8" EN 3,17 mm [PR]
VG	VIGUETA - TUBO 2x6" EN 2,38 mm @0,60 m [PR]
	VACÍO (PATIO O ESCALERA)

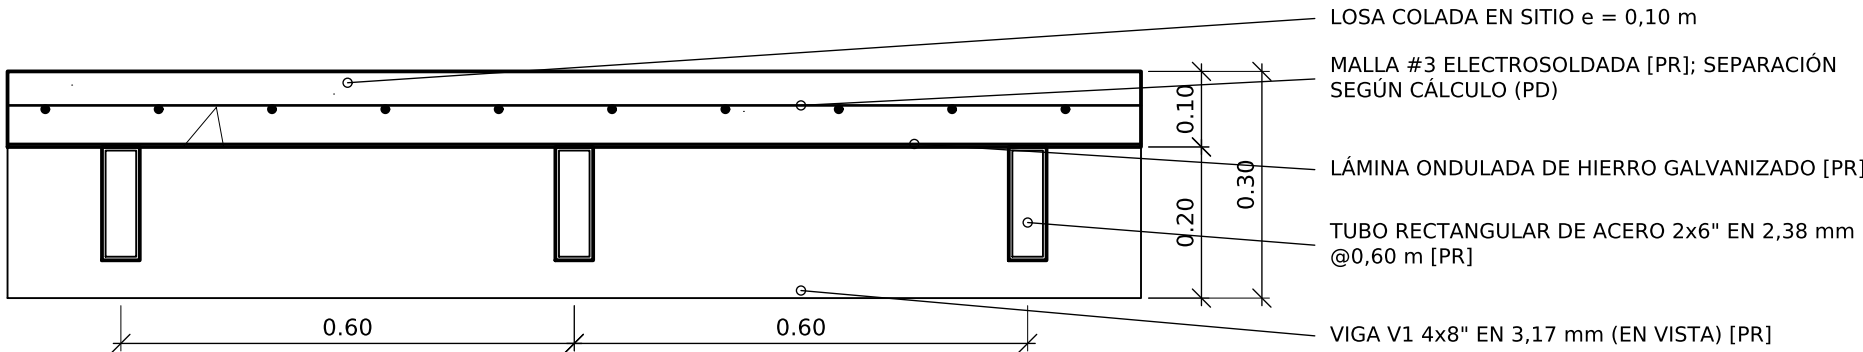

DETALLE DE ENTREPISO

CORTE PERPENDICULAR A LAS VIGUETAS - Esc. 1:10

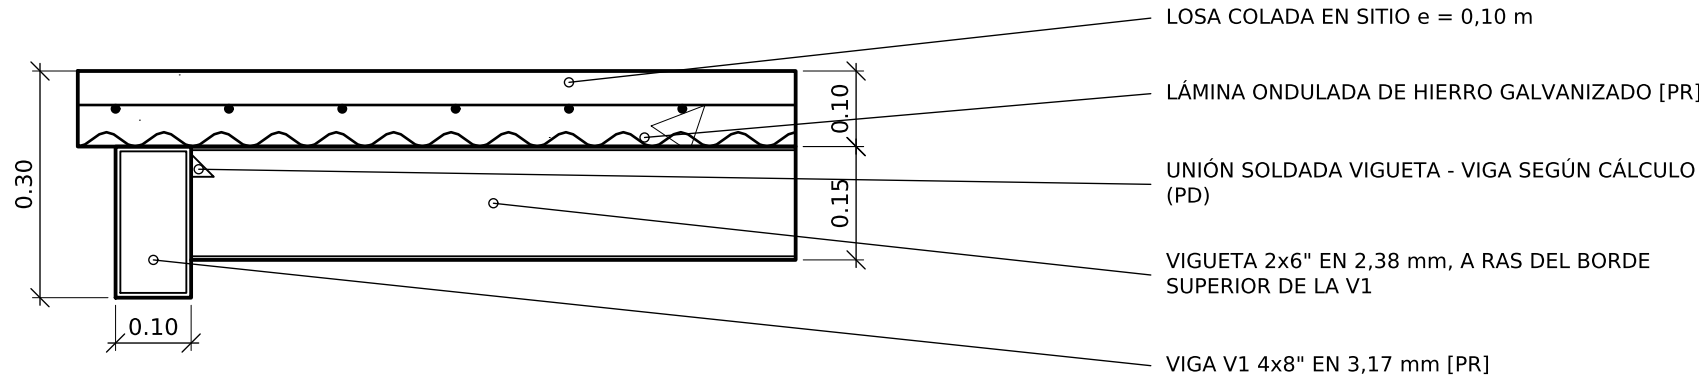

SECCIÓN A-A

A LO LARGO DE LA VIGUETA - Esc. 1:10

- NOTAS:
- TODAS LAS MEDIDAS ESTÁN DADAS EN METROS, SALVO INDICACIÓN CONTRARIA. [PR]
 - ENTREPISO: LOSA COLADA EN SITIO DE 0,10 m CON MALLA #3 ELECTROSOLDADA SOBRE LÁMINA ONDULADA DE HIERRO GALVANIZADO, APOYADA EN VIGUETAS DE TUBO 2x6" EN 2,38 mm. [PR]
 - VIGUETAS EN SENTIDO TRANSVERSAL (ENTRE LAS VIGAS DE LOS EJES A, C Y D, Y A Y B EN LA FRANJA DEL PASILLO), SEPARACIÓN MÁXIMA 0,60 m REPARTIDA EN CADA PAÑO.
 - VIGAS V1 4x8" EN 3,17 mm EN LOS EJES 1 A 6 (MARCOS A-C-D) Y EN LOS EJES A, C Y D; EN EL EJE B COMO BORDE DE LOS VACÍOS DEL PATIO P1 Y DE LA ESCALERA. [PR]
 - PAQUETE DE ENTREPISO 0,30 m = VIGA 0,20 + LOSA 0,10 (VER A6). LAS VIGUETAS QUEDAN A RAS DEL BORDE SUPERIOR DE LAS VIGAS.
 - COLUMNAS C1 CONTINUAS DEL NIVEL 1 AL NIVEL 3 (VER C01). SIN COLUMNA EN EL EJE C DEL EJE 1.
 - UNIONES SOLDADAS, PERFILES DEFINITIVOS Y SEPARACIÓN DE LA MALLA SEGÚN MEMORIA DE CÁLCULO (PD).
 - MATERIALES, PROTECCIÓN ANTICORROSIVA Y ESPECIFICACIONES SEGÚN LÁMINA C08. [PR]
 - LAS SECCIONES DE ESTA LÁMINA SON LAS DEL PROYECTO DE REFERENCIA, POR INDICACIÓN DEL INGENIERO RESPONSABLE; NO SUSTITUYEN LA MEMORIA DE CÁLCULO.
 - [PR] = NOTA TOMADA DEL PROYECTO DE REFERENCIA, PENDIENTE DE REVISIÓN.

ESPACIO PARA SELLOS Y TIMBRES

CivilCon Diseño y Construcción SRLTDA Céd. Jurídica: 3-102-762712	
PROFESIONAL RESPONSABLE: DIRECTOR TÉCNICO: Steven Viales (Civil) IC-40759 David Barrantes (Electricidad) IE-27499	
PROYECTO: VIVIENDA UNIFAMILIAR DISTRITO 03 SANTIAGO, CANTÓN 05 SAN RAFAEL, PROVINCIA 04 HEREDIA, COSTA RICA.	
INFORMACIÓN REGISTRO PÚBLICO: FOLIO REAL: 4-041200-000 PLANO CATASTRADO: 4-57389-2023 ÁREA SEGÚN CATASTRO: 256 m²	
CONTENIDO: ENTREPISO PLANTA DE ENTREPISO 1 Y 2. DETALLE DE ENTREPISO. SECCIÓN A-A. SIMBOLOGÍA. NOTAS.	
ESCALAS: 1:50 / INDICADAS	
CONTROL DE REVISIONES	
REV.	FECHA DESCRIPCIÓN
0	06-10-2026 VERSIÓN DE TRABAJO PARA REVISIÓN
1	06-10-2026 ENTREPISOS 1 Y 2 EN UNA SOLA LÁMINA
ESTADO:	
VERSIÓN DE TRABAJO NO APTA PARA CONSTRUCCIÓN NI TRÁMITE	
LUGAR	LÁMINA
COSTA RICA	C03
OCT 2026	TOTAL --